




● luminária embuída, 3.000 K, RSC 90

□ alçapão técnico 600 x 600 mm

▨ forro absorvente (alfa 0,70)

FORROS POR AMBIENTE

AMBIENTE	SOLUÇÃO	ÁREA	NOTA
T-03A	forro absorvente (α=0,70) instalado no teto	36,24	único ponto que demanda a instalação de 3,20 x 60
T-03C	gesso liso + cantoneira e lapinha	25,20	abertura entre os módulos, forro técnico aqui não
T-03D	gesso liso lustrado	18,00	superfície de fácil limpeza sem necessidade de manutenção
S-03D	gesso liso + la mineral sobre o forro	25,80	la sobre o forro absorve o ruído de ruído no pavimento
S-03E	gesso liso + la mineral sobre o forro	25,80	idem
S-03F	gesso liso + la mineral sobre o forro	25,80	idem
T-03G	sem forro (estrutura aparente)	36,00	ambiente semi-industrial, acústica não é crítica
T-03H	sem forro (estrutura aparente)	9,00	idem
T-03I	sem forro (estrutura aparente)	3,00	idem

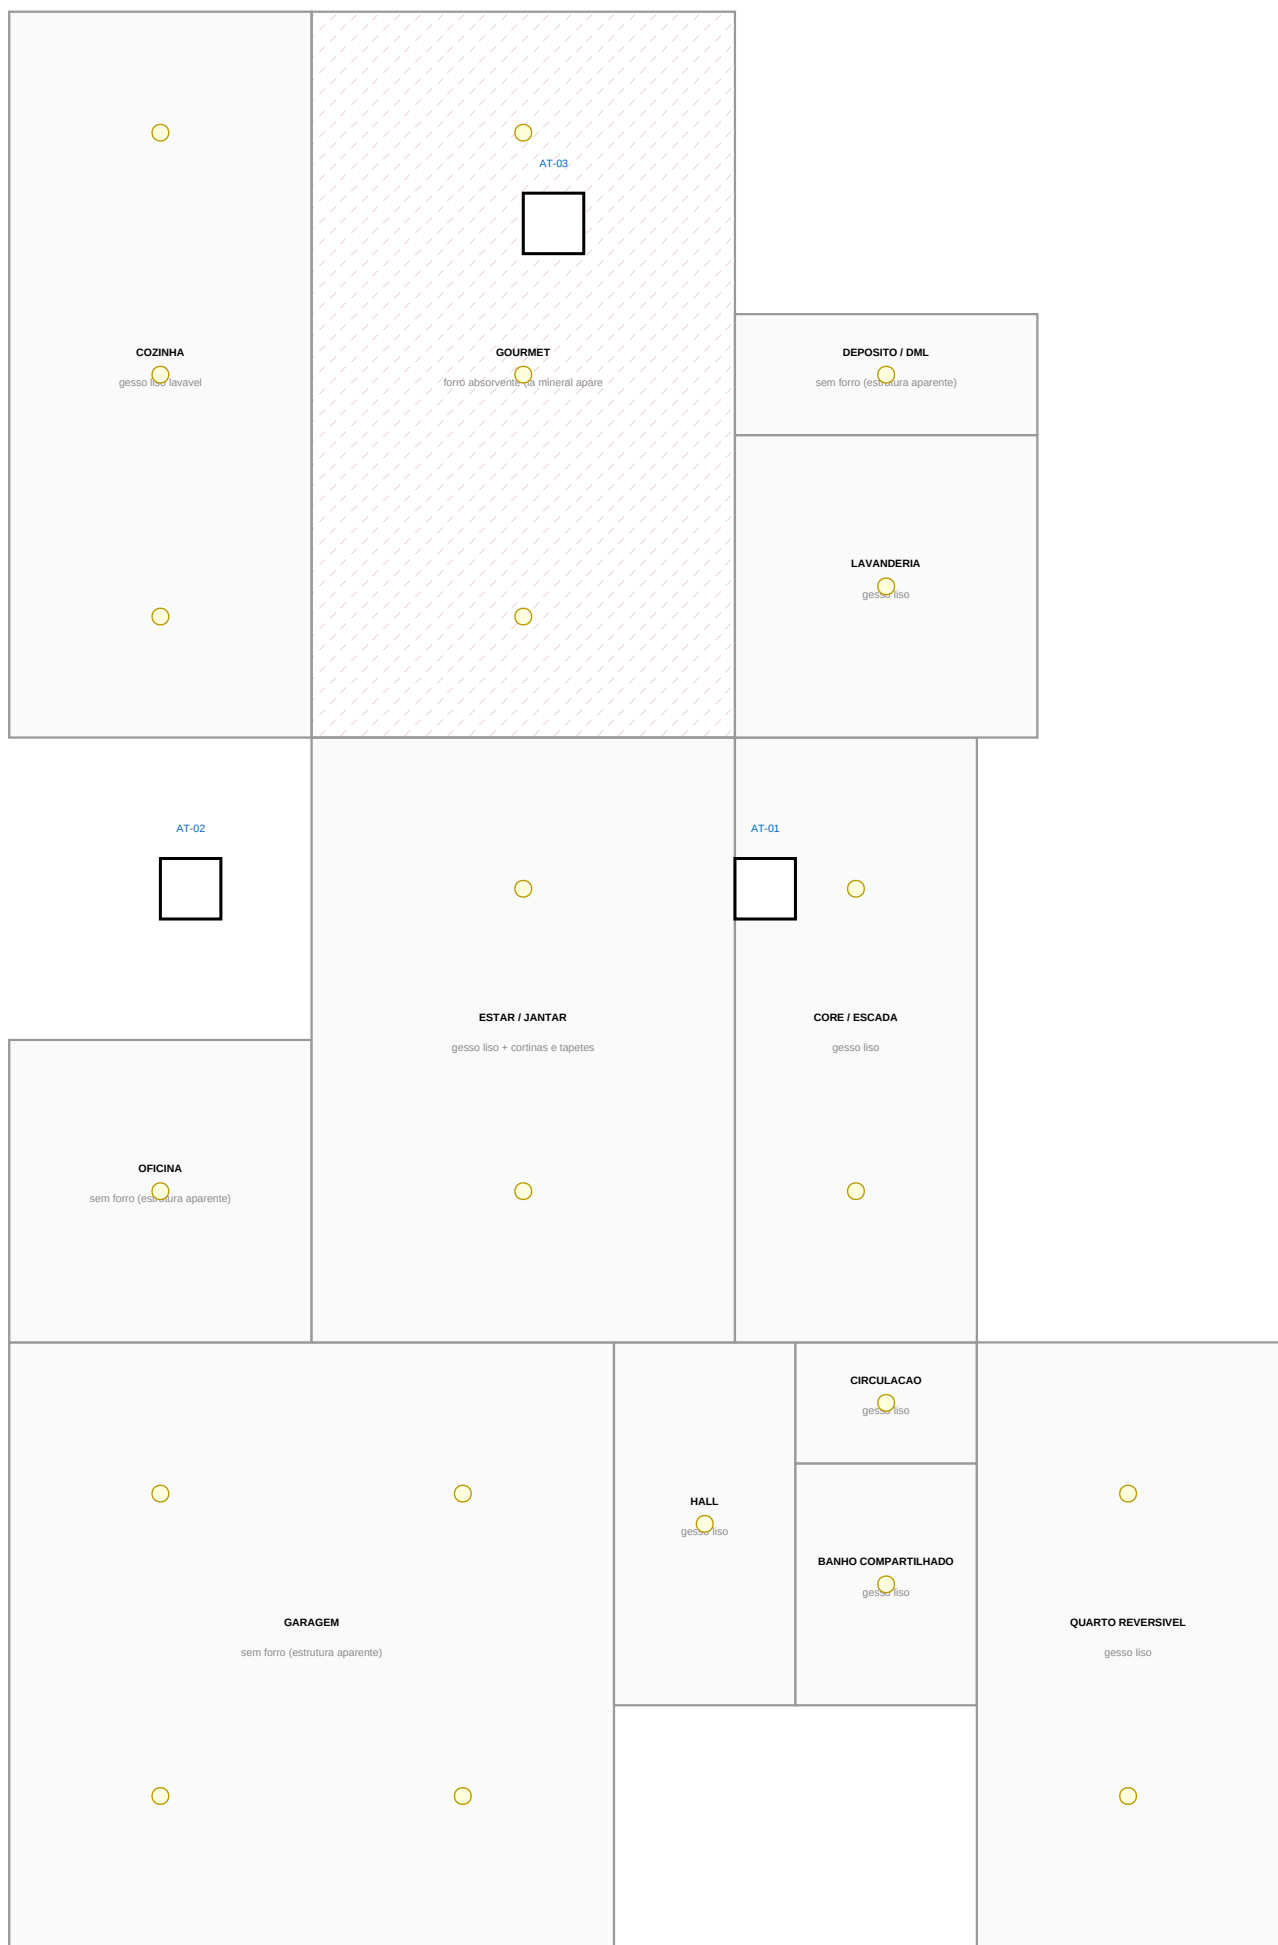

1 FORRO REFLETIDO — TERREO
ESCALA 1:75

NOTAS

1 Planta refletida: vista do forro projetada no plano horizontal.

2 Forro absorvente apenas no gourmet — único ponto com necessidade crítica.

3 Alçapão técnico de 600 x 600 mm, passando de cobertura de 600 mm.

4 Luminária geral 3.000 K, RSC modelo 90.

PROJETO PORTO REAL

RESIDÊNCIA UNIFAMILIAR (MANSÃO - AM) | SOBR TATIANA-PS

PROJETO ARQUITETÔNICO

PLANTA DE FORRO E ILUMINAÇÃO

BASE GEOMÉTRICA	ESCALA	EMISSÃO	PROVA
União Consolidada	1:75	ESTUDO PRELIMINAR RDS	16
ISO-RDS (previsão)	FORMATO A1	ISO LIBERADO PARA ORÇ	
UNIDADE MÉTRICA: mm	MÁQUINA: 600/600/300	SEM ART / RNT	06-25 REV-03