


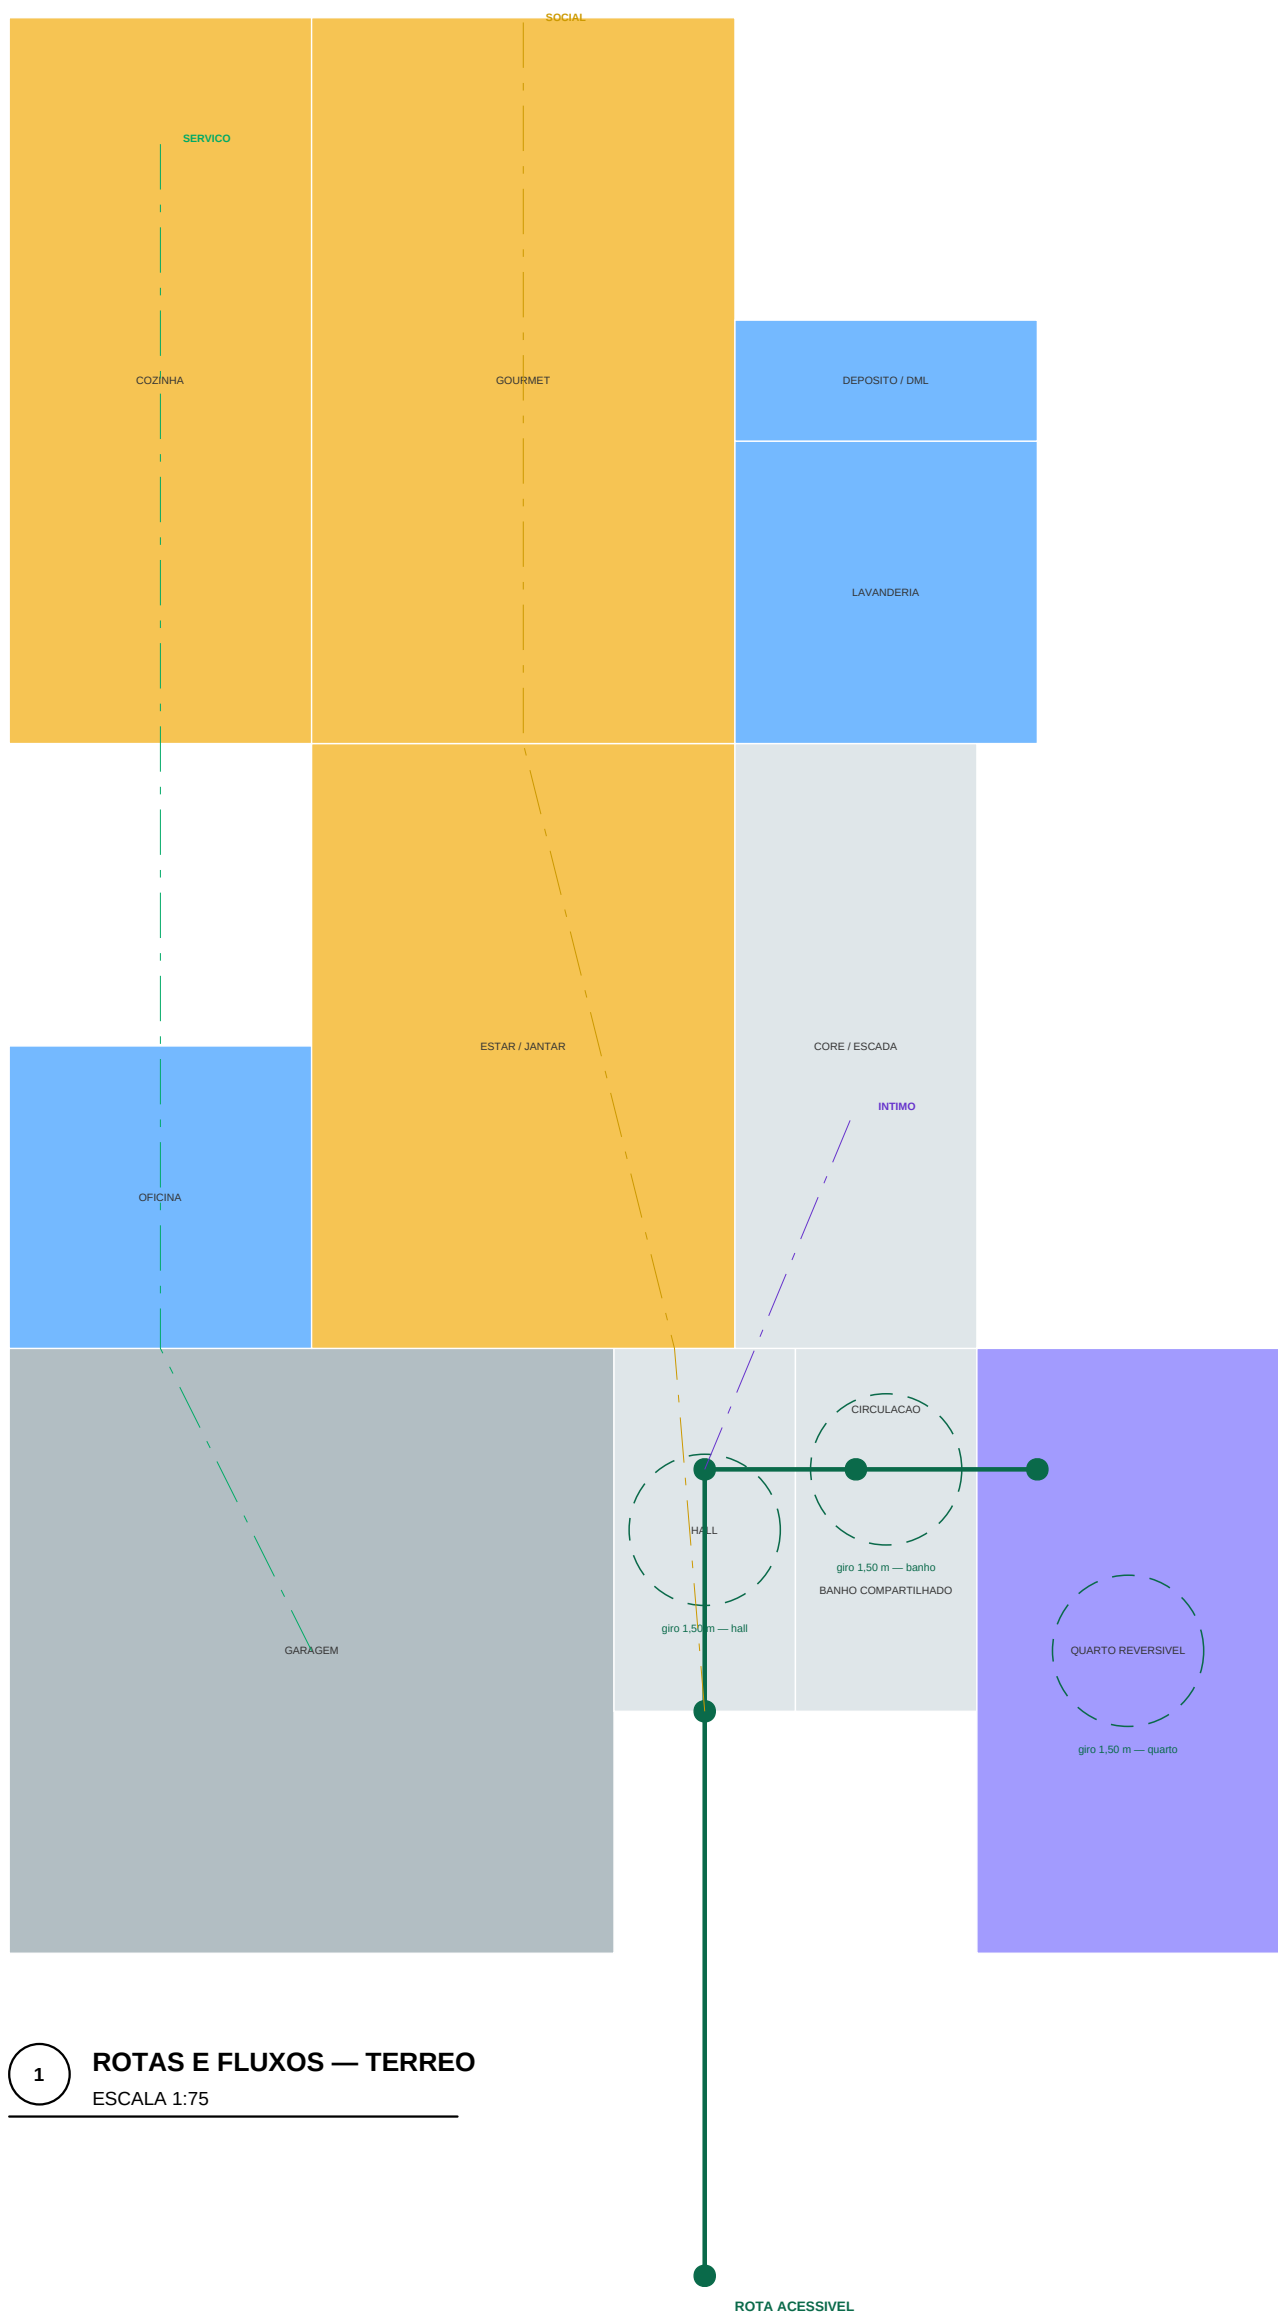


1 ROTAS E FLUXOS — TERREO
ESCALA 1:75

VERIFICACAO NBR 9050

ITEM	EXISTENTE	PROJETO	
Vel. livre de porta	800 mm	940 mm (altura de 900)	OK
Circulo de giro 360 graus	1.500 mm	hall, banheiro e quarto	OK
Desnivel sem rampas	até 5 mm	soluções niveladas	OK
Largura de circulação	900 mm	1.800 mm no hall	OK
Barras de apoio	relevo no piso	instaladas no P1 e P10.1	OK
Barras de acesso	altura livre 750 mm	sem barreiras até a altura	OK
Corrimão e interruptor	600 a 1.000 mm	a altura no relevo	pendente

FLUXOS — SEPARACAO DE CIRCUITOS

CIRCUITO	PERCURSO	CIRCUITO SOCIAL?
Serviço	garagem → estufa → lavanderia → cozinha → despensa	NÃO
Social	entrada → hall → estar → gourmet → alameda → piscina	—
Área íntima	hall → banheiro compartilhado → quarto reservado	NÃO
Área íntima	hall → core → hall superior → suíte	NÃO
Área de carga	cozinha → despensa → reservado	NÃO

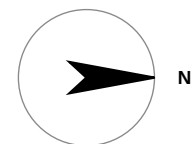

- NOTAS
- * Rota acessível do passeio ao quarto reservado e ao banheiro compartilhado.
 - * Circulo de giro de 1.500 mm verificado nos pontos de manobra.
 - * Porta de correr de 900 mm no banheiro libera a área de manobra.
 - * Reforço para barras de apoio instaladas antes do fechamento das placas.

PROJETO PORTO REAL

RESIDENCIA UNIFAMILIAR (MANAUS - AM) | SOUZA TATIANA-PS

PROJETO ARQUITETONICO

ACESSIBILIDADE E FLUXOS

BASE GEOMETRICA Linha Consolidada em P102 (previsão) UNIDADE MESTRE: mm	ESCALA 1:75 FORMATO A1 MILHA 465/000000	EMISSAO ESTUDO PRELIMINAR RDS NÃO LIBERADO PARA OBRA SEM ART / RNT	PROJETA 17 de 25 REVIZOES
--	---	---	--