




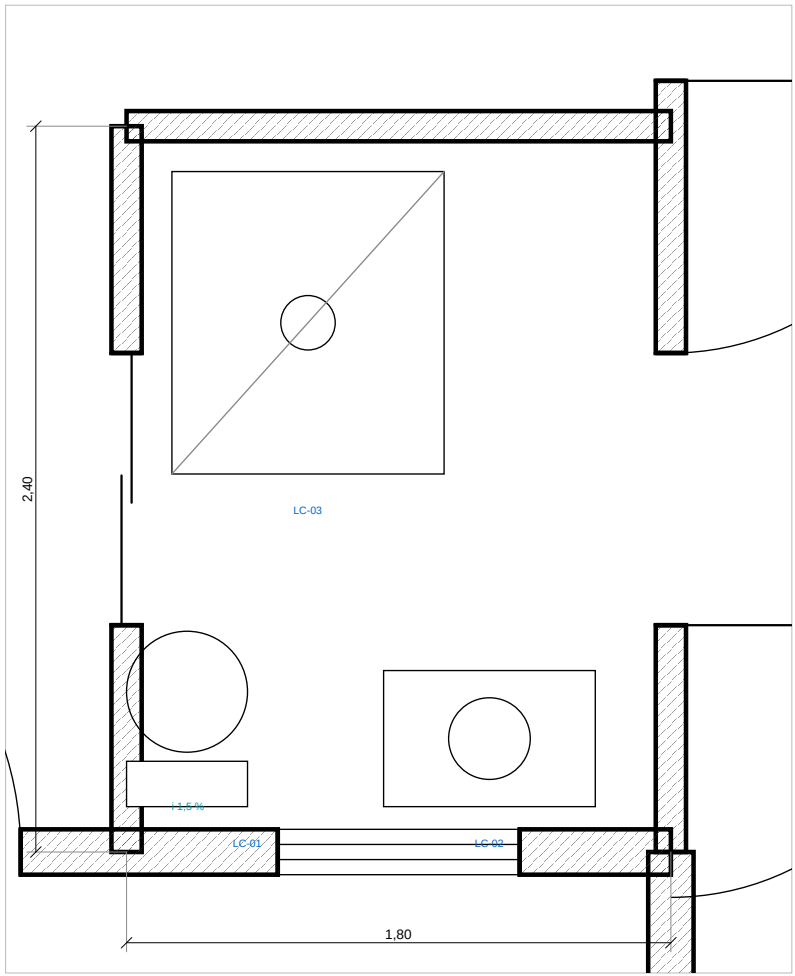


1 BANHO SOCIAL  
ESCALA 1:25

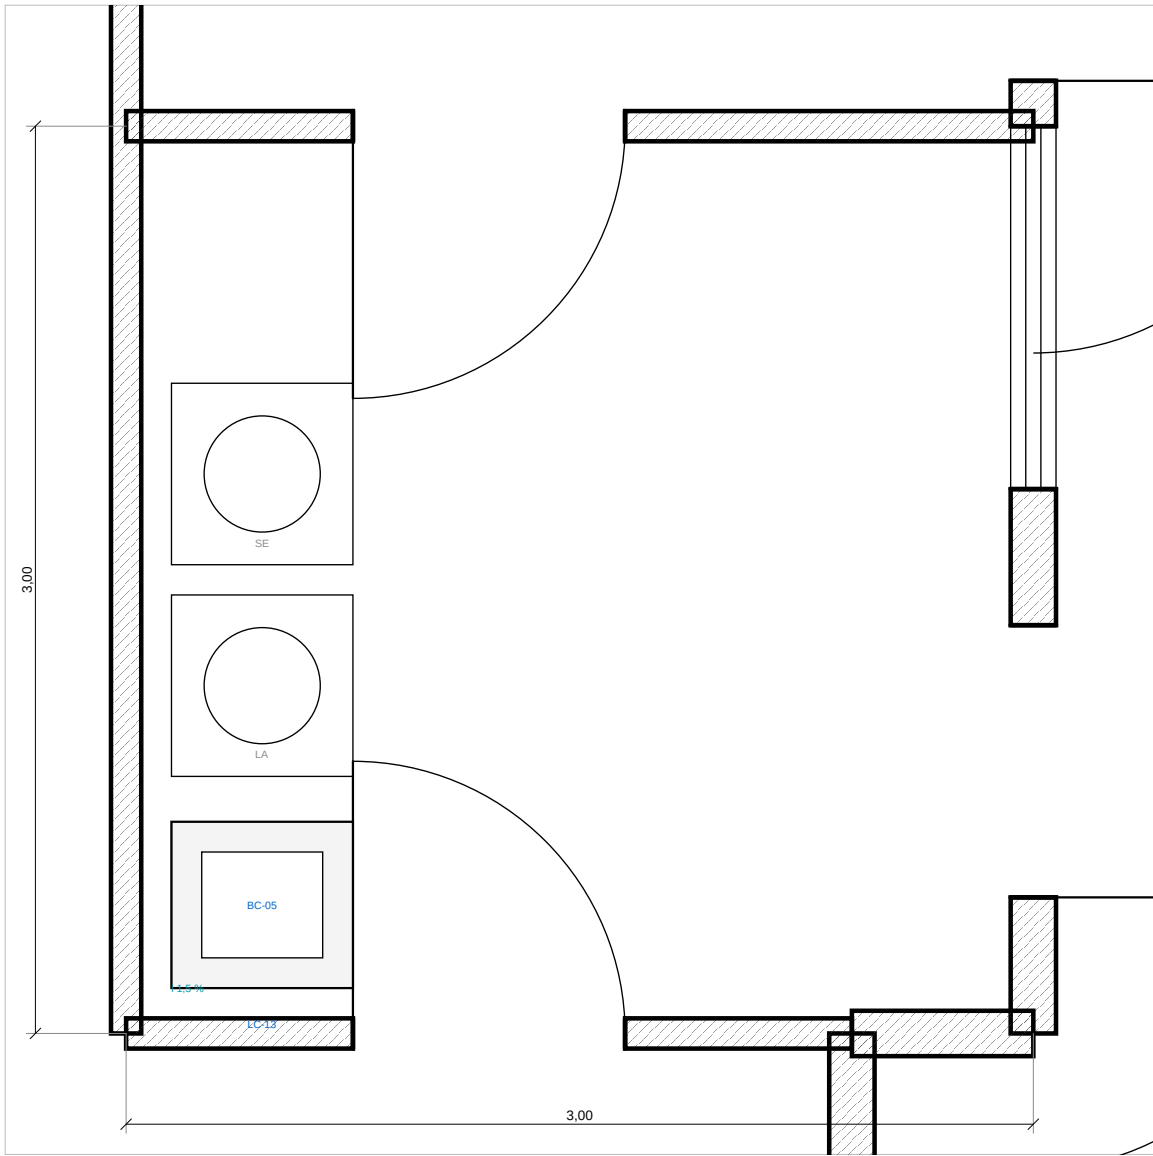

2 LAVANDERIA  
ESCALA 1:25

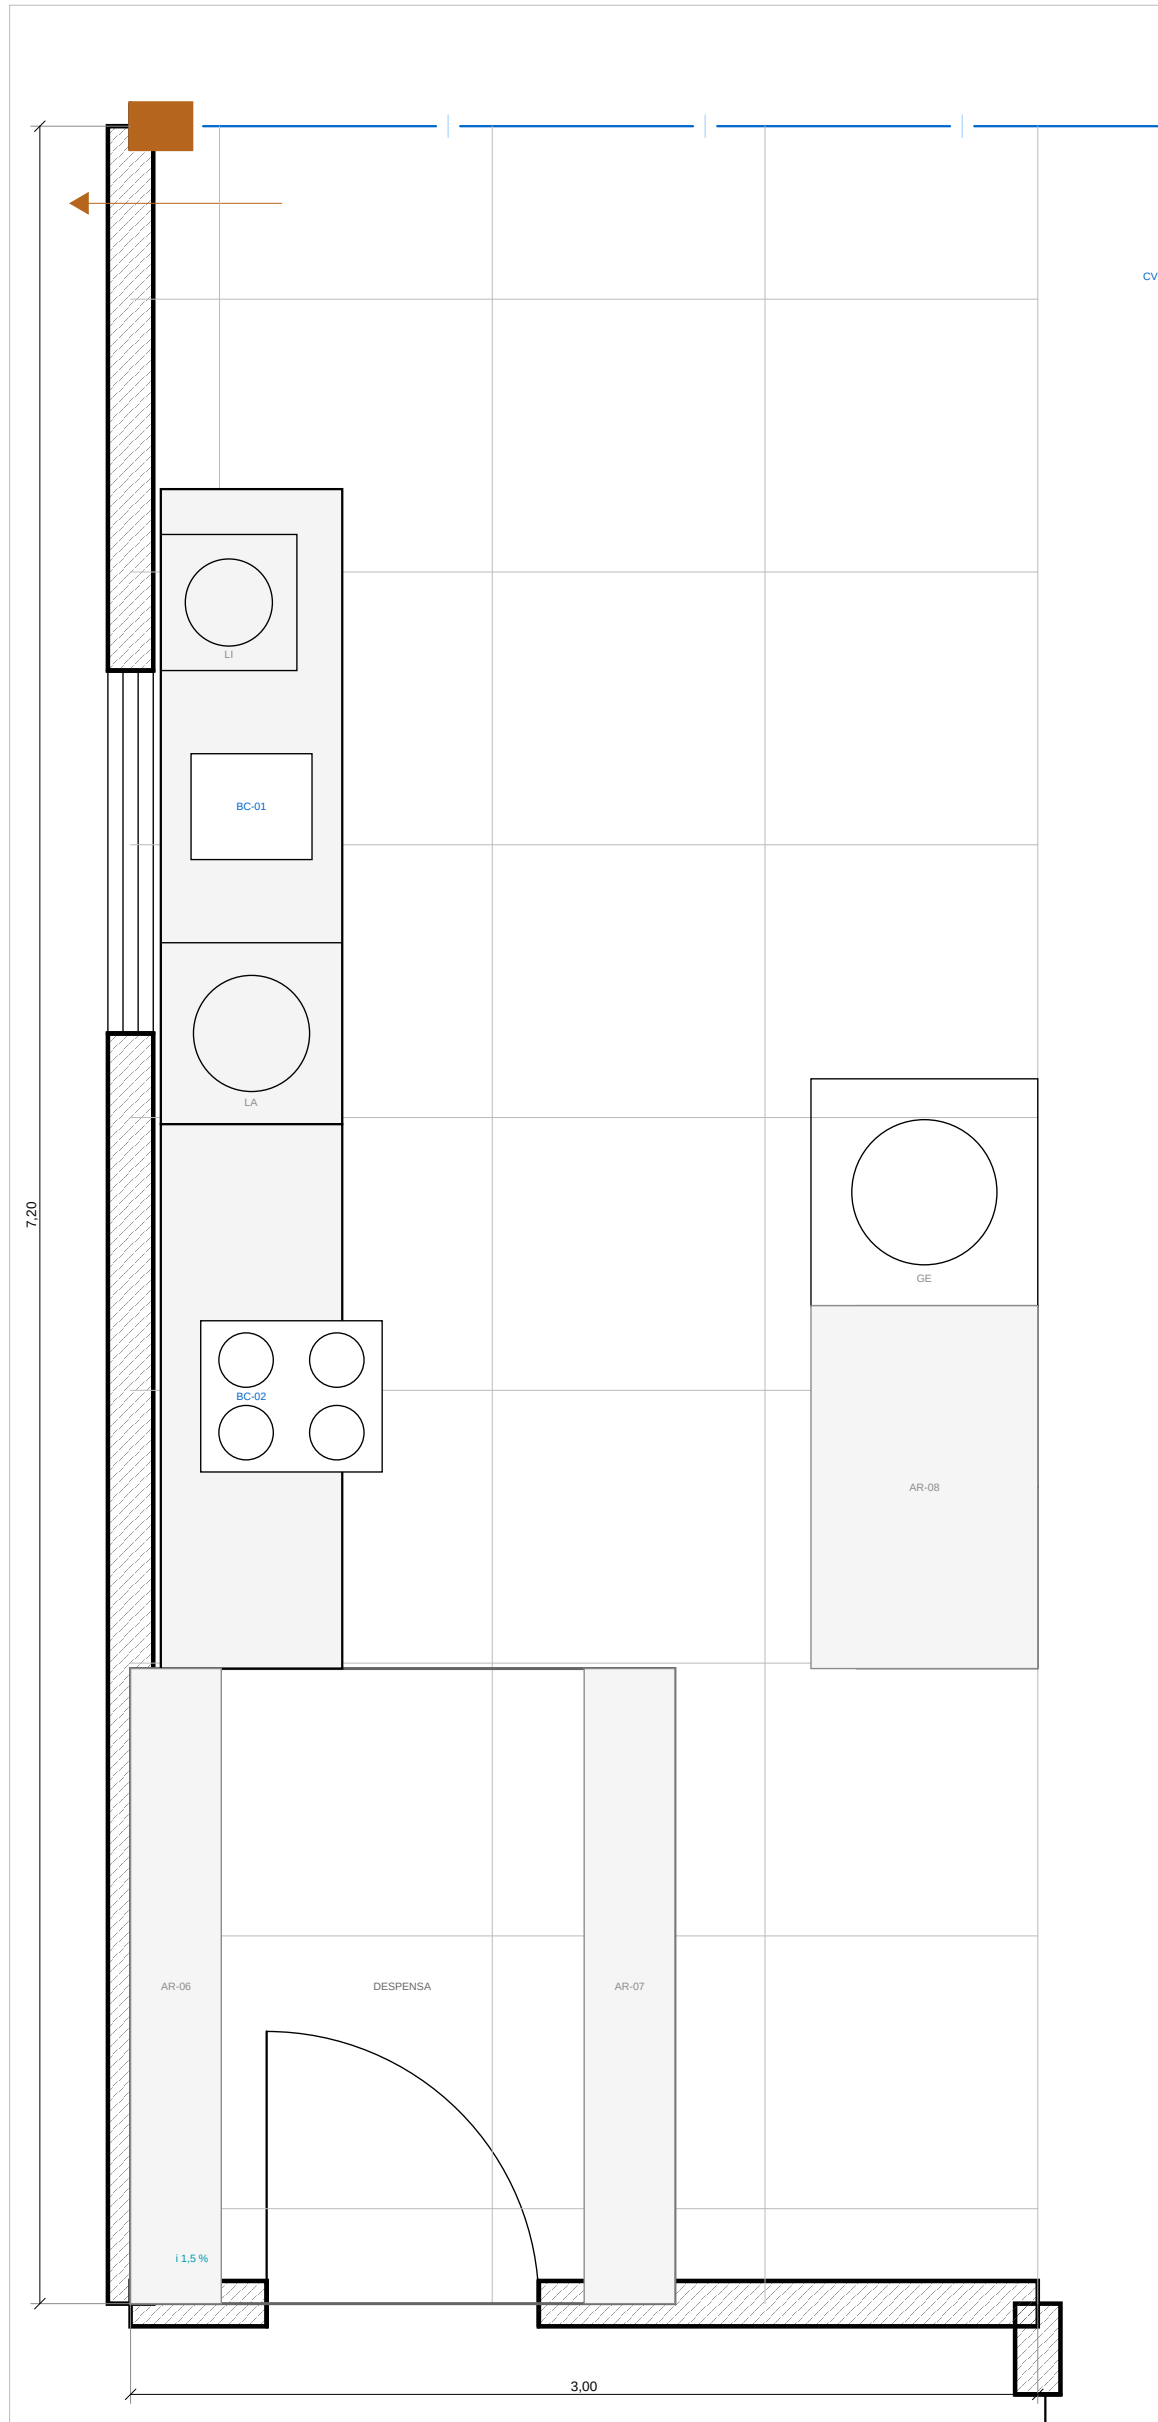

3 COZINHA  
ESCALA 1:25

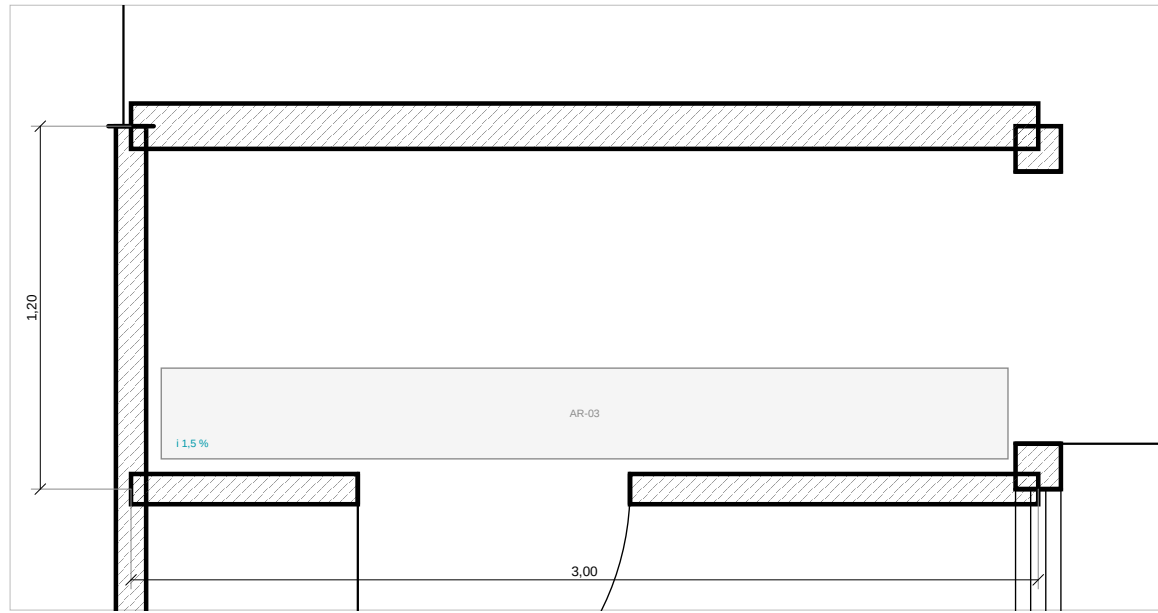

4 DEPOSITO / DML  
ESCALA 1:25

PAGINACAO VERIFICADA — PECAS INTEIRAS + RECORTE EM CADA PONTA

| AMB   | AMBIENTE       | ZONA | PEÇA   | EXD X    | EXD Y     | ALTURA (mm)         |
|-------|----------------|------|--------|----------|-----------|---------------------|
| T-BWC | BANHO SOCIAL   | ZP-4 | parede | 0 + 0200 | 0 + 0000  | 2400 (2 Ruas + 100) |
| T-LAV | LAVANDERIA     | ZP-5 | parede | 0 + 0200 | 4 + 0500  | 1800 (2 Ruas + 100) |
| T-COC | COZINHA        | ZP-1 | pis    | 0 + 0200 | 7 + 11000 | —                   |
| T-DEP | DEPOSITO / DML | ZP-5 | parede | 0 + 0200 | 1 + 0500  | 1800 (2 Ruas + 100) |

NOTAS

- \* Pignoneus de piso em linha fina, a malha vem da ZONA de pignoneus, não do canto do ambiente.
- \* Peca de piso porcelanado retificado 300 x 300, parede ceramico retificado 300 x 600, junta 2 mm.
- \* Caminho de 1.5 % para o lado em toda area molhada, solteira elevada 15 mm nos bicos.
- \* Representação: marra lquida em 2 dimensoes, subido 300 mm na parede e 1.800 mm nos bicos.

PROJETO PORTO REAL

RESIDENCIA UNIFAMILIAR (MARIAUS - AM) | SOUS TATIANA-PS

PROJETO ARQUITETONICO

AMPLIACOES DE AREA MOLHADA — TERREO

|                                                                                    |                                                  |                                                                              |                                |
|------------------------------------------------------------------------------------|--------------------------------------------------|------------------------------------------------------------------------------|--------------------------------|
| BASE GEOMETRICA<br>Linha Consolidada<br>psu-RDZ (previsível)<br>UNIDADE MESTRE: mm | ESCALA<br>1:25<br>FORMATO A1<br>MILHA 605/000000 | EMISSAO<br>ESTUDIO PRELIMINAR RDS<br>NAO LIBERADO PARA OBRA<br>SEM ART / RNT | PROJETA<br>22<br>06-25 REV-KDS |
|------------------------------------------------------------------------------------|--------------------------------------------------|------------------------------------------------------------------------------|--------------------------------|