



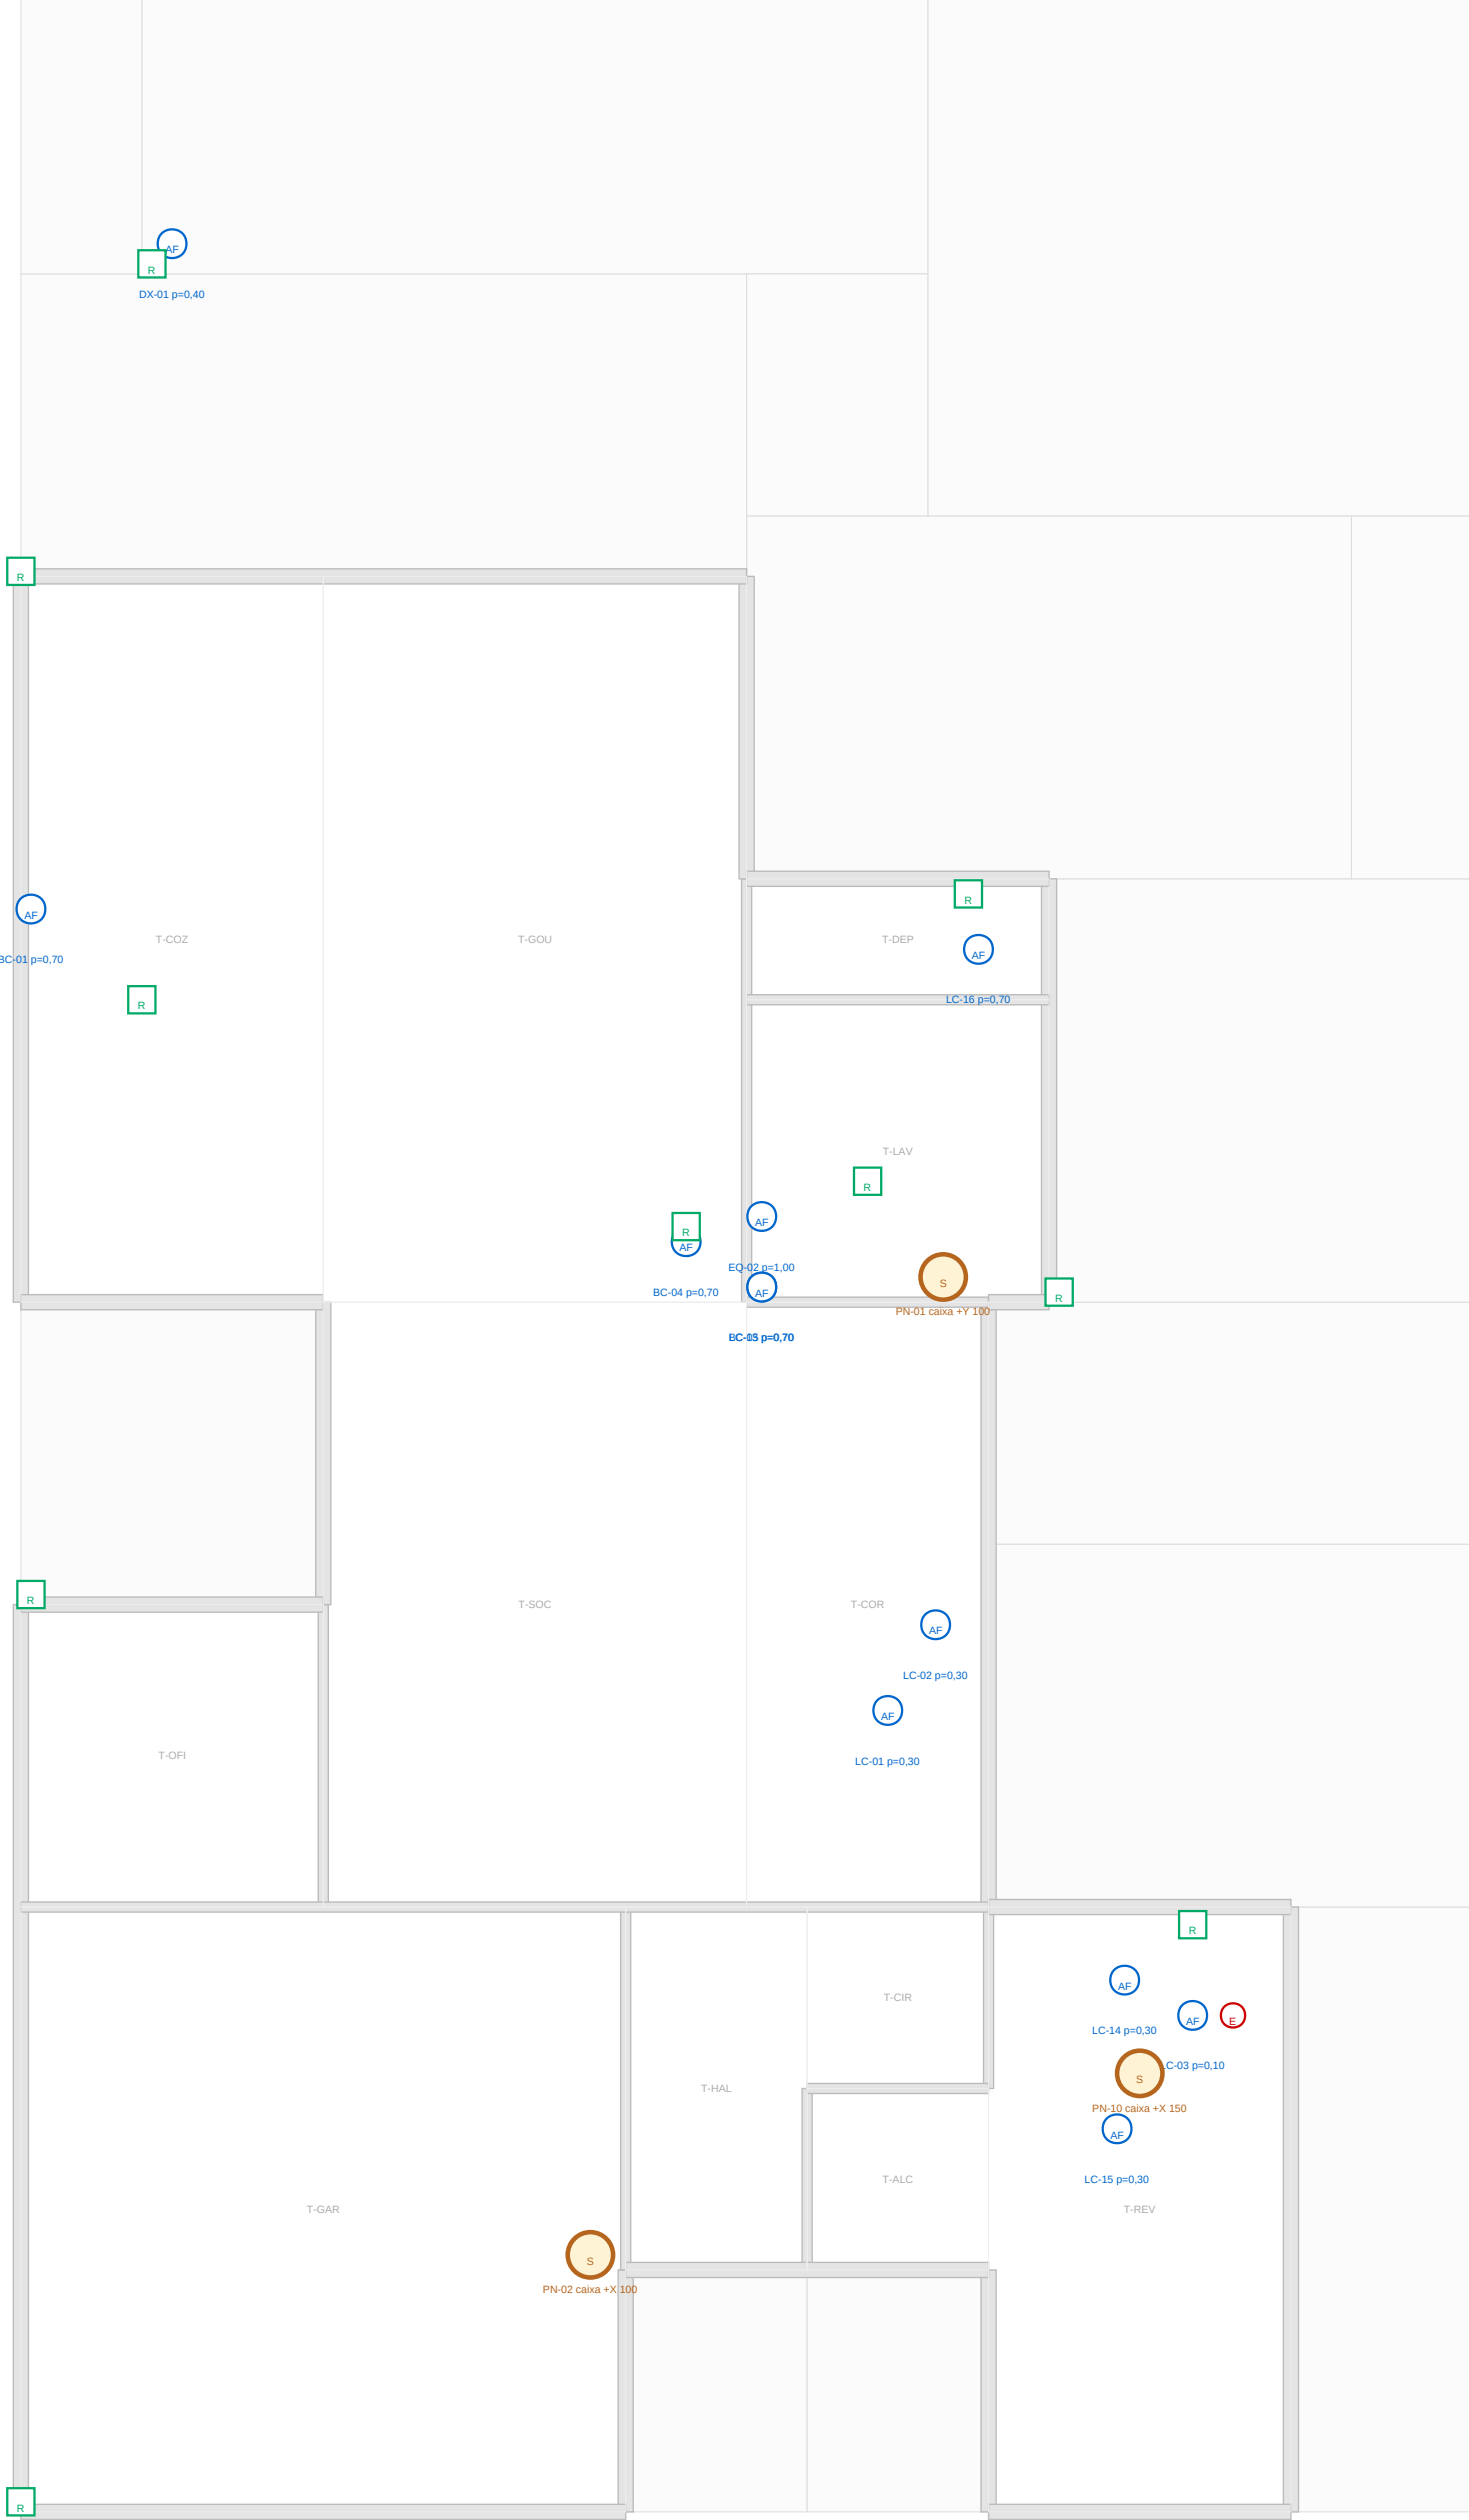

1 PONTOS HIDRAULICOS — TERREO
ESCALA 1:75

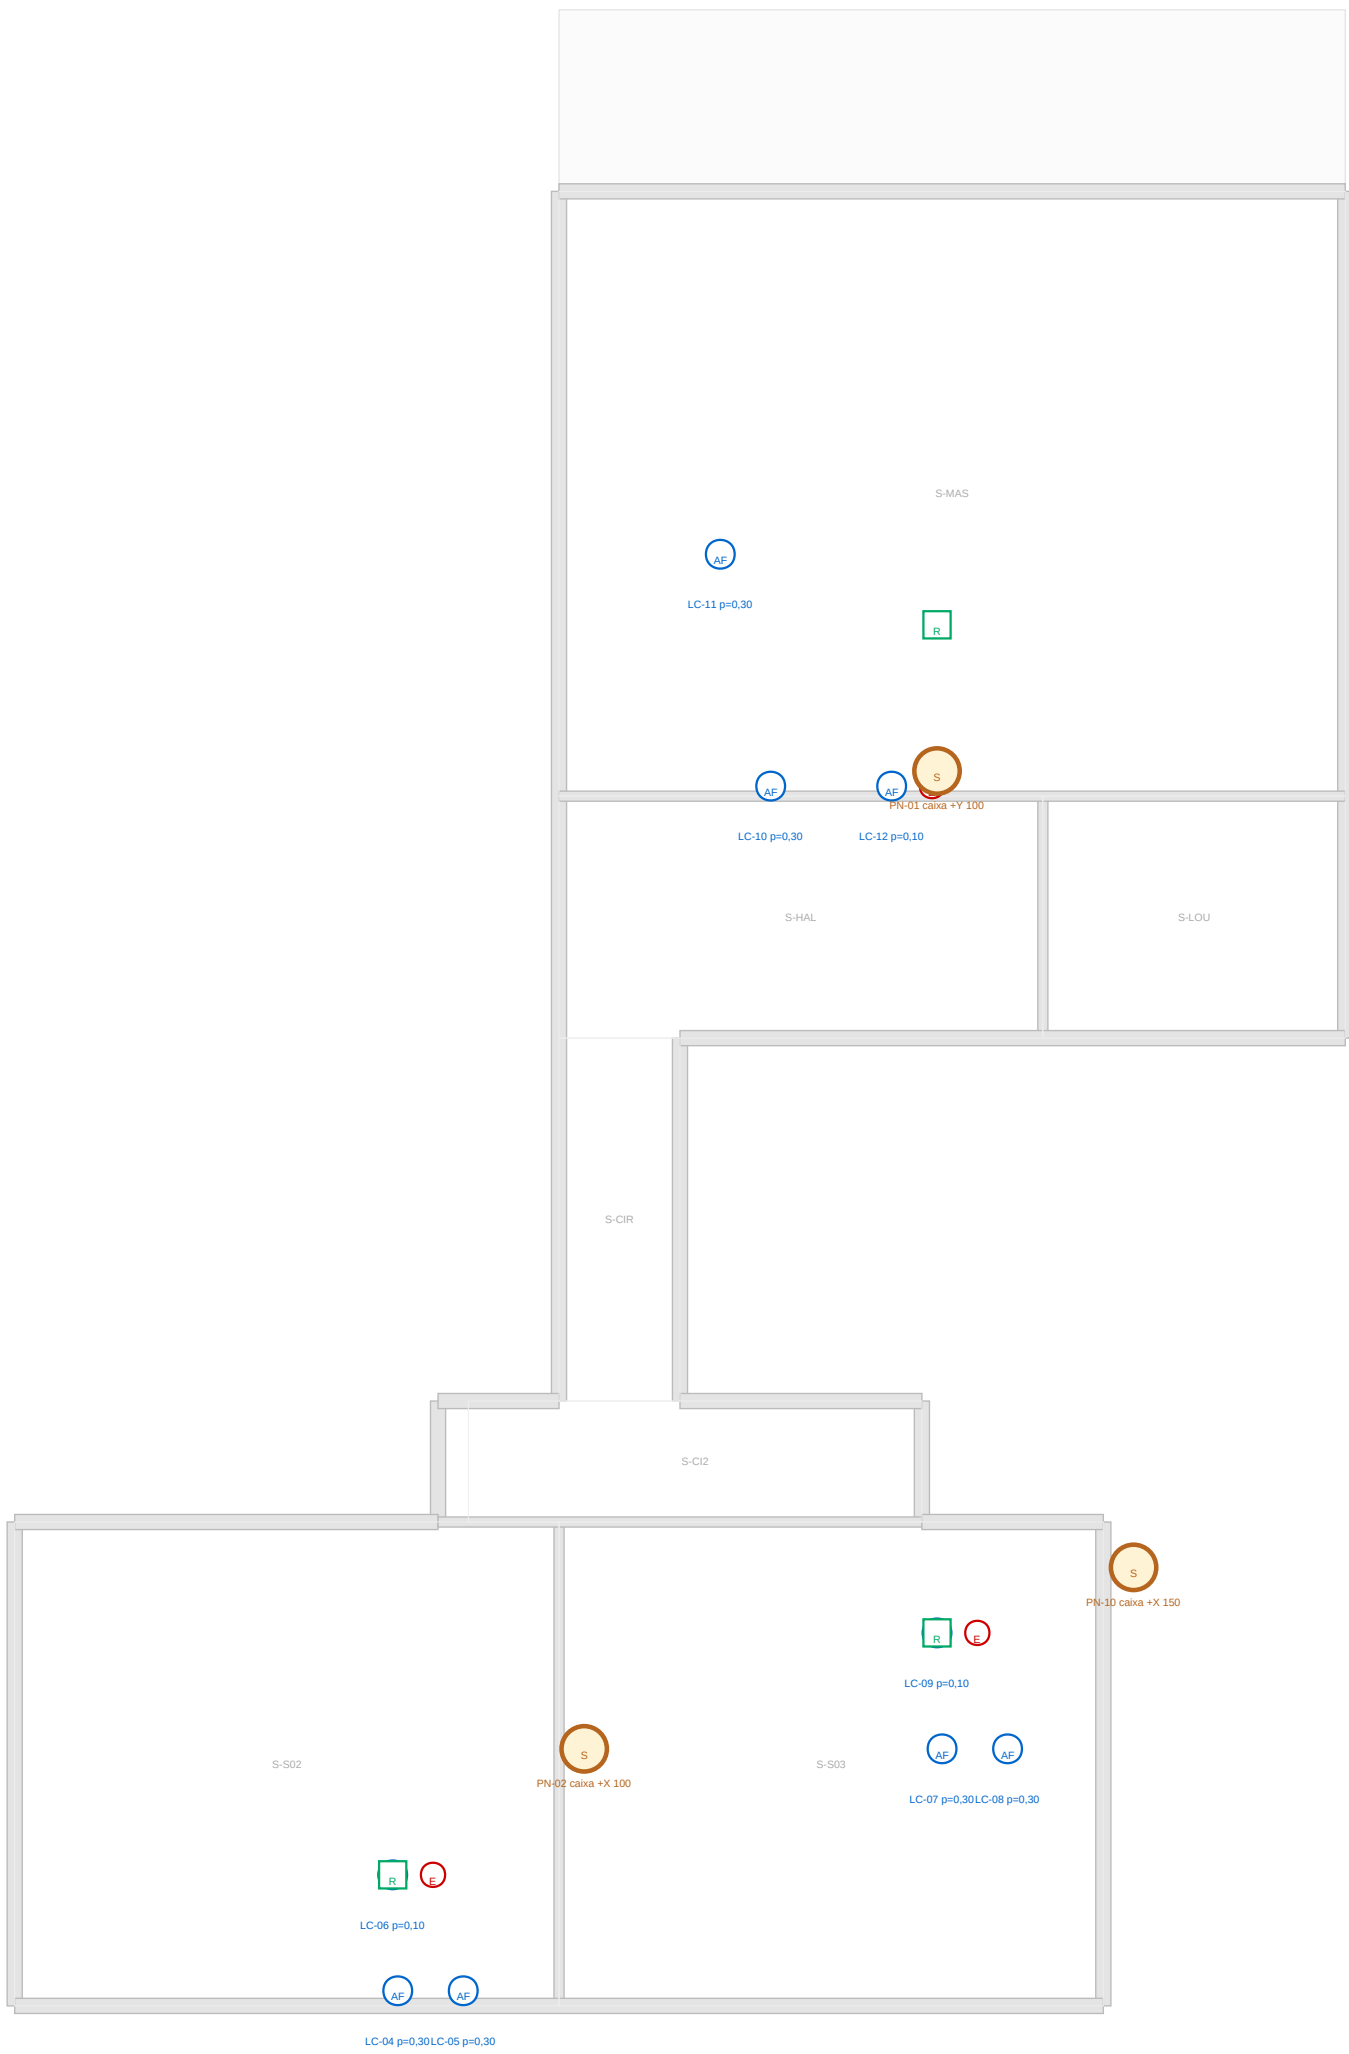

2 PONTOS HIDRAULICOS — SUPERIOR
ESCALA 1:75

DIMENSIONAMENTO — AGUA FRIA E ESGOTO

TRECHO	PECAS	PESOS	Q (L/s)	DN AGUA	V (m/s)	UMC	DN ESGOTO	REGIME
Superior	4	2,10	0,435	DN25	1,39	27	DN100	pressurizado
Terreo	33	6,39	0,747	DN32	1,39	36	DN100	gravidade
GERAL	37	8,50	0,884	DN32	1,42	43	DN100	gravidade

PECAS DE UTILIZACAO

COD	AMB	TIPO	PESO	UMC	DN AF	DN ESG	QUENTE
LC-01	T-CORR	vaso	0,30	6	DN25	DN40	—
LC-02	T-CORR	sanifone	0,30	1	DN25	DN40	—
LC-03	T-REV	box	0,33	2	DN25	DN40	qns
LC-04	T-REV	vaso	0,30	6	DN25	DN40	—
LC-05	T-REV	sanifone	0,30	1	DN25	DN40	—
LC-06	S-ESC	vaso	0,30	6	DN25	DN40	—

(continuacao)

COD	AMB	TIPO	PESO	UMC	DN AF	DN ESG	QUENTE
LC-01	S-MAS	vaso	0,30	6	DN25	DN40	—
LC-02	S-MAS	sanifone	0,30	1	DN25	DN40	—
LC-03	S-MAS	box	0,33	2	DN25	DN40	qns
LC-04	T-LAV	sanifone	0,70	3	DN25	DN40	—
LC-05	T-DEP	sanifone	0,70	3	DN25	DN40	—

(continuacao)

COD	AMB	TIPO	PESO	UMC	DN AF	DN ESG	QUENTE
BC-01	T-CORR	pin	0,70	3	DN25	DN40	—
BC-02	T-CORR	pin	0,70	3	DN25	DN40	—
BC-03	T-LAV	sanifone	1,00	3	DN25	DN40	—
BC-04	T-DEP	sanifone	0,60	2	DN25	DN40	—

DECISoes QUE O DIAMETRO REVELA

DECISAO	CONSEQUENCIA HIDRAULICA
Chuveiro eletrico em vez de aquecimento central	peso 0,02 por chuveiro em vez de 0,42 a soma cai de 5,2 para 5,3 pesos e o alimentador de DN40 para DN32
Limite de velocidade por conforto, nao por norma	DN32 elevando a norma a 2,37 m/s a 3,0 m/s e tudo nao acontece. Custa alguns metros de tubo
Pressurizador na rede superior	0,8 mca por gravidade nos setores chuveiro eletrico, TC-14 entrega 12 mca
Uma unica rede de agua	PR2 alimenta o setor, nao faz rede nao passa no box, e com ela desaparece a unica possibilidade de conexoes cruzadas
Canal de gotejao antes da impressao	canal + TC-11 (DN-1) + TC-12 = rede, DN100 com cobertura de 2%

NOTAS

- Agua fria por metrado dos pesos (PR2 S-ESC) Q = 0,30 e vazante dos pesos = 0,004 L/s com 0,3 pesos.
- Alimentador DN32 a 1,42 m/s — limitado pelo conforto (2,3 m/s) nao pela norma (3,0 m/s).
- Exigido por LNC (DN32) 63 LNC, tubo de queda DN100, ventilacao DN40.
- Chuveiro 63x100 com peso 0,02, nos 0,40 a decisao de aquecimento aquece agua com diametro menor em toda a casa.

PROJETO PORTO REAL

RESIDENCIA UNIFAMILIAR (MANSO - AM) | 500x700m (p)

PROJETO ARQUITETONICO

INSTALACOES HIDROSSANITARIAS

BASE GEOMETRICA

PR-PR2 (previsto)

UNIDADE MEDIDA: m³

ESCALA

1:75

FORMATO A1

MAQUA 605050505

EMISSAO

ESTUDO PRELIMINAR RHM

NAO LIBERADO PARA OBRA

SEM ART / RNT

PROVINCIA

26

06-78 REV 004