



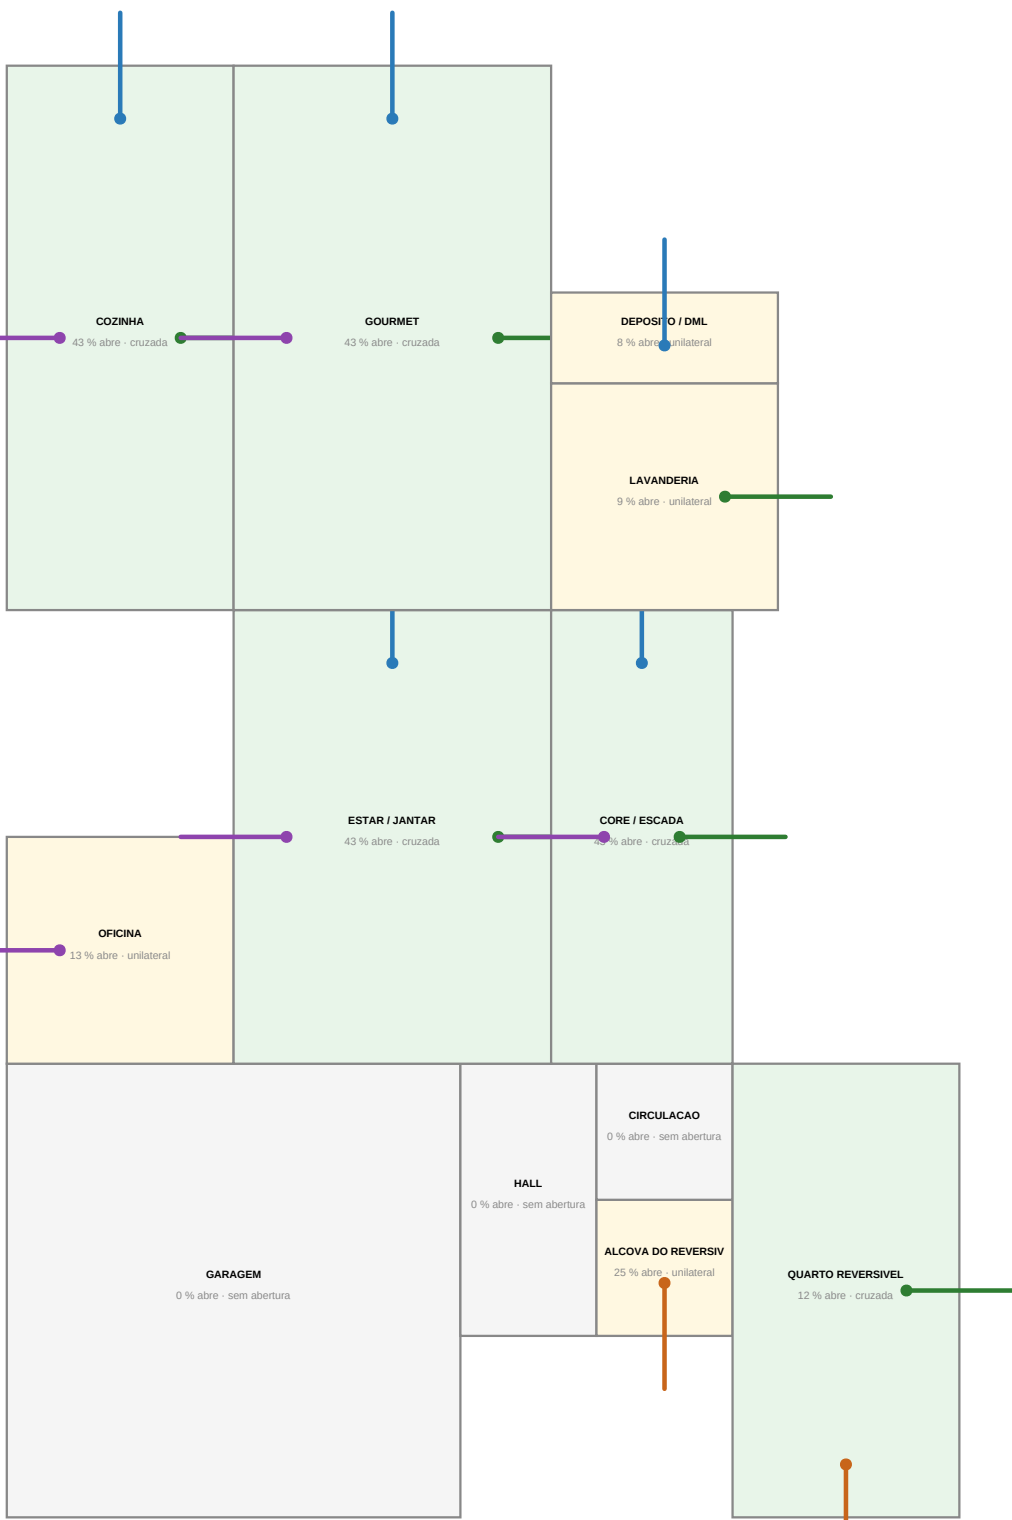

1 TERREO — faces que abrem
ESCALA 1:100

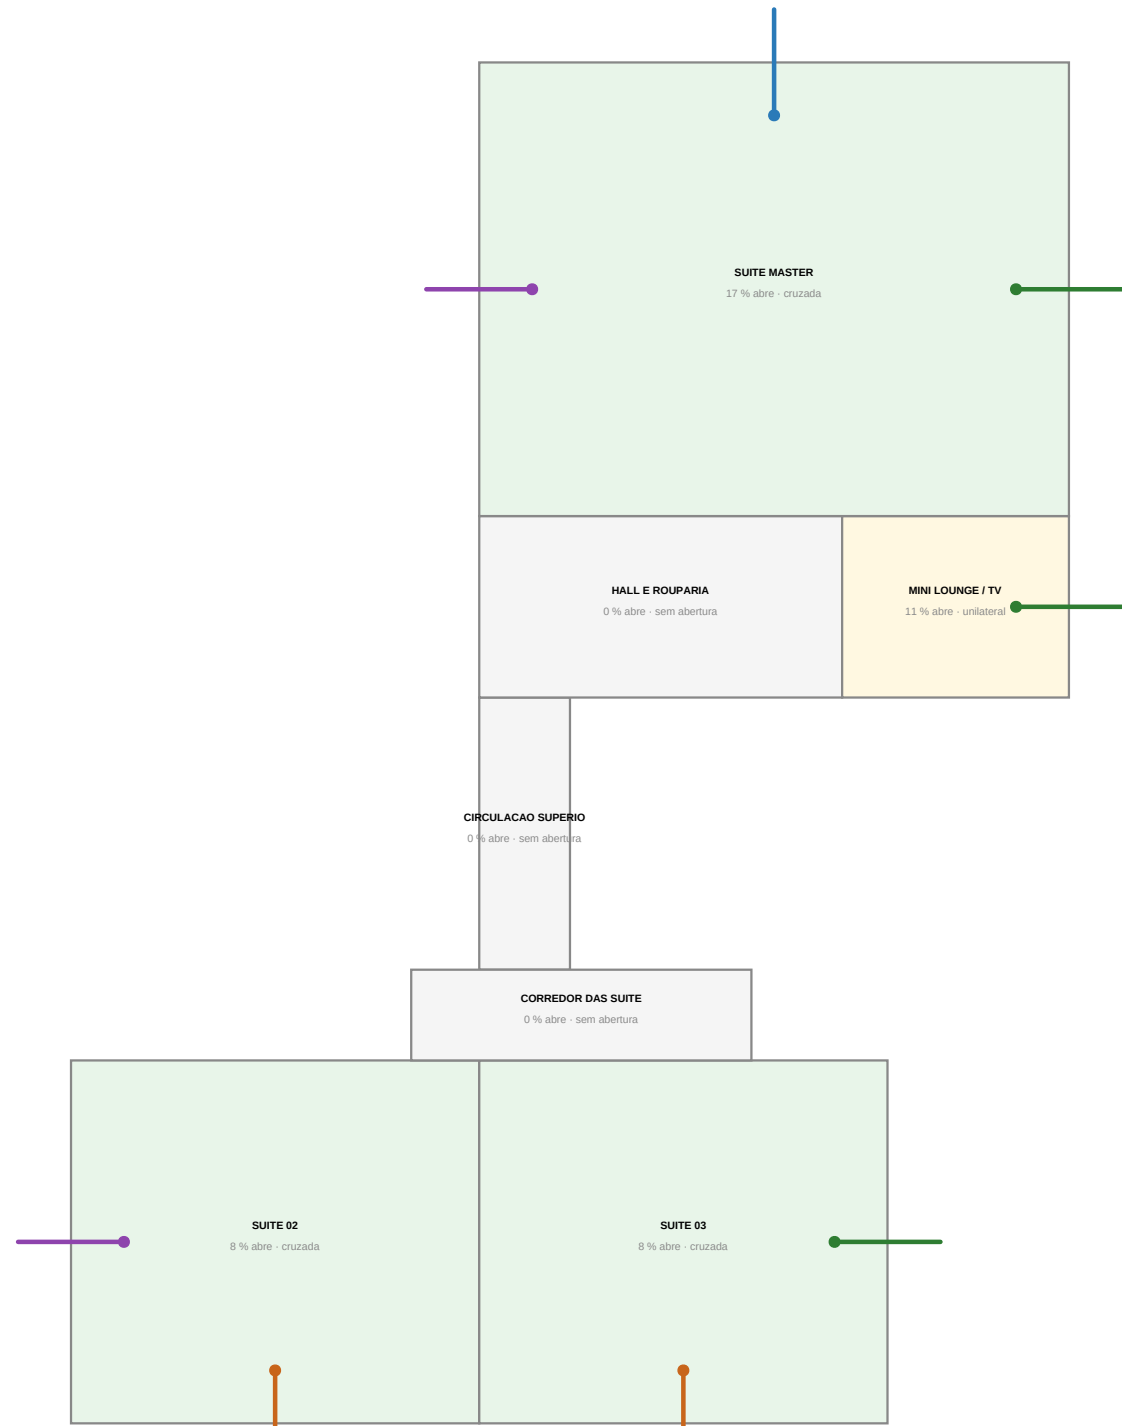

2 SUPERIOR — faces que abrem
ESCALA 1:100

VENTILACAO POR AMBIENTE

COD	AMBIENTE	CAT.	PRO. m²	ABRE. m²	PERÍM.	FACIES	TIPO	NOTA
T-001	COZINHA	INTERIO	34,3	0,00	0 m	—	—	INT
T-002	HALL	INTERIO	9,8	0,00	0 m	—	—	INT
T-003	ALCOVA DO REVERSÍVEL	INTERIO	2,8	0,72	20 m	L	unidirecional	OK
T-004	CIRCULACAO	INTERIO	2,8	0,00	0 m	—	—	INT
T-005	QUARTO REVERSÍVEL	INTERIO	26,7	2,04	22 m	L, N	cruzada	OK
T-006	OFICINA	INTERIO	43,1	1,08	22 m	S	unidirecional	INT
T-007	ESTAR/JANTAR	INTERIO	86,7	36,86	43 m	N, D, S	cruzada	OK
T-008	CORR. E ESCADA	INTERIO	86,7	36,86	43 m	N, D, S	cruzada	INT
T-009	COZINHA	INTERIO	86,7	36,86	43 m	N, D, S	cruzada	OK
T-010	GOURMET	INTERIO	86,7	36,86	43 m	N, D, S	cruzada	OK
T-011	LAVANDERIA	INTERIO	8,3	0,72	9 m	N	unidirecional	INT
T-012	DEPOSITO DmL	INTERIO	3,1	0,24	8 m	O	unidirecional	INT
S-001	SUITE 02	INTERIO	26,5	2,04	8 m	L, S	cruzada	OK
S-002	SUITE 03	INTERIO	26,7	2,04	8 m	L, N	cruzada	OK
S-003	CIRCULACAO SUPERIOR	INTERIO	3,8	0,00	0 m	—	—	INT
S-004	CORREDOR DAS SUITES	INTERIO	4,6	0,00	0 m	—	—	INT
S-005	HALL E ROUPARIA	INTERIO	10,6	0,00	0 m	—	—	INT
S-006	MINI LOUNGE / TV	INTERIO	9,5	0,72	11 m	N	unidirecional	OK
S-007	SUITE MASTER	INTERIO	44,9	7,60	17 m	N, D, S	cruzada	OK

PRIVACIDADE — CADA JANELA CONTRA A DIVISA QUE OLHA (art. 1.301 CC)

VAO	AMB.	FACE	DIST. m	MIN. m	PROTEC.	ORIE.	LEITURA	
004	T-REV	N	8,00	1,50	1500	—	diagonal	OK
002	T-COR	N	8,00	1,50	1500	—	diagonal	OK
005	T-REV	L	7,20	—	1100	BR-L	rua	OK
001	T-REV	N	8,00	1,50	1500	—	diagonal	OK
003	T-REV	L	9,60	—	1000	—	rua	OK
006	T-CO1	S	3,40	1,50	1100	—	ângulo ao vento	OK
001	T-CO2	S	3,40	1,50	1100	—	ângulo ao vento	OK
001	T-LAV	N	7,40	1,50	1500	—	diagonal	OK
004	T-DEP	O	30,80	1,50	1500	—	diagonal	OK
PRO1	T-COR	N	8,00	1,50	9	—	diagonal	OK
PRO2	T-GOU	N	30,40	1,50	9	—	diagonal	OK
PRO3	T-GOU	O	33,60	1,50	9	BR-O	percepção por frente	OK
PRO2	T-DOU	S	5,40	1,50	9	—	diagonal	OK
001	S-GOU	N	4,40	1,50	1100	—	diagonal	OK
005	S-002	S	3,40	1,50	1100	—	ângulo ao vento	OK
001	S-002	L	7,20	—	1100	BR-L	rua	OK
004	S-002	L	7,20	—	1000	BR-L	rua	OK
005	S-003	N	6,80	1,50	1100	—	diagonal	OK
001	S-003	L	7,20	—	1100	BR-L	rua	OK
004	S-003	N	6,80	1,50	1000	—	diagonal	OK
005	S-005	S	7,80	1,50	1100	—	diagonal	OK
PRO3	S-005	O	14,80	1,50	9	—	diagonal	OK
004	S-005	N	4,40	1,50	1000	—	diagonal	OK
001	S-005	N	4,40	1,50	1100	—	diagonal	OK

NOTAS

- * Área que ABRE por ambiente contra a área do piso. NBR 15275-4 exige 0 m na região Norte. NBR 15275-3 recomenda 40 m na ZSB (abertura grande).
- * Facies que abre por fachada (FC) contra a parede lateral 200 m, janela de corte 50 %, baseado 33 %, porta opaca 0 %.
- * Privacidade pelo art. 1.301 do Código Civil: janela que olha a divisa a menos de 2,50 m e protegida. O brisa que protege esta norma.
- * Seis em cada face com abertura, duas de mais faces = ventilação cruzada.

PROJETO PORTO REAL

RESIDENCIA UNIFAMILIAR (MANSÃO - AM) | SUITE TURTURA-PR

PROJETO ARQUITETONICO

VENTILACAO NATURAL, CRUZADA E PRIVACIDADE

BASE GEOMETRICA União Consolidada Projeto (previsão) UNIDADE MESTRE: AM	ESCALA 1:100 FORMATO A1 MANSÃO 6050/5050	EMISSÃO ESTUDO PRELIMINAR RM LADO LIBERADO PARA OBRA SEM ART / INT	PRIVACIDADE 49 60 m REV 004
--	--	---	--