
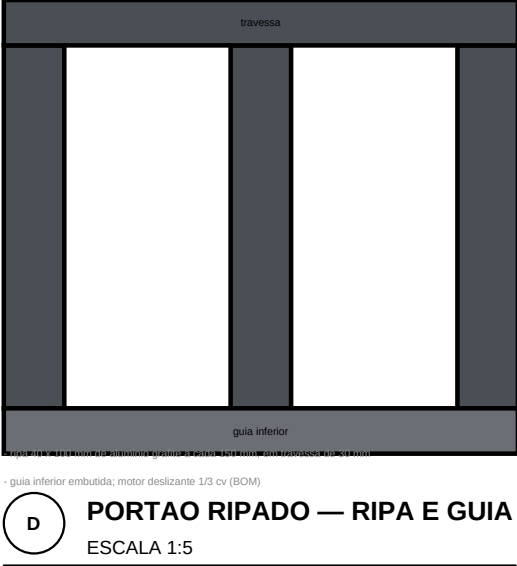
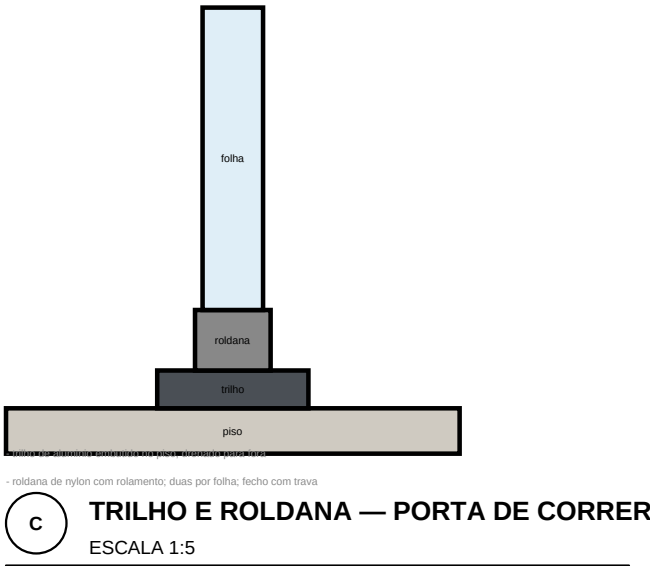
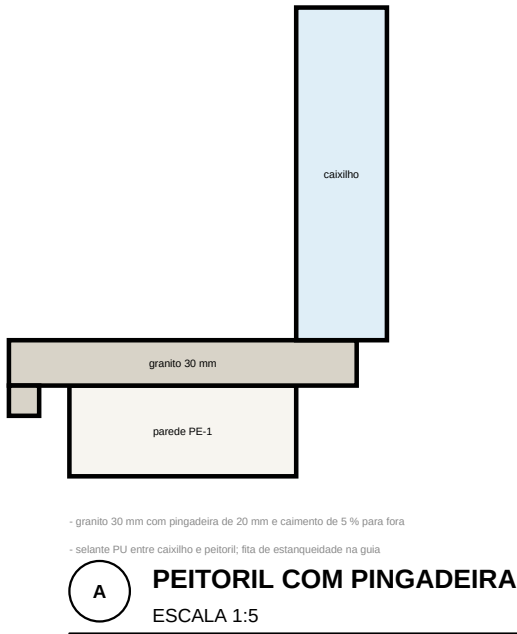
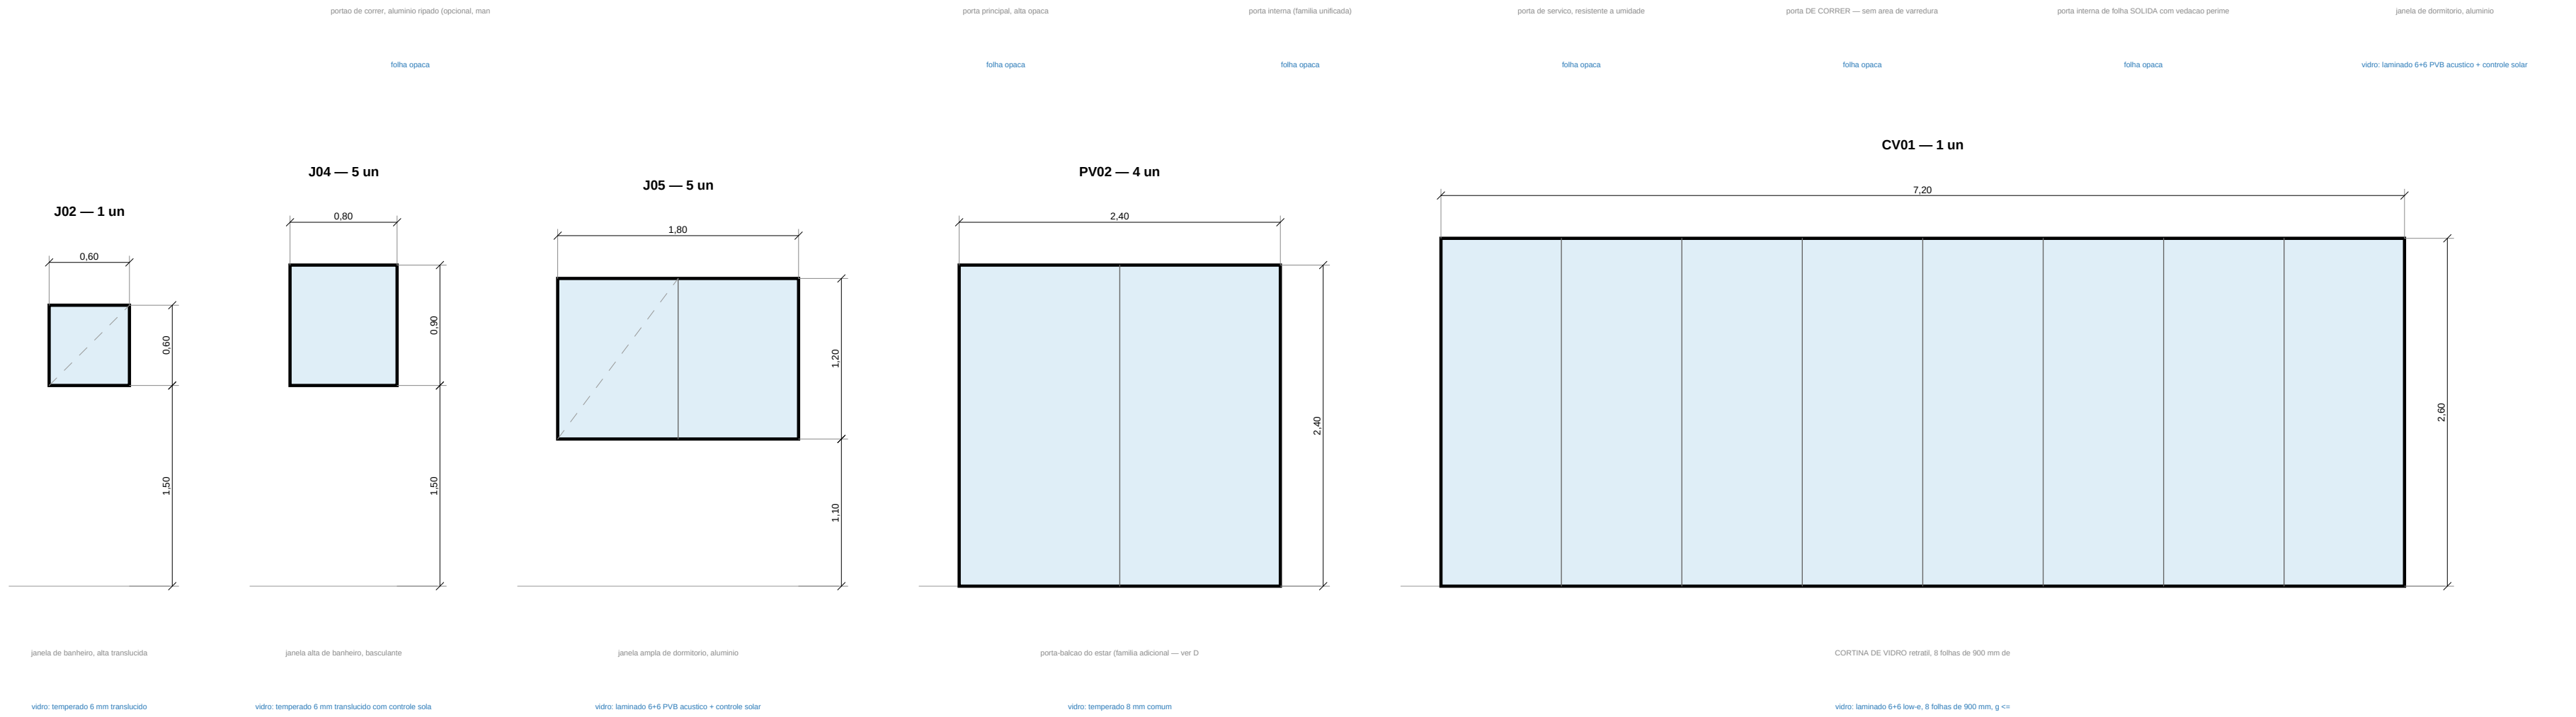


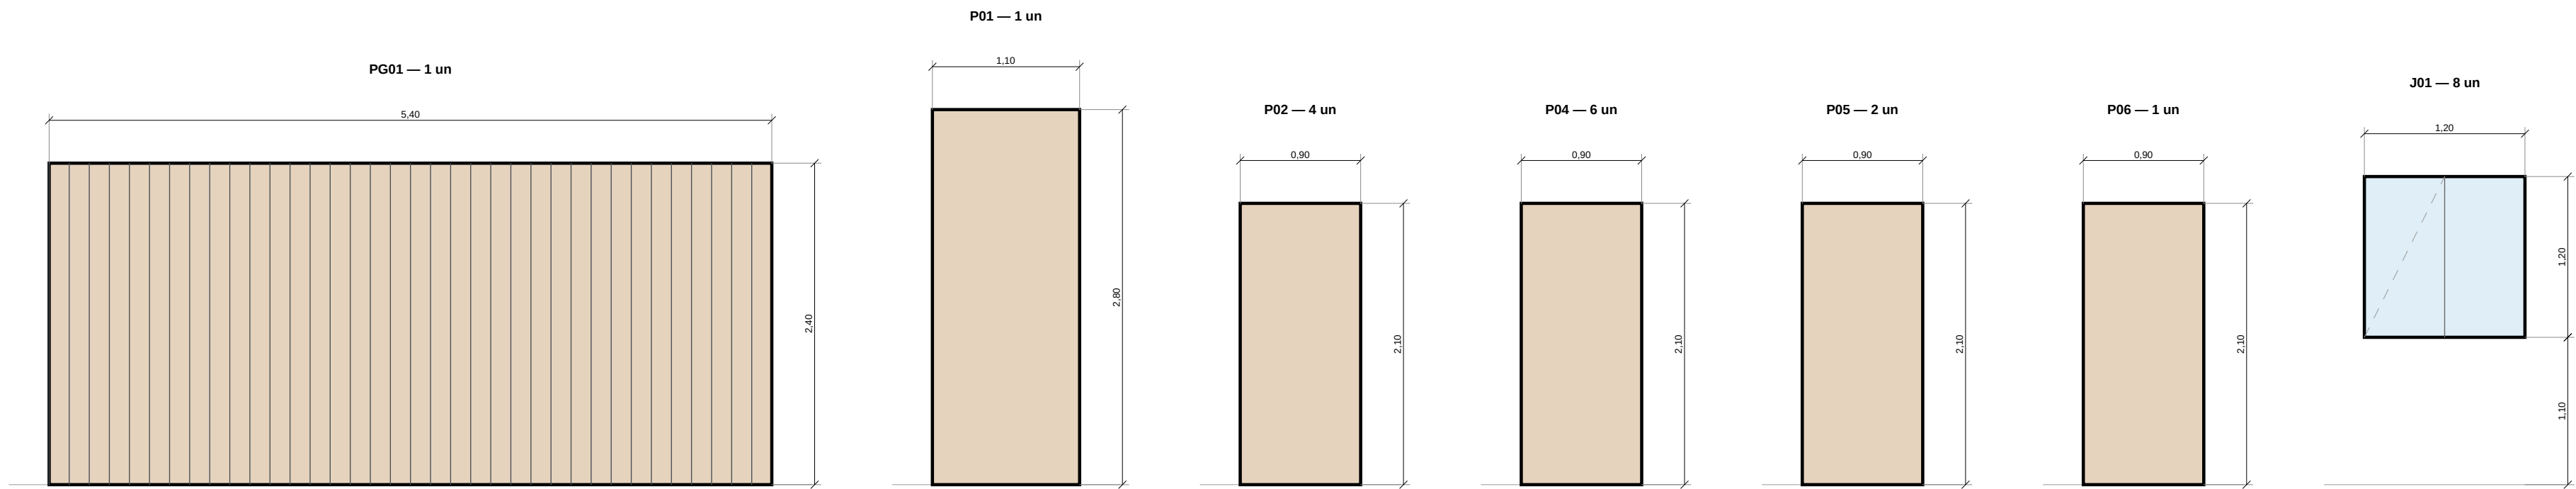

- NOTAS**
- 1. Uma referência por família em uso, com largura e altura, perfil, quantidade e o vidro que a regula de fator solar (veja ver_Vidros).
 - 2. Famílias declaradas SEM USO (J02, PV02) ficam fora, enquanto que não estão em VACOS não é comprada.
 - 3. Detalhes 1:5 — perfil com pingadeira, sulcos de porta externa, vidro e sistema de porta de correr, ripa e guia de perfil — são os quatro elementos que decidem a estanqueidade.
 - 4. Aluminio grão em todas as famílias (ALUMINIO_MATIZADO), sem PVC, sem ventilação.

PROJETO PORTO REAL			
RESIDENCIA UNIFAMILIAR (MARAUAS - AM) SOUZA TATIANA-PS			
PROJETO ARQUITETONICO			
ESQUADRIAS — TIPOS, QUANTIDADES E DETALHES			
BASE GEOMETRICA	ESCALA	EMISSAO	PROJETO
Lista Consolidada	1:40 • 1:5	ESTUDIO PRELIMINAR RIM	52
em PDF (previsão)	FORMATO A1	NAO LIBERADO PARA OBRA	
UNIDADE MESTRE: mm	MALHA 600/600/300	SEM ART / RINT	06-78 REV104