




1 CORTE LONGITUDINAL (SUL -> NORTE)
ESCALA 1:25

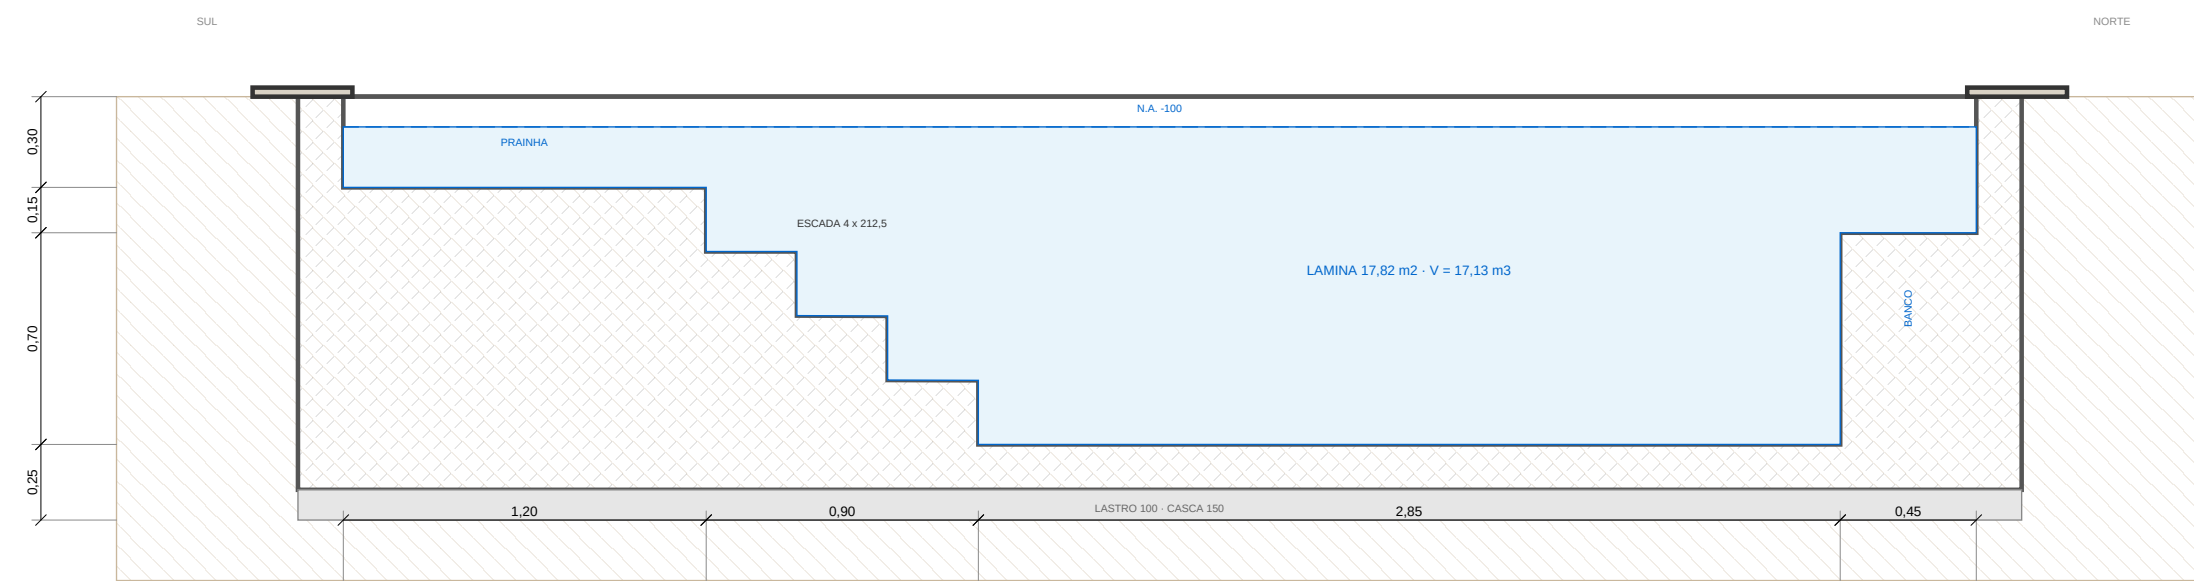


2 CORTE TRANSVERSAL PELO DRENO (LESTE -> OESTE)
ESCALA 1:25

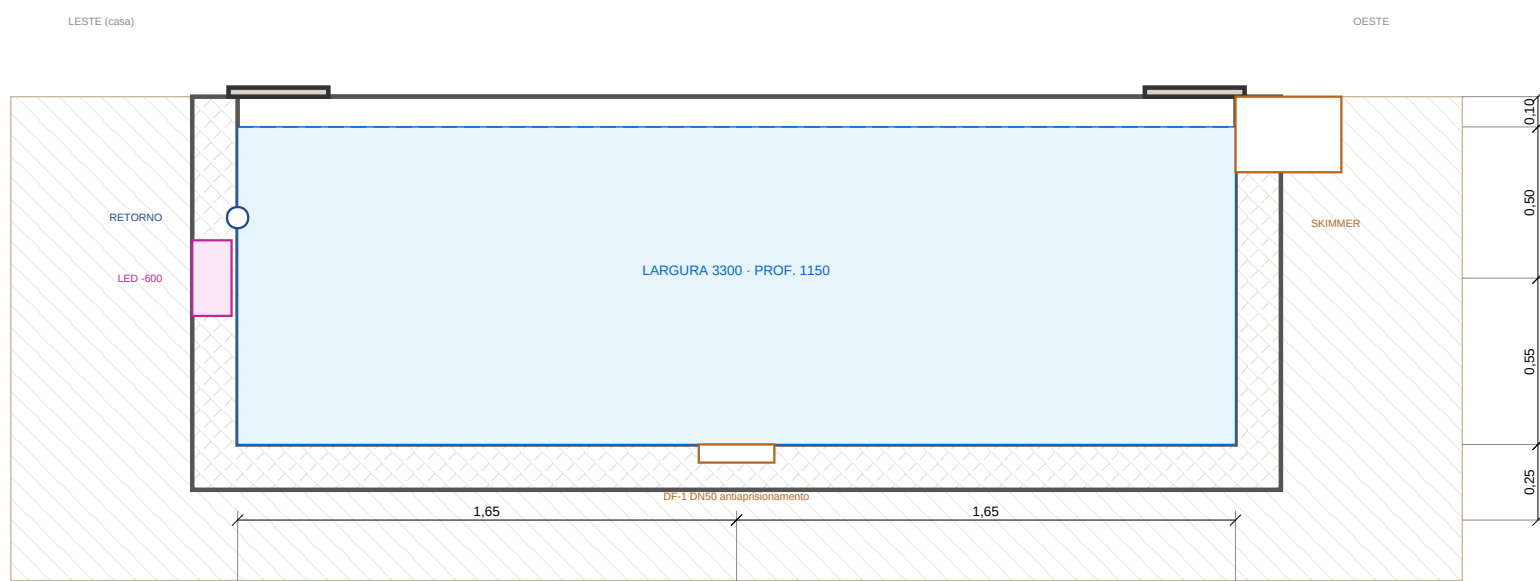


3 ESCADA DE PRAIA
ESCALA 1:10

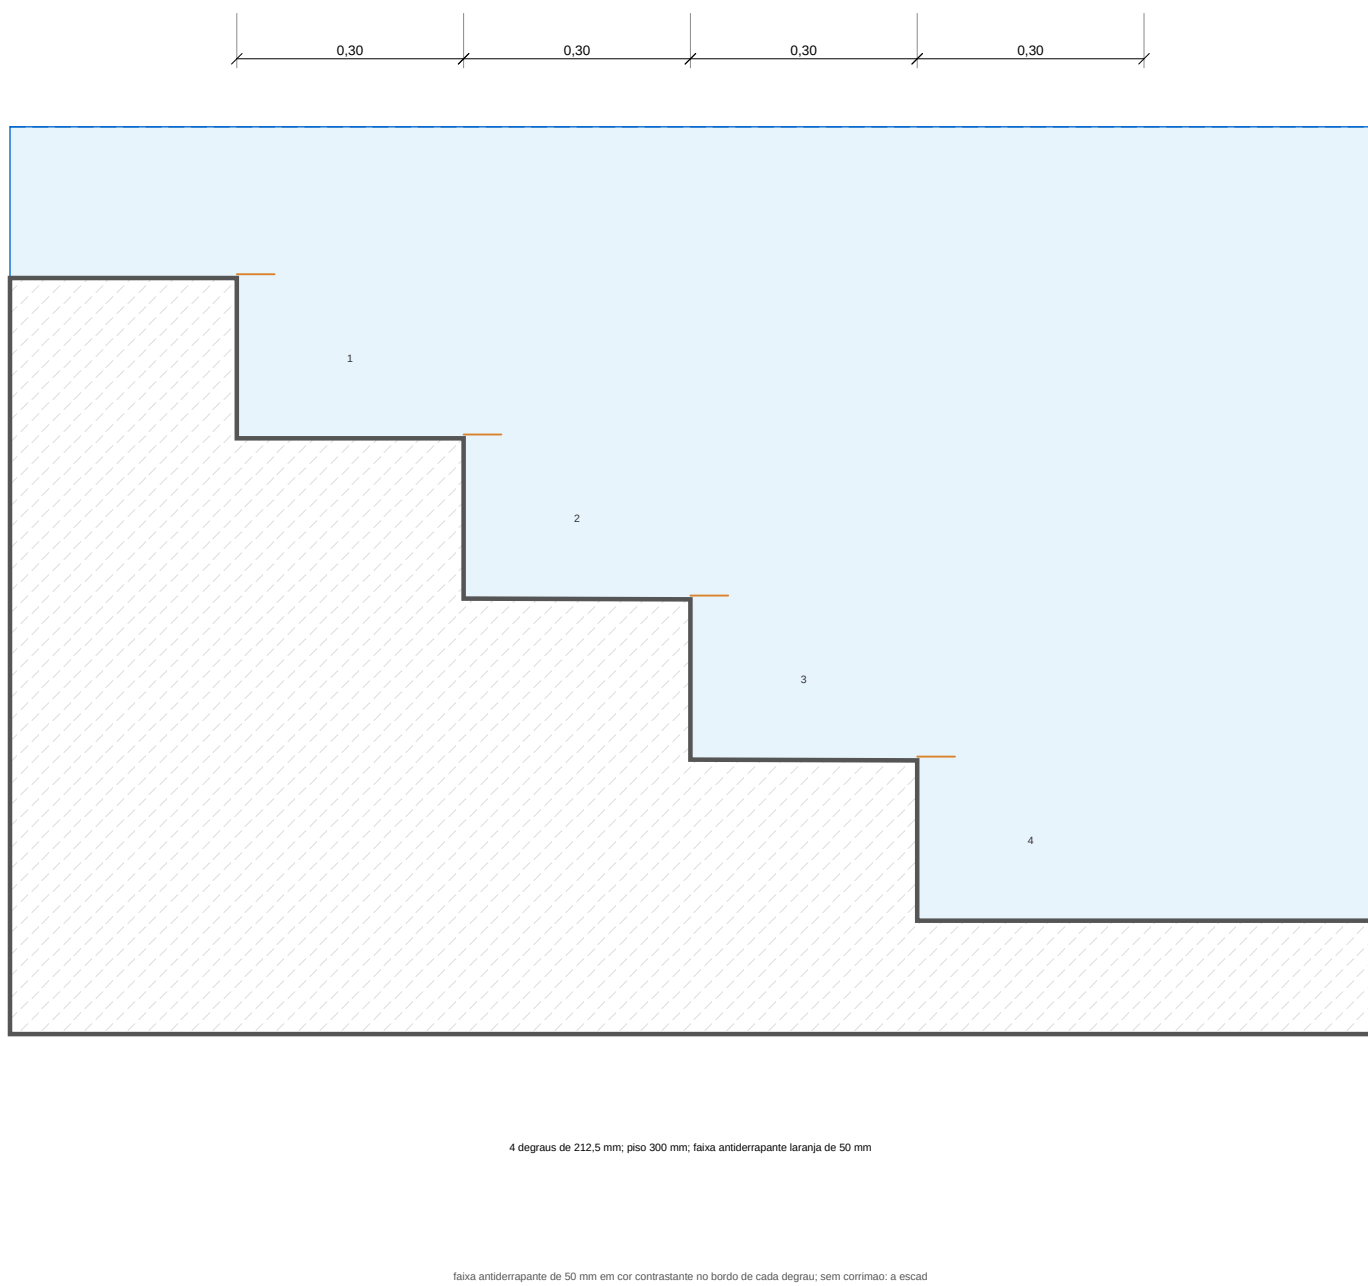



4 BORDA COM PINGADEIRA E FAIXA SECA
ESCALA 1:5

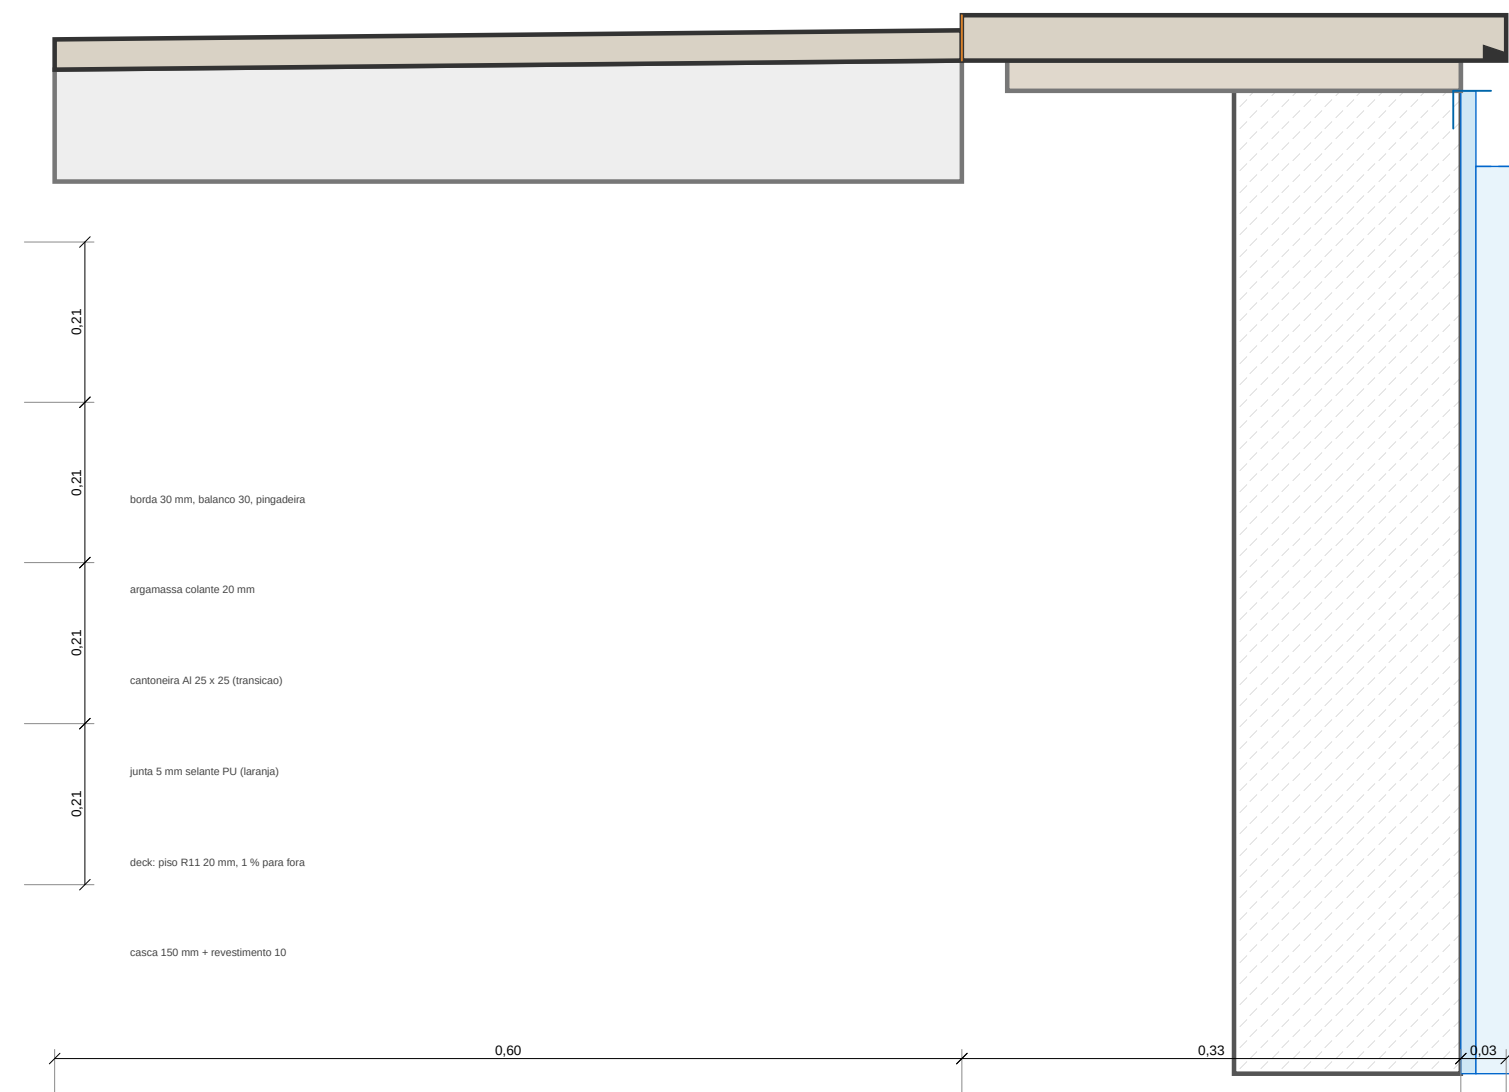

5 NICHOS DO LED E CAIXA DE PASSAGEM
ESCALA 1:5

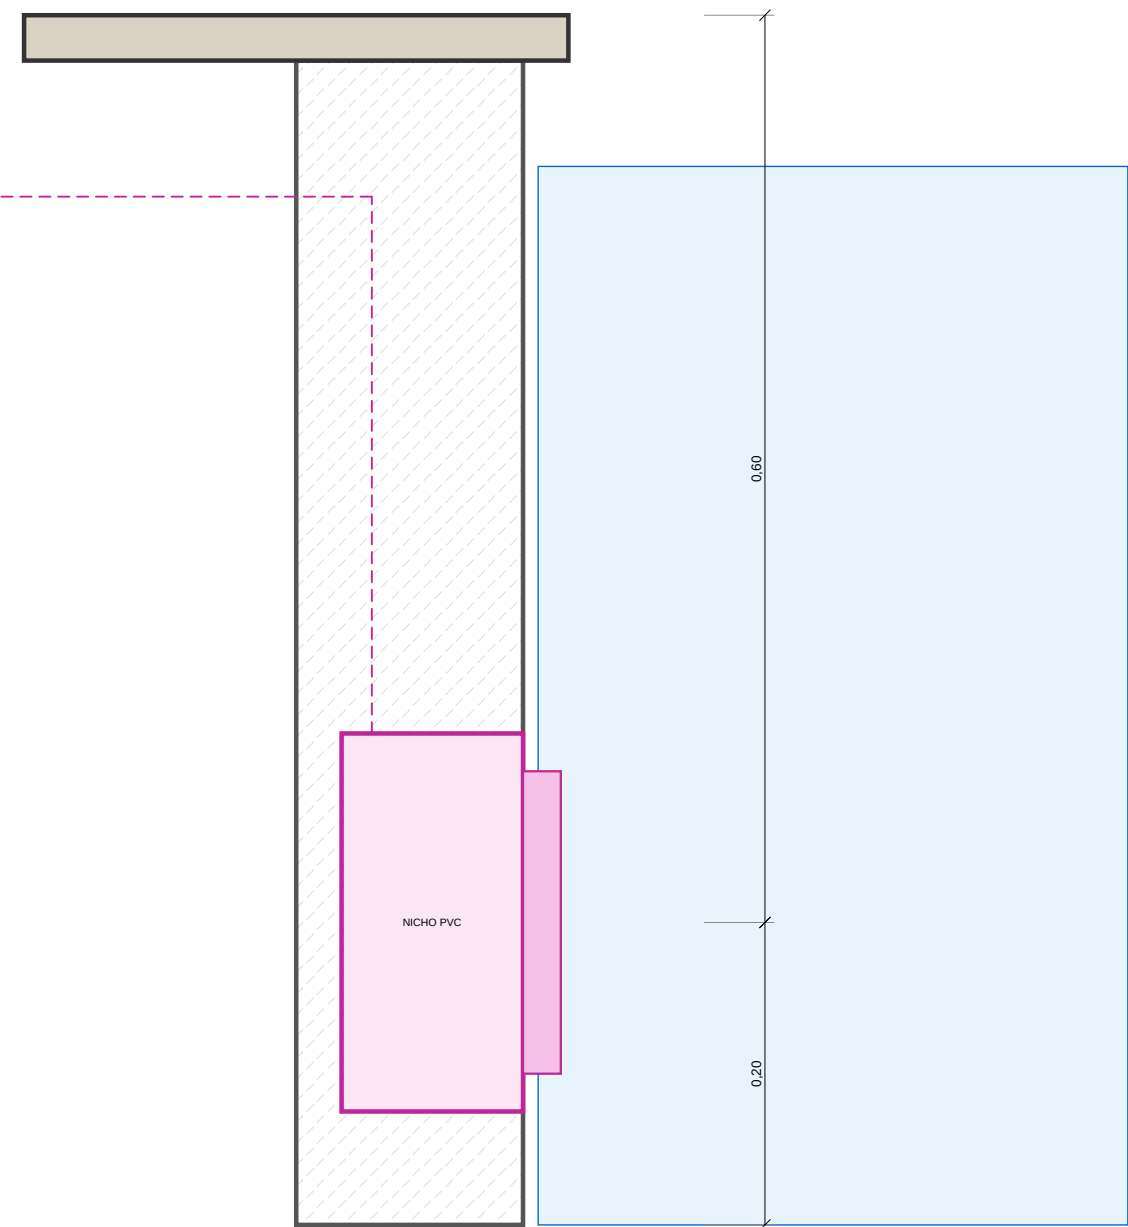

6 PLANTA DE ILUMINACAO SUBAQUATICA
ESCALA 1:50

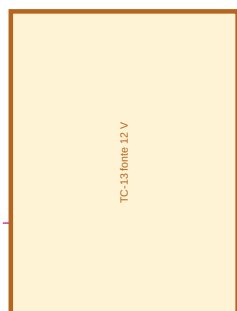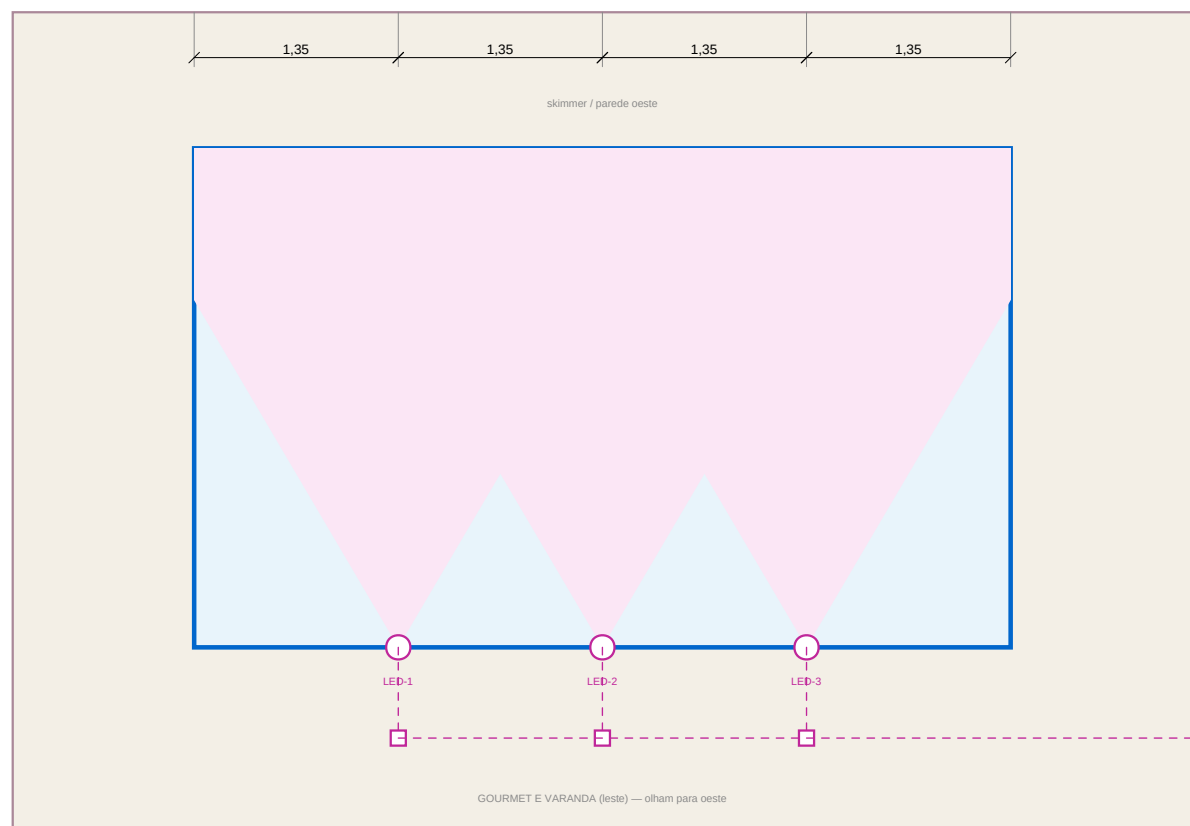

ITEM	VALOR	ORIGEM
Laurel e volume	17,02 m ² / 17,12 m ²	FISCINA
Nível da água	-100 mm	alvenaria [9]
Plumão	1200 x 200 mm	FISCINA
Escada	4 x 212 x 1 800 mm, altura 800	desnatel / 250 [9]
Fundo	1150 mm (barra 1003)	FISCINA
Banco	460 mm, assento p. 450	FISCINA
Caixa / bacia	160 / 200 mm, encanado p. 400	encanato/plástico [9]
Concreto	4,57 m ³	CONCRETO ARMADO S/A 35 MPa, LACSA
Impermeabilização	30,42 m ²	area mictória
Borda	33 peças de 800 mm, 17,4 m	paralelo da laje

LUMINACAO SUBQUATICA (SELV 12 V)							
LED	x mm	z mm	W	lin	CABO m	mm2	QUEDA
LED-1	650	-600	18	1530	11.8	1.5	3.7 %
LED-2	750	-600	18	1530	11.5	1.5	3.3 %
LED-3	850	-600	18	1530	10.2	1.5	2.9 %
TOTAL			54				3.02 WH/m2

REGRAS DA ILUMINACAO

REGRA	PROJETO
Letão	alentejo bruto - mais perto do gourmet, que oferta para servir - a lanchada
Fora	fora SELV 12 V, 70 VA, no quarto estande de TC-13, protegida por DR
Não	richo de PVC embutido na caixa, com calha de passagem estande no deck
Previsão específica	1,02 W/m ² na base 2,0-4,2 (H)

CONFERENCIAS DESTA P

O QUE	COMO	
escada, espelho	4 degraus de 212,5 mm (para 250)	OK
escada, piso	300 mm (para 300)	OK
escada sobre trecho fundo	anelos 900 mm, sacos coveira a 3750 mm	OK
luzes para UF	1200 mm (para 900)	OK
luzes para rede	1200 mm (para 900)	OK
luzes saca-foto	1200 mm (para 900)	OK
luzes saca-ventilador	900 mm (para 600)	OK
luzes saca-declarado por lado conf	luz 1200x1200, rede 1200x1200, rede 1200x1200, rede 900	OK
circuito do pisca-chocho bomba e	TUE 17 700 VA coroa 475 VA bomba 851 + bomba dos LEDs	OK
potência de luz por m²	5,00 MW (para 10-4)	OK
quatro x 12 V LED	3,00 W em 1,5 m² a 12 V	OK
quatro x 12 V LED	5,00 W em 1,5 m² a 12 V	OK
quatro x 12 V LED	2,00 W em 1,5 m² a 12 V	OK
LEDs na parede vertical para a casa	potência 100W	OK
potência da bomba - e da BOM	17 m e 17,4 m	OK

NOTAS

- Anel da água: 100 mm (diâmetro), Platina 300 mm; escada de praia de esboço (212,5 x 300 mm) na largura interna, fundo 1150 mm; banco com assento a 450 mm.

- Colunas: concreto armado 30 MPa, casca de 150 mm, tela dupla 8 mm x 15 (H); lauro 100 mm; fundo da escaneca a -1400 mm. Impermeabilização: cristalinizante em concreto fresco + argamassa polimérica biocomponente em 2 demãos (H); teste de estanqueidade de 72 h antes do revestimento.

- Borda: 600 x 300 x 30 mm, polipropileno R11 (Bordc, o deck e WPC), bordo bolido e pingadeira, deck com 1 % para fora da piscina, iluminação: 3 LEDs 2700-3000 K a 500 mm, SELV 12 V, 3,03 W/m2.

- **Notas:** marcadão (H) em homenagem ao projeto: limites da NBR 13231 e prática de piscina residencial.

PROJETO PORTO REAL

RESIDÊNCIA UNIFAMILIAR | MANAUS - AM | SUITE TARUMA (H)

PROJETO ARQUITETÔNICO

PISCINA: CORTES, ESCADA, BORDA E ILUMINACAO

BASE GEOMÉTRICA	ESCALA	EMISSÃO	PRIMAVERA
Lista Consolidada	indicada	ESTUDO PRELIMINAR R1B4	70
pos-R132 (pre-eleito)	FORMATO A1	NÃO LIBERADO PARA OBRA	
UNIDADE MESTRE - 100m	MALHA 600/600/350	SEM ART / RBT	06-76 REB R1B4