


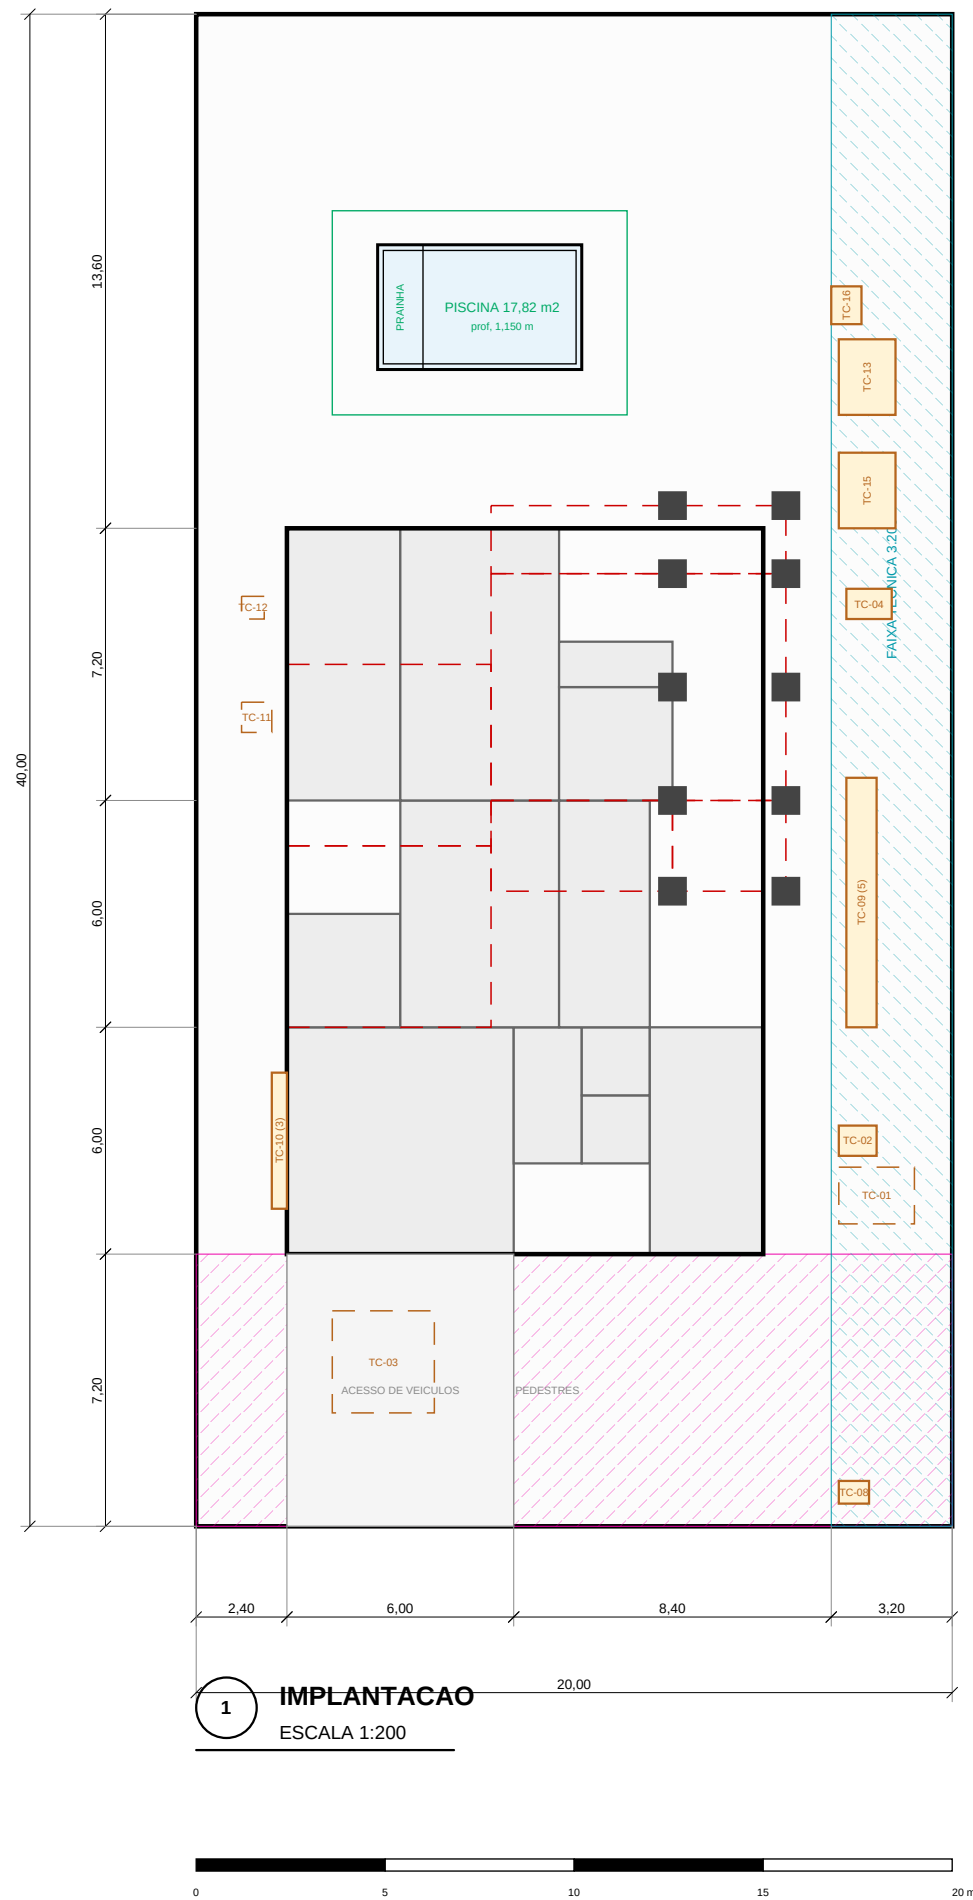

VERIFICACAO URBANISTICA (H)

PARAMETRO	PROJETO	LIMITE	
Taxa de ocupação	33,21 %	até 50 %	OK
Coef. de aproveitamento	0,372	até 1,00	OK
Galvao	2 pavimentos	até 4	OK
Recuo frontal	7200 mm	conforme 50/00 (H)	OK
Recuo lateral sup.	2400 mm	sem limite no caso	OK
Recuo lateral inf.	3000 mm	até 3000 mm	OK
Recuo de fundo	13800 mm	até 15000 mm	OK



- NOTAS
- * Lote: 25.000 x 40.000 mts = 800.00 m².
 - * Recuo: frontal 7.200 / lateral sup. 2.400 / lateral inf. 3.000 / fundo 13.800 mts.
 - * Parametros do SUD: Taxa de Ocupação (TO) = 50%; Coeficiente de Aproveitamento (CA) = 1,00; Recuo Frontal (RF) = 7,20 m; Recuo Lateral Superior (RLS) = 2,40 m; Recuo Lateral Inferior (RLI) = 3,00 m; Recuo de Fundo (RFU) = 13,80 m.
 - * Sem muro frontal, mural lateral e de fundo 0 a 2,00 mts.

PROJETO PORTO REAL

RESIDENCIA UNIFAMILIAR (MANSÃO) - AM | SOUS TATIANA (H)

PROJETO ARQUITETONICO

IMPLANTACAO E SITUACAO

BASE GEOMETRICA Linha Consolidada SUD (SUD) (previsão) UNIDADE: METROS - MM	ESCALA 1:200 FORMATO: A1 MATERIAL: 60/60/60/60	EMISSAO ESTUDIO PRELIMINAR R54 Linha Consolidada PARA OBRAS SEM ART / RNT 06/48 REV 054	PROJECION 01
--	---	---	-----------------