


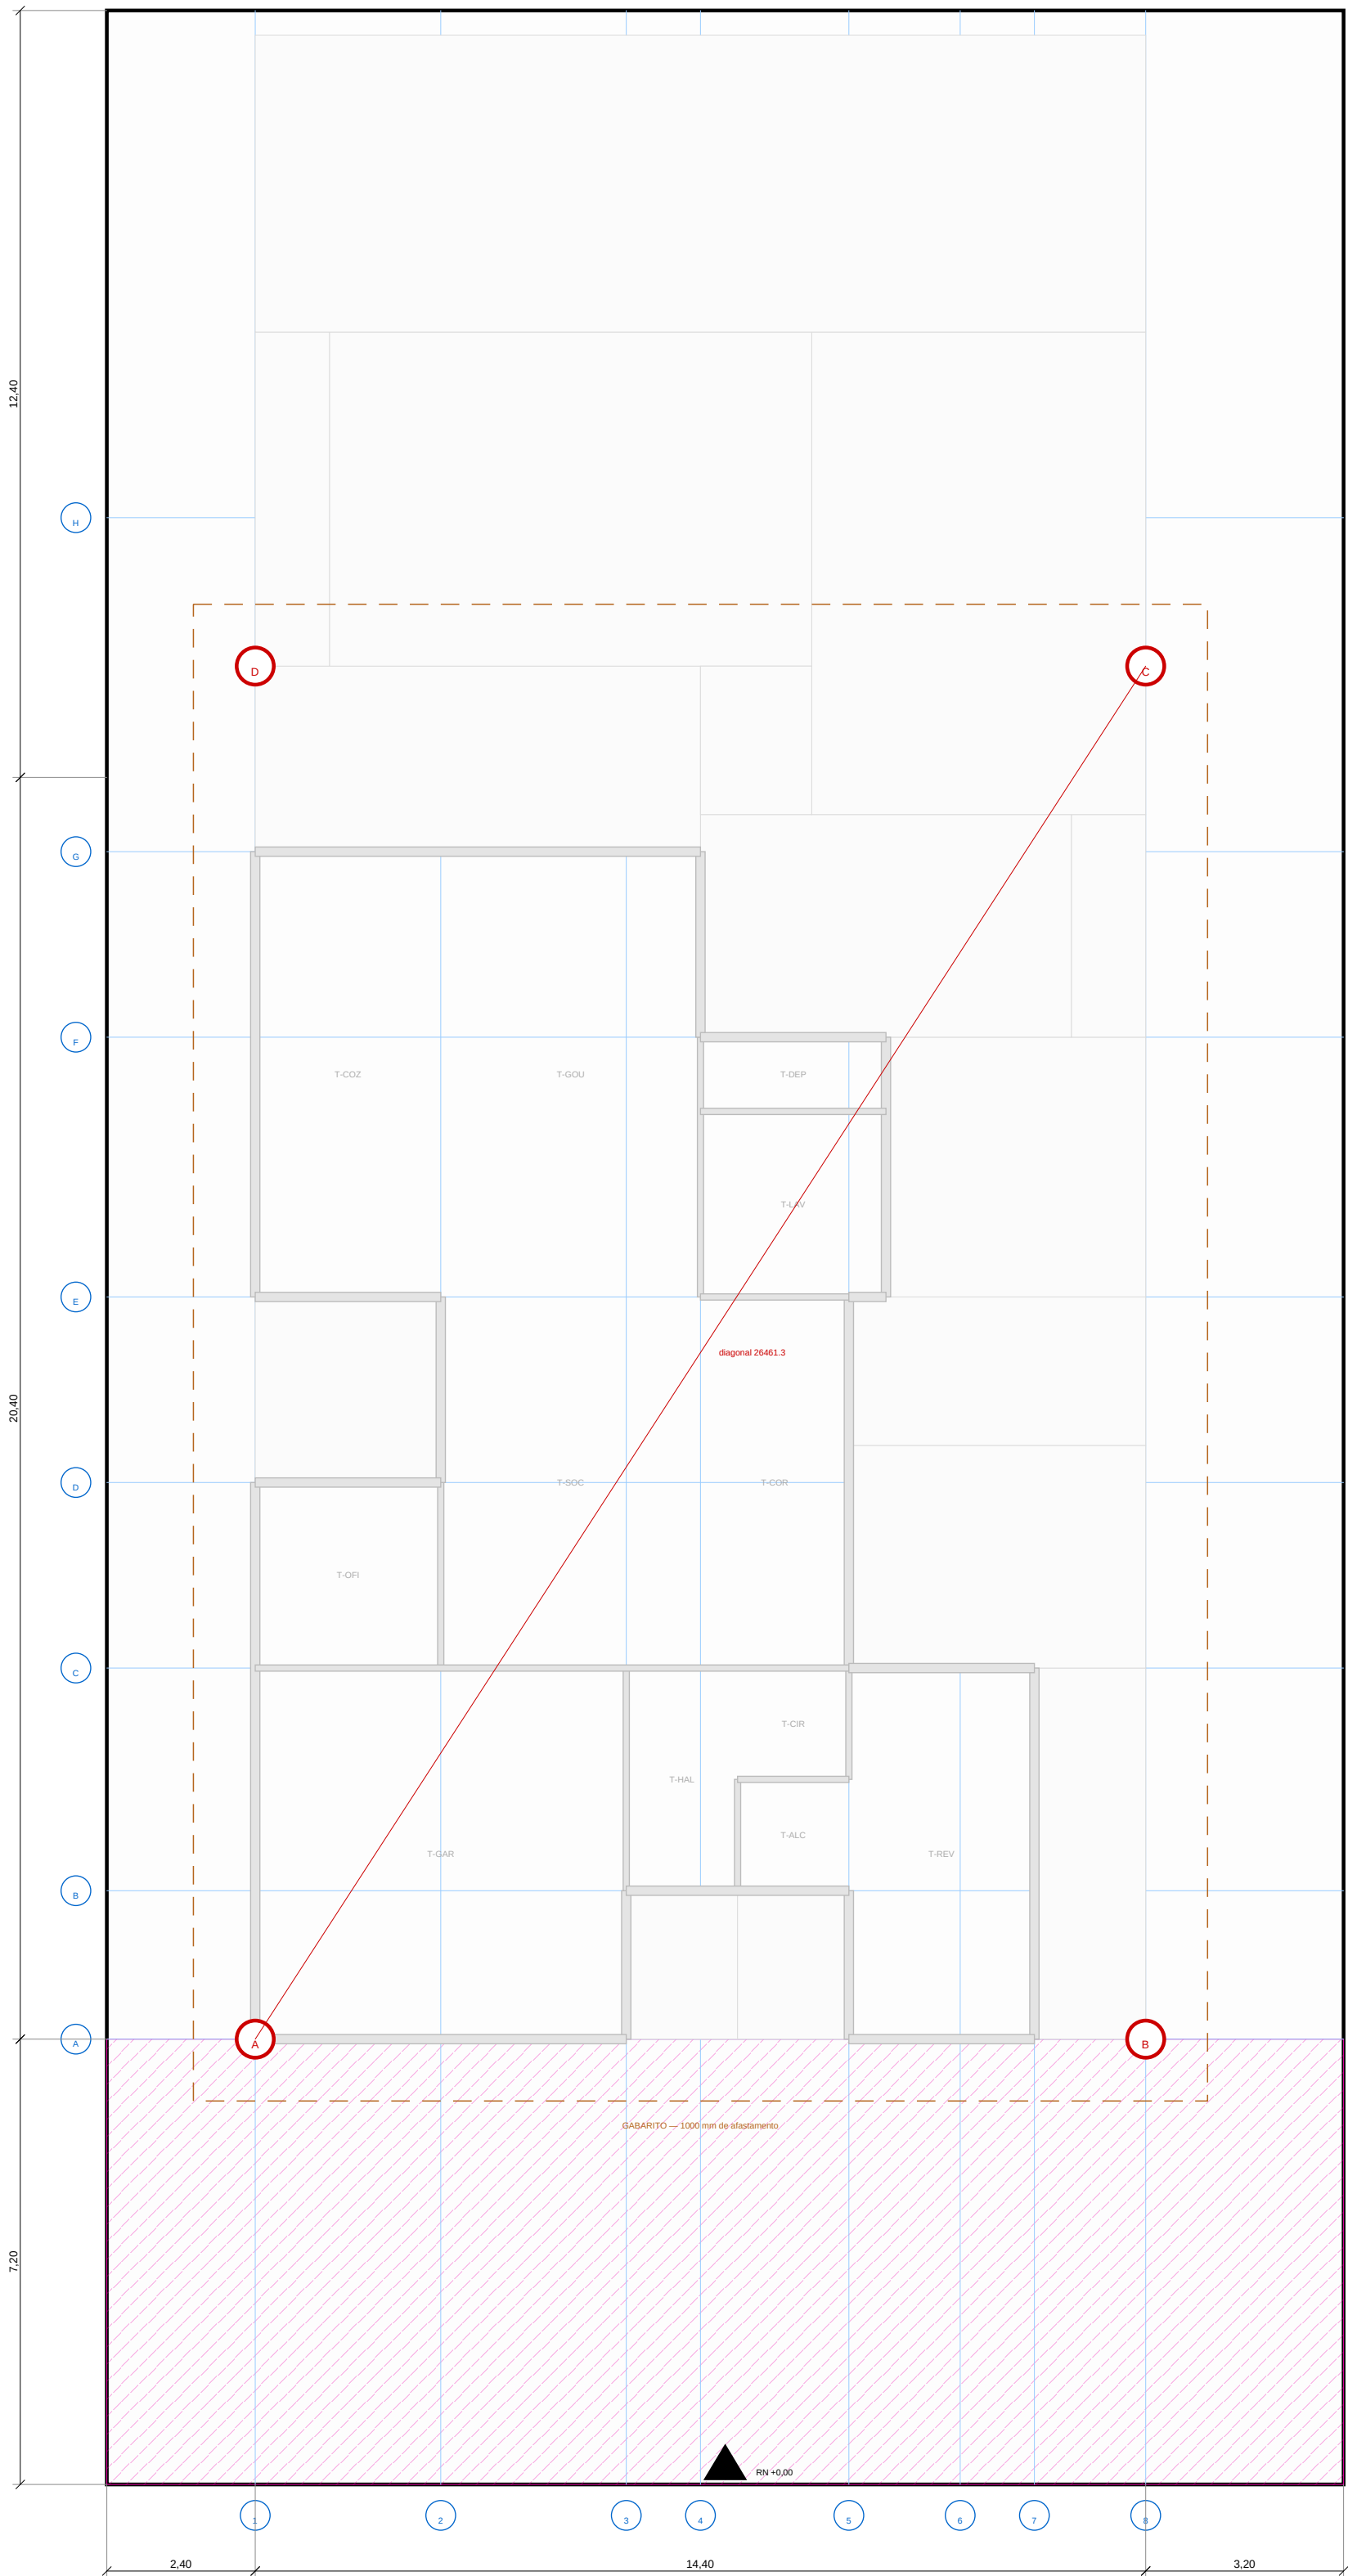

COORDENADAS DOS CANTOS (mm)

CANTO	X	Y	DIVISA SUL	DIVISA NORTE	TESTADA	QUIBO	DIAGONAL
A	2400	7200	2400	17600	7200	32800	26461,3
B	18800	7200	18800	3200	7200	32800	26461,3
C	18800	28400	18800	3200	28400	19600	26461,3
D	2400	28400	2400	17600	28400	19600	26461,3

PROCEDIMENTO DE LOCAÇÃO

#	PASSO	CRITÉRIO DE ACEITE
1	Conferir as divisões com o material de mão de obra	divergência acima de 10 mm interromper a locação
2	Instalar o RMC marca de concreto 100 x 200 x 100 mm, fora da área de obra	fora da área de obra
3	Montar o gabarito a 1000 mm do cantoneiro	perguntar 75 x 75 a tubos 20 x 100
4	Marcar os eixos X (1) e Y (1) a 10 m no gabarito	linha coordenada múltipla de 200 mm
5	Colar cado canto dos QUADs dividos	verificar em cado, erro de cado de soma
6	Conferir a diagonal A-C	26461,3 mm com tolerância de 10 mm
7	Conferir o quadrado por 3-4-5 em cada canto	antes de qualquer concretagem
8	Registrar em ata com foto e modelo	gabarito continuo nos dois lados da obra, conferência

EIXOS MODULARES

DIREÇÃO	VALORES (mm)
X (1) e Y (1)	2400 - 5400 - 8400 - 9600 - 12600 - 13800 - 15000 - 18000
Y (1) e X (1)	7200 - 9600 - 13200 - 14200 - 15000 - 28400 - 29400 - 32800
Módulo	principal 600 mm - submódulo 300 mm
Origem	canto frontal esquerdo da base
Unidade	milímetros

NOTAS

- Locação é o único documento em que o erro não tem contorno técnico: a casa sai do lugar.
- Cada canto é o cado dos QUADs dividos, nunca em cado acumulados — erro de cado de soma, erro de referência independente não.
- Conferência obrigatória pela diagonal 26461,3 mm entre A e C antes de concretar o radier.
- Ata ou ata de locação, alinhado ao medidor TC-06, cado 0,00 (+) para acabado do terreno.

PROJETO PORTO REAL

RESIDENCIA UNIFAMILIAR (MANSÃO - AM) | SOBR TATIANA-PS

PROJETO ARQUITETONICO

LOCAÇÃO DE OBRA E GABARITO

BASE GEOMETRICA

União Consolidada

Projeto (previsão)

Unidade: milímetros (mm)

ESCALA

1:100

FORMATO A1

Módulo: 600/300 (mm)

DIVISÃO

ESTUDO PRELIMINAR R54

IMÓ LIVRE PARA OBRA

SEM ART / RNT

PROJETO

31

06-48 REV 054