


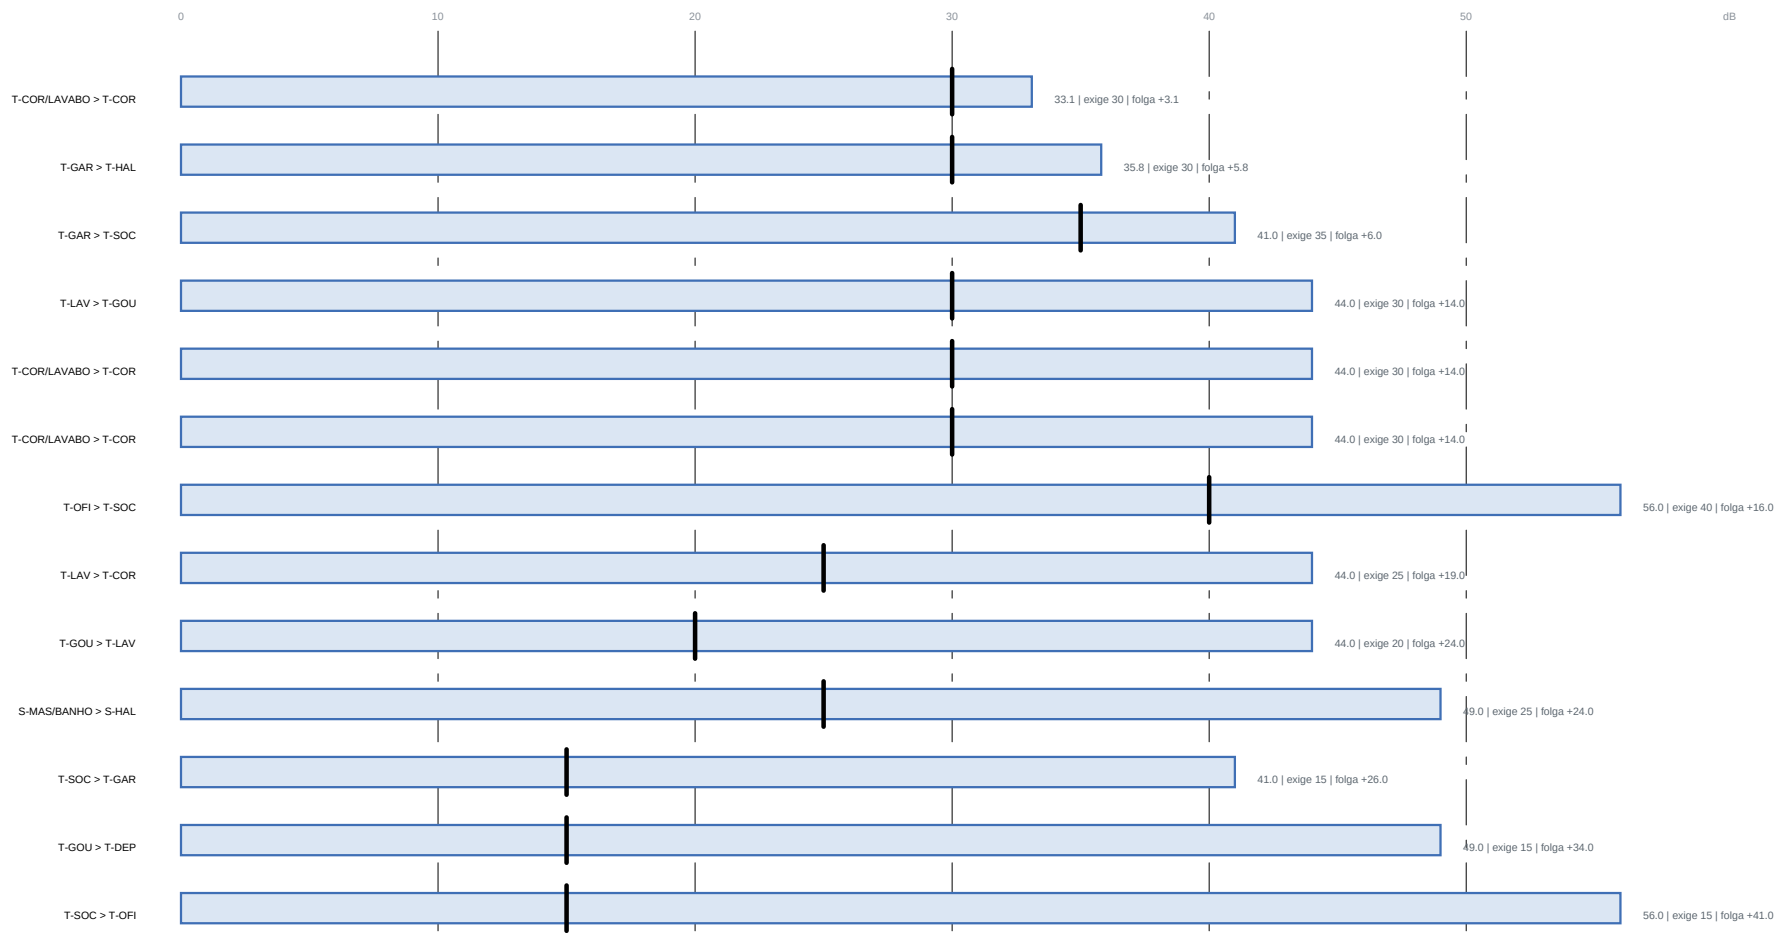

Nota: o isolamento obtido, traço vertical: o nível (valor da fonte menos nível do receptor, NBR 10152)

O QUE MUDOU EM R52

ONDE	ANTES	DEPOIS	POR QUE
Banho compartilhado - hall de entrada	porta de correr (Rw 25) - conjunto de 20,2 dB	parede CEGSA, 44 dB	o acesso de volta passou para a circulação
Banho compartilhado - quarto eventual	porta com (Rw 25) - conjunto de 25,5 dB, nível 30	parede CEGSA, 44 dB	era a por passagem da casa, e não era a saída
Hall - garagem	porta com - 36,9 dB, nível 30	PDS isolada vedada - 36,9 dB	porta entre garagem e casa tem dupla função para ser móbica
Banho compartilhado - circulação	não havia porta	PDS isolada vedada - 35,7 dB, nível 25	único acesso do banho, e abria para fora
Bloco do chuveiro	encostado na parede do hall	canto arredondado, toldo e janela alta	consequência da porta nova, a regra dos 900 cm de bloco responde a primeira tentativa

TABELAS ADOTADAS

ITEM	VALOR	FONTE
Fonte: boca sanitária	75 dB(A)	prática corrente de acústica
Fonte: bloco do chuveiro	70 dB(A)	prática corrente de acústica
Fonte: cozinha e gourmet	70 dB(A)	prática corrente de acústica
Fonte: sala e jantar	70 dB(A)	prática corrente de acústica
Fonte: garagem	70 dB(A)	prática corrente de acústica
Fonte: máquina de lavar e secar	70 dB(A)	prática corrente de acústica
Fonte: oficina	60 dB(A)	prática corrente de acústica
Límite: banho	45 dB(A)	NBR 10152:2017 (circulação e entrada adjacente)
Límite: circulação	45 dB(A)	NBR 10152:2017 (circulação e entrada adjacente)
Límite: cozinha	45 dB(A)	NBR 10152:2017 (circulação e entrada adjacente)
Límite: depósito	55 dB(A)	NBR 10152:2017 (circulação e entrada adjacente)
Límite: dormitório	35 dB(A)	NBR 10152:2017 (circulação e entrada adjacente)
Límite: entrada	45 dB(A)	NBR 10152:2017 (circulação e entrada adjacente)
Límite: estar	45 dB(A)	NBR 10152:2017 (circulação e entrada adjacente)
Límite: garagem	55 dB(A)	NBR 10152:2017 (circulação e entrada adjacente)
Límite: office	45 dB(A)	NBR 10152:2017 (circulação e entrada adjacente)
Límite: oficina	55 dB(A)	NBR 10152:2017 (circulação e entrada adjacente)
Límite: serviço	50 dB(A)	NBR 10152:2017 (circulação e entrada adjacente)
Fonte: acústica	Flw 25 dB	Nota de mercado declarada
Fonte: cozinha	Flw 25 dB	Nota de mercado declarada
Fonte: sala	Flw 25 dB	Nota de mercado declarada
Fonte: depósito	Flw 25 dB	Nota de mercado declarada
Fonte: isolamento	Flw 30 dB	Nota de mercado declarada

NOTAS

Esta planilha serve para o proprietário perguntar e que 100 verificações não sabem responder: quem entra na casa ouve o chuveiro do banheiro da entrada?

Nota: A parede era bloco (Rw 25), Flw 40 e a porta era de correr (Rw 25), o conjunto entregava 20 dB. Em acústica o bloco DOMINA — não se faz média aritmética do isolamento, se soma energia que passa.

Isolamento no ar (nível ENTRE) zeros. Dentro da file social o ruído não é definido, é o programa.

O adotado igual ao R52 (nível de isolamento) não é pre-verificação de projeto, não entra no campo da NBR 10152-3.

PROJETO PORTO REAL

RESIDENCIA UNIFAMILIAR (MANSÃO - AM) | SOBR TATIANA-PS

PROJETO ARQUITETONICO

DESEMPENHO ACUSTICO ENTRE AMBIENTES

BASE GEOMETRICA	ESCALA	EMISSAO	PROVA
Lista Consolidada	s/ escala	ESTUDIO PRELIMINAR R54	
Flw R52 (previsão)	FORMATO A1	IMPOSSIVEL PARA ORCA	39
UNIDADE MESTRE: mm	MILHA 605000000	SEM ART / INT	06-48 REV04