



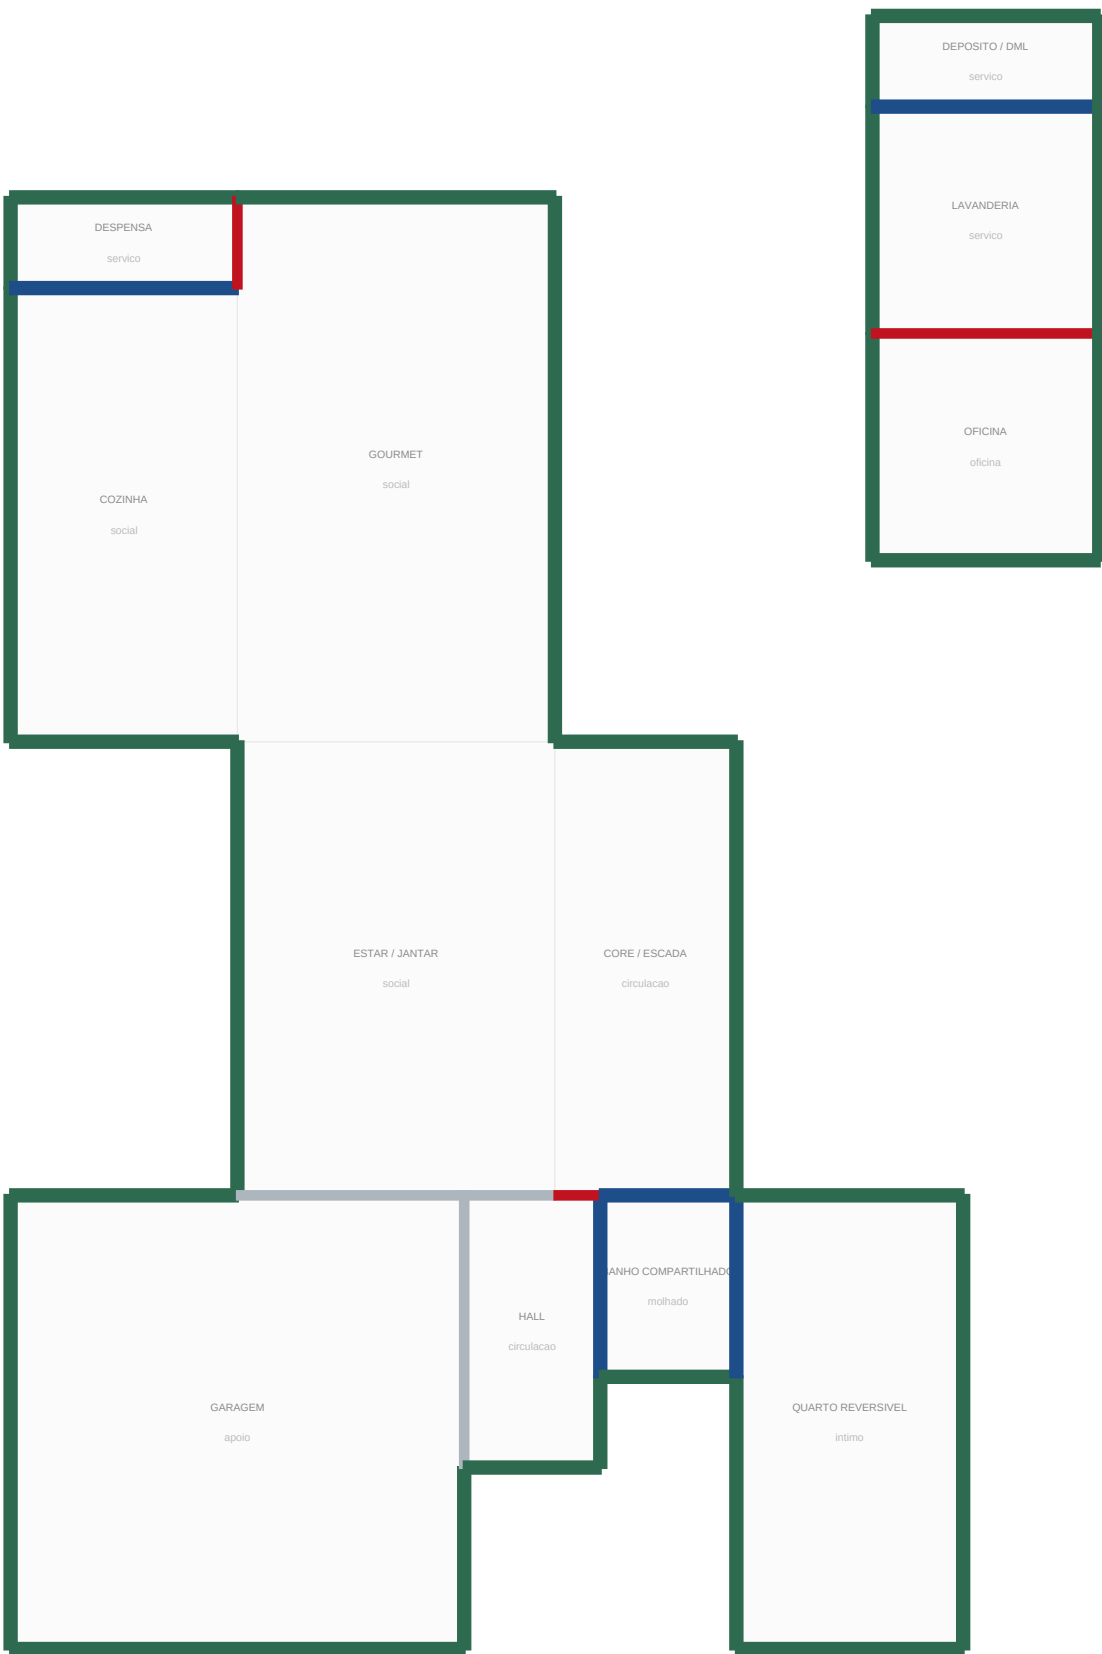

TERREO

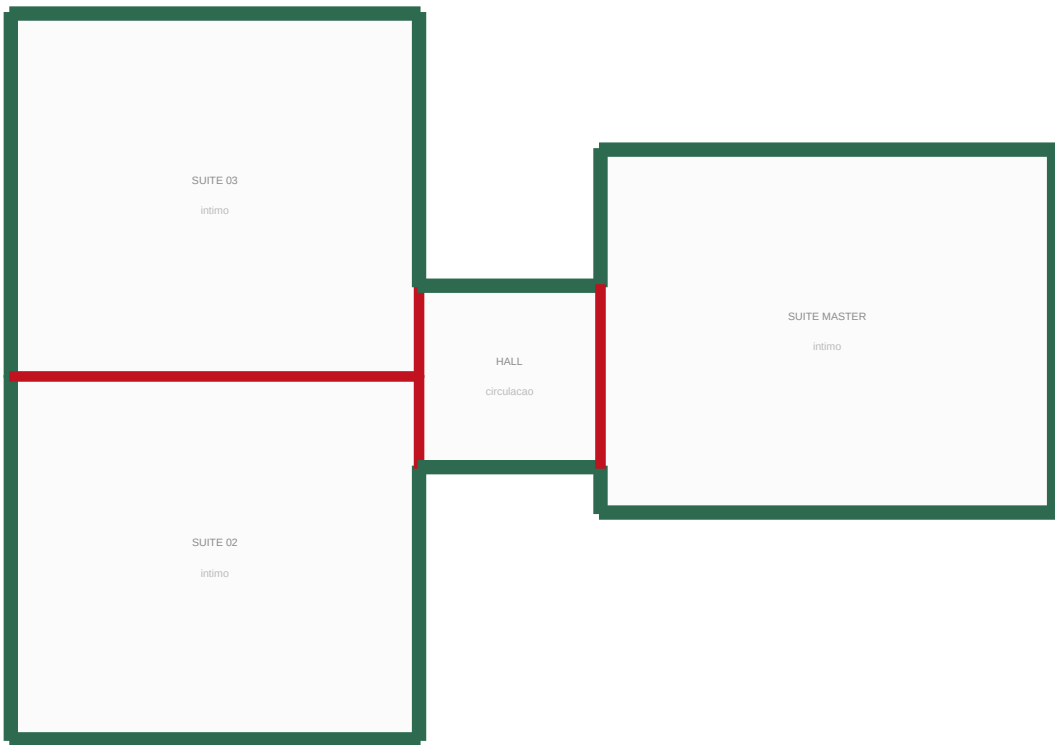

SUPERIOR

FAMÍLIAS DE VEDACÃO — COMPOSIÇÃO POR EXIGÊNCIA

COD	FAMÍLIA	eps	flw	AREA m2	inibico	ONDE SE APLICA
FE-1	Paralela externa única	200	40	300.00	1.12	telas de facas externas, sem acossos
FE-1	Paralela hidráulica interna	100	60	12.70	1.20	apenas onde passa por dentro de vigas (CNC) ou na base
FE-1	Paralela acústica	100	60	10.00	1.20	telas e telas de fundo, telas e telas de fundo
FE-1	Divisória interna simples	100	40	30.00	1.00	divisória de janelas homogêneas (janelas com telas, telas)
	TOTAL			478.00		

FE-1 — cinerética 10 + EPS 20 (200 mm) + montante 90 c/ 10 + gesso 12,5 + acabamento
O ISO sempre constrói e, ao mesmo tempo, quebra termica e barreira de vapor do lado quente-unidade. São funções principais NAO e economias de energia (payback longo), e evitar condensação no montante.

FE-1 — gesso 12,5 + montante 90 c/ 10 + gesso 12,5 + reforço para base
A espessura de 200 mm evita para acomodar o tubo (CNC). Usar 200 mm não faz diferença e despende de área útil.

FE-1 — dupla chapa 12,5 + montante 48 c/ 10 + dupla chapa 12,5
Dupla chapa e o único ganho acústico básico: +5 dB por chapa adicional. Despende-se a mesma área e espessura modular.

FE-1 — gesso 12,5 + montante 70 c/ 10 + gesso 12,5
Fe 11, 48 (a partir do mínimo de 100) 10275 é entre ambientes de mesma unidade. Reduzir aqui não produz diferença perceptível.

POR QUE O ISO STRIP, SE O PAYBACK É LONGO

Ganho energético: $dU = 0.356 \text{ kWh/m}^2$ sobre $387 \text{ m}^2 \rightarrow 776 \text{ kWh/ano}$, payback de 18 anos (4).

Isolado, o argumento energético NAO sustenta o investimento.

O argumento é outro: em clima quente-unidade com ar condicionado o vapor migra

de FORA para DENTRO. O montante de aço fica mais frio que o ponto de emalho

externo (28.2 C a 32 C / 80 % UR) e a água condensa DENTRO do painel — sobre o

aço, encharcando a la, sem sinal visível até a patologia estar instalada.

O XPS de célula fechada e quebra termica E barreira de vapor, na posição certa

(lado quente-unidade). Um material, duas funções. Precisa ser CONTINUO: aplicar

por partes cria justamente o ponto frio onde a condensação se concentra.

NOTAS

- Dado famílias dimensionais (120 x 120 mm), quatro composições.
- Não é um valor, mas um valor médio, varia-se o conteúdo dentro da espessura.
- A cor indica a exigência do local, não a exigência.

PROJETO PORTO REAL

RESIDENCIA UNIFAMILIAR (MANAUS - AM) | SOUS TATIANA-PS

PROJETO ARQUITETONICO

MAPA DE FAMÍLIAS DE VEDACÃO

BASE GEOMETRICA	ESCALA	EMISSÃO	PROVA
Lista Consolidada	1:100	ESTUDO PRELIMINAR	12
ISO-R12 (previsão)	FORMATO A1	ISO LIBERADO PARA CRIA	
UNIDADE MESTRE: mm	MILHA 400/500/700	SEM ART / INT	06-13