

○

downlight embudo

⊕

plafon de sobrepor (forno perfurado / aparente)

○

pendente (je-direito duplo)

—

linear do tampo (bancado, closet, mesa)

□

arandela de espelho

•

balizador de escada

● 2700 K

● 3000 K

● 4000 K

forno absorvente perfurado (refl. 0.70)

sem forno (painel PPR aparente)

LUMINOTECNICA POR AMBIENTE — METODO DOS LUMENS


AMB	USO	h2	altura	aberto	LUMINARIA	cm	m
T-GAR	apoi	30.5	75	108	4 x Plafon LED de sobrepor 24 W	4000 K	96
T-AL	circulacao	6.5	100	151	2 x Downlight LED embudo 18 W	3000 K	36
T-ALC	varia	3.2	150	151	1 x Downlight LED embudo 18 W	2700 K	18
T-CM	circulacao	3.2	100	151	1 x Downlight LED embudo 18 W	3000 K	18
T-DEV	varia	12.7	150	200	5 x Downlight LED embudo 18 W	2700 K	90
T-CM	aberto	9.9	500	511	4 x Downlight LED embudo 18 W	4000 K	144
T-SOC	soci	25.2	200	242	8 x Downlight LED embudo 24 W	3000 K	144
T-COR	escada	12.2	150	188	2 x Pendente LED de je-direito dup	3000 K	90
T-COE	cocina	17.8	300	303	7 x Downlight LED embudo 18 W	4000 K	108
T-GOU	soci	30.2	200	208	6 x Plafon LED de sobrepor 24 W	3000 K	144
T-LAV	servico	9.0	200	245	4 x Downlight LED embudo 18 W	4000 K	72
T-DEP	servico	3.0	200	272	2 x Downlight LED embudo 18 W	4000 K	36
S-SO2	varia	21.6	150	182	5 x Downlight LED embudo 18 W	2700 K	90
S-SO3	varia	21.6	150	182	5 x Downlight LED embudo 18 W	2700 K	90
S-AL	circulacao	11.5	100	120	2 x Downlight LED embudo 24 W	3000 K	40
S-LOU	soci	7.2	200	300	4 x Downlight LED embudo 24 W	3000 K	96
S-MAS	varia	21.6	150	182	6 x Downlight LED embudo 18 W	2700 K	90
S-SO2BANHO	banho	4.3	200	233	2 x Downlight LED embudo 18 W	3000 K	36
S-SO3BANHO	banho	4.3	200	233	2 x Downlight LED embudo 18 W	3000 K	36
T-CO2ESPENSA	servico	9.9	200	398	2 x Downlight LED embudo 24 W	4000 K	48
T-RE2BANHO	banho	4.3	200	233	2 x Downlight LED embudo 18 W	3000 K	36
T-CO2BANHO	banho	2.1	200	227	1 x Downlight LED embudo 18 W	3000 K	18
S-MASBANHO	banho	10.8	200	251	4 x Downlight LED embudo 18 W	3000 K	72
S-MAS2CLOSET	closet	9.0	200	245	4 x Downlight LED embudo 18 W	3000 K	72
S-MAS3OFFICE	ofico	5.4	300	512	4 x Downlight LED embudo 24 W	4000 K	96

LUZ DE TAREFA

COD	ONDE	TIPO	QTD	cm
L3-BC-01	bancada BC-01 (T-CO2)	linear	2.1 m	4000 K
L3-BC-02	bancada BC-02 (T-CO2)	linear	1.8 m	4000 K
L3-BC-03	bancada BC-03 (T-GOU)	linear	1.5 m	4000 K
L3-BC-04	bancada BC-04 (T-GOU)	linear	3.0 m	4000 K
L3-BC-05	bancada BC-05 (T-GOU)	linear	2.4 m	4000 K
L3-LC-02	espelho do banheiro LC-02 (T-COR)	arandela	1	4000 K
L3-LC-05	espelho do banheiro LC-05 (T-REV)	arandela	1	4000 K
L3-LC-06	espelho do banheiro LC-06 (S-SO2)	arandela	1	4000 K
L3-LC-08	espelho do banheiro LC-08 (S-SO3)	arandela	1	4000 K
L3-LC-11	espelho do banheiro LC-11 (S-MAS)	arandela	2	4000 K
L3-S-MAS-CLOSET	closet do S-MAS	linear	3.0 m	3000 K
L3-S-MAS-OFFICE	mesa do office do S-MAS	linear	1.2 m	4000 K
L3-ENCADA	escada (balizadora)	balizador	6	3000 K



1 FORRO REFLETIDO — TERREO
ESCALA 1:75

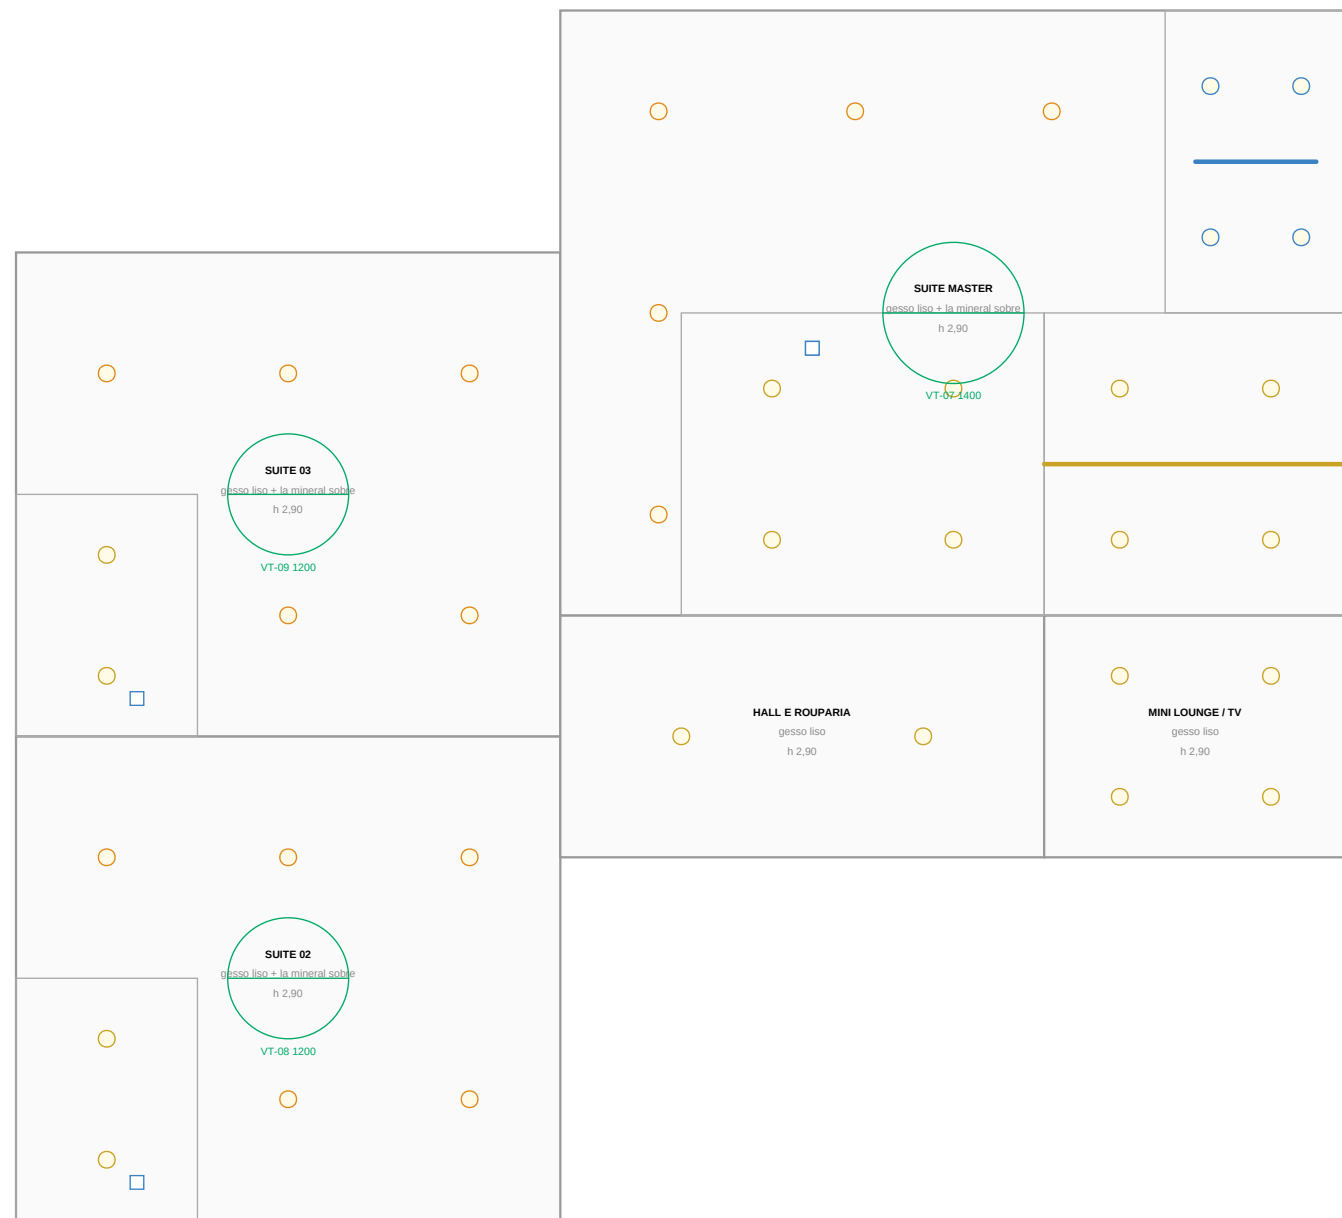

2 FORRO REFLETIDO — SUPERIOR
ESCALA 1:75

NOTAS

- Planta refletida: vista do forno projetada no plano horizontal, terreno e superior.
- Luminarias pelo METODO DOS LUMENS por ambiente (NBR ISO/IEC 8955-1 / NBR 5413), malha de uniformidade SHL 1.2.
- 18 pontos gerais, 12 pontos de tarefa, 3074 W (3.3 kWh).
- Cor: 2.700 K interno - 3.000 K social e circulacao - 4.000 K cozinha, banheiro e trabalho.
- 11 unidades de teto (painel), diâmetro 400 mm.

PROJETO PORTO REAL

RESIDENCIA UNIFAMILIAR (MANGUEIRAS - AM) | SUELO TATAMI-PS

PROJETO ARQUITETONICO

PLANTA DE FORRO E ILUMINACAO

BASE GEOMETRICA União Consolidada por R2D (previsível) UNIDADE MESTRE: 400	ESCALA 1:75 FORMATO A1 MILIMETROS (50/50/50)	EMISSAO ESTUDO PRELIMINAR R16 TUDO LIBERADO PARA OBRA SEM ART / RNT	PRONCHIA 16 06-48 REV 006
---	--	---	--