


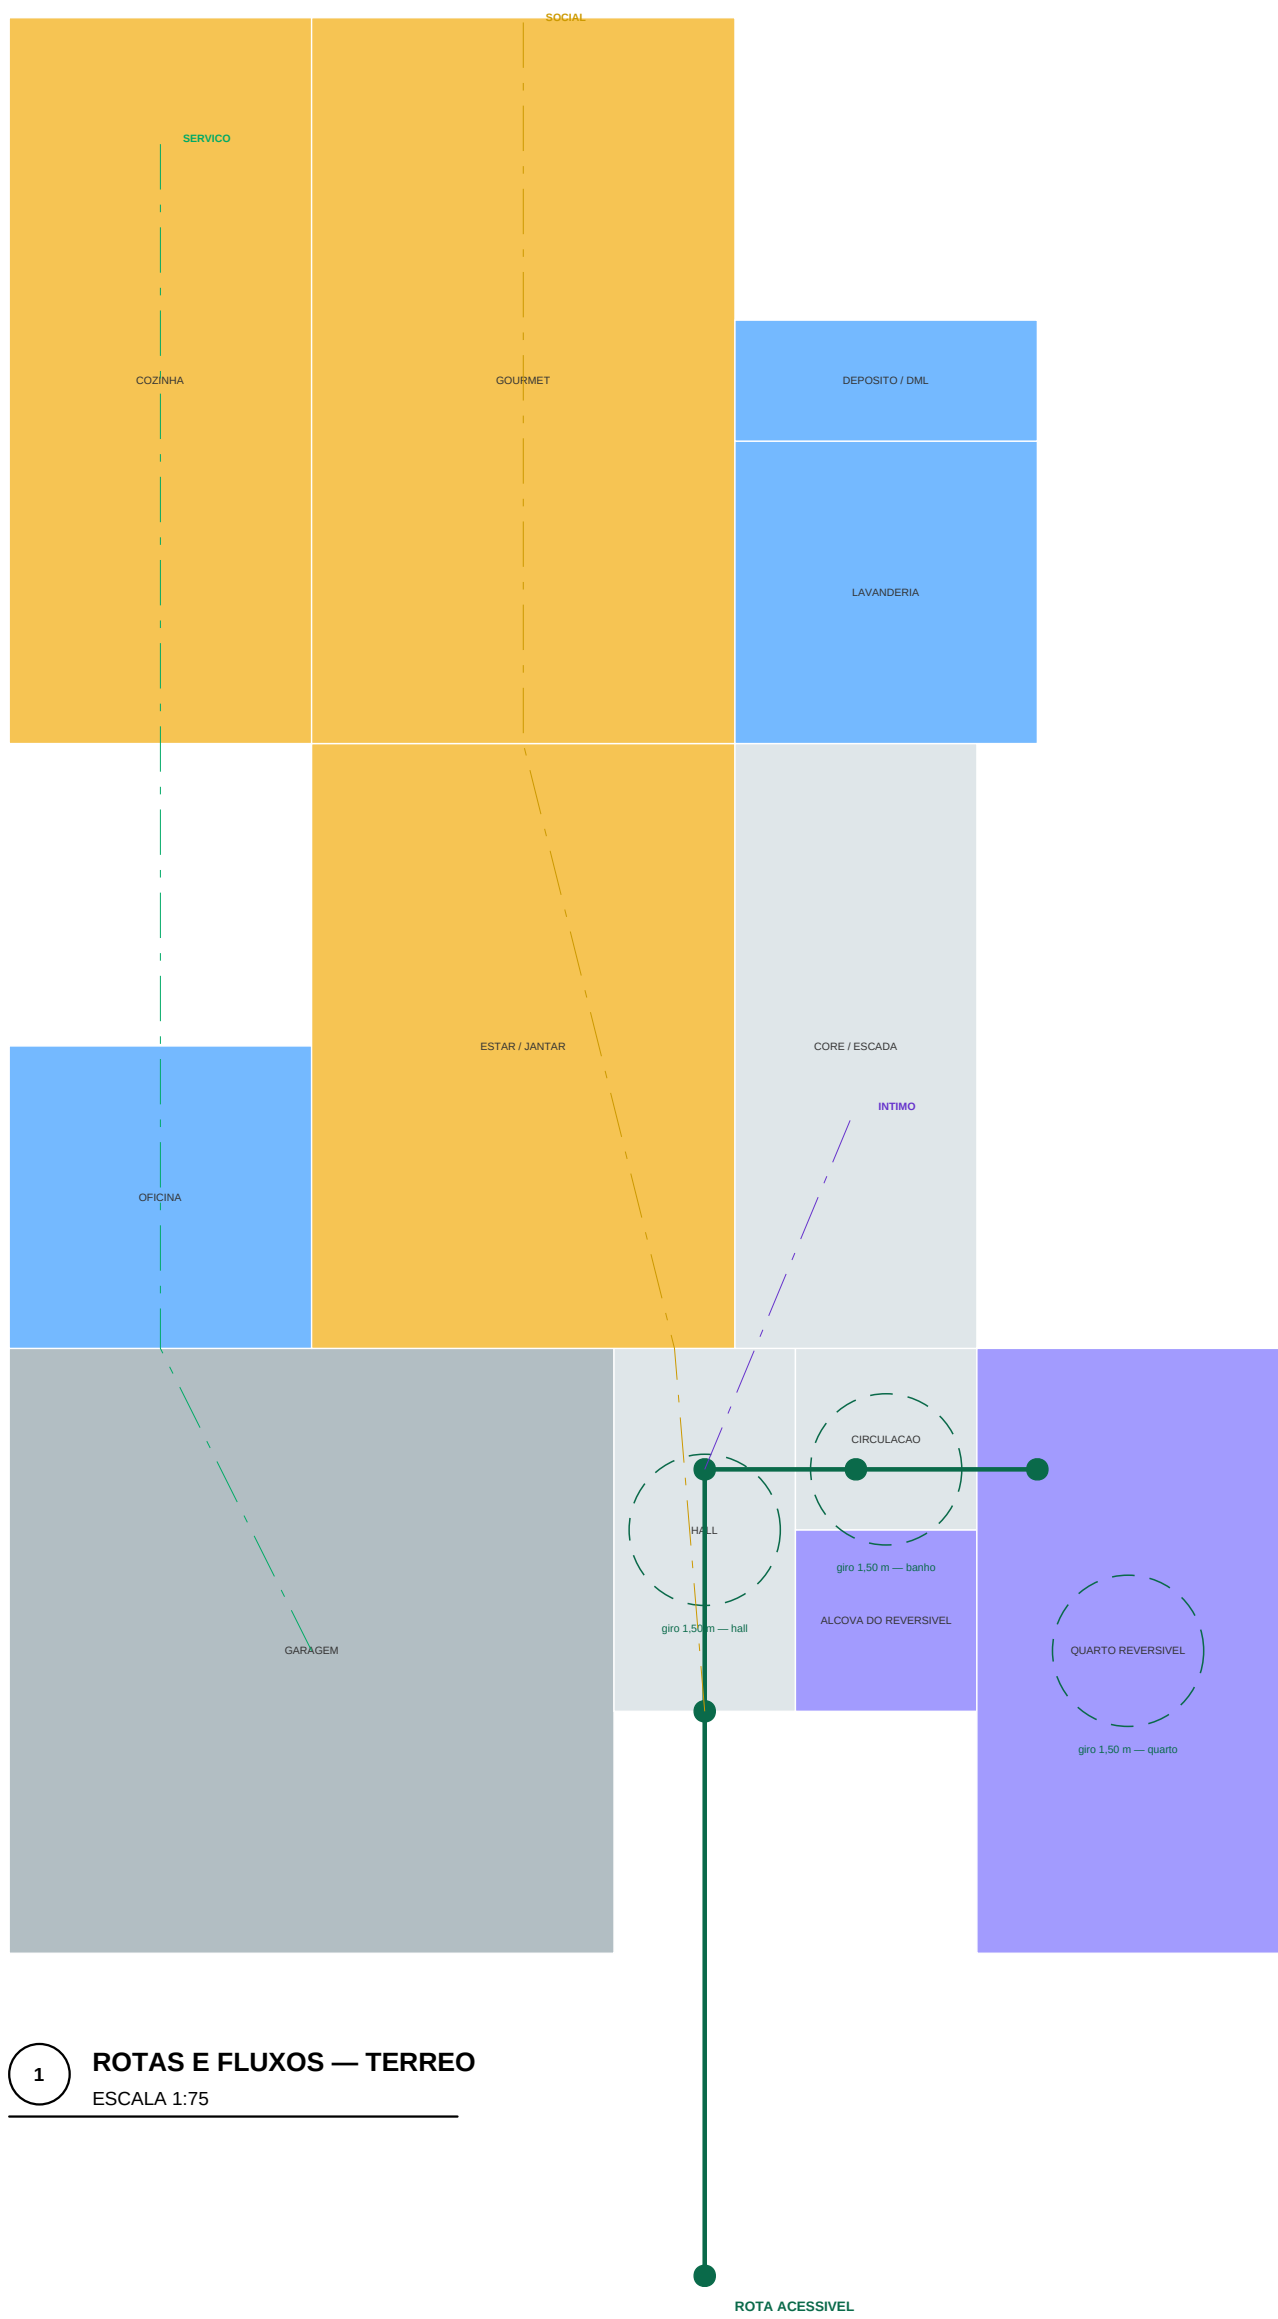

1 ROTAS E FLUXOS — TERREO  
ESCALA 1:75

#### VERIFICACAO NBR 9050

| ITEM                       | EXISTENTE           | PROJETO                     |          |
|----------------------------|---------------------|-----------------------------|----------|
| Visão livre de porta       | 800 mm              | 940 mm (prof. de 900)       | OK       |
| Circuito de giro 360 graus | 1.500 mm            | hall, banheiro e quarto     | OK       |
| Deslocar sem rampas        | até 5 mm            | soluções niveladas          | OK       |
| Largura de circulação      | 900 mm              | 1.800 mm no hall            | OK       |
| Barras de apoio            | relívios prévios    | instaladas na PTE 1 e PTE 2 | OK       |
| Barras de acesso           | altura livre 750 mm | sem barreiras sob a calha   | OK       |
| Corrimão e interruptor     | 600 a 1.000 mm      | a definir no detalhe        | pendente |



#### FLUXOS — SEPARACAO DE CIRCUITOS

| CIRCUITO        | PERCURSO                                                                     | CRUZAR O SOCIAL? |
|-----------------|------------------------------------------------------------------------------|------------------|
| Serviço         | garagem → estufa → lavanderia → cozinha → despensa                           | NÃO              |
| Social          | entrada → hall → estar → gourmet → alameda → piscina                         | —                |
| Área de serviço | hall → circulação → banheiro social (quarto reversível) (se não for projeto) | NÃO              |
| Área superior   | hall → core → hall superior → suíte                                          | NÃO              |
| Área de carga   | cozinha → despensa → reserv. hall                                            | NÃO              |

- NOTAS
- \* Rota acessível do passeio ao quarto reversível e ao banheiro social.
  - \* Circuito de giro de 1.500 mm verificado nos pontos de manobra.
  - \* Porta de correr de 900 mm no banheiro social e área de varanda.
  - \* Reforço para barras de apoio instaladas antes do fechamento das placas.

#### PROJETO PORTO REAL

RESIDENCIA UNIFAMILIAR (MANSÃO - AM) | SOBR TATIANA-PS

PROJETO ARQUITETONICO

#### ACESSIBILIDADE E FLUXOS

|                                                                                       |                                                         |                                                                                    |                                    |
|---------------------------------------------------------------------------------------|---------------------------------------------------------|------------------------------------------------------------------------------------|------------------------------------|
| BASE GEOMETRICA<br><b>Unia Consolidada</b><br>ps-RDZ (previsto)<br>UNIDADE MESTRE: AM | ESCALA<br><b>1:75</b><br>FORMATO A1<br>MILHA 955/000000 | EMISSAO<br><b>ESTUDO PRELIMINAR R06</b><br>NÃO LIBERADO PARA OBRA<br>SEM ART / RNT | PROVA<br><b>17</b><br>DE 48 REVISE |
|---------------------------------------------------------------------------------------|---------------------------------------------------------|------------------------------------------------------------------------------------|------------------------------------|