


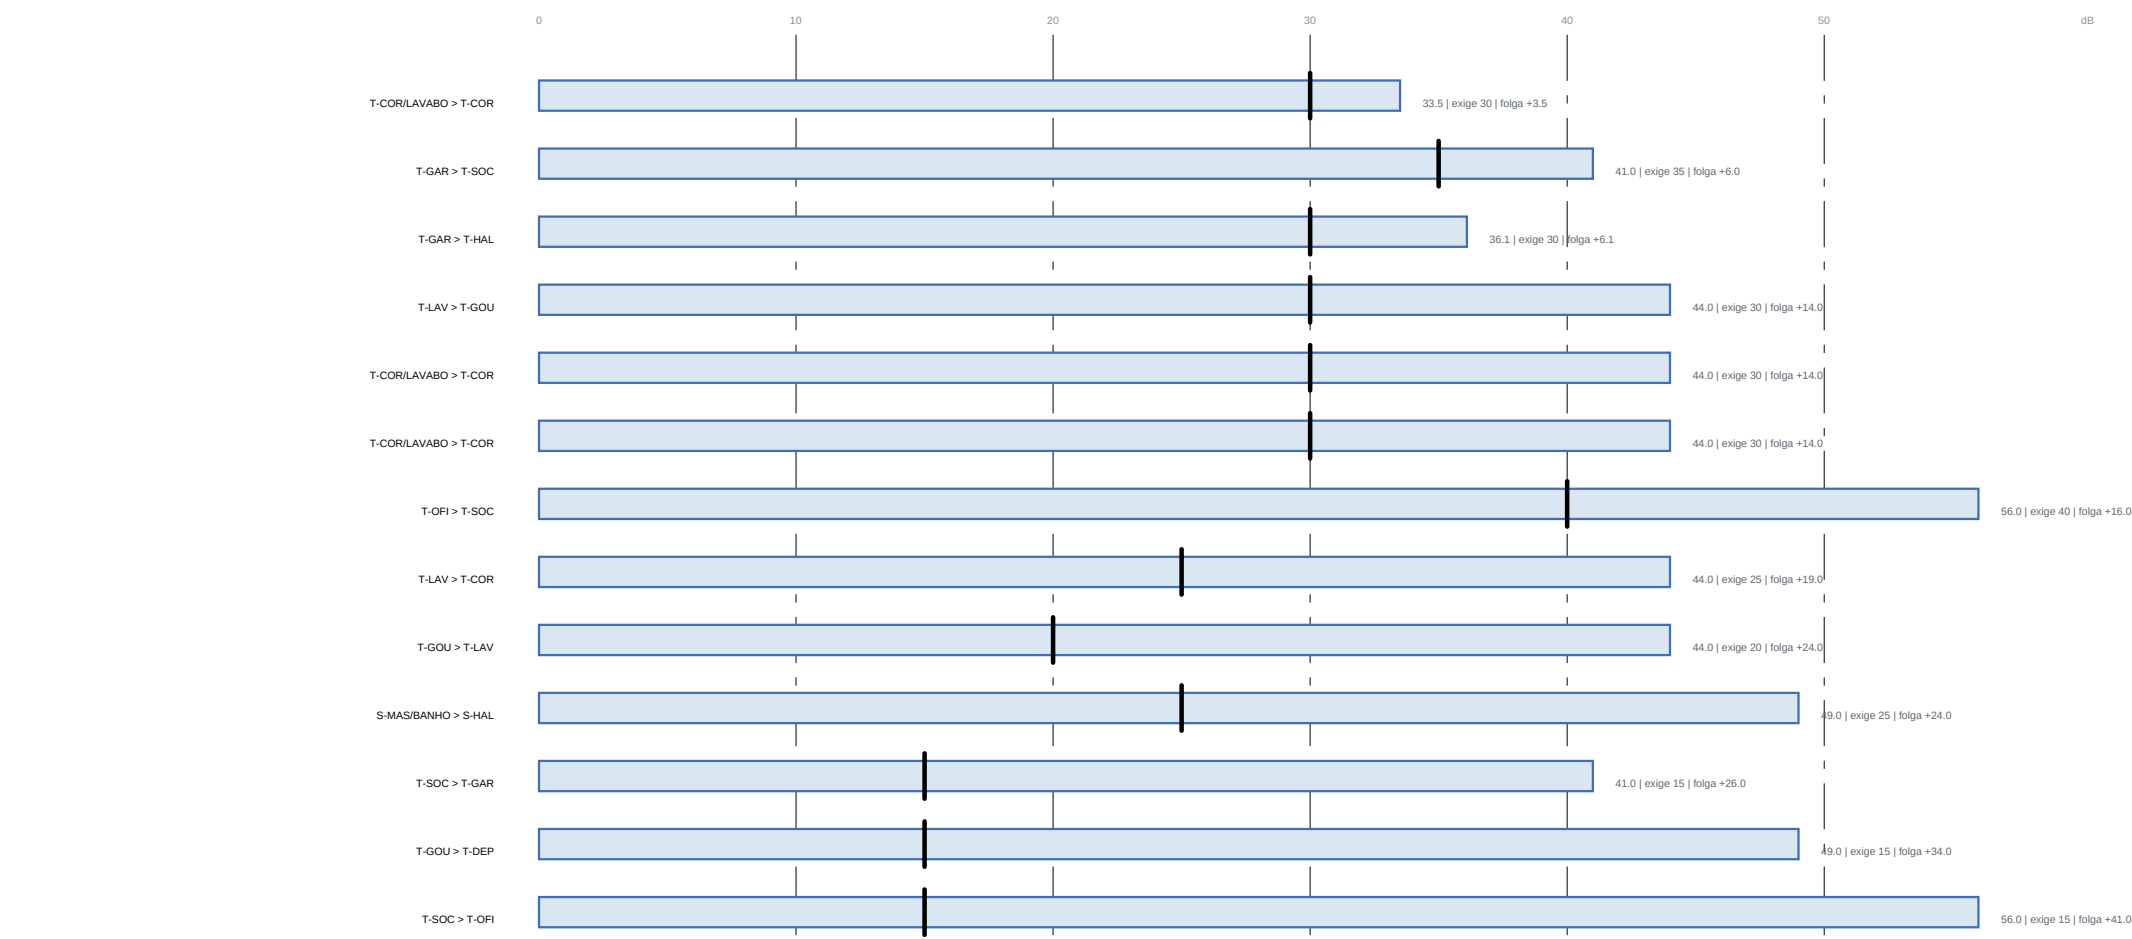

Barra = isolamento obtido; traço vertical = exigência (valor da fonte menos limite do receptor, NBR 15102)

O QUE MUDOU EM R\$2

ONDE	ANTES	DEPOIS	POR QUE
Banho compartilhado + hall de entrada	porta de correr (Rw 25) — conjunto de 25,2 dB	parede CEGSA, 44 dB	o acesso de volta passou para a circulação
Banho compartilhado + quarto eventual	porta com (Rw 25) — conjunto de 25,5 dB, exigia 25	parede CEGSA, 44 dB	era a por passagem da casa, e não era a saída
Hall + garagem	porta com — 26,9 dB, exigia 30	PDS isolou vedado — 36,9 dB	porta entre garagem e casa tem dupla função para ser móbica
Banho compartilhado + circulação	não havia porta	PDS isolou vedado — 35,7 dB, exigia 25	único acesso do banho, e abria para fora
Bloco do chuveiro	encostado na parede do hall	canto arredondado, toldo e janela alta	consequência da porta nova, a regra dos 900 cm de box obrigou a primeira tentativa

TABELAS ADOTADAS

ITEM	VALOR	FONTE
Fonte: caixa sanitária	75 dB(A)	prática corrente de acústica
Fonte: bloco do chuveiro	70 dB(A)	prática corrente de acústica
Fonte: cozinha e gourmet	70 dB(A)	prática corrente de acústica
Fonte: sala e jantar	70 dB(A)	prática corrente de acústica
Fonte: garagem	70 dB(A)	prática corrente de acústica
Fonte: máquina de lavar e secar	70 dB(A)	prática corrente de acústica
Fonte: oficina	60 dB(A)	prática corrente de acústica
Limite: banho	45 dB(A)	NBR 15102:2017 (circulação e entrada adotadas)
Limite: circulação	45 dB(A)	NBR 15102:2017 (circulação e entrada adotadas)
Limite: cozinha	45 dB(A)	NBR 15102:2017 (circulação e entrada adotadas)
Limite: depósito	55 dB(A)	NBR 15102:2017 (circulação e entrada adotadas)
Limite: dormitório	35 dB(A)	NBR 15102:2017 (circulação e entrada adotadas)
Limite: entrada	45 dB(A)	NBR 15102:2017 (circulação e entrada adotadas)
Limite: estar	45 dB(A)	NBR 15102:2017 (circulação e entrada adotadas)
Limite: garagem	55 dB(A)	NBR 15102:2017 (circulação e entrada adotadas)
Limite: office	45 dB(A)	NBR 15102:2017 (circulação e entrada adotadas)
Limite: oficina	55 dB(A)	NBR 15102:2017 (circulação e entrada adotadas)
Limite: serviço	50 dB(A)	NBR 15102:2017 (circulação e entrada adotadas)
Fonte: academia	Pin 25 dB	Nota de mercado declarada
Fonte: cinema	Pin 25 dB	Nota de mercado declarada
Fonte: sala	Pin 20 dB	Nota de mercado declarada
Fonte: sala de	Pin 25 dB	Nota de mercado declarada
Fonte: sala de visita	Pin 30 dB	Nota de mercado declarada

- NOTAS
- Esta planilha existe porque o proprietário perguntou o que 100 verificações não sabem responder: quem entra na casa ouve o chuveiro do banho da entrada?
 - Ouça. A parede era box (Pin 1, Pin 44) e a porta era de correr (Rw 25), o conjunto entregava 20 dB. Em acústica o eixo físico DOMINA — não se faz média aritmética do isolamento, se soma energia que passa.
 - Isolamento se se exige ENTRE portas. Dentro da file social o ruído não é definido, é o programa.
 - O adotado igual ao R2 compõe (significância declarada), não o pre-verificação de projeto, não enviado do corpo da NBR 15107-3.

PROJETO PORTO REAL

RESIDENCIA UNIFAMILIAR (MANSÃO - AM) | SOBR TATIANA-PS

PROJETO ARQUITETONICO

DESEMPENHO ACUSTICO ENTRE AMBIENTES

BASE GEOMETRICA	ESCALA	EMISSAO	PROVA
Lista Consolidada	s/ escala	ESTUDIO PRELIMINAR R\$6	
Pin R\$2 (previsão)	FORMATO A1	IMAO LIBERADO PARA OBRA	39
UNIDADE MESTRE: mm	MILIMETROS (50/100/200)	SEM ART / RNT	06-48 REVISE