


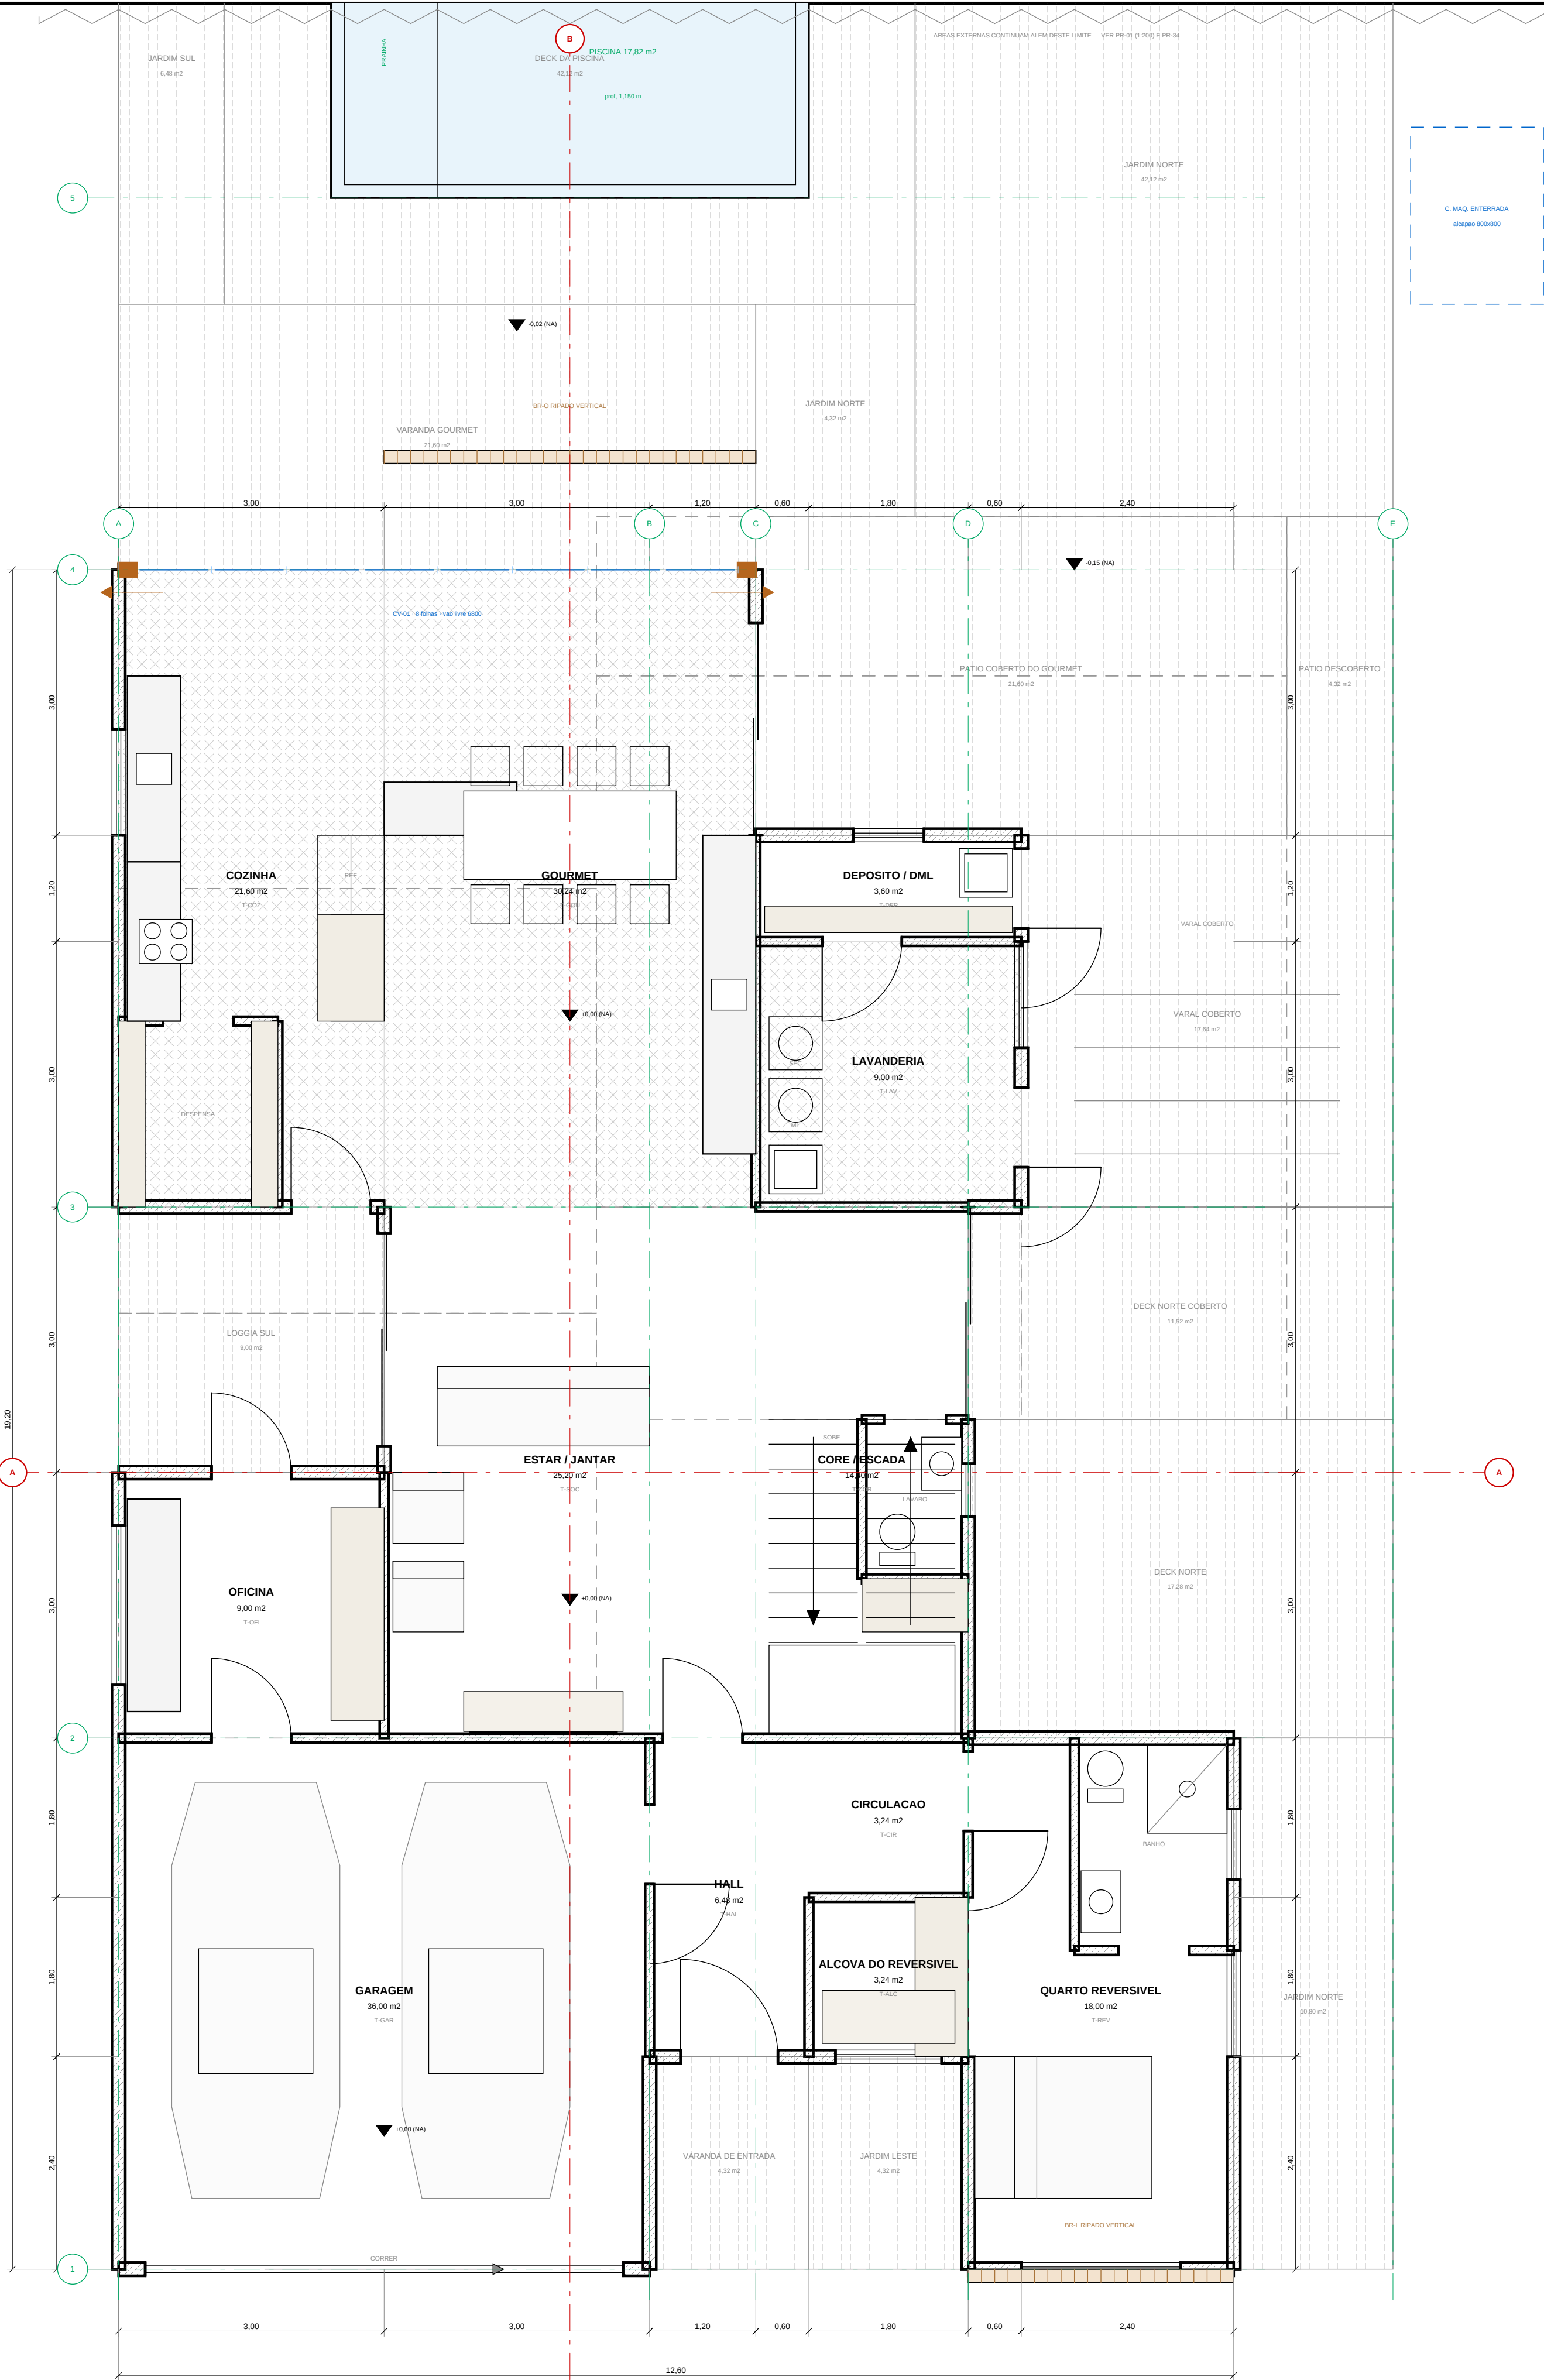

1 PAVIMENTO TERREO
ESCALA 1:50





QUADRO DE ÁREAS — PAVIMENTO TERREO			
COD	AMBIENTE	MÓDULO (mm)	ÁREA (m²)
T-GAR	CARAGEM	600x600	36,00
T-HAL	HALL	1800x3000	5,40
T-ALC	ALCOVA DO REVERSÍVEL	1800x900	1,62
T-CIR	CIRCULAÇÃO	1800x1800	3,24
T-REV	QUARTO REVERSÍVEL	3000x3000	9,00
T-OFI	OFICINA	3000x3000	9,00
T-SOC	ESTAR / JANTAR	4500x6000	27,00
T-COR	CORRER / ESCADA	2400x6000	14,40
T-COZ	COZINHA	3000x2700	8,10
T-GOU	GOURMET	4500x2700	12,15
T-LAV	LAVANDERIA	3000x3000	9,00
T-DEP	DEPOSITO / D.M.	3000x1200	3,60
TOTAL FECHADO			186,00
T-VAR	VARANDA DE ENTRADA (aberta)	1800x2400	4,32
T-J.E	JARDIM LESTE (aberto)	1800x3000	5,40
T-J.N	JARDIM NORTE (aberto)	1800x3000	5,40
T-LOG	LOGGIA SUL (aberto)	3000x3000	9,00
T-D.M	DECK NORTE (aberto)	4800x3000	14,40
T-D.M	DECK NORTE COBERTO (aberto)	4800x2400	11,52
T-VAR	VARAL COBERTO (aberto)	4500x4500	20,25
T-PAT	PATIO COBERTO DO GOURMET (aberto)	6000x3000	18,00
T-PAT	PATIO DESCOBERTO (aberto)	1200x3000	3,60
T-VAR	VARANDA GOURMET (aberto)	7500x3000	22,50
T-DEP	DECK DA COZINHA (aberto)	7500x3000	22,50
T-J.S	JARDIM SUL (aberto)	1200x4500	5,40
T-J.N	JARDIM NORTE (aberto)	1800x2400	4,32
T-J.N	JARDIM NORTE (aberto)	5400x7800	42,12
T-PV	JARDIM DE FUNDO (aberto)	14400x4800	69,12

REF	VALOR (mm)	QTD	QTD	TIPO
CVE1	7000x2000	0	1	CORTINA DE VIDRO vertical, 0 folha de 900 mm
J1	1200x1200	1200	4	porta de banheiro, alumínio
J2	800x800	1800	1	porta de banheiro, vidro translúcido
J3	800x800	1800	2	porta de banheiro, alumínio
J4	1800x1200	1200	2	porta de banheiro, alumínio
J5	1200x1200	1200	2	porta de banheiro, alumínio
J6	1200x1200	0	1	porta principal, vidro opaco
J7	800x1200	0	2	porta interna (divisão sanitária)
J8	800x1200	0	6	porta de serviço, alumínio a unidade
J9	800x1200	0	1	porta interna de sala SOLADA com vidros (pau)
J10	5400x2400	0	1	porta de correr, alumínio opaco
J11	3600x2400	0	1	porta lateral de entrada adicional - var

LEGENDA E CONVENÇÕES (NBR 6492 / 8403)

- Elemento seccionado pelo plano de corte (h = 1,50 m)
- Área vista / folha de espelhos
- Mobiliário fixo, equipamento e sinetologia
- Propriedade do pavimento superior e da cobertura
- Eixo modular e linha de corte
- Linha de vista e linha auxiliar

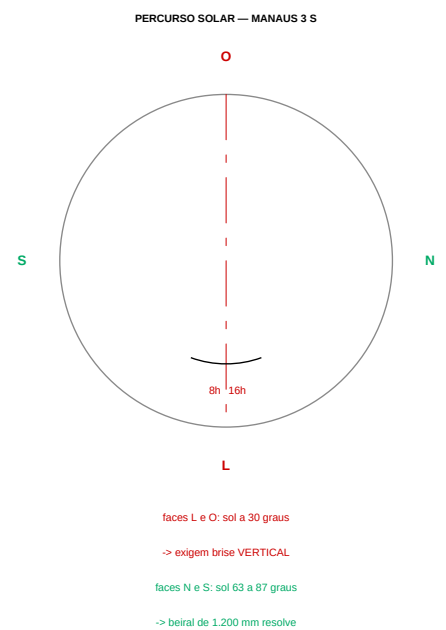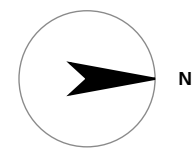

- NOTAS
- Dimensões em milímetros; cotas de nível em metros.
 - Malha modular 600 mm; cotas elevadas a 600.
 - Planta externa 120 mm / planta interna 120 mm (p).
 - Modulador fixo indica pontos de água e esgoto (NBR 6492).

PROJETO PORTO REAL

RESIDÊNCIA UNIFAMILIAR (MANUS - AM) | SOU TATIANA-PS

PROJETO ARQUITETÔNICO

PLANTA DE LAYOUT — PAVIMENTO TERREO

BASE GEOMÉTRICA Linha Consolidada pelo P22 (previsto) UNIDADE: METRO (m)	ESCALA 1:50 FORMATO A1 MALHA: 600/600 (mm)	EXIBIÇÃO ESTUDO PRELIMINAR R09 Linha Consolidada PARA ORÇAMENTO SEM ART / RNT	PROJETO 04 04-49 REV 003
---	---	--	--------------------------------