



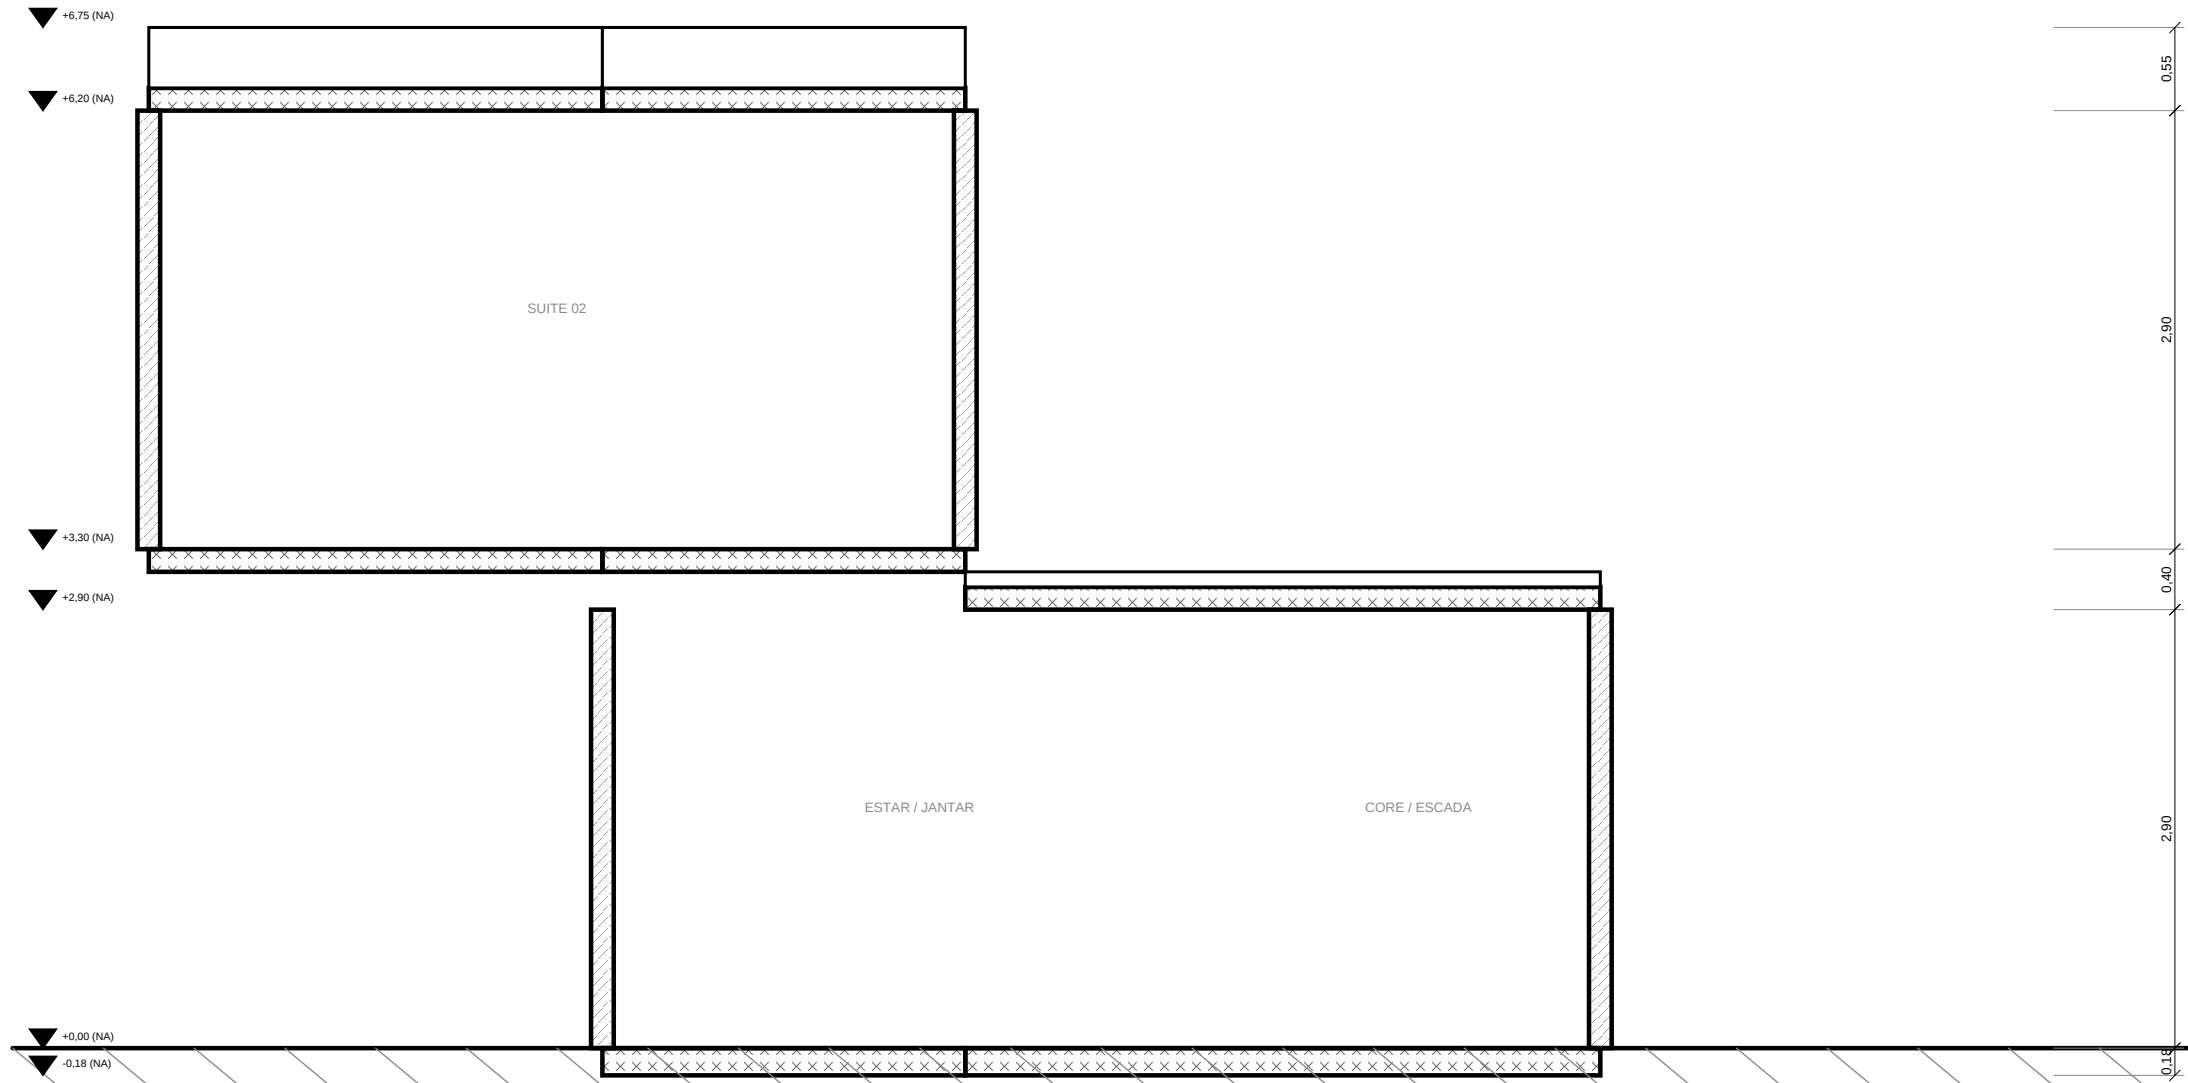

1 CORTE AA — TRANSVERSAL
ESCALA 1:50

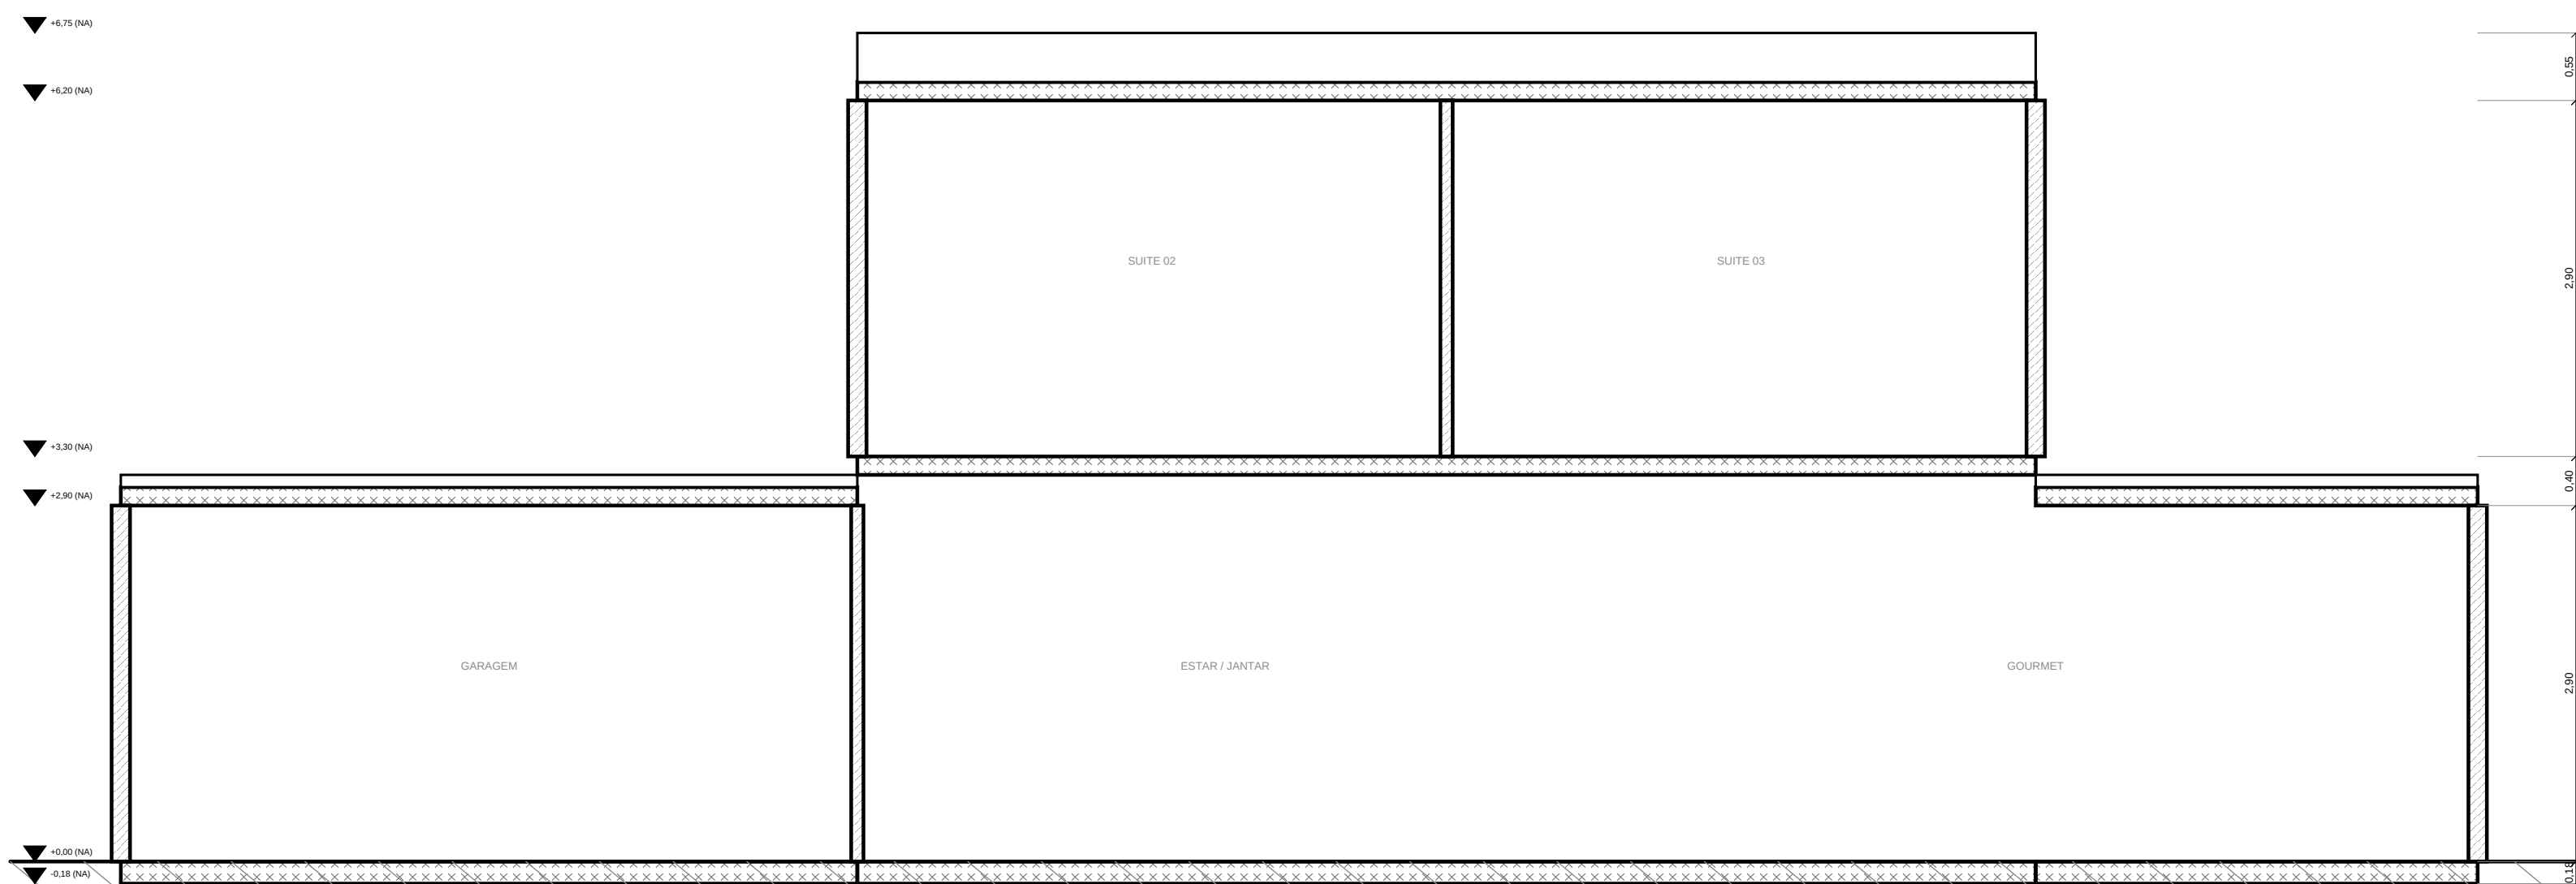

2 CORTE BB — LONGITUDINAL
ESCALA 1:50



NOTAS

- * Piso direito acabado 2500 mm x piso a piso 3200 mm.
- * Topo da platibanda +6.750 m (isto pavimento) e +3.300 m (isto pavimento) — H.
- * Fundações em radier 180 mm, taxa 30 MPa, aço CA-50 (S).
- * Vedação em Light Steel Frame, vãos grandes em perfil metálico estrutural.

PROJETO PORTO REAL			
RESIDENCIA UNIFAMILIAR (MARIAUS - AM) (SUITE TATIANA-PS)			
PROJETO ARQUITETONICO			
CORTES AA E BB			
BASE GEOMETRICA	ESCALA	EMISSAO	PROJECION
Unia Consolidada	1:50	ESTUDIO PRELIMINAR R09	06
Projeto (previsão)	FORMATO A1	NAO LIBERADO PARA OBRA	
UNIDADE MESTRE: AM	MALHA 600/600/300	SEM ART / INT	06-49 REV 002