

- downlight embudo
- ⊕


plafon de sobrepor (forno perfurado / aparente)
- pendente (je-direito duplo)
- linear do tafeia (bancado, closet, mesa)
- arandela de espelho
- balizador de escada
- 2700 K
- 3000 K
- 4000 K
- forno absorvente perfurado (afa 0.70)
- sem forno (painel PPR aparente)

LUMINOTECNICA POR AMBIENTE — METODO DOS LUMENS

AMB	USO	mx	mx/ta	mx/ta	LUMINARIA	lux	m
T-GAR	apoi	30.5	75	108	4 x Plafon LED de sobrepor 24 W	4000 K	96
T-AL	circulacao	6.5	100	151	2 x Downlight LED embudo 18 W	3000 K	36
T-ALC	recep	3.2	150	151	1 x Downlight LED embudo 18 W	2700 K	18
T-CM	circulacao	3.2	100	151	1 x Downlight LED embudo 18 W	3000 K	18
T-DEV	recep	12.7	150	200	5 x Downlight LED embudo 18 W	2700 K	90
T-CM	abaco	9.0	500	151	4 x Downlight LED embudo 18 W	4000 K	144
T-SOC	social	25.2	200	242	8 x Downlight LED embudo 24 W	3000 K	144
T-COR	escada	12.2	150	188	2 x Pendente LED de je-direito dup	3000 K	90
T-COE	cocina	17.8	300	350	7 x Downlight LED embudo 24 W	4000 K	168
T-GOU	social	30.2	200	208	6 x Plafon LED de sobrepor 24 W	3000 K	144
T-LAV	servico	9.0	200	245	4 x Downlight LED embudo 18 W	4000 K	72
T-DEP	servico	3.0	200	272	2 x Downlight LED embudo 18 W	4000 K	36
S-S01	recep	21.6	150	182	5 x Downlight LED embudo 18 W	2700 K	90
S-S03	recep	21.6	150	182	5 x Downlight LED embudo 18 W	2700 K	90
S-APL	circulacao	11.5	100	120	2 x Downlight LED embudo 24 W	3000 K	40
S-LOU	social	7.2	200	350	4 x Downlight LED embudo 24 W	3000 K	96
S-MAS	recep	21.6	150	182	6 x Downlight LED embudo 18 W	2700 K	90
S-S03BANHO	banho	4.3	200	233	2 x Downlight LED embudo 18 W	3000 K	36
S-S03BANHO	banho	4.3	200	233	2 x Downlight LED embudo 18 W	3000 K	36
T-CLOSET/DEPENDENCIA	servico	3.6	200	398	2 x Downlight LED embudo 24 W	4000 K	48
T-BEUSBANHO	banho	4.3	200	233	2 x Downlight LED embudo 18 W	3000 K	36
T-COM/LAVABO	banho	2.1	200	227	1 x Downlight LED embudo 18 W	3000 K	18
S-MASBANHO	banho	10.8	200	251	4 x Downlight LED embudo 18 W	3000 K	72
S-MAS/CLOSET	closet	9.0	200	245	4 x Downlight LED embudo 18 W	3000 K	72
S-MAS/OFFICE	office	5.4	300	512	4 x Downlight LED embudo 24 W	4000 K	96

LUZ DE TAREFA

COO	ONDE	TIPO	QTO	lux
L3-BC-01	bancada BC-01 (T-CO2)	linear	2.1 m	4000 K
L3-BC-02	bancada BC-02 (T-CO2)	linear	1.8 m	4000 K
L3-BC-03	bancada BC-03 (T-CO3)	linear	1.5 m	4000 K
L3-BC-04	bancada BC-04 (T-CO3)	linear	3.0 m	4000 K
L3-BC-05	bancada BC-05 (T-CO3)	linear	2.4 m	4000 K
L3-LC-02	espelho do banheiro LC-02 (T-CO3)	arandela	1	4000 K
L3-LC-05	espelho do banheiro LC-05 (T-REV)	arandela	1	4000 K
L3-LC-06	espelho do banheiro LC-06 (S-S03)	arandela	1	4000 K
L3-LC-08	espelho do banheiro LC-08 (S-S03)	arandela	1	4000 K
L3-LC-11	espelho do banheiro LC-11 (S-MAS)	arandela	2	4000 K
L3-BANHO-CLOSET	closet do S-MAS	linear	3.0 m	3000 K
L3-S-MAS-OFFICE	mesa do office do S-MAS	linear	1.2 m	4000 K
L3-ENCADA	escada (banheiro)	balizadora	6	3000 K

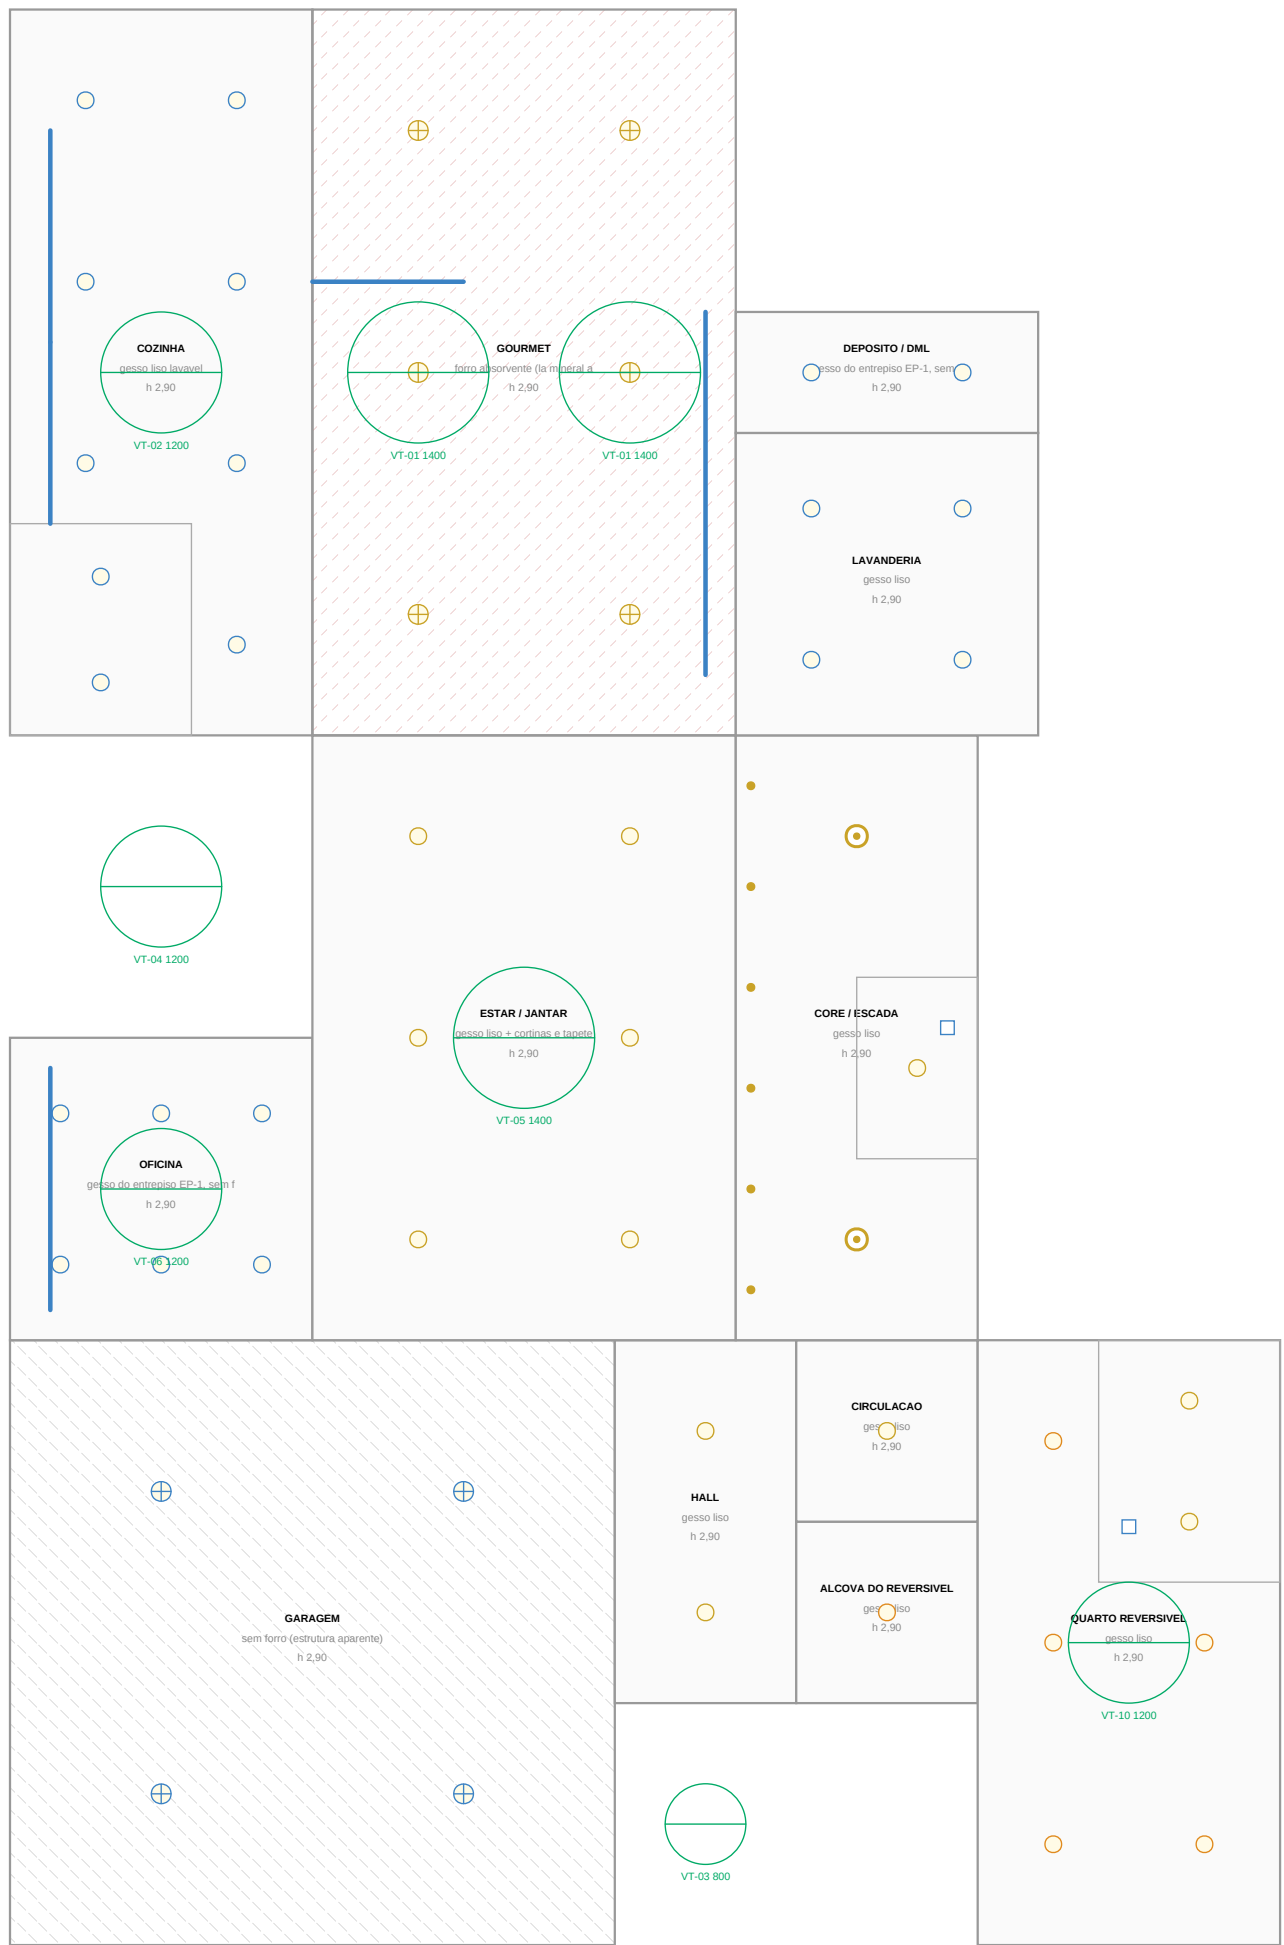

1 FORRO REFLETIDO — TERREO
ESCALA 1:75



2 FORRO REFLETIDO — SUPERIOR
ESCALA 1:75

NOTAS

- Planta refletida: vista do forno projetada no plano horizontal, terreno e superior
- Luminarias pelo METODO DOS LUMENS por ambiente (NBR 9050:2005 / NBR 5413), malha de uniformidade SHL 1.2
- 18 pontos gerais, 12 pontos de tarefa, 3714 W (3.3 kW)
- Cor: 2.700 K interno - 3.000 K social e circulacao - 4.000 K cocina, banho e trabalho
- 11 unidades de teto (painel), diâmetro 400 mm

PROJETO PORTO REAL

RESIDENCIA UNIFAMILIAR (MANGUEIRA - AM) (SUA TUBERIA-PS)

PROJETO ARQUITETONICO

PLANTA DE FORRO E ILUMINACAO

BASE GEOMETRICA União Consolidada por R2D (previsível) UNIDADE: METRO: mm	ESCALA 1:75 FORMATO A1 MILHA: 600/500/500	EMISSAO ESTUDIO PRELIMINAR R09 LAW LIBERADO PARA OBRA SEM ART / RNT	PROJECION 16 06-49 REV 003
--	--	--	----------------------------------