


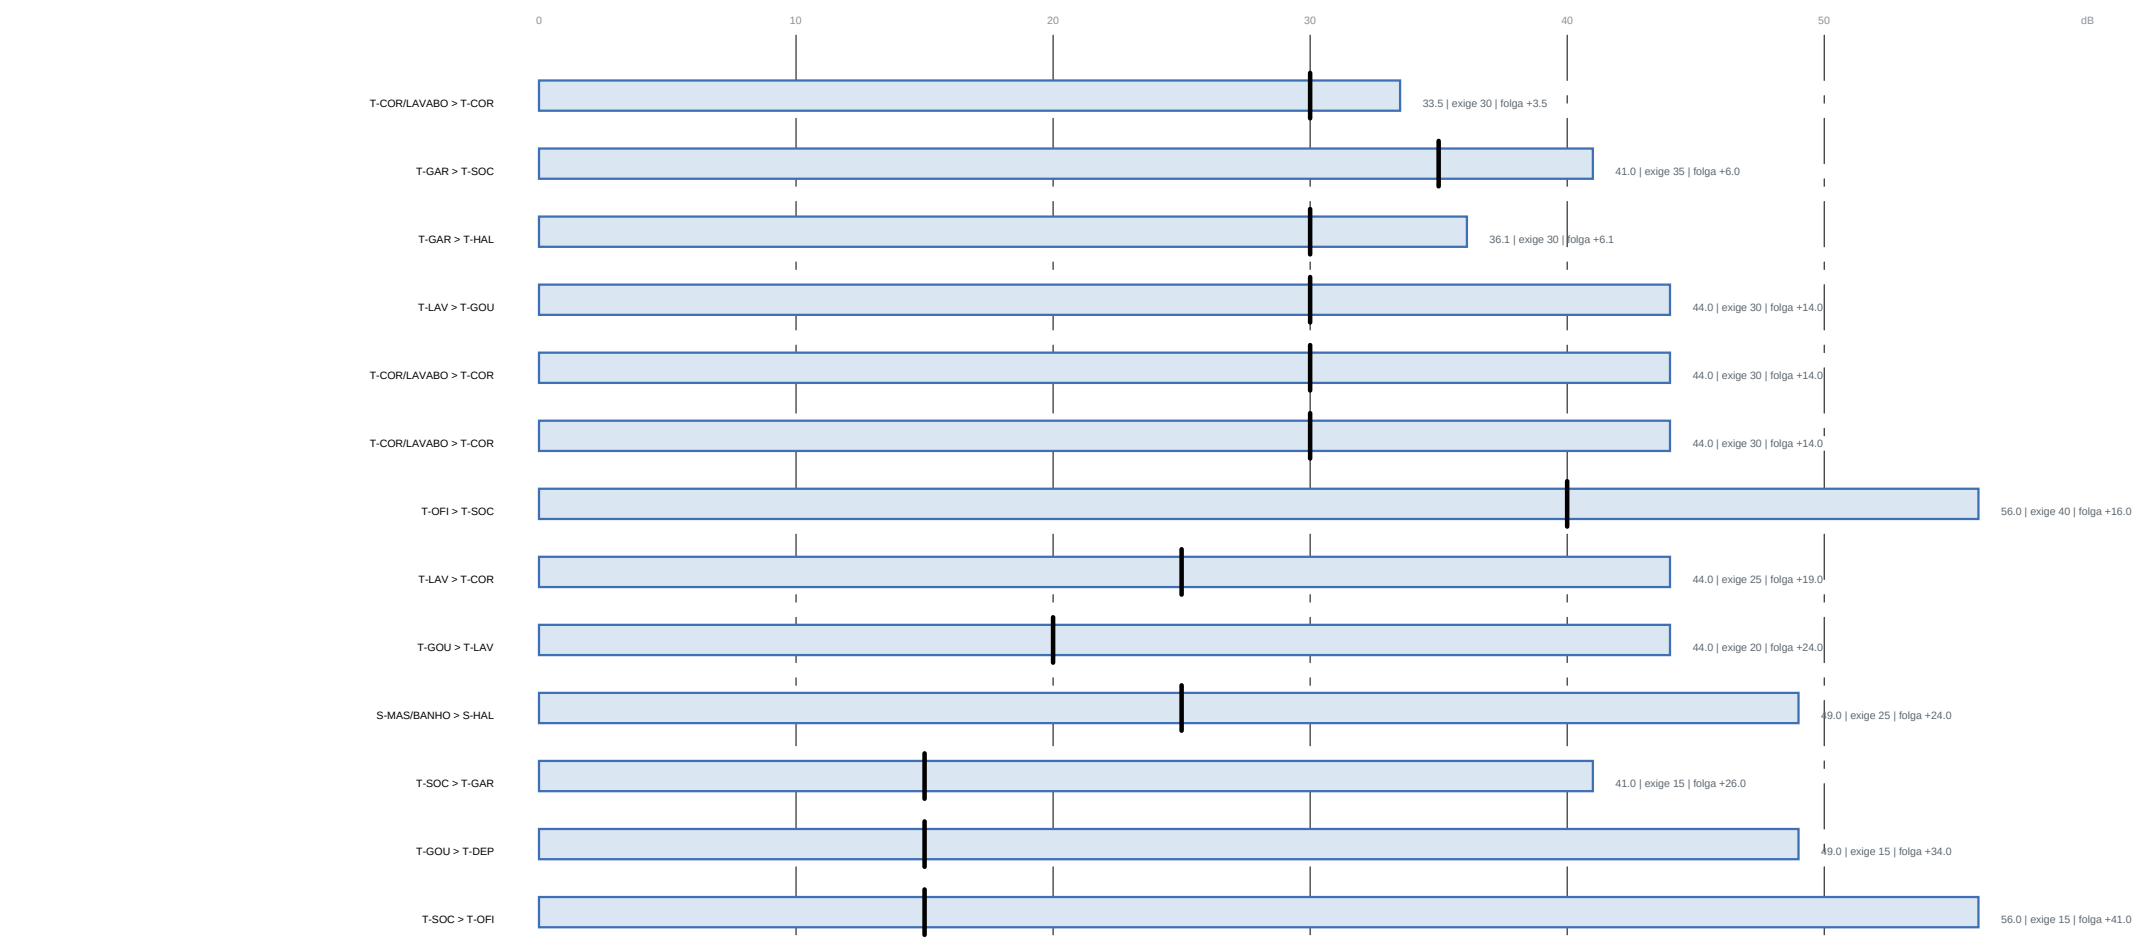

Barra = isolamento obtido; traço vertical = energia (valor da fonte menos nível do receptor, NBR 15102)

O QUE MUDOU EM R52

ONDE	ANTES	DEPOIS	POR QUE
Banho compartilhado > hall de entrada	porta de correr (Pw 25) — conjunto de 20,2 dB	parede CEGSA, 44 dB	o acesso de volta passou para a circulação
Banho compartilhado > quarto eventual	porta com (Pw 25) — conjunto de 25,3 dB, energia 25	parede CEGSA, 44 dB	era a por passagem da casa, e não era a saída
Hall > garagem	porta com — 36,9 dB, energia 35	PDS isolada vedada — 36,9 dB	porta entre garagem e casa tem dupla função para ser móbica
Banho compartilhado > circulação	não havia porta	PDS isolada vedada — 35,7 dB, energia 25	único acesso do banho, e abria para fora
Bloco do chuveiro	encostado na parede do hall	canto arredondado, toldo e janela alta	consequência da porta nova, a regra dos 900 cm de box obrigou a primeira tentativa

TABELAS ADOTADAS

ITEM	VALOR	FONTE
Fonte: caixa sanitária	75 dB(A)	prática corrente de acústica
Fonte: bloco do chuveiro	75 dB(A)	prática corrente de acústica
Fonte: cozinha e gourmet	75 dB(A)	prática corrente de acústica
Fonte: sala e jantar	75 dB(A)	prática corrente de acústica
Fonte: garagem	75 dB(A)	prática corrente de acústica
Fonte: máquina de lavar e secar	75 dB(A)	prática corrente de acústica
Fonte: oficina	85 dB(A)	prática corrente de acústica
Límite: banho	45 dB(A)	NBR 15102:2017 (circulação e entrada adjacente)
Límite: circulação	45 dB(A)	NBR 15102:2017 (circulação e entrada adjacente)
Límite: cozinha	45 dB(A)	NBR 15102:2017 (circulação e entrada adjacente)
Límite: depósito	55 dB(A)	NBR 15102:2017 (circulação e entrada adjacente)
Límite: dormitório	35 dB(A)	NBR 15102:2017 (circulação e entrada adjacente)
Límite: entrada	45 dB(A)	NBR 15102:2017 (circulação e entrada adjacente)
Límite: estar	45 dB(A)	NBR 15102:2017 (circulação e entrada adjacente)
Límite: garagem	55 dB(A)	NBR 15102:2017 (circulação e entrada adjacente)
Límite: office	45 dB(A)	NBR 15102:2017 (circulação e entrada adjacente)
Límite: oficina	55 dB(A)	NBR 15102:2017 (circulação e entrada adjacente)
Límite: serviço	55 dB(A)	NBR 15102:2017 (circulação e entrada adjacente)
Fonte: acústica	Pw 25 dB	Nota de mercado declarada
Fonte: sonar	Pw 25 dB	Nota de mercado declarada
Fonte: sala	Pw 25 dB	Nota de mercado declarada
Fonte: sala de	Pw 25 dB	Nota de mercado declarada
Fonte: sala de visita	Pw 30 dB	Nota de mercado declarada

NOTAS

1 Esta planilha está pensada para o proprietário perguntar e que 100 verificações não sabem responder: quem entra na casa ouve o chuveiro do banho da entrada?

2 Ouviu. A parede era boa (Pw 45), mas não a porta era do correio (Pw 25), o conjunto entregava 20 dB. Em acústica o eixo físico DOMINA — não se faz média aritmética do isolamento, se soma energia que passa.

3 Isolamento se se encaixa ENTRE os dois. Dentro da file social o ruído não é definido, é o programa.

4 O adotado igual ao 15 (composto por 15 verificações declaradas), não é por verificação de projeto, mas em função do corpo da NBR 15107-3.

PROJETO PORTO REAL

RESIDENCIA UNIFAMILIAR (MANSÃO - AM) | SOBR TATIANA-PS

PROJETO ARQUITETÔNICO

DESEMPENHO ACUSTICO ENTRE AMBIENTES

BASE GEOMÉTRICA	ESCALA	EMISSÃO	PROVA
Lista Consolidada	s/ escala	ESTUDO PRELIMINAR R50	
ISO R52 (previsão)	FORMATO A1	ISO LIBERADO PARA CRIAÇÃO	39
UNIDADE MÉTRICA: mm	MILHA 605/500/500	SEM ART / RNT	06-48 REV 002