




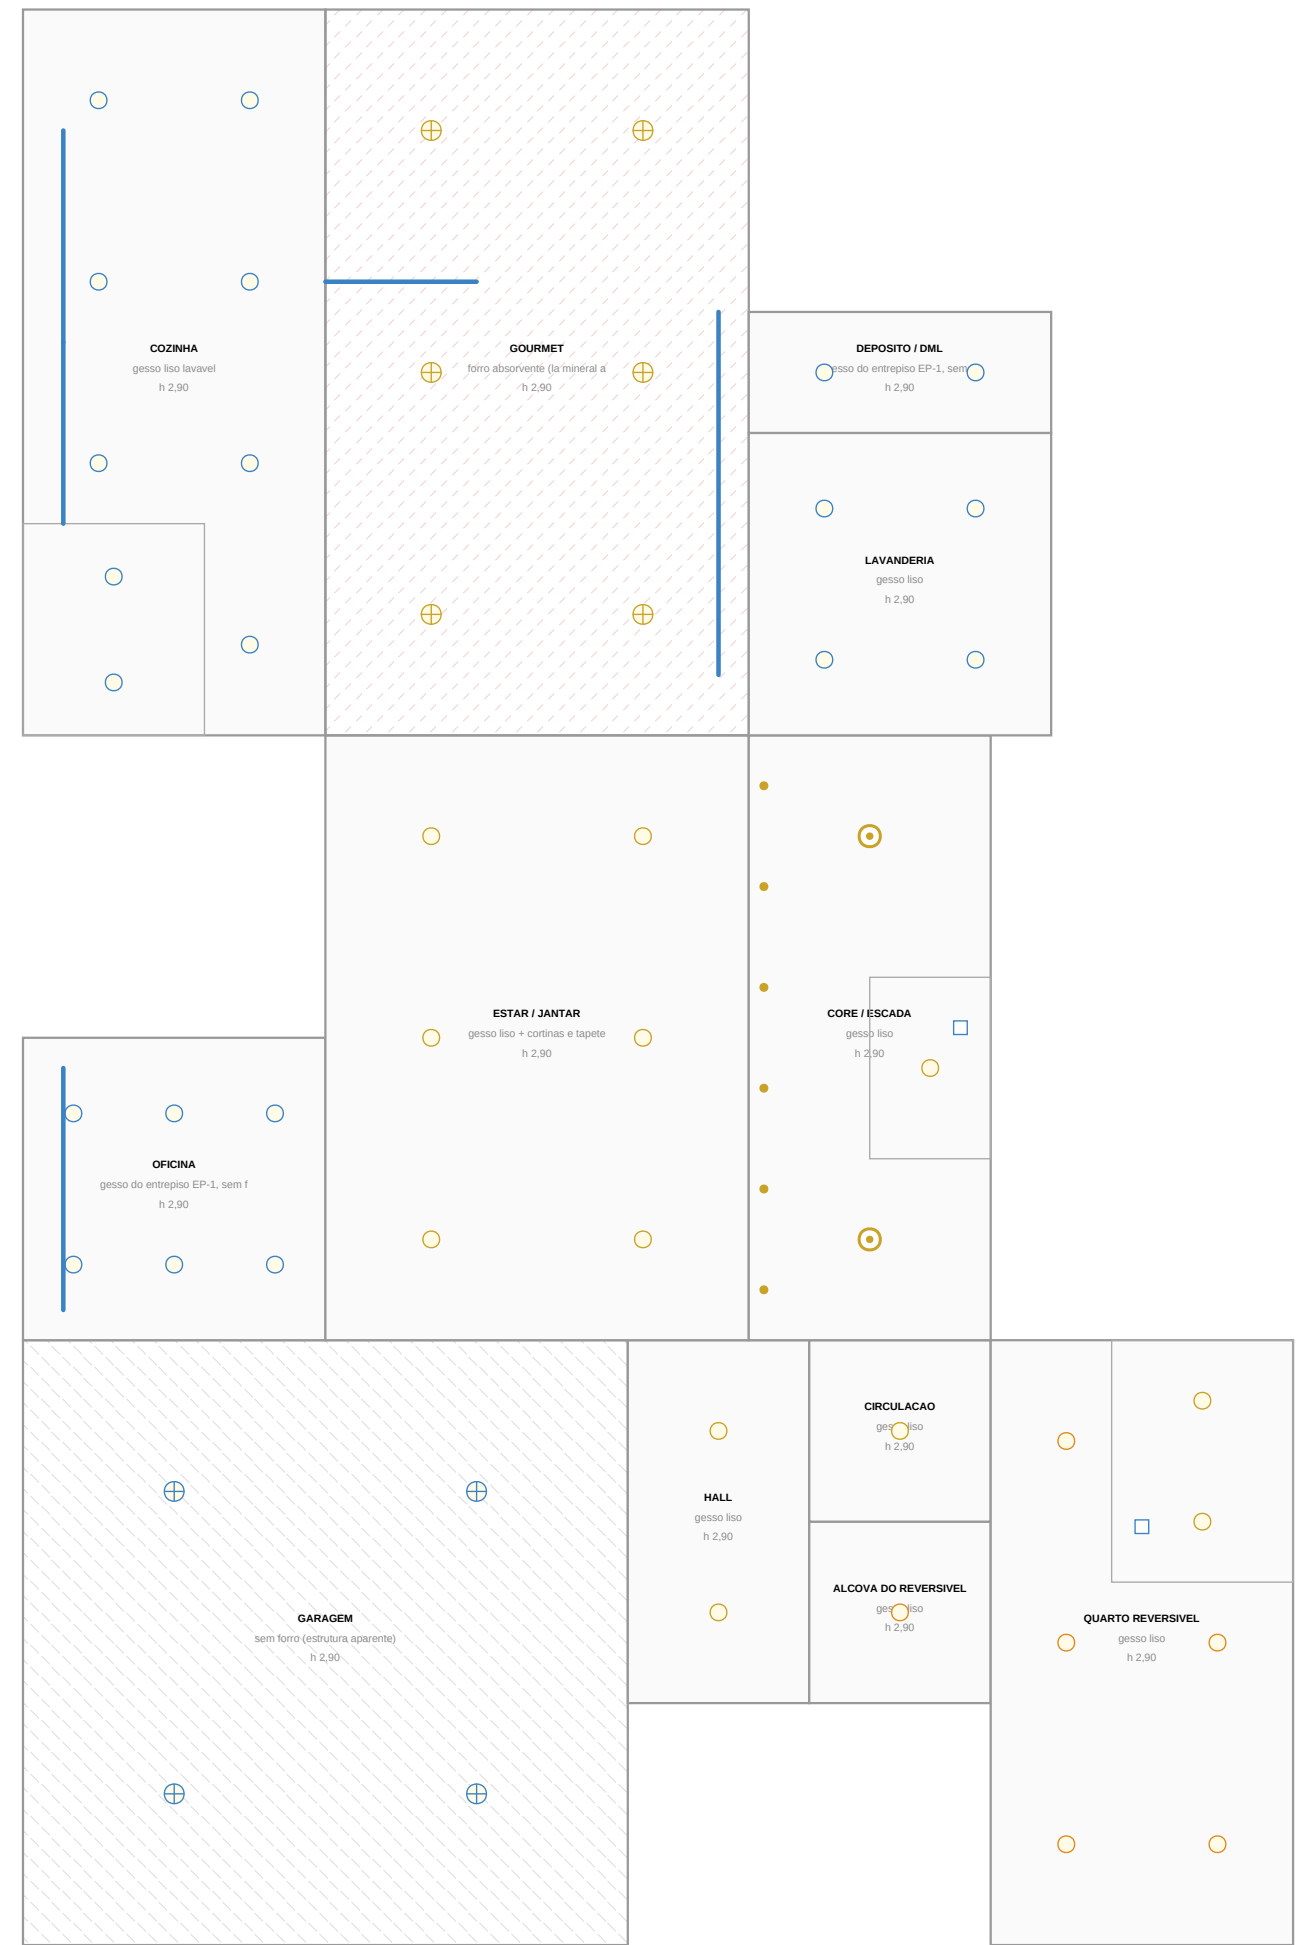

1 FORRO REFLETIDO — TERREO
ESCALA 1:75

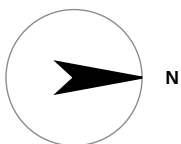

2 FORRO REFLETIDO — SUPERIOR
ESCALA 1:75

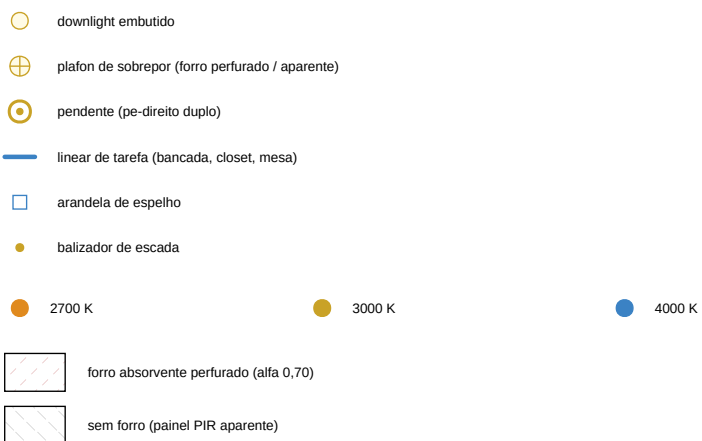

LUMINOTECNICA POR AMBIENTE — METODO DOS LUMENS

AMB	USO	AL	ALC/TA	ALC/TA	LUMINARIA	cor	W
T-GAR	apoi	30.0	75	108	4 x Plafon LED de sobrepor 24 W	4000 K	96
T-AL	circulacao	6.5	100	151	2 x Downlight LED embudo 18 W	3000 K	36
T-ALC	varia	3.0	100	151	1 x Downlight LED embudo 18 W	2700 K	18
T-COR	circulacao	3.0	100	151	1 x Downlight LED embudo 18 W	3000 K	18
T-DEV	varia	12.7	100	200	5 x Downlight LED embudo 18 W	2700 K	90
T-COR	alcova	9.0	100	151	4 x Downlight LED embudo 18 W	4000 K	144
T-SOC	socor	25.2	200	242	8 x Downlight LED embudo 24 W	3000 K	144
T-COR	escada	12.2	100	188	7 x Pendente LED de je-direito dup	3000 K	90
T-COR	circulacao	17.8	300	393	7 x Downlight LED embudo 24 W	4000 K	108
T-GOU	socor	30.2	200	208	6 x Plafon LED de sobrepor 24 W	3000 K	144
T-LAV	varia	9.0	200	245	4 x Downlight LED embudo 18 W	4000 K	72
T-DEP	varia	3.0	200	272	2 x Downlight LED embudo 18 W	4000 K	36
S-SR	varia	20.2	100	172	5 x Downlight LED embudo 18 W	2700 K	90
S-SR	varia	20.2	100	172	5 x Downlight LED embudo 18 W	2700 K	90
S-AL	circulacao	11.5	100	120	2 x Downlight LED embudo 24 W	3000 K	40
S-LOU	socor	7.2	200	393	4 x Downlight LED embudo 24 W	3000 K	96
S-MA	varia	21.6	100	160	6 x Downlight LED embudo 18 W	2700 K	90
S-SR-BANHO	banho	4.3	200	233	2 x Downlight LED embudo 18 W	3000 K	36
S-SR-CLOSET	closet	1.4	100	288	1xw 0.9 m	3000 K	16
S-SR-BANHO	banho	4.3	200	233	2 x Downlight LED embudo 18 W	3000 K	36
S-SR-CLOSET	closet	1.4	200	288	1xw 0.9 m	3000 K	16
T-CLOSET-ESPENSA	varia	3.8	200	398	2 x Downlight LED embudo 24 W	4000 K	48
T-REVER-SANHO	banho	4.3	200	233	2 x Downlight LED embudo 18 W	3000 K	36
T-COR-LAVABO	banho	2.2	200	237	1 x Downlight LED embudo 18 W	3000 K	18
S-MA-SR-BANHO	banho	10.8	200	292	4 x Downlight LED embudo 18 W	3000 K	72
S-MA-SR-CLOSET	closet	9.0	200	242	4 x Downlight LED embudo 18 W	3000 K	72
S-MA-SR-OFFICE	office	5.4	300	512	4 x Downlight LED embudo 24 W	4000 K	96

LUZ DE TAREFA

COD	ONDE	TIPO	QTD	cor
L7-BC-01	banhada BC-01 (T-COD)	linear	2.1 m	4000 K
L7-BC-02	banhada BC-02 (T-COD)	linear	1.8 m	4000 K
L7-BC-03	banhada BC-03 (T-COD)	linear	1.5 m	4000 K
L7-BC-04	banhada BC-04 (T-COD)	linear	3.8 m	4000 K
L7-BC-05	banhada BC-05 (T-COD)	linear	2.4 m	4000 K
L7-AC-01	espelho do banheiro LC-01 (T-COR)	arandela	1	4000 K
L7-AC-02	espelho do banheiro LC-02 (T-RED)	arandela	1	4000 K
L7-AC-03	espelho do banheiro LC-03 (S-SR)	arandela	1	4000 K
L7-AC-04	espelho do banheiro LC-04 (S-SR)	arandela	1	4000 K
L7-AC-05	espelho do banheiro LC-05 (S-MA)	arandela	2	4000 K
L7-S-MA-SR-CLOSET	closet do S-MA	linear	0.9 m	3000 K
L7-S-MA-SR-OFFICE	mesa do office do S-MA	linear	1.2 m	4000 K
L7-ESCADA	escada (balizadores)	balizador	6	3000 K

NOTAS

- Plano refletido: vista do forro projetada no plano horizontal, interno e superior.
- Luminarias pelo METODO DOS LUMENS por ambiente (NBR 9070:2020 / NBR 14123, multa de uniformidade 0.8 1.2).
- 90 pontos por m², 12 pontos de tarefa, 2000 W (6 AL 16W).
- Cor: 2.700 K interno / 3.000 K social e circulação / 4.000 K cozinha, banheiro e trabalho.

PROJETO PORTO REAL

RESIDENCIA UNIFAMILIAR (MANAUS - AM) | 5000 TAREFAS (90)

PROJETO ARQUITETONICO

PLANTA DE FORRO E ILUMINACAO

BASE GEOMETRICA União Consolidada por R2D (previsível) UNIDADE: METRO: mm	ESCALA 1:75 FORMATO: A1 MILHA: 600/500/300	EMISSAO ESTUDO PRELIMINAR RES NÃO LIBERADO PARA OBRA SEM ART / RNT	PROJETO 16 06-43 REV 02
--	--	--	--------------------------------------