


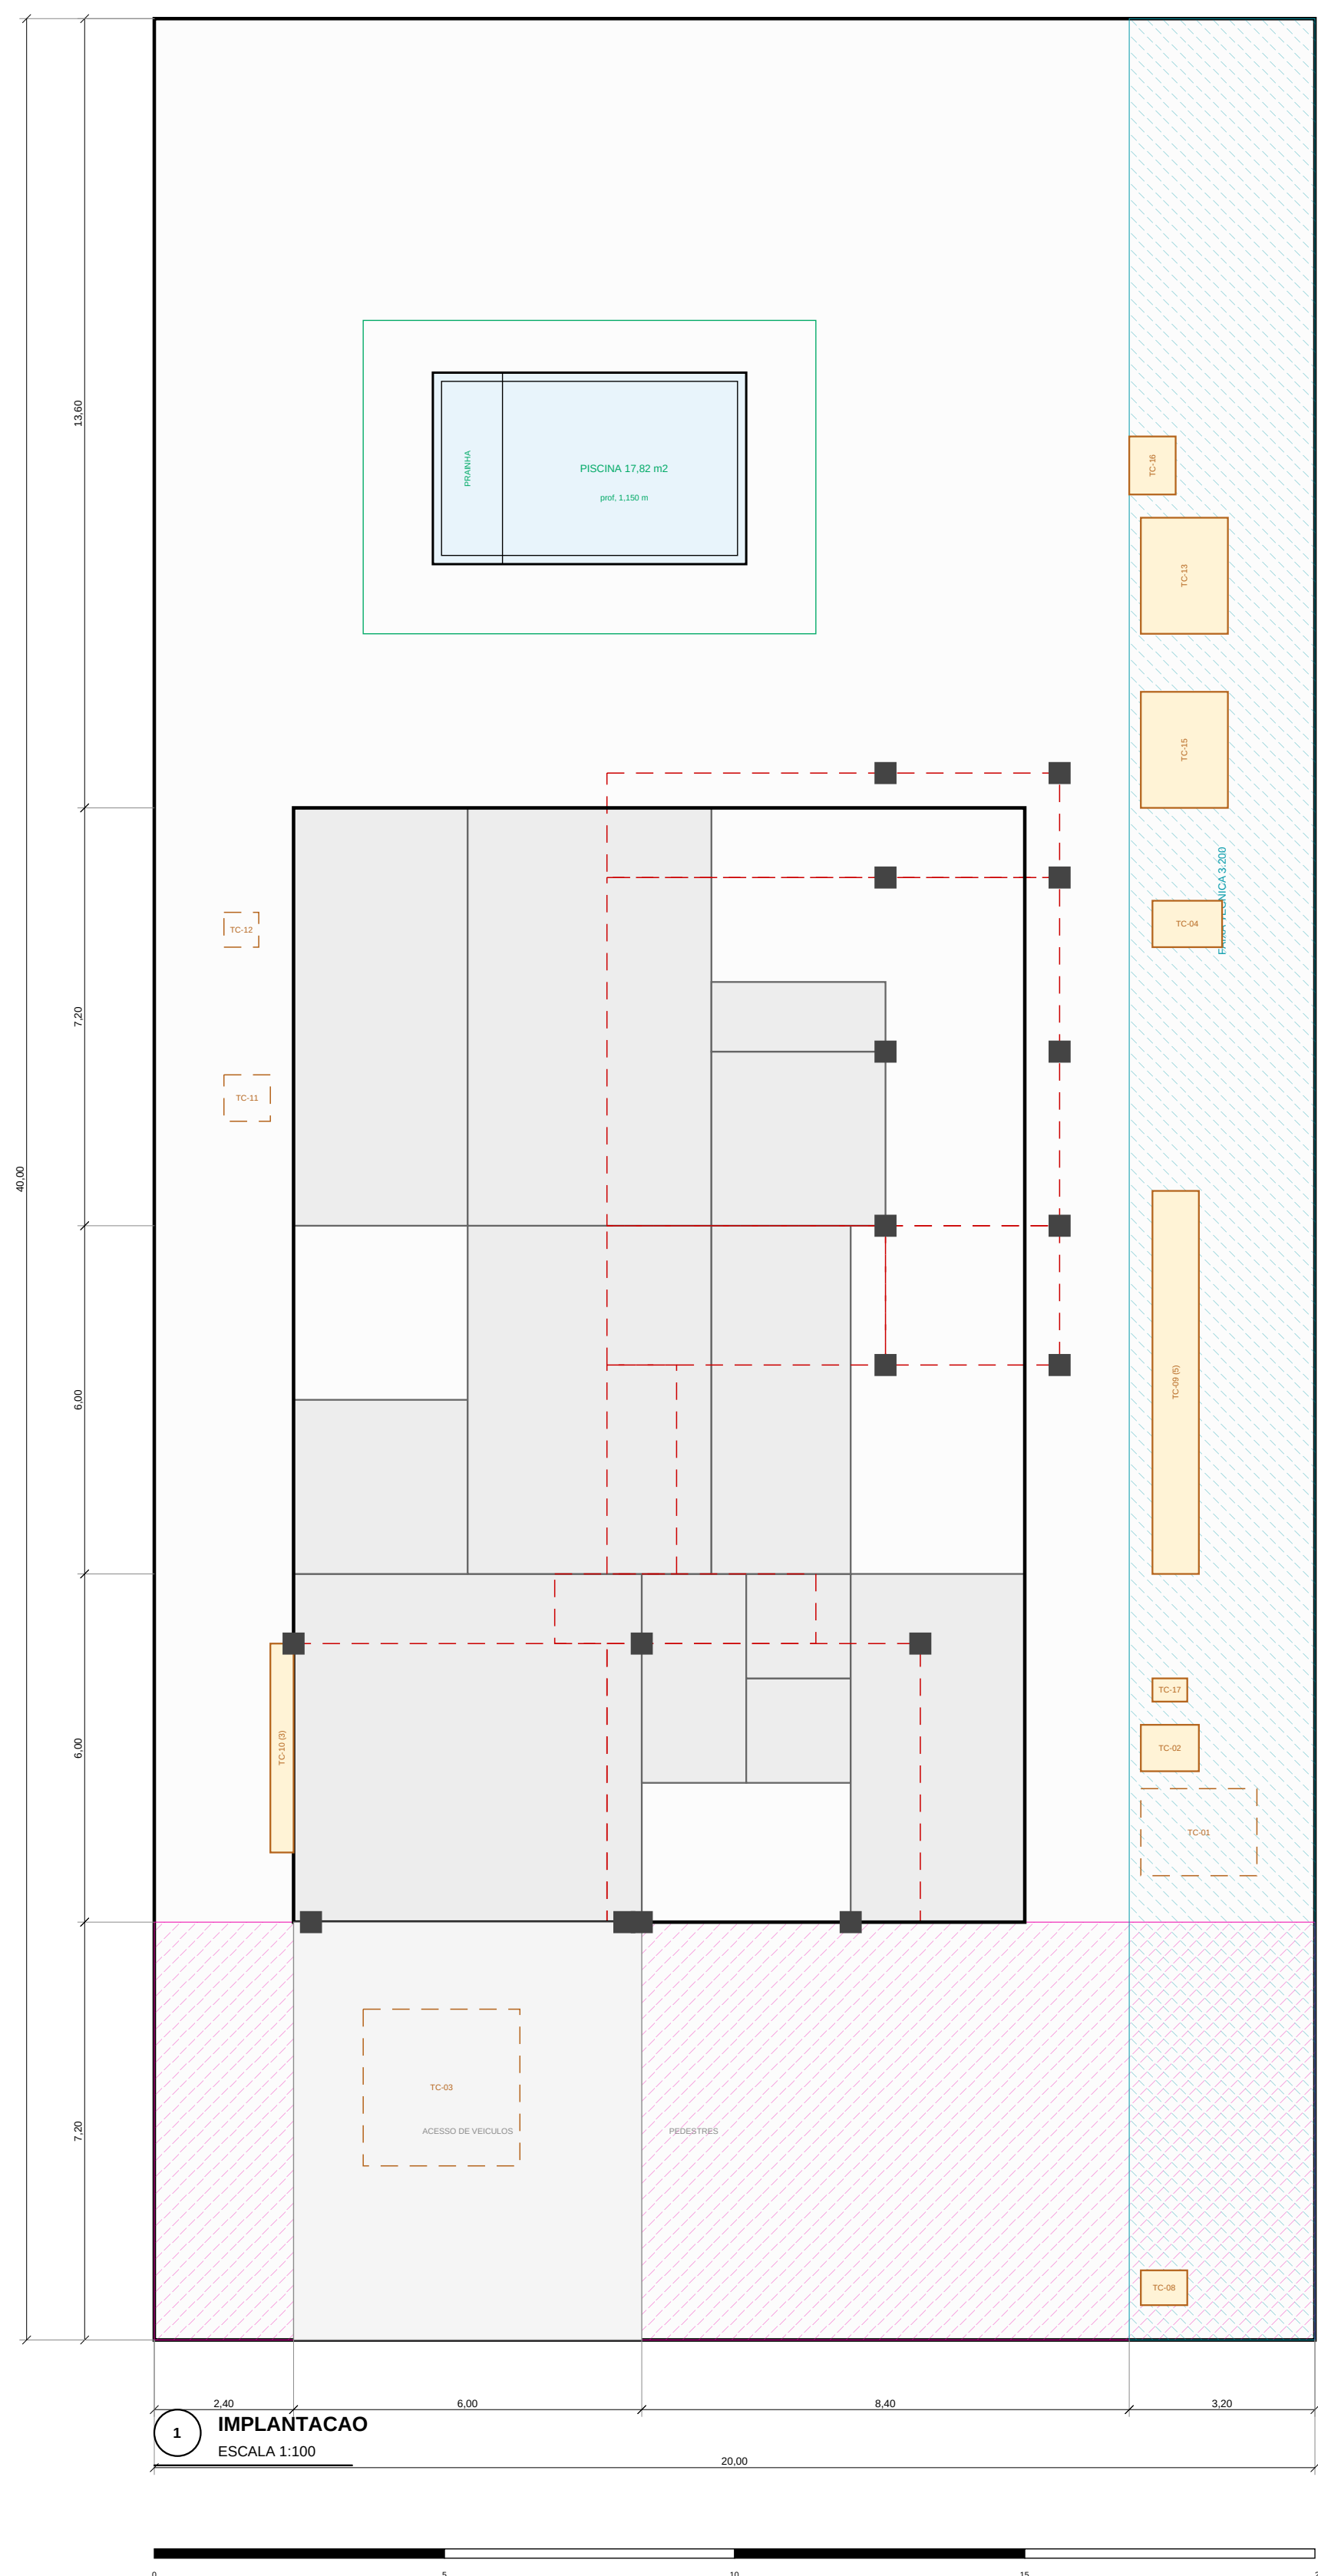

PARAMETRO	PROJETO	LIMITE	
Taxa de ocupação	32,62 %	max 30 %	OK
Cof. de aproveitamento	0,284	max 1,00	OK
Coberto	2 pavimento	max 4	OK
Recuo frontal	7200 mm	conforme SCSB (n)	OK
Recuo lateral eq.	2400 mm	sem parâmetro definido	OK
Faixa técnica de	3300 mm	var. 3000 mm	OK
Recuo de fundo	12600 mm	var. 5000 mm	OK

NOTAS

- Lote 20.000 x 40.000 m = 800.00 m2.
- Recuos: frontal 7,200 / lateral esq. 2,400 / faixa técnica dir. 3,200 / fundo 13,600 metros.
- Parâmetros de SUDS Tatum/Tatum+Águ são hipotéticos (H) – pendente certidão de uso do solo.
- Casa de condôminos: sem muro frontal; muros laterais e de fundo h = 2,200 m; portões laterais PG03/PG03 na linha da frente da casa.

PROJETO PORTO REAL

RESIDÊNCIA UNIFAMILIAR | MANAUS - AM | SU16 TARUMA 7

IMPLANTACAO E SITUACAO

BASE GEOMÉTRICA	ESCALA	EMISSÃO	PRANCHA
Lista Consolidada	1:100	ESTUDO PRELIMINAR R13	01
pos-R13 (previsto)	FORMATO A1	NÃO LIBERADO PARA OBRA	
UNIDADE MEDIDA: m/m	MALHA 600/300/350	SEM ART. RBT	OK 78 REV R13