
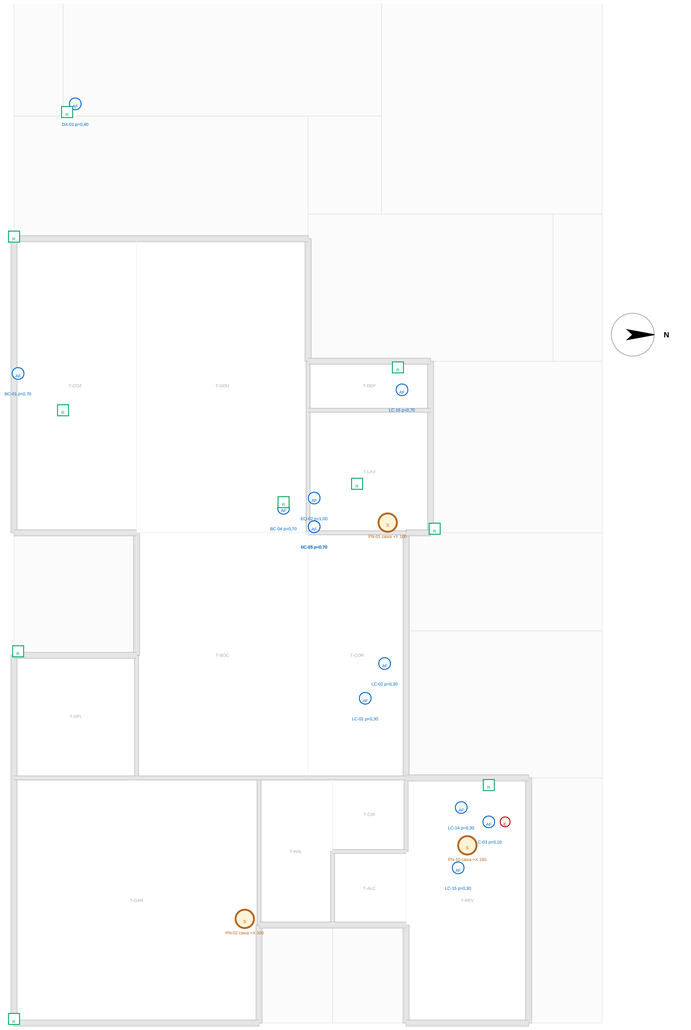


N

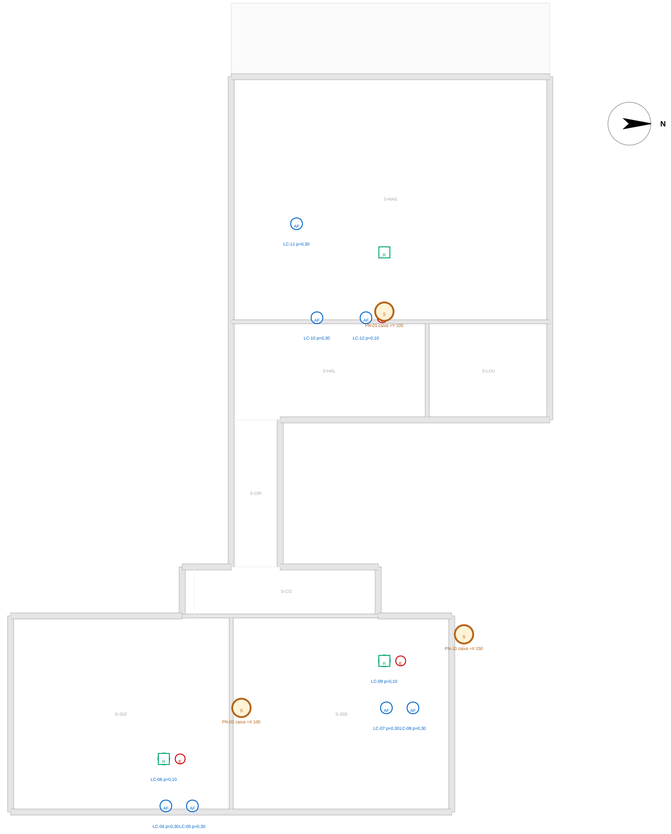

N

1 PONTOS HIDRAULICOS — TERREO

ESCALA 1:75

2 PONTOS HIDRAULICOS — SUPERIOR

ESCALA 1:75

DIMENSIONAMENTO — AGUA FRIA E ESGOTO

TRECHO	PECAS	PESOS	Q (L/s)	DN AGUA	v (m/s)	UHC	DN ESGOTO	REGIME
Superior	9	2,10	0,435	DN25	1,19	27	DN100	pressurizado
Terreo	12	6,20	0,747	DN32	1,23	36	DN100	gravidade
GERAL	21	8,30	0,864	DN32	1,42	63	DN100	gravidade

DECISOES QUE O DIAMETRO REVELA

DECISAO	CONSEQUENCIA HIDRAULICA
Chuveiro eletrico em vez de aquecimento central	peso 0,10 por chuveiro em vez de 0,40: a soma cai de 8,2 para 8,3 pesos e o alimentador de DN40 para DN32
Limite de velocidade por conforto, nao por norma	DN25 atenderia a norma a 2,17 m/s, a 2,0 m/s o tubo nao assobia. Custa alguns metros de tubo
Pressurizador no ramal superior	0,8 mca por gravidade nao aciona chuveiro eletrico; TC-14 entrega 12 mca
Uma unica rede de agua	R52 encerrou o reuso: nao ha rede nao potavel no lote, e com ela desapareceu a unica possibilidade de conexao cruzada
Caixa de gordura antes da inspecao	cozinha -> TC-11 (30 L) -> TC-12 -> rede; DN100 com caimento de 2 %

PECAS DE UTILIZACAO

COD	AMB	TIPO	PESO	UHC	DN AF	DN ESG	QUENTE
LC-01	T-COR	vaso	0,30	6	DN25	DN50	—
LC-02	T-COR	lavatorio	0,30	1	DN25	DN40	—
LC-03	T-REV	box	0,10	2	DN25	DN40	sim
LC-14	T-REV	vaso	0,30	6	DN25	DN50	—
LC-15	T-REV	lavatorio	0,30	1	DN25	DN40	—
LC-04	S-SO2	vaso	0,30	6	DN25	DN50	—

(continuacao)

COD	AMB	TIPO	PESO	UHC	DN AF	DN ESG	QUENTE
LC-10	S-MAS	vaso	0,30	6	DN25	DN50	—
LC-11	S-MAS	lavatorio	0,30	1	DN25	DN40	—
LC-12	S-MAS	box	0,10	2	DN25	DN40	sim
LC-13	T-LAV	tanque	0,70	3	DN25	DN40	—
LC-16	T-DEP	tanque	0,70	3	DN25	DN40	—

(continuacao)

COD	AMB	TIPO	PESO	UHC	DN AF	DN ESG	QUENTE
BC-01	T-COZ	pia	0,70	3	DN25	DN40	—
BC-04	T-GOU	pia	0,70	3	DN25	DN40	—
BC-05	T-LAV	pia	0,70	3	DN25	DN40	—
EQ-02	T-LAV	lavadora	1,00	3	DN25	DN40	—
DX-01	T-DKP	ducha_externa	0,40	2	DN25	DN40	—

NOTAS

- Agua fria por metodo dos pesos (NBR 5626): Q = 0,30 x raiz(soma dos pesos) = 0,864 L/s com 8,3 pesos.
- Alimentador DN32 a 1,42 m/s — limitado pelo conforto (2,0 m/s), nao pela norma (3,0 m/s).
- Esgoto por UHC (NBR 8160): 63 UHC, tubo de queda DN100, ventilacao DN50.
- Chuveiro ELETRICO tem peso 0,10, nao 0,40: a decisao do aquecimento reaparece aqui como diametro menor em toda a casa.

PROJETO PORTO REAL

RESIDENCIA UNIFAMILIAR | MANAUS - AM | S/158 TARUMÃ (H)

PROJETO ARQUITETONICO

INSTALACOES HIDROSSANITARIAS

BASE GEOMETRICA	ESCALA	EMISSAO	PRANCHA
Lista Consolidada pos-R32 (prevalece)	1:75 FORMATO A1	ESTUDO PRELIMINAR R83 NAO LIBERADO PARA OBRA	26
UNIDADE MESTRE: mm	MALHA 600/300/150	SEM ART / RRT	de 76 REV R83