

folha opaca

folha opaca


folha opaca

folha opaca

folha opaca

folha opaca

vidro laminado 6+6 PVB acústico + controle solar

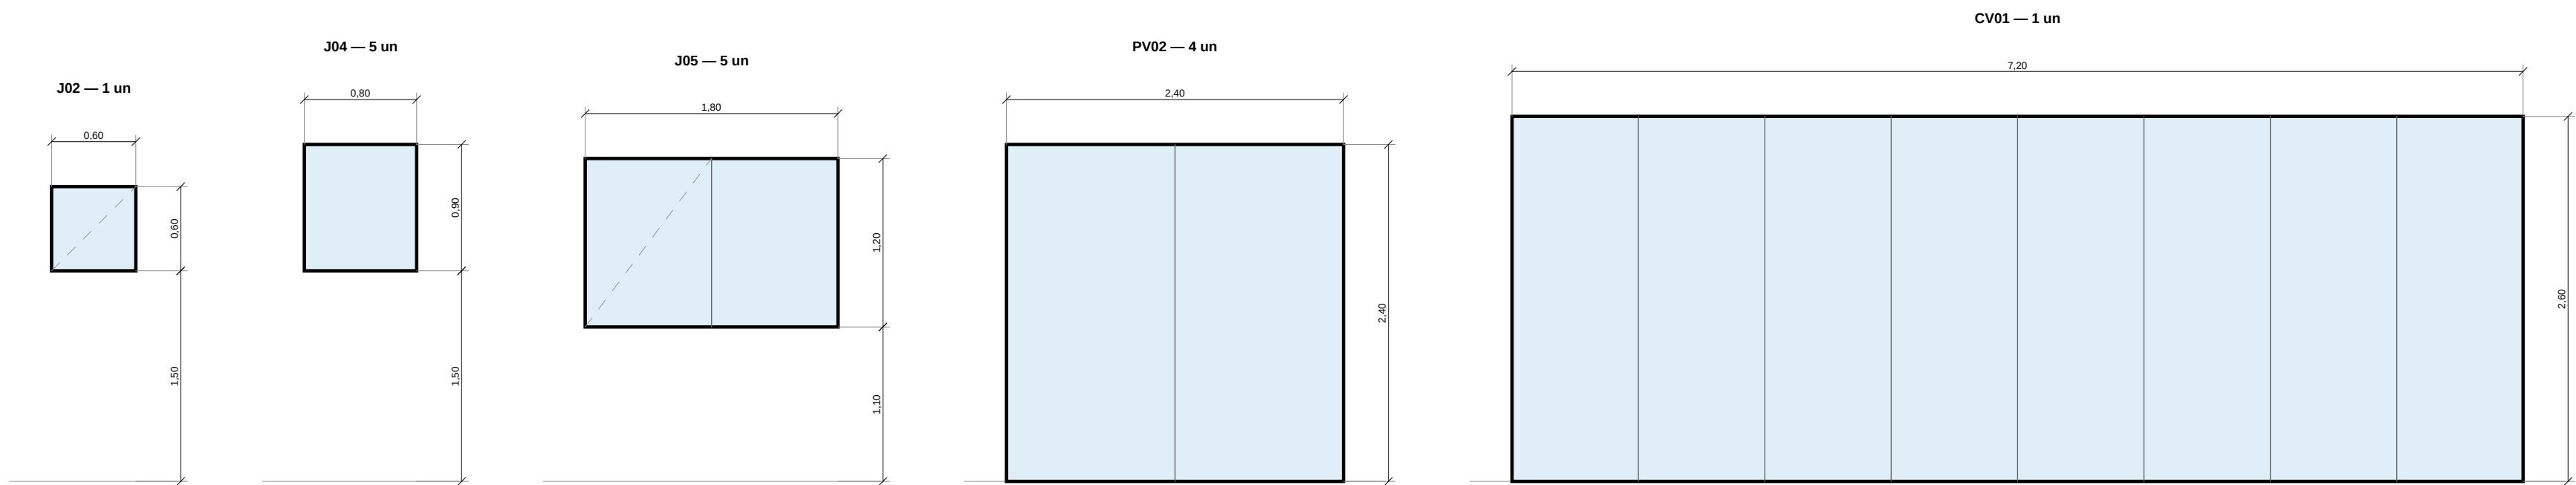




vidro temperado 6 mm translúcido

vidro temperado 6 mm translúcido com controle solar

vidro laminado 6+6 PVB acústico + controle solar

vidro temperado 6 mm controle

vidro laminado 6+6 baixa, 6 folhas de 800 mm, 6 m

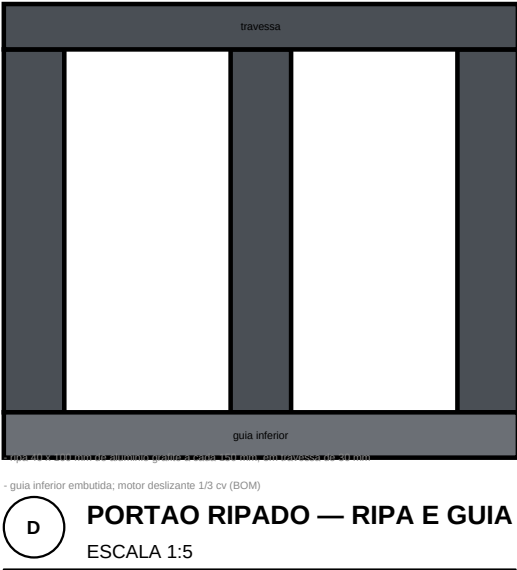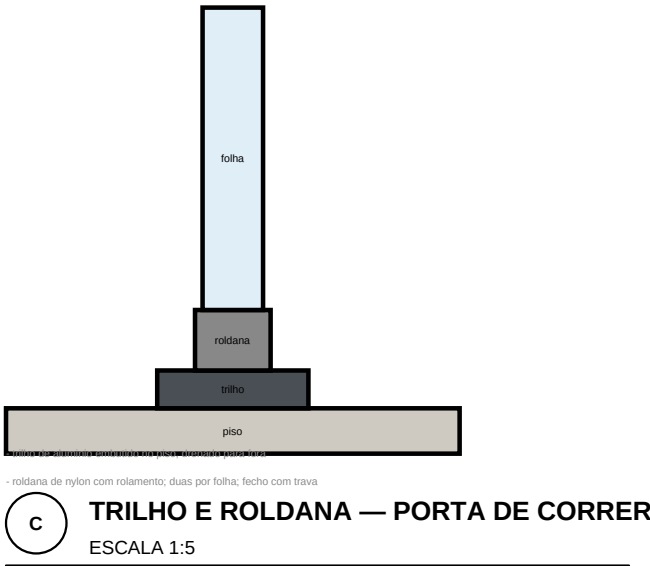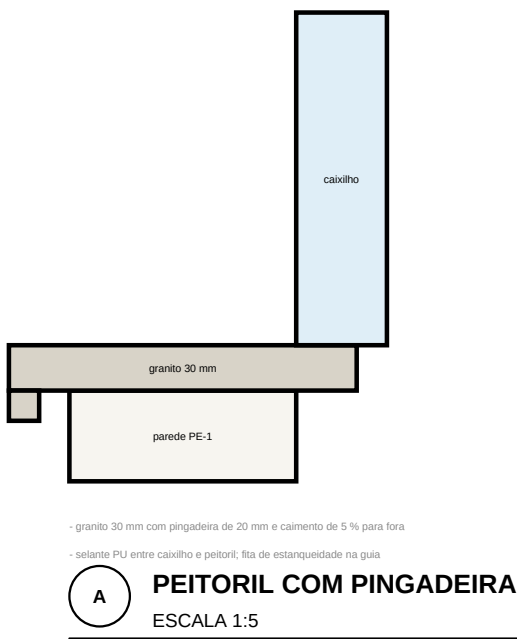

- NOTAS
- 1. Uma referência por família em uso, com largura e altura, perfil, quantidade e o vidro que a regula de fator solar (verificar a família vidro_06_vidro).
 - 2. Famílias declaradas SEM USO (J02, PV02) ficam fora, enquanto que não estão em VACOS não é comprada.
 - 3. Detalhes 1:5 — perfil com pingadeira, sulcos de porta externa, vidro e sistema de porta de correr, ripa e guia de perfil — são os quatro elementos que decidem a estanqueidade.
 - 4. Acabamento grates em todas as famílias (ACABADA_MATEMATICA), sem PVC, sem ventilação.

PROJETO PORTO REAL

RESIDENCIA UNIFAMILIAR (MARIAUS - AM) | SOUZA TATIANA-PS

PROJETO ARQUITETONICO

ESQUADRIAS — TIPOS, QUANTIDADES E DETALHES

BASE GEOMETRICA	ESCALA	EXATIDAO	PROVA
Unidade Consolidada	1:40 • 1:5	ESTUDO PRELIMINAR RES	52
uso RIZZ (previsão)	FORMATO A1	NAO LIBERADO PARA OBRA	SEM ART / RINT
UNIDADE MESTRE: mm	MAIUS 600/600/600		60-75 REV 02