



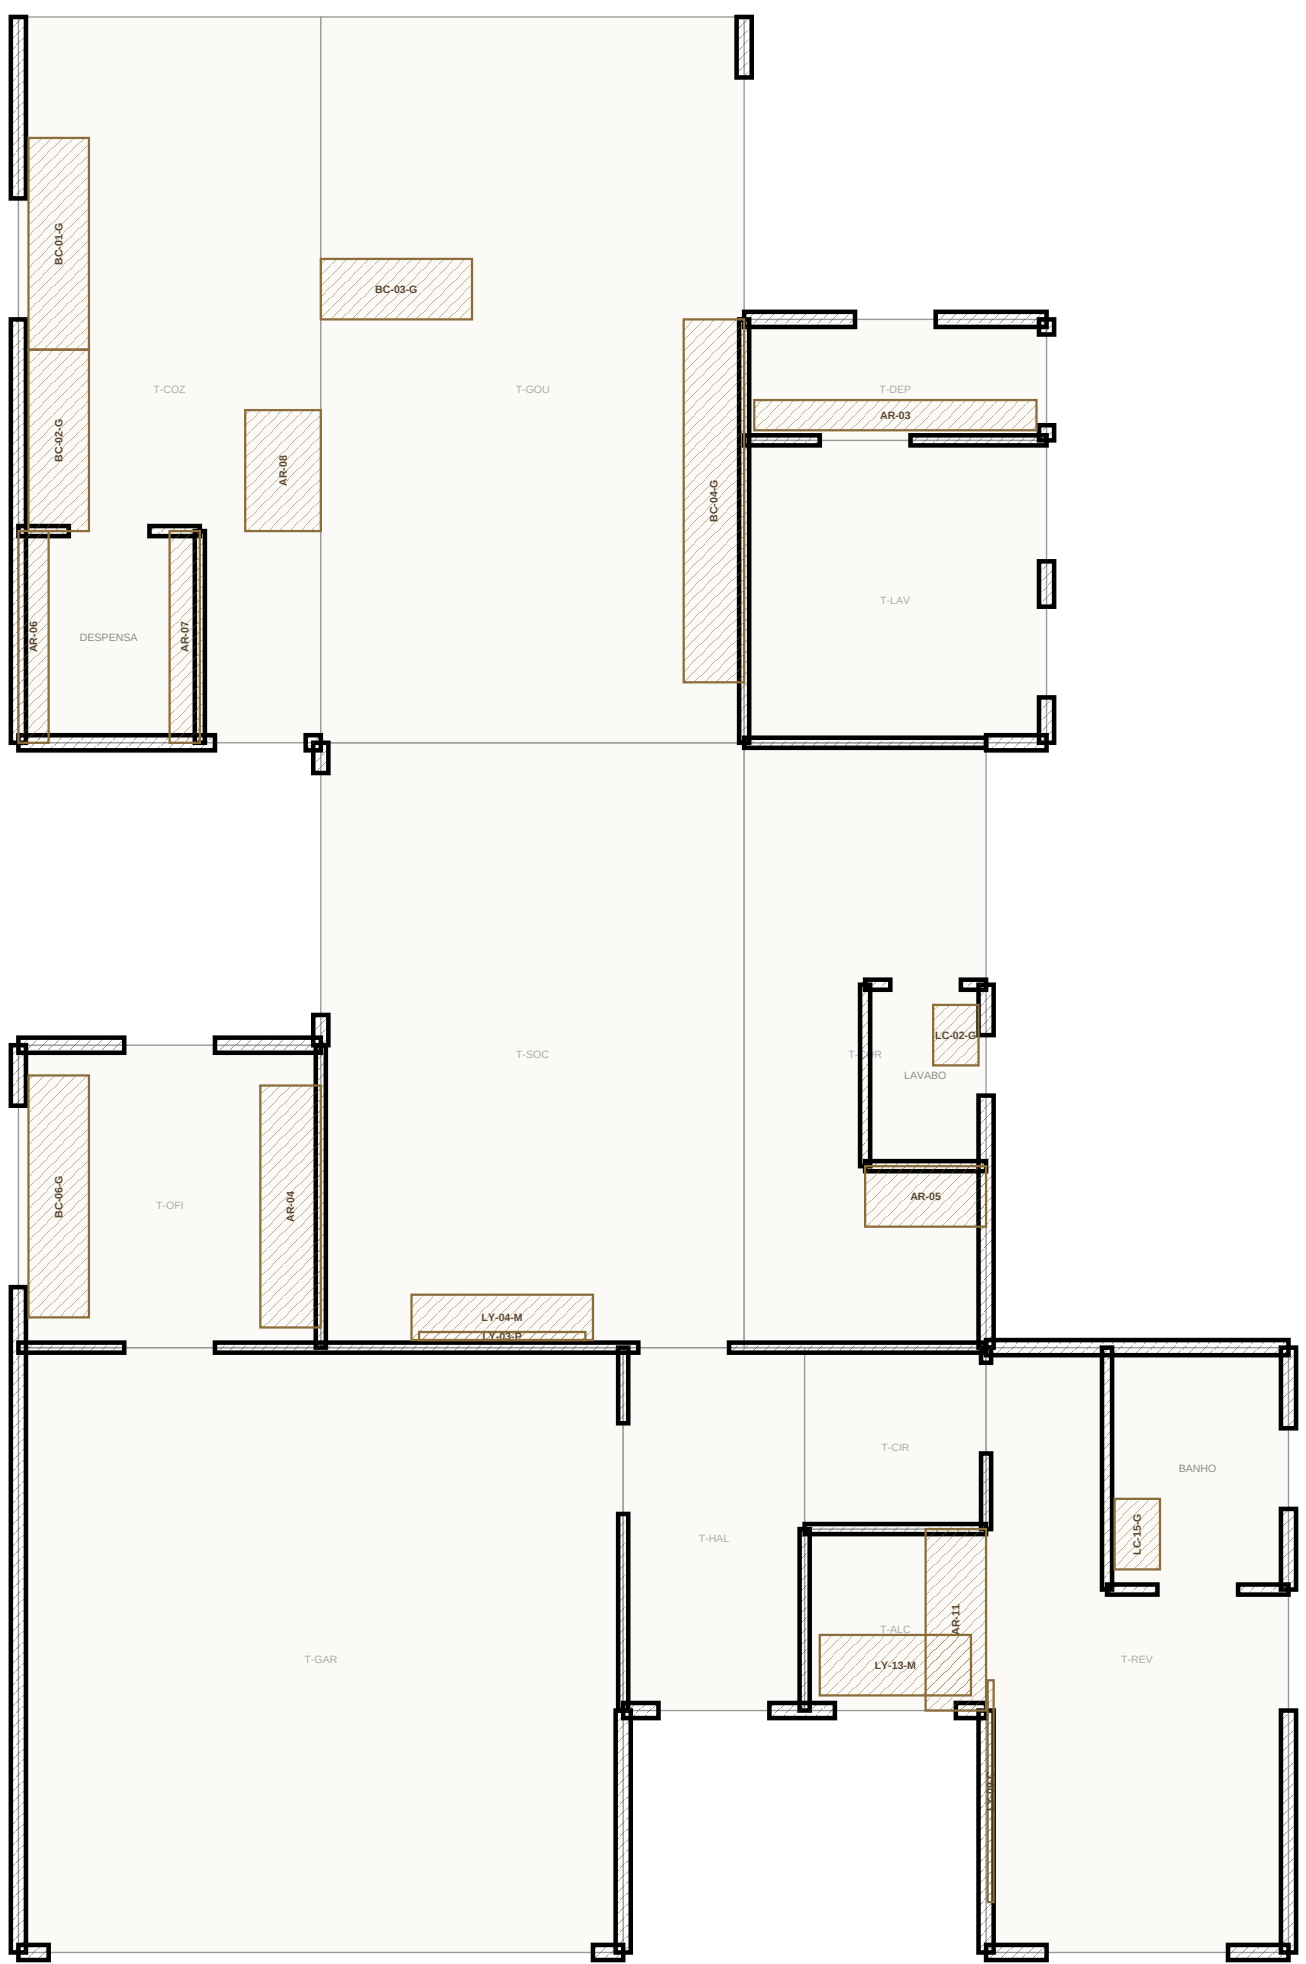

1 TERREO — MARCENARIA
ESCALA 1:75

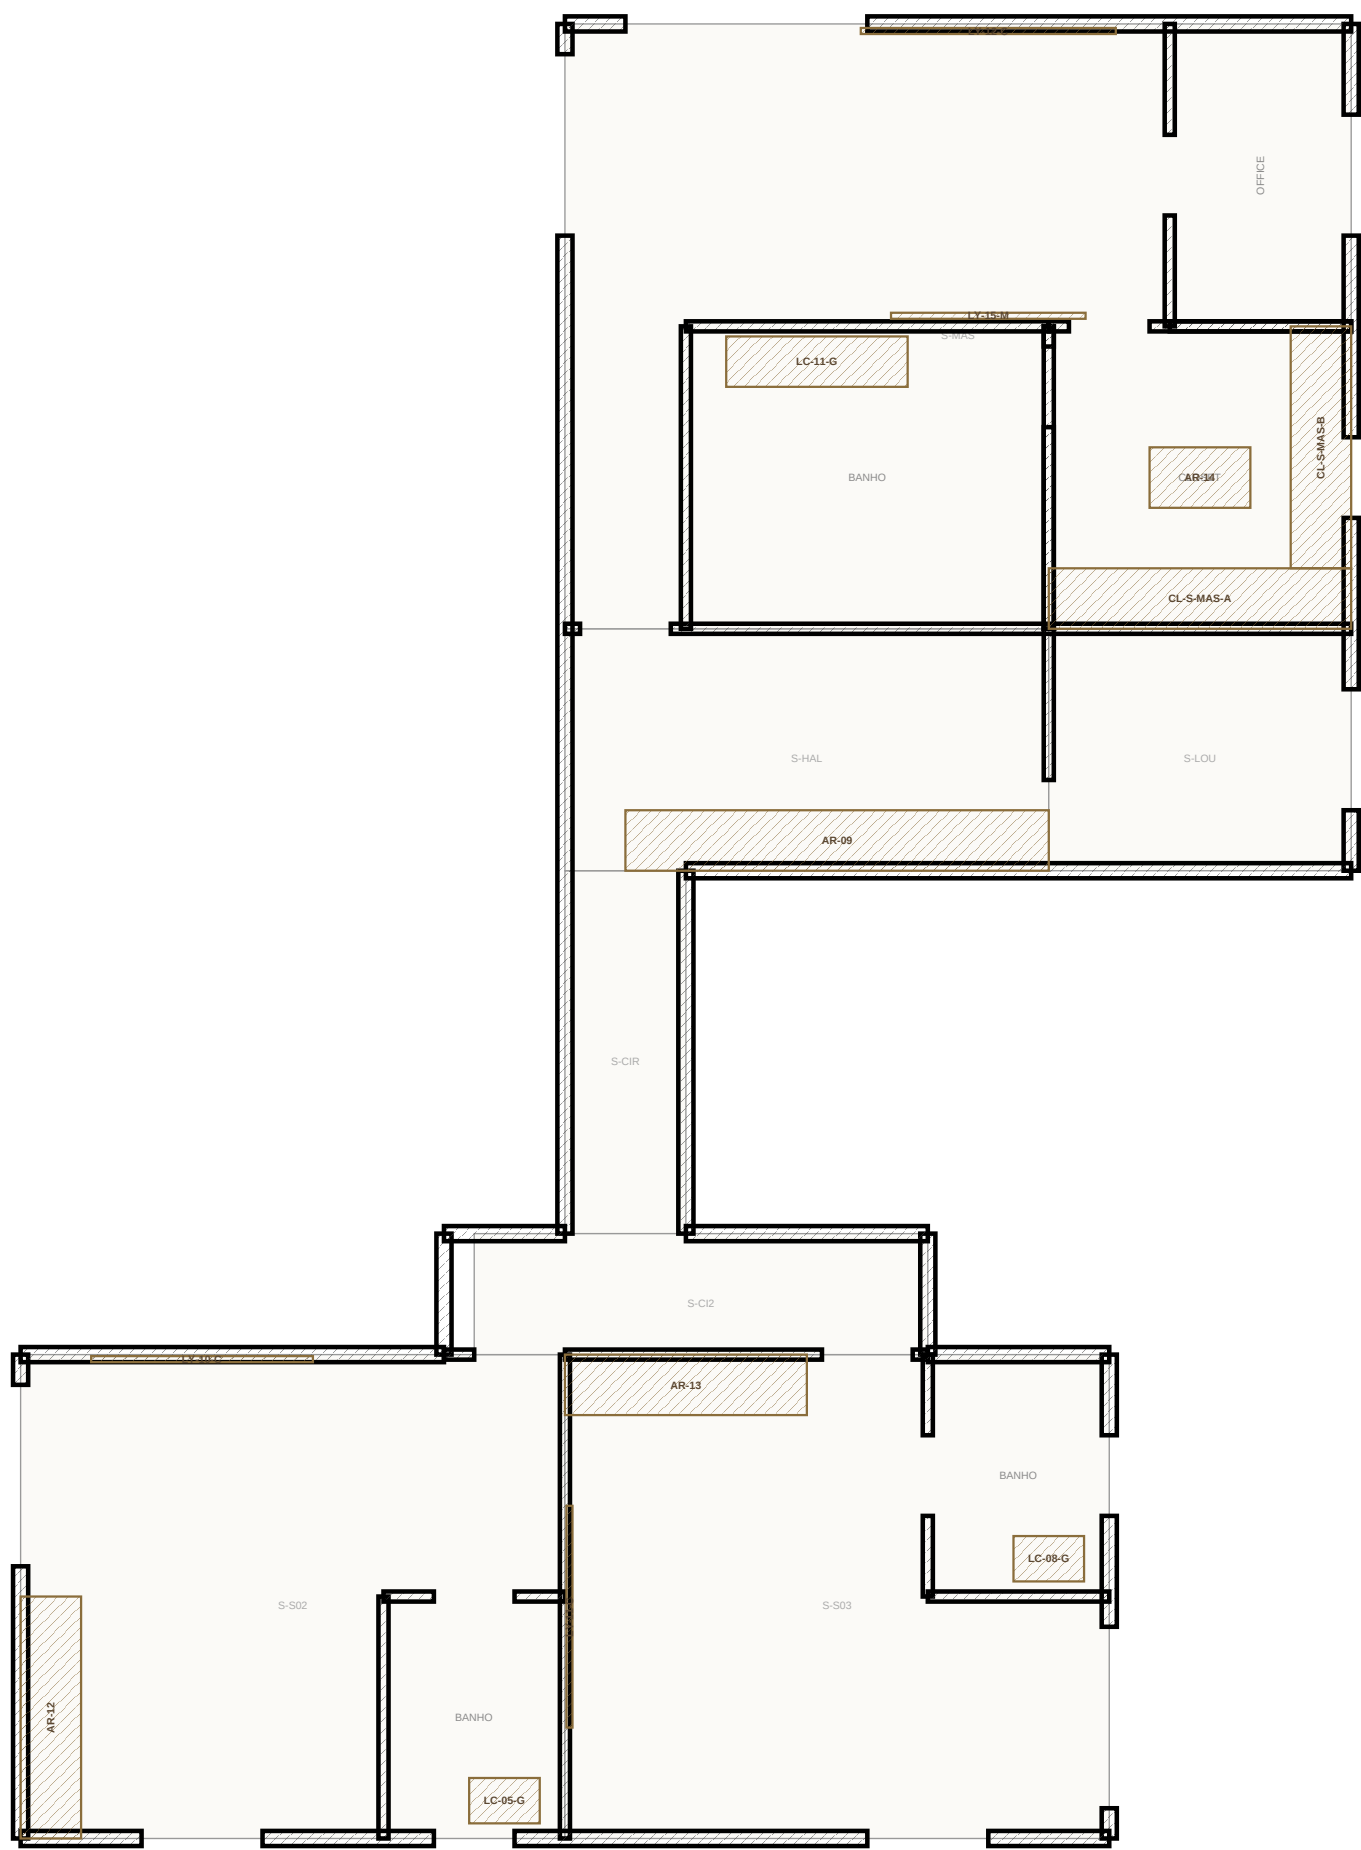

2 SUPERIOR — MARCENARIA
ESCALA 1:75

QUADRO DE MOVEIS — TUDO O QUE E MARCENARIA NA CASA

COD	AMB	FAMILIA	FRENTE	PROF	ALT	MOD	PORTAS	QAV	m2 FR
AB-05	T-COR	prateleira	1.200	800	1.200	2	0	0	1,44
AD-06	T-COZ	prateleira	2.100	300	2.100	4	0	0	4,42
AD-07	T-COZ	prateleira	2.100	300	2.100	4	0	0	4,42
AB-08	T-COZ	armario alto	1.300	750	2.300	2	2	0	2,64
AD-03	T-DEP	prateleira	2.800	300	2.200	5	0	0	6,16
AB-04	T-GR	armario alto	2.400	600	2.300	4	4	0	6,16
AB-09	S-HAL	rouparia	4.200	600	2.200	7	7	0	9,24
AB-11	T-ALC	guarda-roupa	1.800	600	2.200	3	3	8	3,96
AB-12	S-SO2	guarda-roupa	2.400	600	2.200	4	4	8	5,28
AB-13	S-SO3	guarda-roupa	2.400	600	2.200	4	4	8	5,28
AB-14	S-MAS	guarda-roupa	1.900	600	900	2	0	8	0,60
BC-01-G	T-COZ	patinete	2.100	580	770	4	4	0	1,62
BC-02-G	T-COZ	patinete	1.800	580	770	3	3	0	1,36
BC-03-G	T-COZ	patinete	1.500	580	770	3	3	0	1,18
BC-04-G	T-COZ	patinete	1.800	580	770	4	4	0	2,17
BC-05-G	T-GR	patinete	2.400	580	770	4	4	0	1,65
LC-05-G	T-COR	patinete banho	800	450	580	1	0	2	0,36
LC-06-G	T-REV	patinete banho	700	450	580	2	0	2	0,36
LC-08-G	S-SO2	patinete banho	700	450	580	2	0	2	0,36
LC-08-G	S-SO3	patinete banho	700	450	580	2	0	2	0,36
LC-11-G	S-MAS	patinete banho	1.900	580	760	3	0	2	0,60
LV-03-P	T-DEC	panela tv	1.800	55	1.800	1	0	5	3,24
LV-04-M	T-SOC	rack	1.800	450	450	3	0	3	0,81
LV-06-C	T-REV	cabineira	2.200	65	1.200	1	0	5	2,64
LV-12-M	T-ALC	mesa	1.500	600	750	1	0	3	1,12
LV-13-C	S-SO2	cabineira	2.200	65	1.200	1	0	5	2,64
LV-13-C	S-SO3	cabineira	2.200	65	1.200	1	0	5	2,64
LV-13-C	S-MAS	cabineira	2.200	65	1.200	1	0	5	3,04
LV-15-M	S-MAS	panela tv	1.900	55	1.800	1	0	5	3,47
CL-S-MAS-A	S-MAS	closet	3.000	600	2.200	5	0	10	6,60
CL-S-MAS-B	S-MAS	closet	2.400	600	2.200	4	0	8	6,16

TOTAIS

moveis	25
rodapeis	85
portas	584
portas / guarda	44 164
frente total	91,34 m2
chapeis 15,16 m2	66 1,20

NOTAS

- * Cada moveel vem de nucleos/marcenarias: ARMARIOS, gabinete de cada BANCADA de granito, gabinete suspenso de cada bancada, rack, painel de TV e mesa de LAYOUT, cabineira de cada cama e os dois paineis do CLOSET.
- * Mobili maximo 500 mm (altura da porta), altura por familia (2).
- * Frente e a dimensao ao longo da parede, profundidade e o outro. Elevacoes nas PR-05 e 07.
- * Posicao por categoria de ambiente: sala de aluminio grafico nos areas sociais e de servico, cama e 60 gram nos dormitorios.

PROJETO PORTO REAL

RESIDENCIA UNIFAMILIAR (MARIAUS - AM) | SOUS TATIANA-PS

PROJETO ARQUITETONICO

PLANTA DE MARCENARIA — TERREO E SUPERIOR

BASE GEOMETRICA

Unia Consolidada

PR-012 (previsao)

UNIDADE METRICA: MM

ESCALA

1:75

FORMATO A1

MALHA 600/600/300

ENTRADA

ESTUDO PRELIMINAR RES

NAO LIBERADO PARA OBRA

SEM ART / RNT

PROJETA

55

06-78 REV 002