



1 BC-01 GABINETE SOB GRANITO
ESCALA 1:40

4 mod. - 0,53m - 0,80m - 2,12m - perfil gabi de alumínio graf

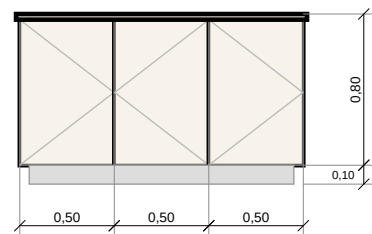


4 BC-03 GABINETE SOB GRANITO
ESCALA 1:40

3 mod. - 0,50m - 0,80m - 1,50m - perfil gabi de alumínio graf

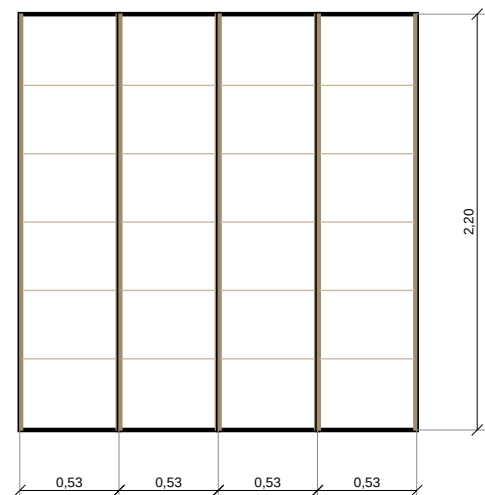


7 AR-06 PRATELEIRAS
ESCALA 1:40

4 mod. - 0,53m - 0,80m - 2,12m - perfil gabi de alumínio graf

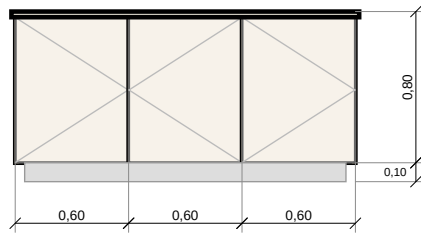


2 BC-02 GABINETE SOB GRANITO
ESCALA 1:40

3 mod. - 0,60m - 0,80m - 1,80m - perfil gabi de alumínio graf

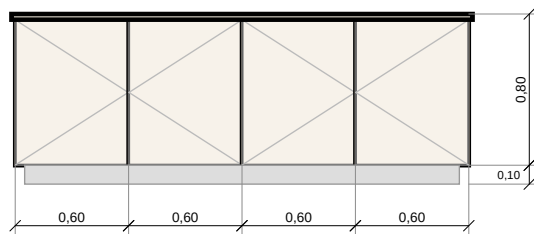


5 BC-06 GABINETE SOB GRANITO
ESCALA 1:40

4 mod. - 0,60m - 0,80m - 2,40m - perfil gabi de alumínio graf

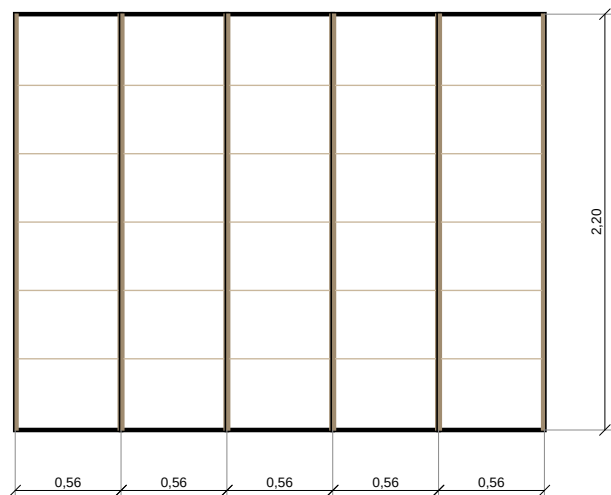


8 AR-03 PRATELEIRAS
ESCALA 1:40

5 mod. - 0,56m - 0,80m - 2,80m - perfil gabi de alumínio graf

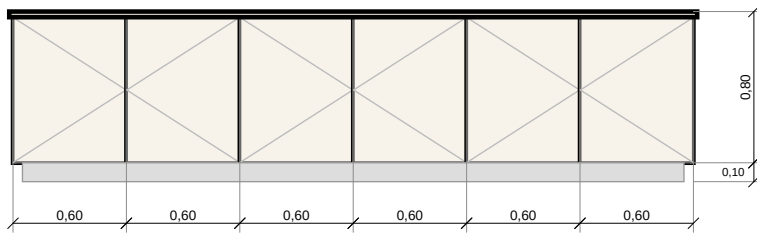


3 BC-04 GABINETE SOB GRANITO
ESCALA 1:40

6 mod. - 0,60m - 0,80m - 3,60m - perfil gabi de alumínio graf

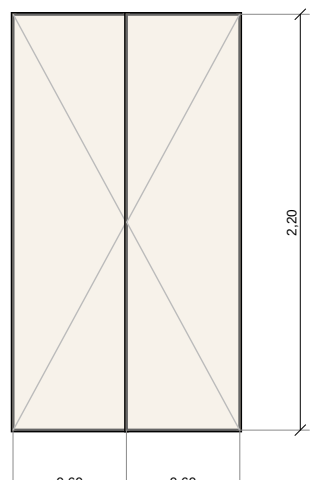


6 AR-08 ARMARIO ALTO
ESCALA 1:40

2 mod. - 0,60m - 0,80m - 1,20m - perfil gabi de alumínio graf

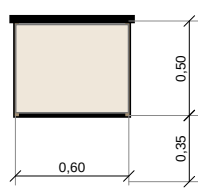


9 LC-02 GAB. LAVATORIO
ESCALA 1:40

1 mod. - 0,60m - 0,80m - 0,80m - perfil gabi de alumínio graf

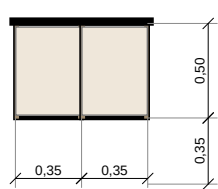


11 LC-05 GAB. LAVATORIO
ESCALA 1:40

2 mod. - 0,35m - 0,80m - 0,70m - perfil gabi de alumínio graf

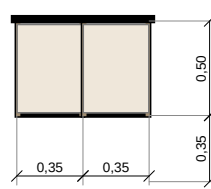


10 LC-15 GAB. LAVATORIO
ESCALA 1:40

2 mod. - 0,35m - 0,80m - 0,70m - perfil gabi de alumínio graf

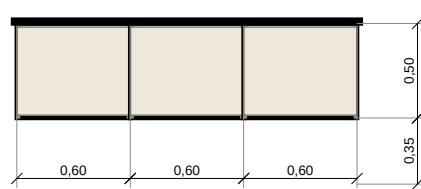

12 LC-11 GAB. LAVATORIO
ESCALA 1:40

3 mod. - 0,60m - 0,80m - 1,80m - perfil gabi de alumínio graf

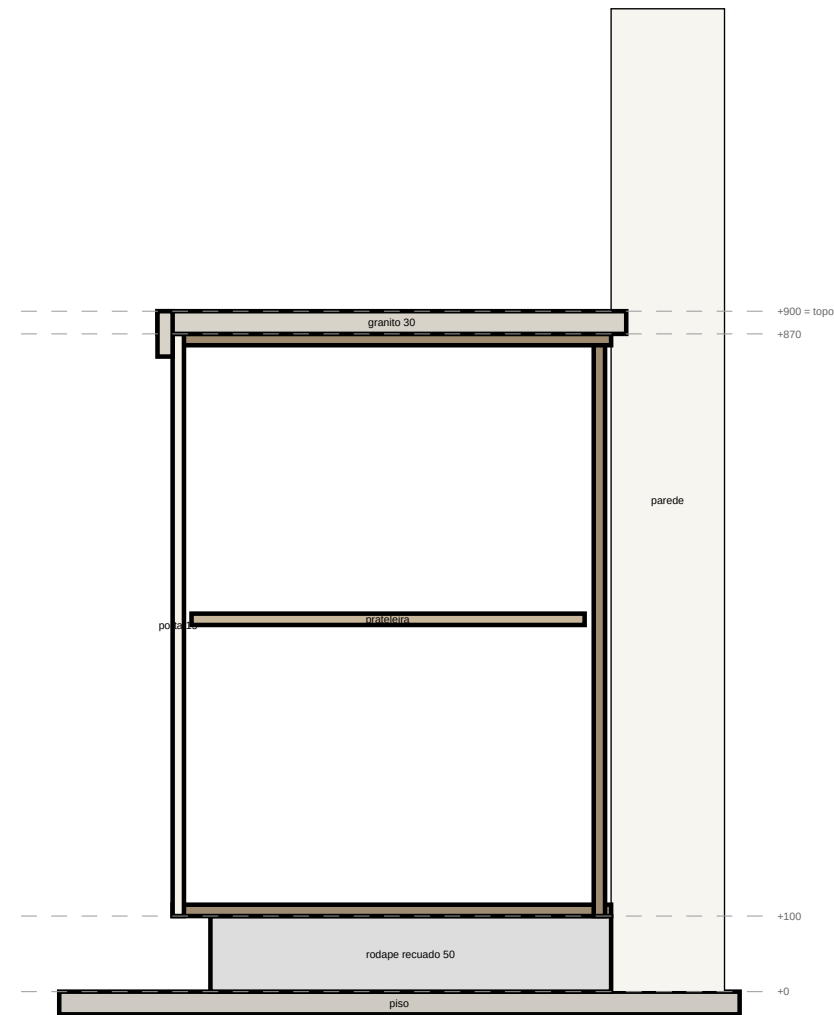

A SECAO DO GABINETE SOB GRANITO — APOIO E RODAPE
ESCALA 1:10

NOTAS

- Gabinete sob granito: caixa de MDF 15 mm sobre suporte, rodape recuado 50 mm, tempo a 800 mm. Módulo com tábua sem prateleira, módulo de cooktop com uma.
- Gabinete de lavatório suspenso a 200 mm do piso, uma gaveta por módulo, cuba de apoio.
- Porta por módulo, abridoras pela altura (2 até 900, 3 até 1.500, 4 até 2.000, 5 acima).
- Prateleira travada e arca de porta. Puxador perfil gabi graf no sentido vertical.

PROJETO PORTO REAL

RESIDENCIA UNIFAMILIAR (MANAUS - AM) | SOUZA TATIANA-PS

PROJETO ARQUITETONICO

MARCENARIA I — GABINETES DE COZINHA, GOURMET, OFICINA E BANHOS

BASE GEOMETRICA	ESCALA	EMISSAO	PROJECION
União Consolidada	1:40 • 1:10	ESTUDIO PRELIMINAR RES	56
Projeto (previsão)	FORMATO A1	NAO LIBERADO PARA OBRA	SEM ART / PRINT
UNIDADE: METROS: mm	MAQUETA: 600/900/300		em 18 REV 02