
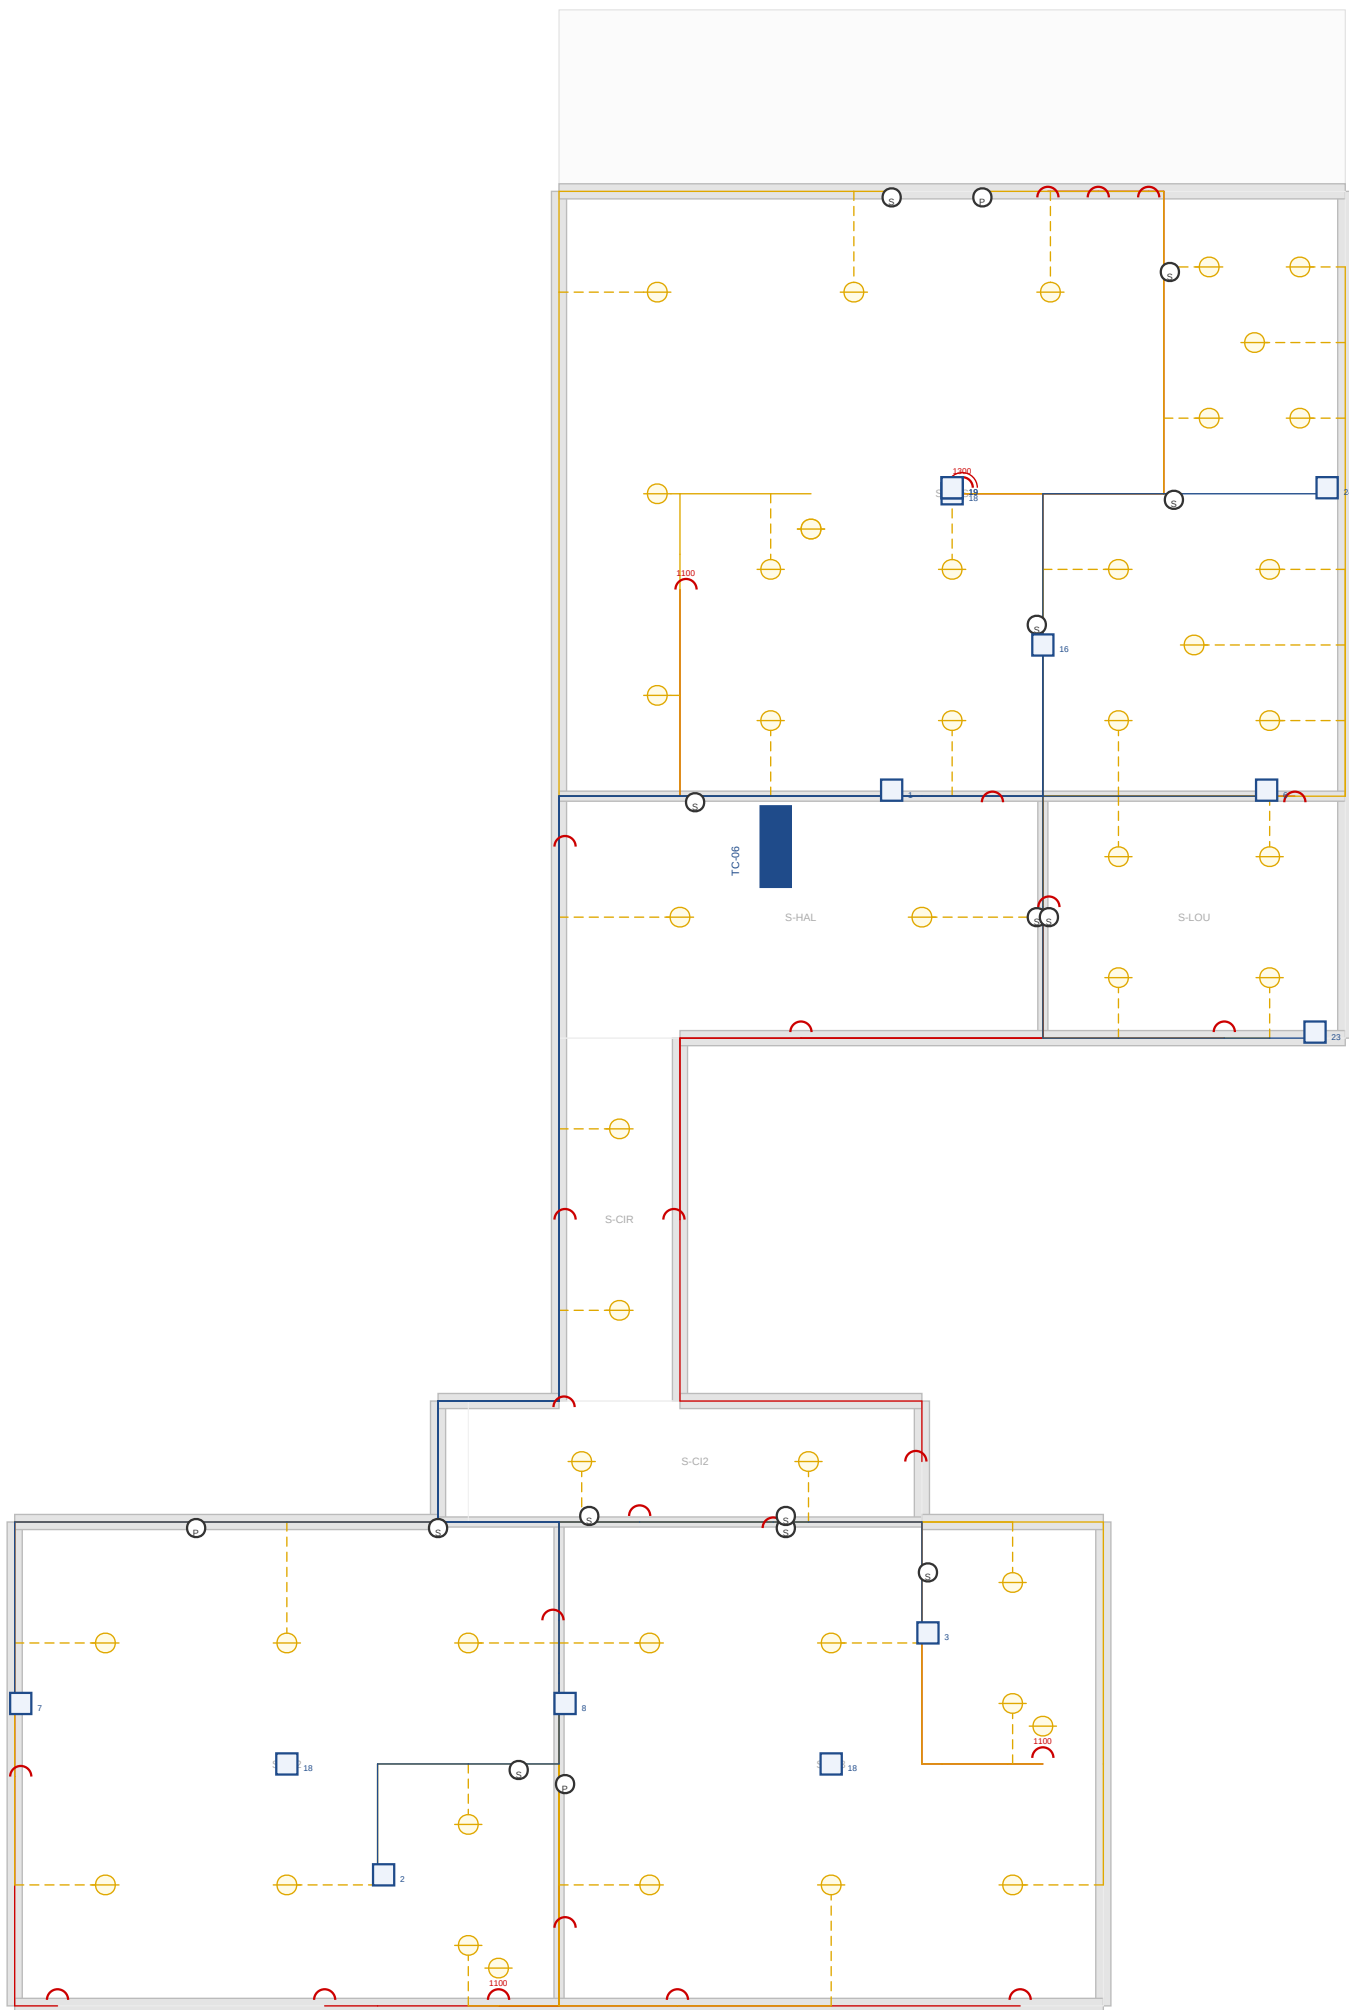


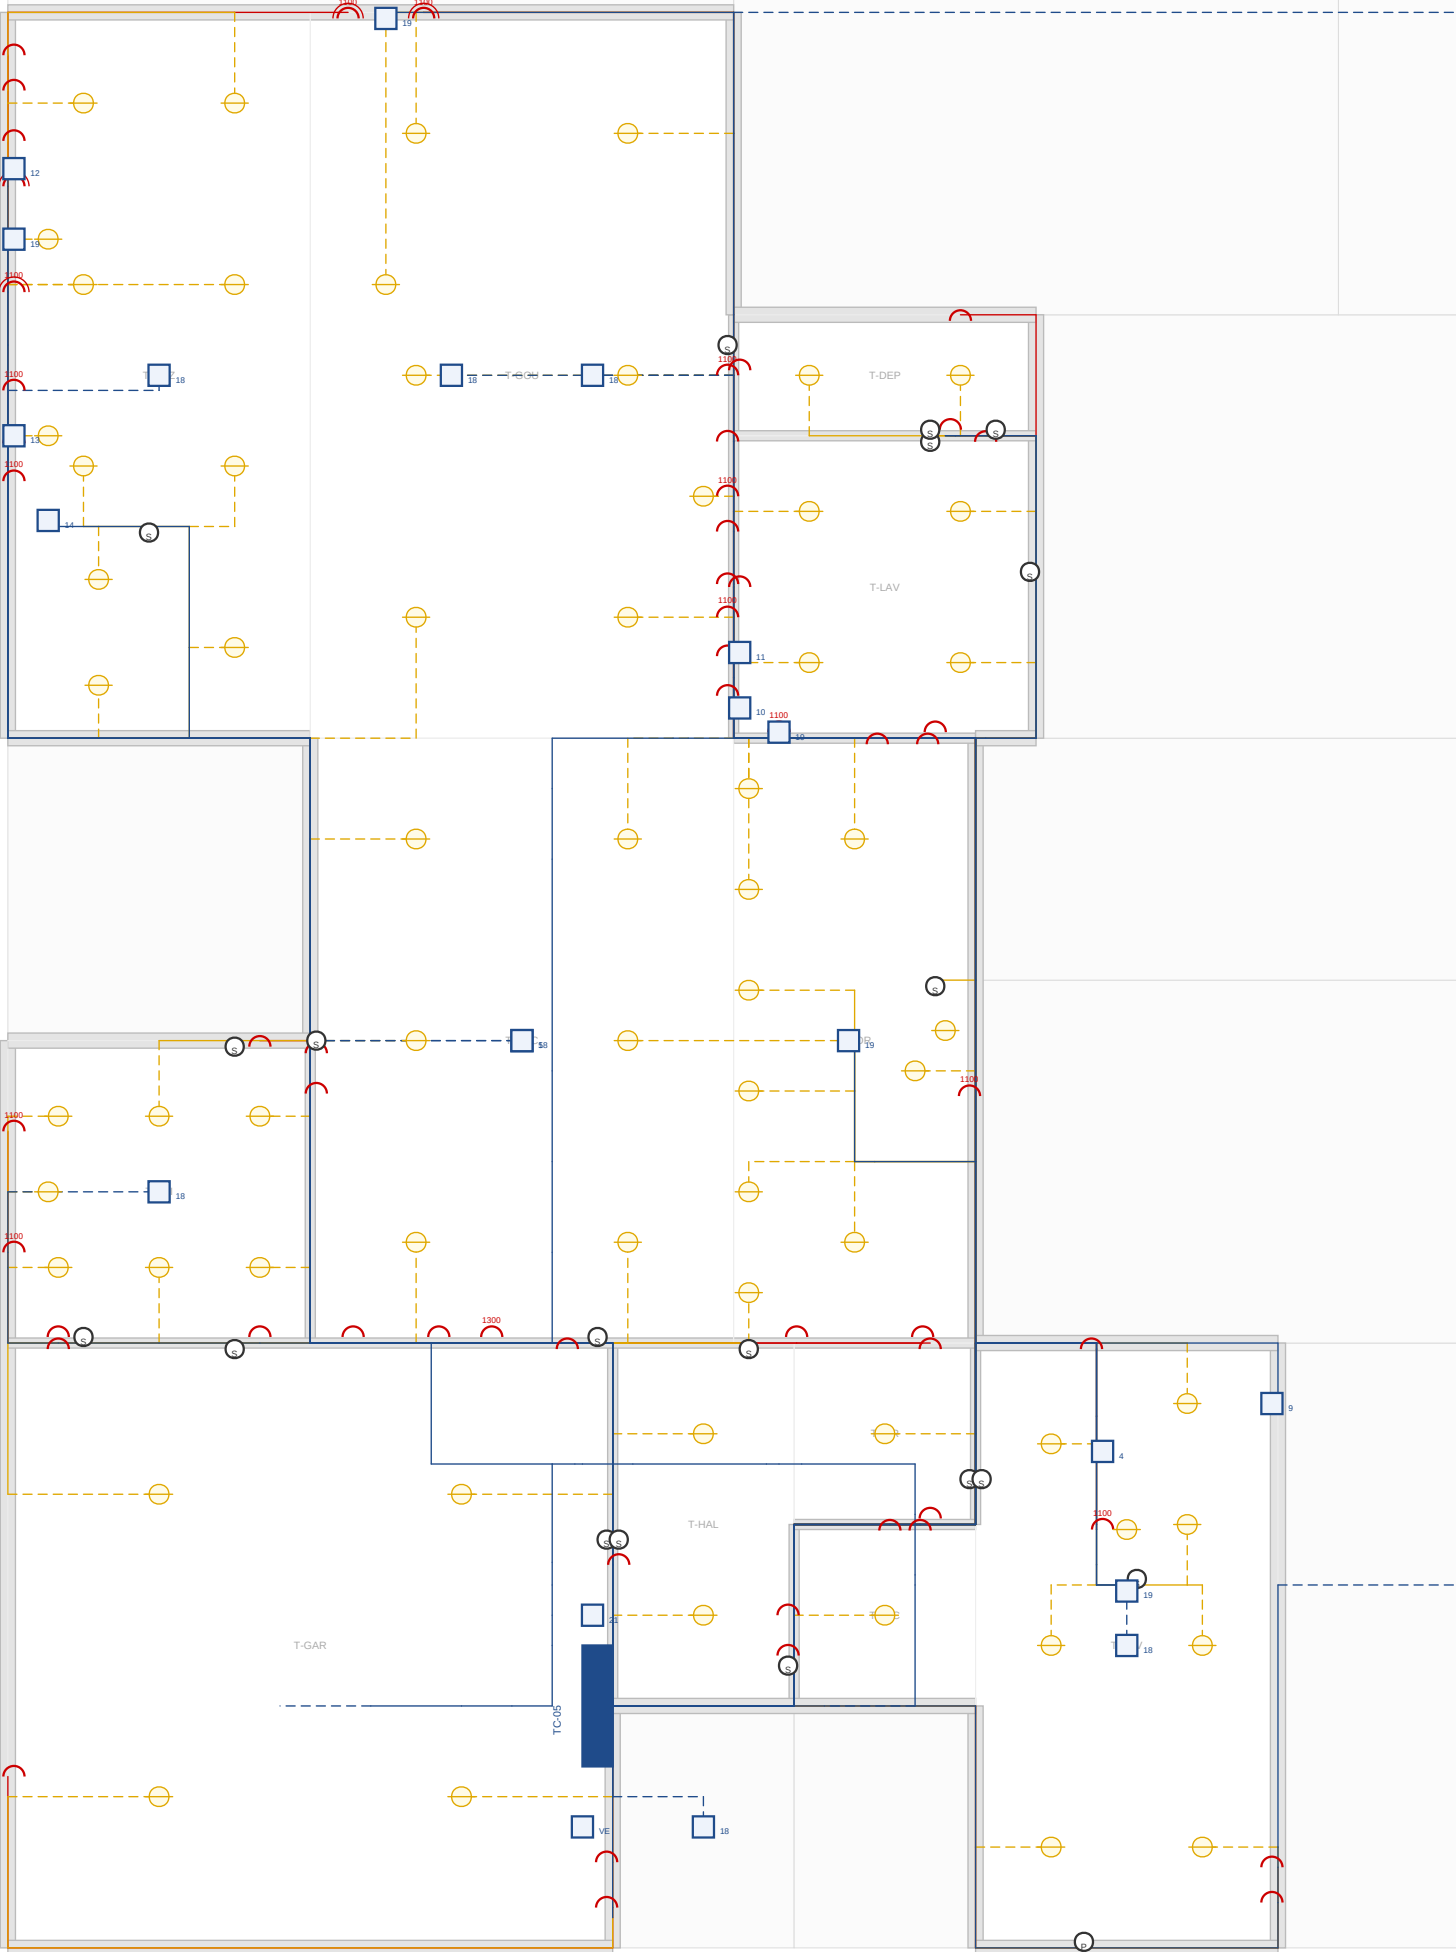

1 PONTOS E PERCURSOS — TERREO

ESCALA 1:75

2 PONTOS E PERCURSOS — SUPERIOR

ESCALA 1:75

CIRCUITOS: ARVORE REAL, PONTO MAIS LONGE, O QUE ERA MANHATTAN x 1.2, QUEDA E SECAO

CIRCUITO	QD	PYS	PAUL	ARVORE - M	LCORRGE - M	MANH - M	QUEDA - %	MMZ	MONC	CE PASS
S-01-C2	TC-06	4	5	150	163	135	0,23	1,5	37	2
S-01-C3	TC-06	2	2	11,3	9,3	11,0	0,13	1,5	18	2
S-01-HAL	TC-06	4	3	13,2	6,3	7,7	0,28	1,5	33	2
S-01-S-01	TC-06	5	3	18,1	9,3	13,3	0,27	1,5	33	2
S-01-S-02	TC-06	26	12	84,1	13,5	17,7	2,35	1,5	68	4
S-01-S-03	TC-06	11	12	49,3	20,7	24,7	1,37	1,5	68	3
S-01-S-04	TC-06	11	14	51,3	23,1	18,9	1,07	1,5	85	4
S-01-S-05	TC-06	1	2	5,9	5,0	5,07	0,07	1,5	7	1
S-01-T-COR	TC-06	2	4	9,2	6,7	13,2	0,17	1,5	18	2
S-01-T-COR	TC-06	11	12	51,5	20,1	18,4	1,15	1,5	67	3
S-01-T-COR	TC-06	11	13	54,0	27,4	30,2	1,86	1,5	72	3
S-01-S-06	TC-06	4	9	28,9	21,2	19,2	0,28	1,5	60	3
S-01-T-GAR	TC-06	6	9	30,5	14,1	14,4	1,06	1,5	50	3
S-01-T-GAR	TC-06	9	14	63,5	30,4	26,6	1,46	1,5	108	4
S-01-T-HAL	TC-06	5	4	12,9	9,3	10,1	0,15	1,5	18	2
S-01-T-LAV	TC-06	6	16	30,9	20,1	20,7	0,67	1,5	60	3
S-01-T-LAV	TC-06	9	15	32,1	18,5	18,0	0,28	1,5	66	3
S-01-T-REV	TC-06	11	10	36,9	13,9	16,8	0,79	1,5	55	3
S-01-T-REV	TC-06	6	13	47,5	20,1	18,0	1,60	1,5	70	3
S-01-T-REV	TC-06	1	9	14,9	21,2	19,2	0,28	1,5	60	3
S-01-T-REV	TC-06	1	9	16,2	16,2	23,7	1,25	2,5	43	2
S-01-T-REV	TC-06	1	8	16,8	16,8	23,7	1,43	2,5	46	2
S-01-T-REV	TC-06	1	8	22,4	22,4	30,2	2,07	2,5	53	2
S-01-T-REV	TC-06	1	8	16,8	16,8	23,7	1,43	2,5	46	2
S-01-T-REV	TC-06	1	7	17,9	17,9	30,2	2,28	2,5	44	2
S-01-T-REV	TC-06	1	4	18,2	18,2	23,7	0,28	2,5	27	1
S-01-T-REV	TC-06	1	2	9,2	9,2	20,5	0,13	2,5	9	1
S-01-T-REV	TC-06	1	9	16,4	16,4	20,5	0,78	2,5	46	2
S-01-T-REV	TC-06	10	10	30,9	20,1	20,5	1,06	2,5	59	7
S-01-T-REV	TC-06	7	26	64,9	27,0	18,0	1,04	2,5	152	5
S-01-T-REV	TC-06	1	8	17,9	17,9	24,7	1,42	4	42	2

(continuação)

CIRCUITO	QD	PYS	PAUL	ARVORE - M	LCORRGE - M	MANH - M	QUEDA - %	MMZ	MONC	CE PASS
S-01-T-REV	TC-06	1	1	4,7	4,7	14,4	0,07	2,5	6	1
S-01-T-REV	TC-06	1	1	2,0	2,0	14,4	0,05	2,5	2	1
S-01-T-REV	TC-06	1	3	8,3	13,3	13,3	0,13	2,5	38	1
S-01-T-REV	TC-06	1	3	9,3	9,3	13,3	0,17	2,5	38	1
S-01-T-REV	TC-06	1	6	17,2	17,2	18,9	1,38	4	62	2
S-01-T-REV	TC-06	1	6	18,2	18,2	18,9	0,82	4	26	1
S-01-T-REV	TC-06	1	3	12,9	12,9	18,9	0,84	2,5	28	1
S-01-T-REV	TC-06	1	1	5,4	5,4	18,9	0,17	1,5	11	1
S-01-T-REV	TC-06	1	6	17,3	17,3	18,7	0,68	2,5	40	2
S-01-T-REV	TC-06	1	6	14,3	14,3	18,9	0,57	2,5	34	1
S-01-T-REV	TC-06	1	7	16,6	16,6	18,9	0,48	2,5	27	1
S-01-T-REV	TC-06	1	1	5,3	5,3	18,9	0,10	8	2	1
S-01-T-REV	TC-06	3	10	35,2	16,4	13,5	0,42	2,5	67	3
S-01-T-REV	TC-06	2	5	18,1	11,6	11,0	0,26	2,5	40	3
S-01-T-REV	TC-06	3	4	13,9	8,8	7,7	0,22	2,5	26	2
S-01-T-REV	TC-06	3	9	18,9	8,8	10,0	0,07	2,5	20	2
S-01-T-REV	TC-06	5	7	18,9	12,5	17,7	0,62	2,5	37	2
S-01-T-REV	TC-06	5	13	33,9	21,1	24,7	0,86	2,5	70	3
S-01-T-REV	TC-06	5	10	34,9	22,5	18,9	0,96	2,5	76	3
S-01-T-REV	TC-06	1	1	5,9	5,9	18,9	0,10	8	2	1
S-01-T-REV	TC-06	2	9	16,9	7,9	12,7	0,13	2,5	30	2
S-01-T-REV	TC-06	5	9	26,4	16,3	18,4	2,01	2,5	50	3
S-01-T-REV	TC-06	5	8	26,4	23,5	30,2	2,14	4	57	3
S-01-T-REV	TC-06	5	10	26,4	26,4	30,2	2,13	2,5	70	3
S-01-T-REV	TC-06	5	9	26,9	11,3	14,4	0,48	2,5	47	3
S-01-T-REV	TC-06	10	18	59,3	26,5	26,6	1,82	4	138	5
S-01-T-REV	TC-06	3	3	7,5	3,9	10,1	0,10	2,5	10	2
S-01-T-REV	TC-06	4	11	26,9	14,1	10,7	2,06	2,5	40	3
S-01-T-REV	TC-06	5	9	23,4	11,3	18,0	0,15	2,5	30	3
S-01-T-REV	TC-06	4	9	22,1	10,9	15,8	0,37	2,5	46	3
S-01-T-REV	TC-06	5	3	14,2	10,6	18,0	0,48	2,5	20	2

PONTOS POR AMBIENTE

AMB	PYSOM	DUPLO	ALTAS	INT	LAM	TUE
T-COR	10	0	0	2	4	0
T-HAL	33	0	0	2	0	0
T-ALC	22	0	0	0	1	0
T-COR	22	0	0	1	1	0
T-REV	44	0	1	3	9	4
T-COR	3	0	2	0	7	1
T-SOC	95	0	1	2	6	2
T-COR	65	0	1	1	10	1
T-COR	800	2	4	1	11	6
T-GOU	1012	2	5	1	9	3
T-LAV	44	0	1	2	4	5
T-SEP	33	0	0	2	4	0
S-REV	65	0	1	3	6	3
S-REV	95	0	1	3	6	3
S-COR	22	0	0	0	2	0
S-COR	33	0	0	0	2	0
S-HAL	33	0	0	2	2	0
S-COR	33	0	0	1	4	1
S-MAS	1	1	2	3	21	7

FIXADORES E CAIXAS (H)

ITEM	QTD	UN
lucha passo 25 mm (montagem universal)	2301	un
clip de eletrificação no montante (a cada 1.200 mm)	1823	un
caixa 402	188	un
caixa de passagem	147	un
abrevidado de eletrificação no formidamento (a cada 1.200 m)	182	un
caixa 444 octagonal	111	un
caixa 444	39	un
abrevidado PS42 eletrificado (m)	15,3	m

CONFERENCIAS DESTA PRANCHA

O QUE	COMO	
todo terminal provido com água	87 terminais em 82 pontos (5 duplos) em 20 ambientes	OK
terminal e interruptor todos providos	87 terminais em 82 pontos (5 duplos) em 20 ambientes	OK
todo terminal dentro de 60 cm de uma parede	87 terminais em 82 pontos (5 duplos) em 20 ambientes	OK
terminal	87 terminais em 82 pontos (5 duplos) em 20 ambientes	OK
terminal provido na zona 1 do bloco (NBR 541)	4 boxes contínuos, máxima 600 mm	OK
terminal de terminal alta	1000 a 1200 mm	OK
todo ambiente com porta bem interruptor	17 ambientes	OK
terminal no ponto de entrada de todo ambiente	4 ambientes	OK
todo TUE com contatado	30 pontos de 24 cargas	OK
todo ponto elétrico adequado pelo grau	280 pontos	OK
qualidade de terminais com o parâmetro real	máximo 1,50 % (máx 4,5 kg)	OK
tudo elétrico e hidráulico alinhado	2000 mm entre eixos (máximo um diâmetro)	OK
caixa de passagem onde o nome pode	147 caixas (21 m de 3 curvas, NBR 5403 8.2.1.1)	OK

NOTAS

- 82 pontos de terminal (87 terminais, 5 duplos, 12 de bancada a 1.200 mm), 38 interruptores (1 parafuso), 111 terminais, 38 pontos de TUE — todos com x, y e z e parede (hoteleiros).
- Distância CENTRO de parede a 1400 mm, ponto final de serviço dos montantes, sobre os furos para terminal e ventilador, sem interferir a 400 mm para terminal e parede, 1400 mm de distância em 82 pontos, ponto mais longe TUE 17 a 38 a m de quadro.
- Problemas (1): Bucha passo 25 em cada um dos 2302 montantes dimensionados, clip a cada 1200 mm, abridor a cada 1000 mm no furo, caixa 402 em terminal e interruptor, 444 em terminal e TUE, caixa de passagem a cada 15 m (NBR 5403 8.2.1.1).
- Letras: pontos luminosos, terminal TUE, luz TUE, interruptor no furo, interruptor ou terminal. Cada das tomadas ao quadro de 300 mm.

PROJETO PORTO REAL

RESIDENCIA UNIFAMILIAR (MANSÃO - AM) - 5000 TATAMÁ-PI

PROJETO ARQUITETONICO

ELETRICA: PONTOS, PERCURSOS E FIXADORES

BASE GEOMETRICA

Uma Consolidação

em R2D (previsão)

UNIDADE MESTRE: AM

ESCALA

1:75

FORMATO A1

MALHA 600/600/600

EMISSÃO

ESTUDO PRELIMINAR RES

NÃO LIBERADO PARA OBRA

SEM ART / INT

PRANCHA

73

06-78 REV 02