

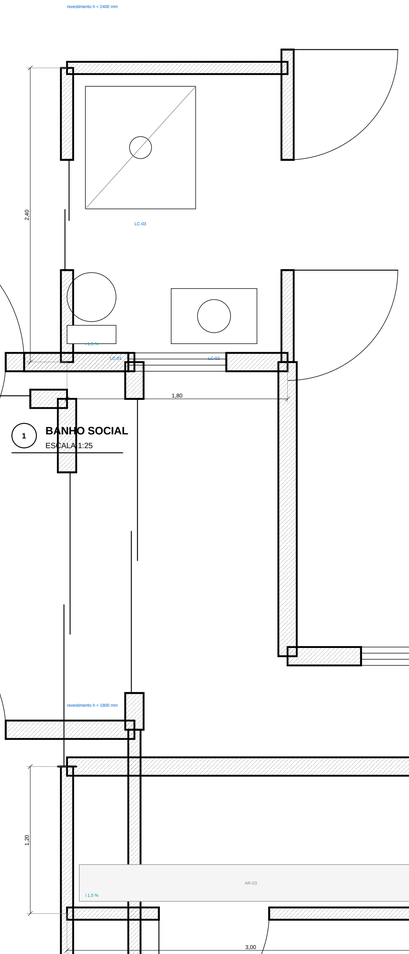



1 **BANHO SOCIAL**
ESCALA 1:25

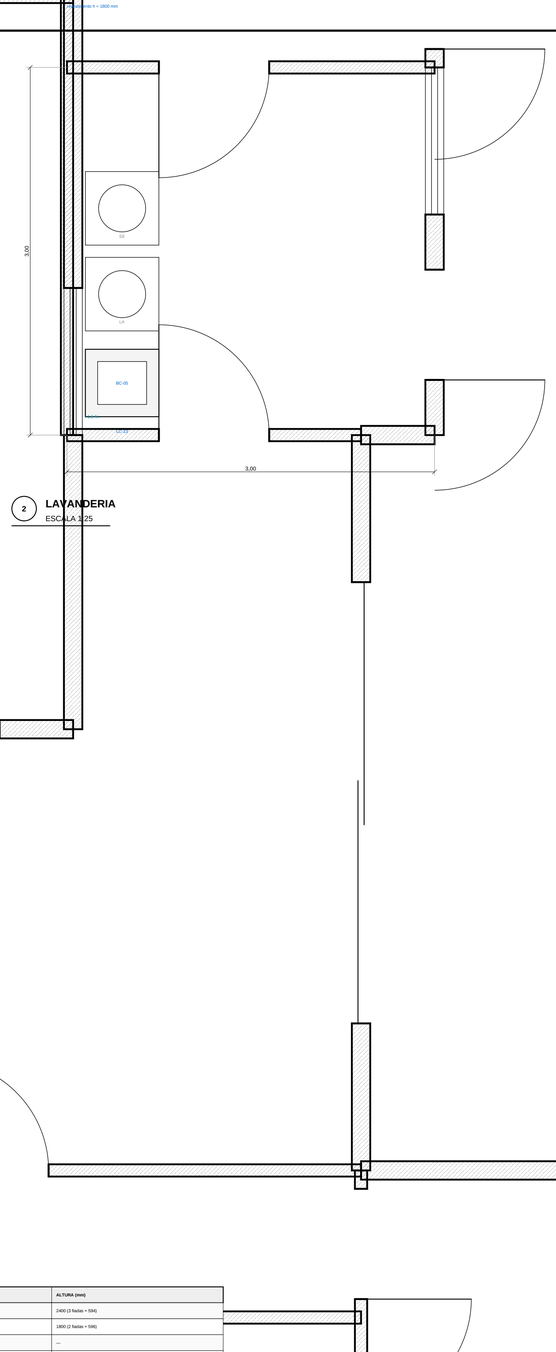

2 **LAVANDERIA**
ESCALA 1:25

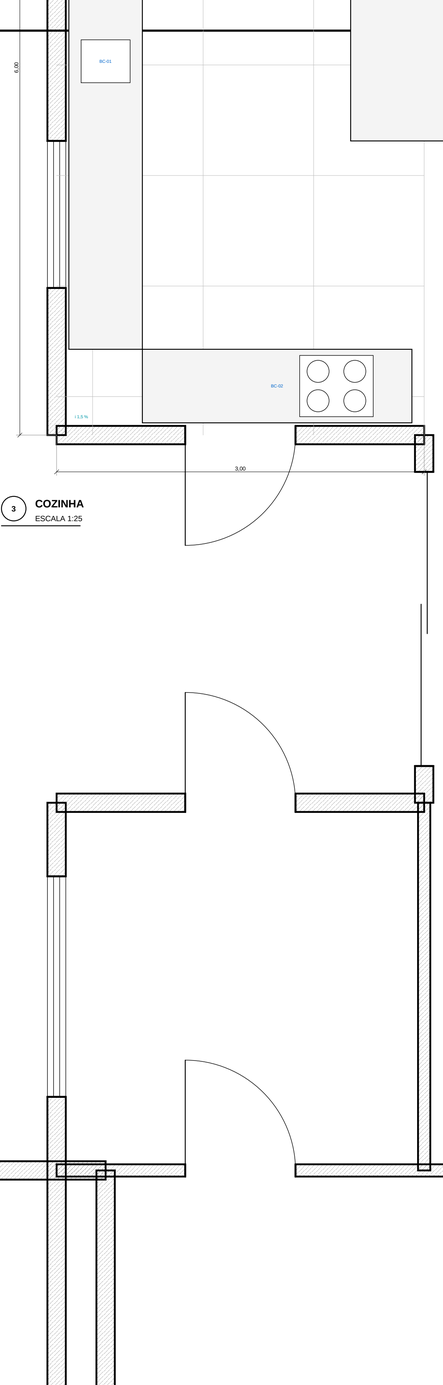

3 **COZINHA**
ESCALA 1:25

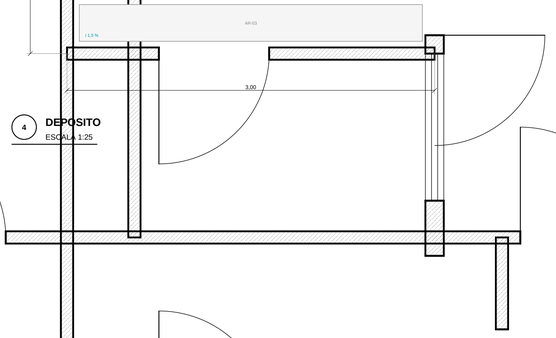

4 **DEPOSITO**
ESCALA 1:25

PAGINACAO VERIFICADA — PECAS INTEIRAS + RECORTE EM CADA PONTA

AMB	AMBIENTE	ZONA	PECA	EIXO X	EIXO Y	ALTURA (mm)
T-BWC	BANHO SOCIAL	ZP-4	parede	5 = 0/288	3 = 0/592	2400 (3 faixas + 594)
T-LAV	LAVANDERIA	ZP-5	parede	9 = 0/280	4 = 0/590	1900 (2 faixas + 596)
T-COZ	COZINHA	ZP-1	piso	3 = 292/0	6 = 312/272	—
T-DEP	DEPOSITO	ZP-5	parede	9 = 0/280	1 = 0/596	1800 (2 faixas + 596)

NOTAS

- Paginacao de piso em linha fria: a linha vem da ZONA de paginacao, nao do canto do ambiente.
- Peca de piso porcelanato retificado 300 x 900; parede ceramico retificado 300 x 600; junta 2 mm.
- Caimento de 1,5 % para o ralo em toda area molhada; soleira elevada 15 mm nos boxes.
- Impermeabilizacao: manta liquida em 2 demaos, subindo 300 mm na parede e 1.800 mm nos boxes.

PROJETO PORTO REAL

RESIDENCIA UNIFAMILIAR | MANAUS - AM | SUB TARUMA (H)

PROJETO ARQUITETONICO

AMPLIACOES DE AREA MOLHADA — TERREO

BASE GEOMETRICA	ESCALA	EMISSAO	PRANCHA
Lista Consolidada pos-R32 (prevalece)	1:25 FORMATO A1 MALHA 600/300/150	ESTUDO PRELIMINAR NAO LIBERADO PARA OBRA SEM ART / RRT	22 de 33

UNIDADE MESTRE HR