


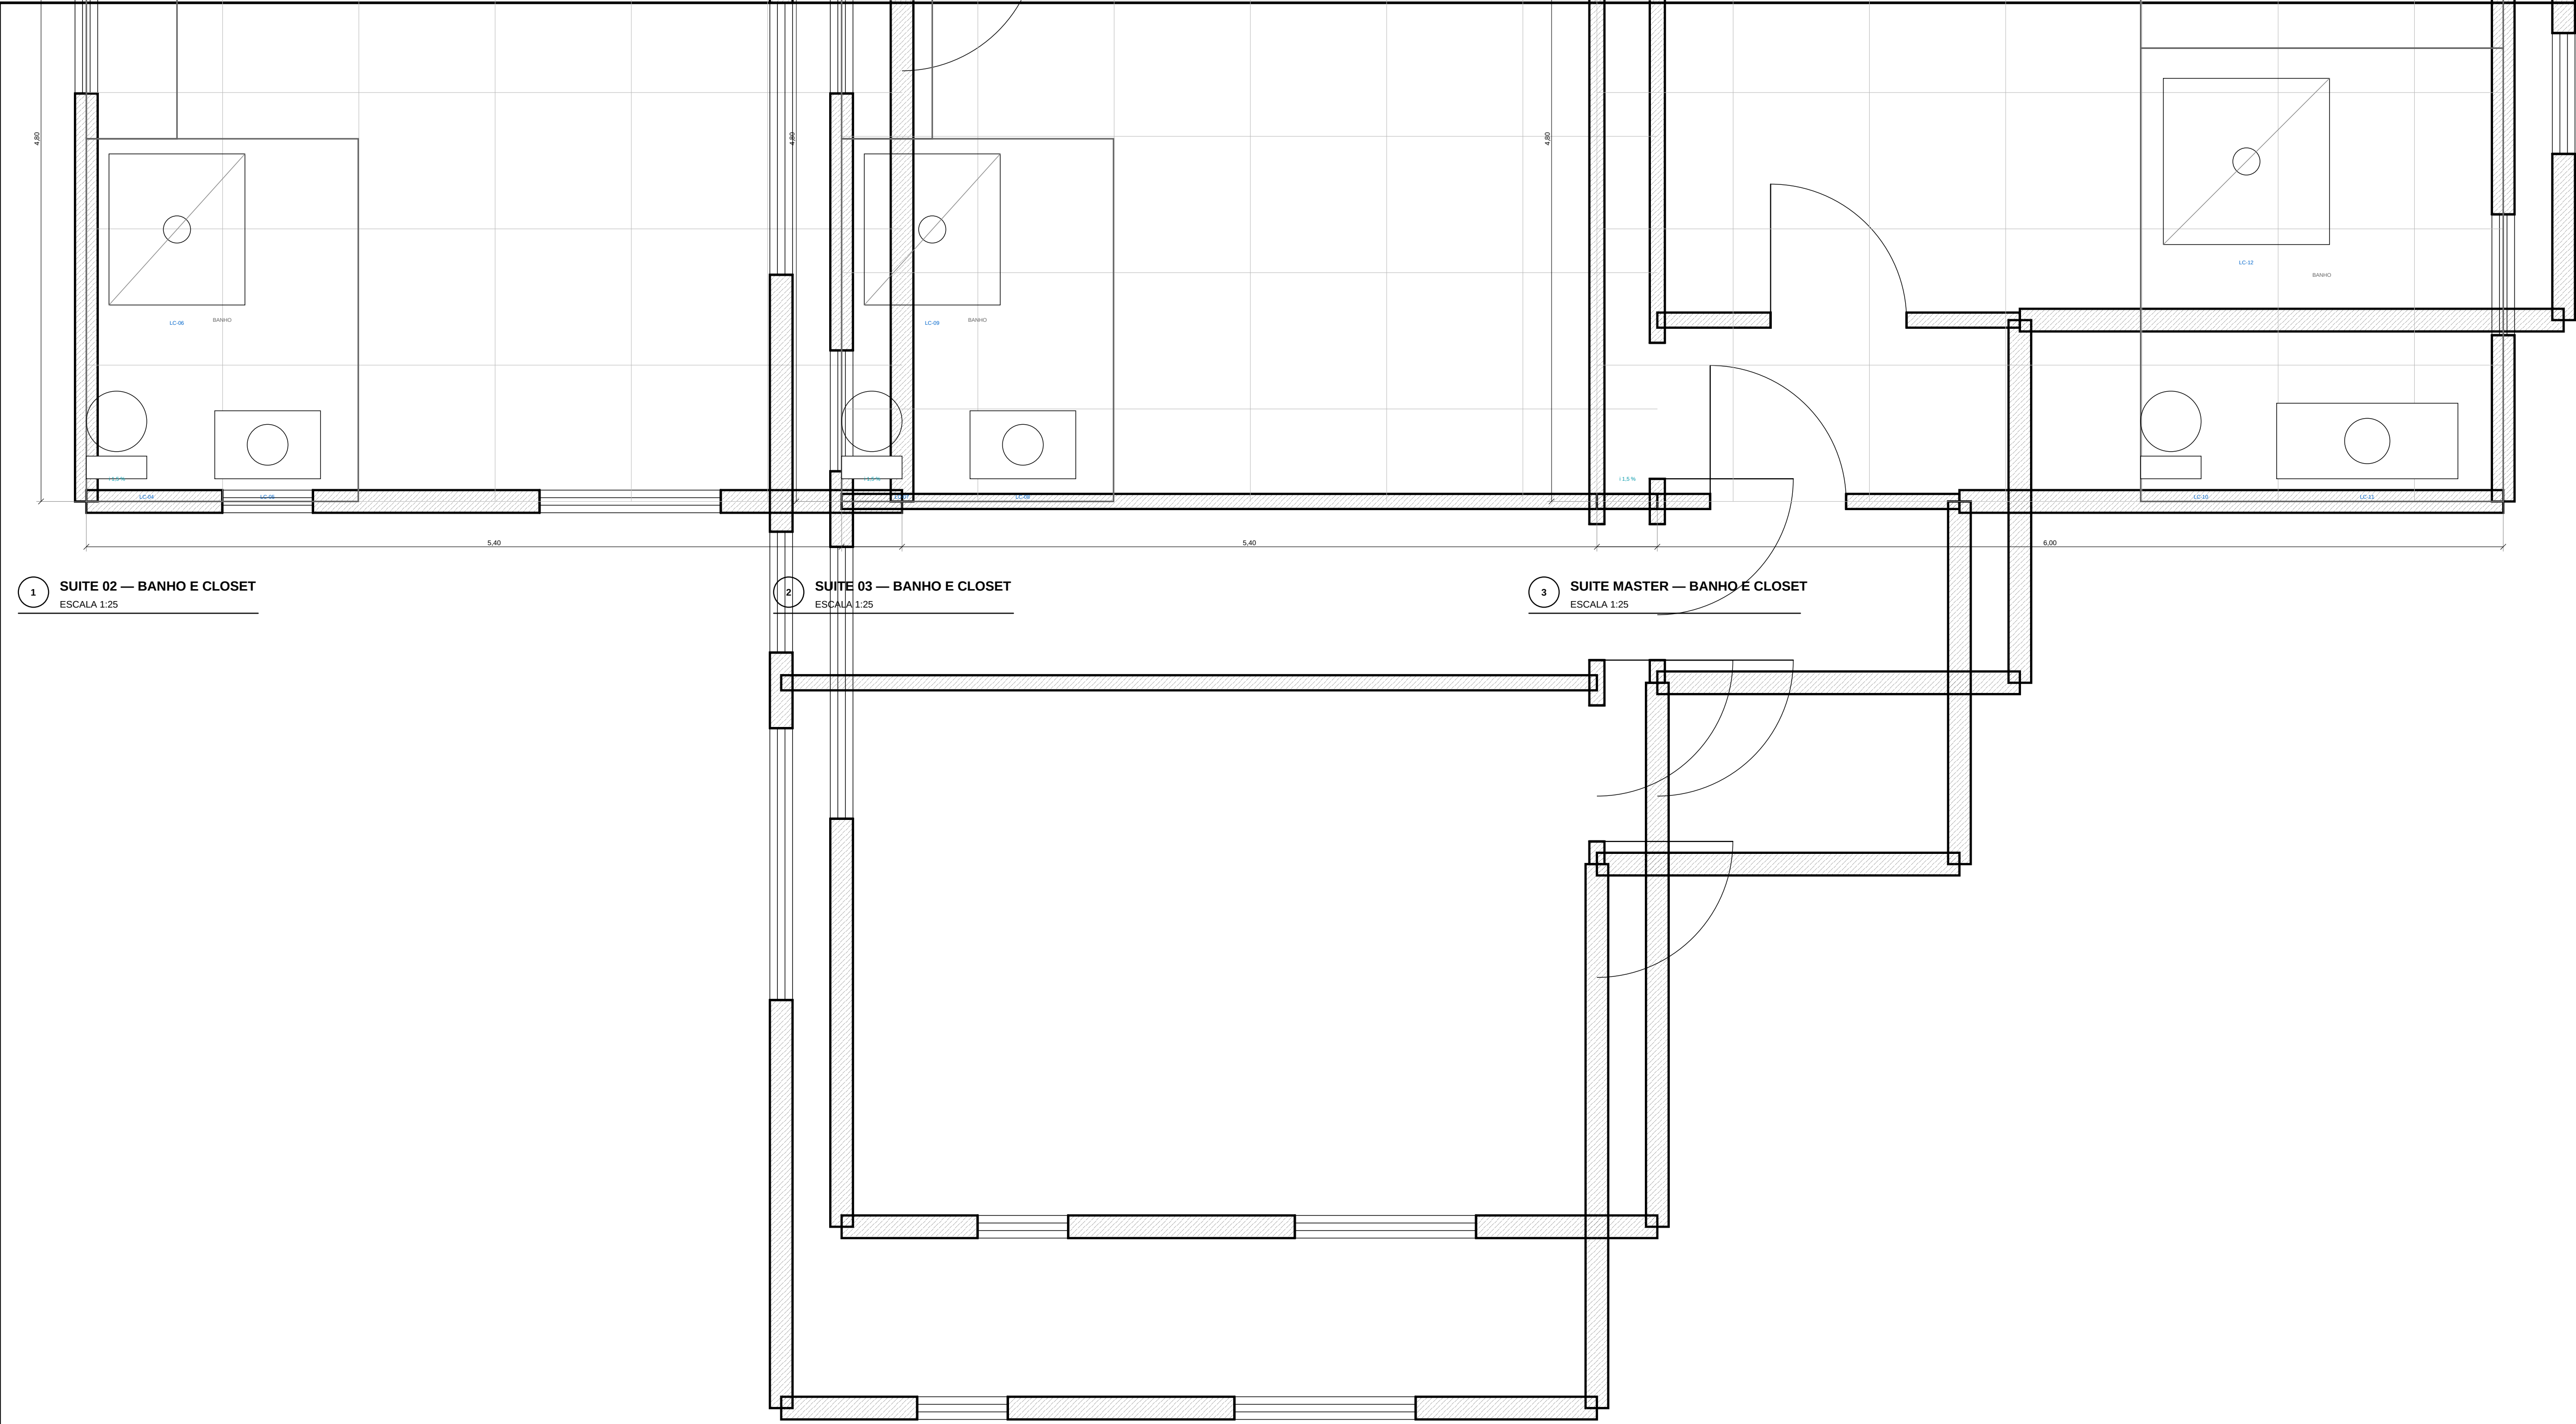

1 SUITE 02 — BANHO E CLOSET
ESCALA 1:25

2 SUITE 03 — BANHO E CLOSET
ESCALA 1:25

3 SUITE MASTER — BANHO E CLOSET
ESCALA 1:25

PAGINACAO VERIFICADA — PECAS INTEIRAS + RECORTE EM CADA PONTA

AMB	AMBIENTE	ZONA	PEÇA	EXTO X	EXTO Y	ALTURA (mm)
S-002	SUITE 02 — BANHO E CLOSET	ZF-3	gnd	3 + 0000	5 + 0000	—
S-003	SUITE 03 — BANHO E CLOSET	ZF-3	gnd	5 + 0000	4 + 0000	—
S-005	SUITE MASTER — BANHO E CLO	ZF-2	gnd	6 + 0000	5 + 0000	—

- NOTAS
- * Pignificas de piso em linha fina, a malha vem da ZONA de pignificas, não do canto do ambiente.
 - * Peca de piso porcelanato retificado 300 x 300, parede ceramico retificado 300 x 600, porta 2 mm.
 - * Camaroto de 1,5 % para o lado em toda area molhada, solteira elevada 15 mm nos bicos.
 - * Representacao: manta lquida em 2 demoes, tubado 300 mm na parede e 1.800 mm nos bicos.

PROJETO PORTO REAL

RESIDENCIA UNIFAMILIAR (MARIAUS - AM) | SOUS TATIANA-PS

PROJETO ARQUITETONICO

AMPLIACOES DE AREA MOLHADA — SUPERIOR

BASE GEOMETRICA Linha Consolidada Projeto (previsão) UNIDADE MESTRE: mm	ESCALA 1:25 FORMATO A1 MILHA 600/500/300	EMISSAO ESTUDO PRELIMINAR TWO LIBERADO PARA OBRA SEM ART / RNT	PROJECIA 23 06-23
--	---	---	-------------------------