
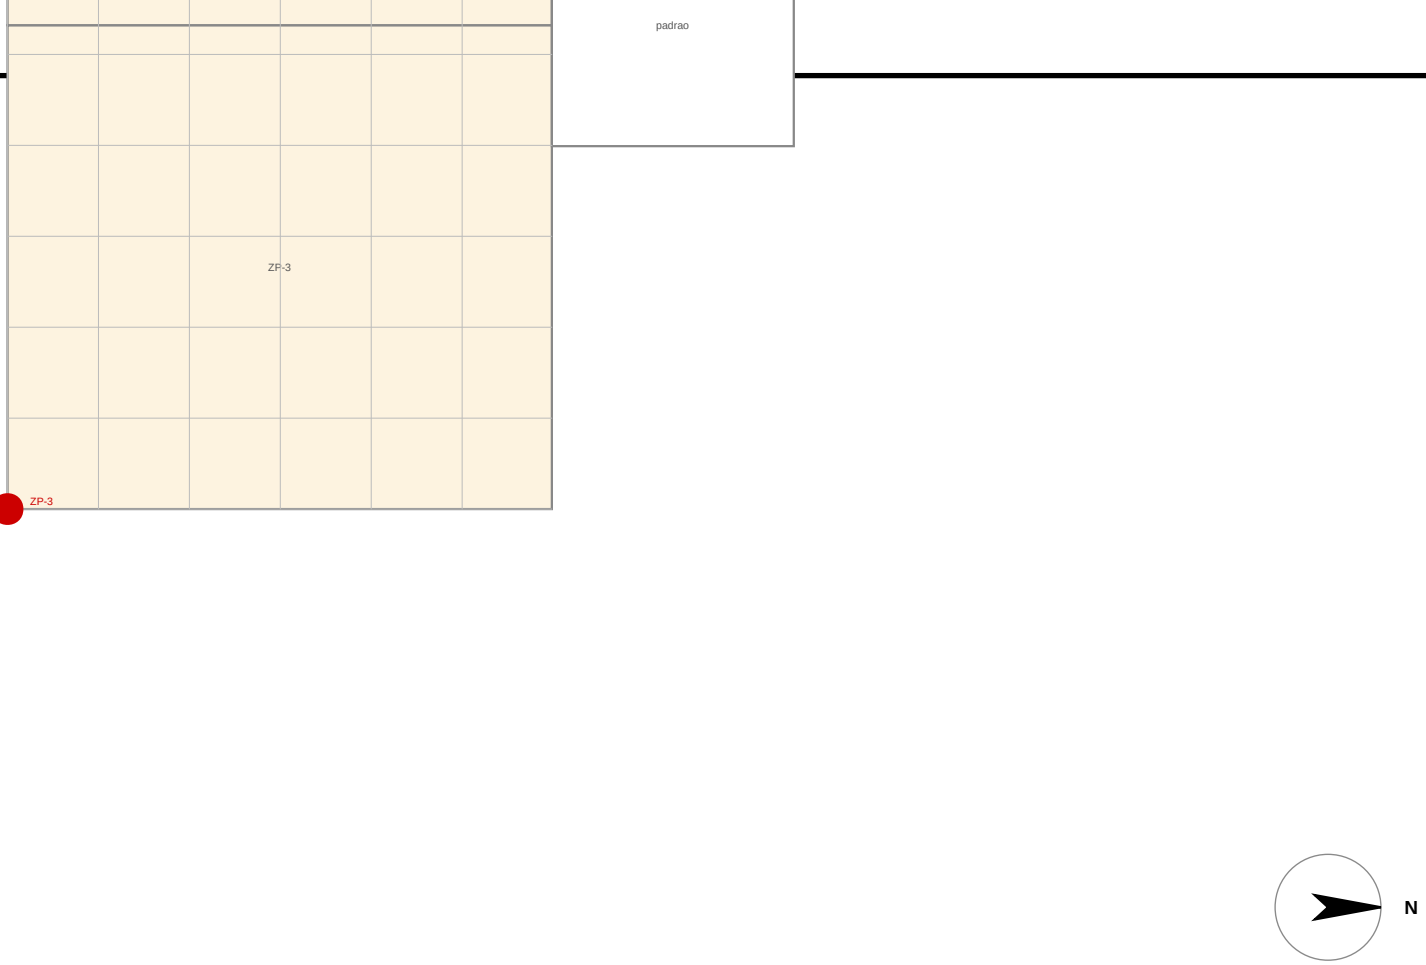


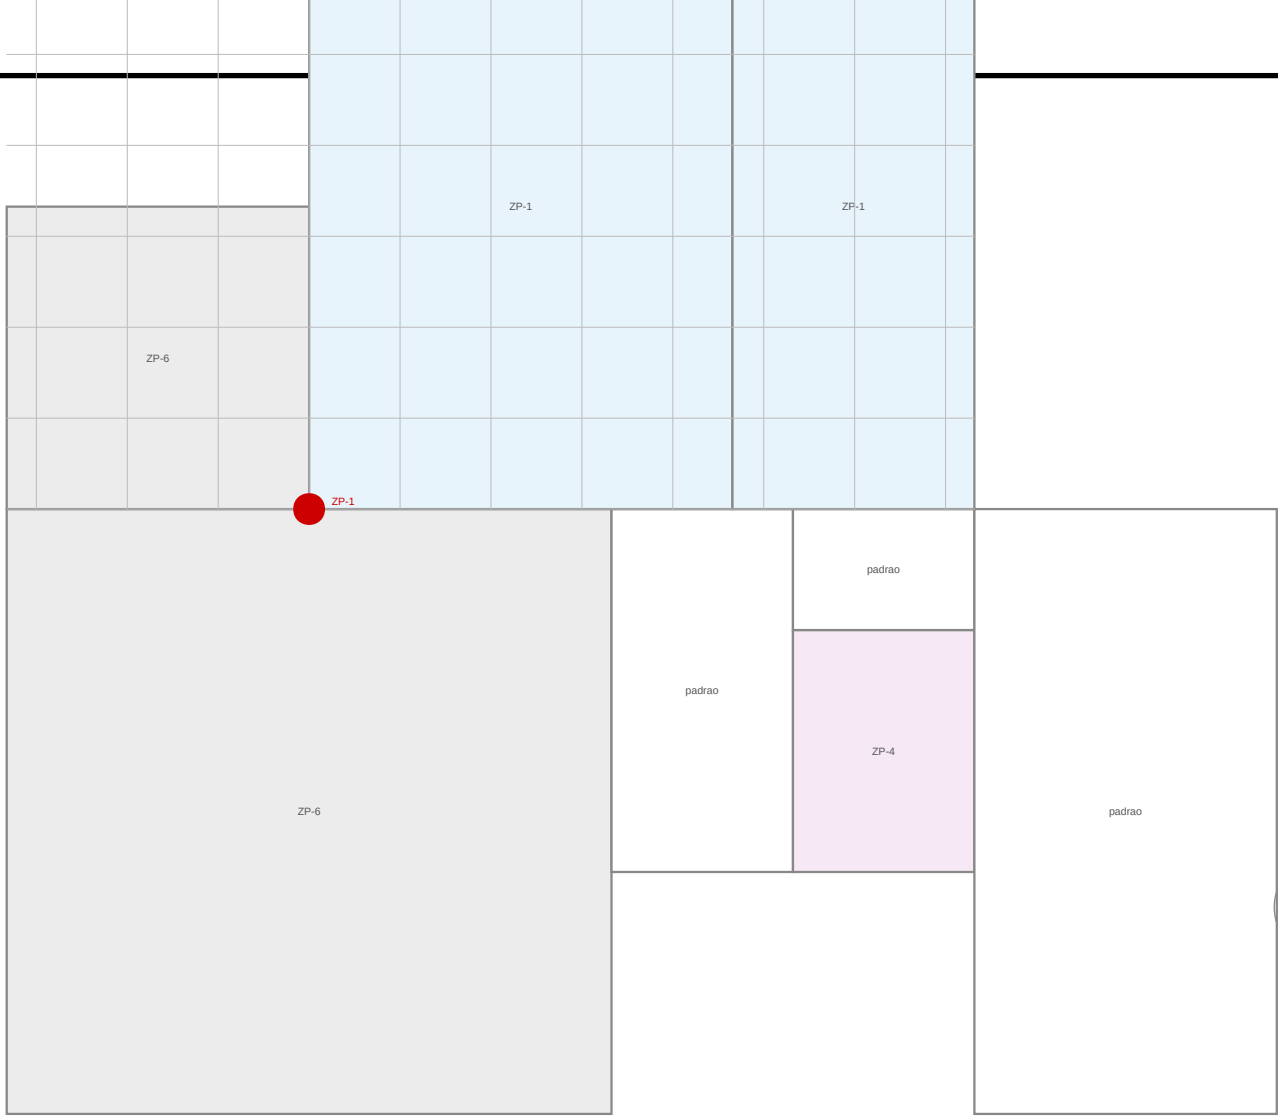

1 PAGINACAO — TERREO
ESCALA 1:75

2 PAGINACAO — SUPERIOR
ESCALA 1:75

ZONAS DE PAGINACAO

ZONA	PEÇA	ORDEM	AMBIENTES	PEÇA ESPECIFICADA	PONTO RECORTE	COMENTÁRIO
ZP-1	plata	(5400, 12000)	T-001, T-002, T-003, T-004, T-005	perforado 900 x 900	272	plata social interna em uma malha, origem no eixo da porta do 1º
ZP-2	plata	(7000, 10000)	S-001, S-002	perforado 900 x 900	288	origem no eixo da porta do 1º
ZP-3	plata	(5400, 12000)	S-003, S-004	perforado 900 x 900	288	salto 12 e 13 na mesma malha, a parede entre elas é deslizada
ZP-4	plata	(5400, 12000)	T-006, T-007	perforado 900 x 900	288	plata social interna em uma malha, origem no eixo da porta do 1º
ZP-5	plata	(5400, 12000)	T-008, T-009, T-010	perforado 900 x 900	288	plata social interna em uma malha, origem no eixo da porta do 1º
ZP-6	plata	(5400, 12000)	T-011, T-012	perforado 900 x 900	288	plata social interna em uma malha, origem no eixo da porta do 1º

NOTAS

- * Paginar no projeto e decidir onde fica o corte. Não paginar e deixar o corte aparecer no lugar mais visível.
- * Ambientes integrados receberão uma malha, a porta diferenciada no meio da sala não tem parede para a diferença.
- * Recorte interno sobre 20% da placa, além de 20% o recorte interno e a reprodução.

PROJETO PORTO REAL

RESIDENCIA UNIFAMILIAR (MANSÃO - AM) | SUEZ TATIANA-PS

PROJETO ARQUITETONICO

PAGINACAO DE PISO E ZONAS DE REVESTIMENTO

BASE GEOMETRICA Linha Consolidada PISO (PISO) (previsão) UNIDADE: METRO: MM	ESCALA 1:75 FORMATO: A1 MILHA: 600/600/600	EXIBICAO ESTUDO PRELIMINAR Linha Consolidada PARA OBRAS SEM ART / INT	PROJETO 24 06/23
--	---	--	------------------------