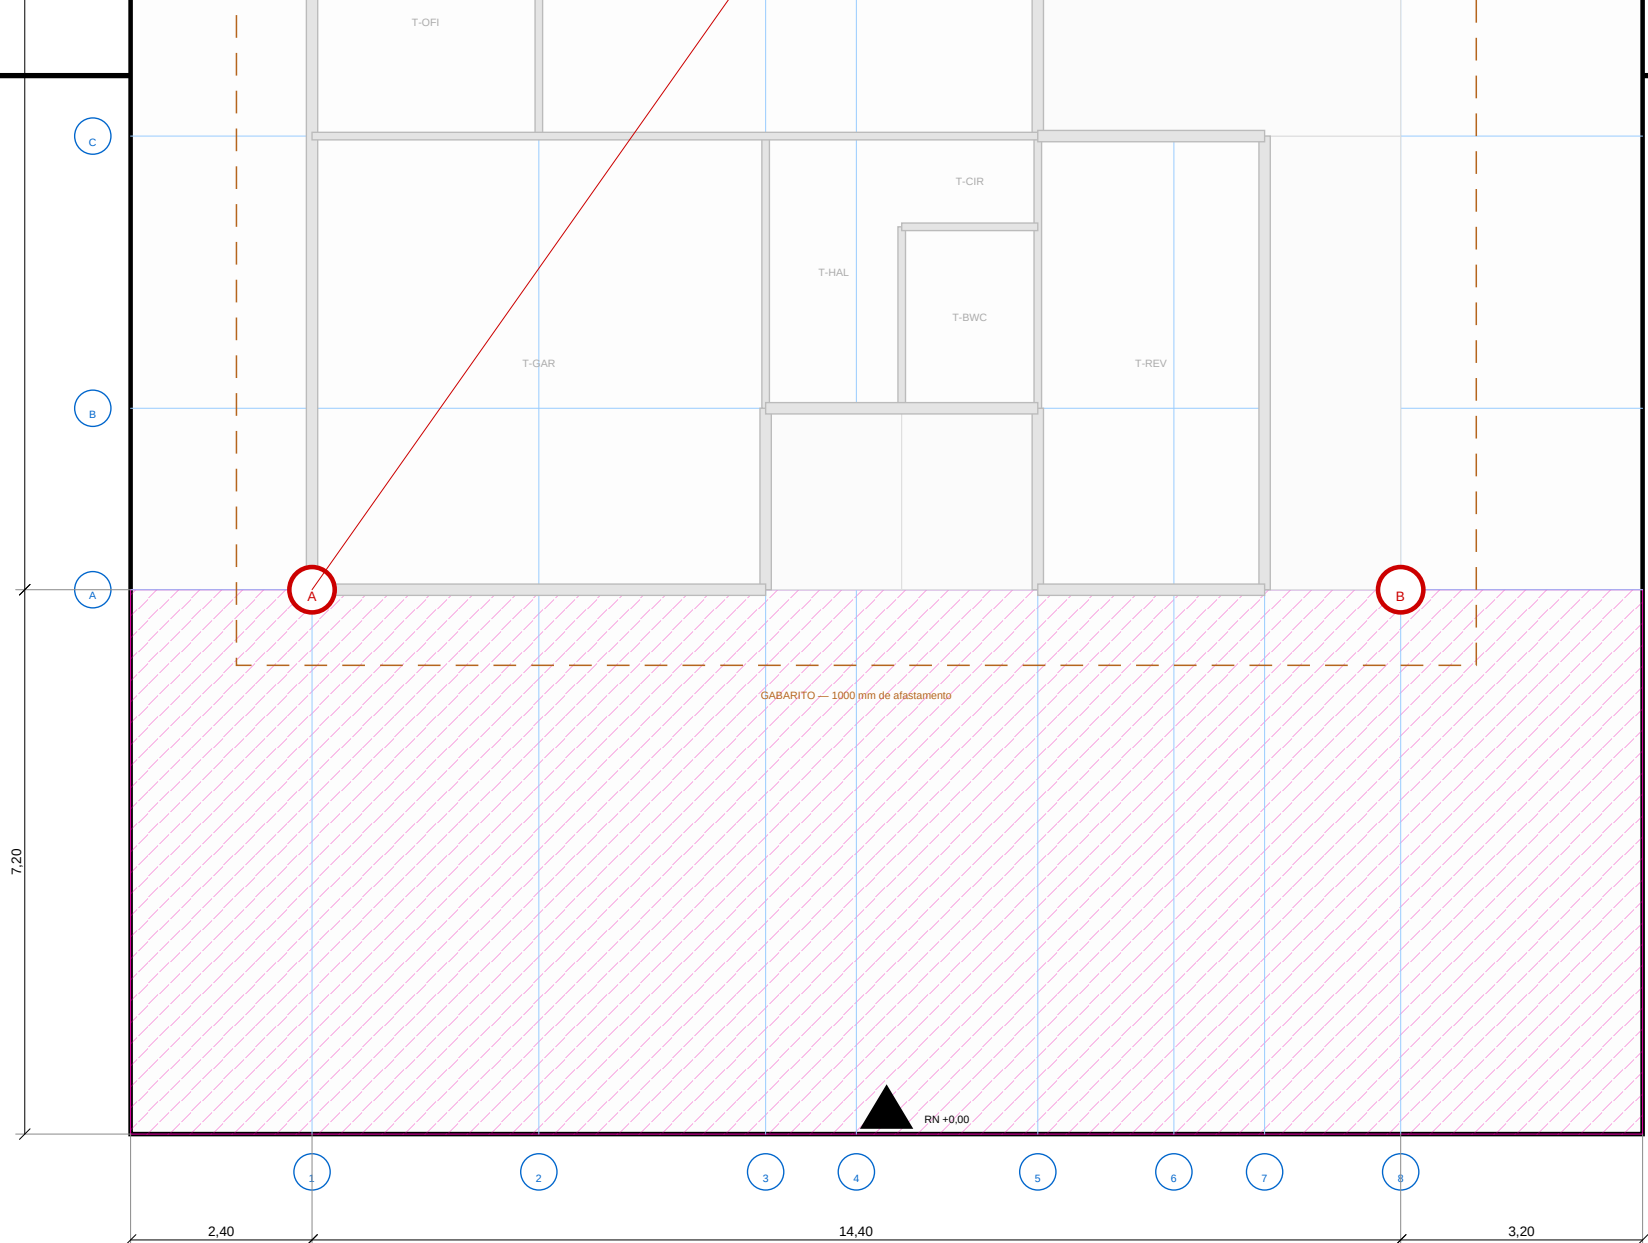


#### COORDENADAS DOS CANTOS (mm)

| CANTO | X     | Y     | DISSA-SIA | DISSA-NORTE | TESTADA | FORNO | DIAGONAL |
|-------|-------|-------|-----------|-------------|---------|-------|----------|
| A     | 2400  | 7200  | 2400      | 17600       | 7200    | 32800 | 24870,4  |
| B     | 16800 | 7200  | 16800     | 3200        | 7200    | 32800 | 24870,4  |
| C     | 16800 | 27600 | 16800     | 3200        | 27600   | 12400 | 24870,4  |
| D     | 2400  | 27600 | 2400      | 17600       | 27600   | 12400 | 24870,4  |

#### PROCEDIMENTO DE LOCAÇÃO

| # | PARSO                                                                    | CRITÉRIO DE ACRTE                                     |
|---|--------------------------------------------------------------------------|-------------------------------------------------------|
| 1 | Conferir as dimensões com a malha e o material de base                   | divergência acima de 10 mm interromper a locação      |
| 2 | Instalar o PNA sobre o concreto 100 x 200 x 100 mm, fora da área de obra | fora da área de obra                                  |
| 3 | Montar o gabarito a 1000 mm do cantoneiro                                | perguntas 75 x 75 e tubos 20 x 100                    |
| 4 | Marcar os eixos X (1) a X (8) e Y (1) a Y (8) no gabarito                | linha coordenada múltipla de 300 mm                   |
| 5 | Cortar cabos com o DQAS diretos                                          | verificar em todos os pontos de corte                 |
| 6 | Conferir a diagonal A-C                                                  | 24870,4 mm com tolerância de 10 mm                    |
| 7 | Conferir o quadrado por 3-4-5 em cada canto                              | senão de qualquer correção                            |
| 8 | Registrar em ata com foto e modelo                                       | gabarito completo nos dois lados da obra, conferência |

#### EIXOS MODULARES

| DIREÇÃO       | PARSO (mm)                                    |
|---------------|-----------------------------------------------|
| X (1) a X (8) | 2400 5400 8400 9600 12600 15600 18600         |
| Y (1) a Y (8) | 7200 9600 12600 15600 18600 21600 24600 27600 |
| Malha         | principal 600 mm - subgrid 300 mm             |
| Origem        | canto frontal esquerdo da base                |
| Unidade       | milímetros                                    |

#### NOTAS

- Locação é o único documento em que o erro não tem contorno técnico: o caso se dá no lugar.
- Cada canto e cada um dos DQAS diretos, nunca em cabos acumulados — erro de cabos soma, erro de referência independente não.
- Conferência obrigatória para diagonal: 24870,4 mm entre A e C antes de concretar o núcleo.
- Ata no ato de locação, assinada por todos os envolvidos (TC-OB, caso DQAS) e pelo responsável da obra.

#### PROJETO PORTO REAL

RESIDÊNCIA UNIFAMILIAR (MANSÃO - AM) | SOBR TATIANA-PS

PROJETO ARQUITETÔNICO

#### LOCAÇÃO DE OBRA E GABARITO

|                                                                                   |                                                            |                                                                         |                               |
|-----------------------------------------------------------------------------------|------------------------------------------------------------|-------------------------------------------------------------------------|-------------------------------|
| BASE GEOMÉTRICA<br>Linha Consolidada<br>ou PDS (previsão)<br>UNIDADE: METROS - MM | ESCALA<br><b>1:100</b><br>FORMATO A1<br>MALHA: 600/300/300 | EMISSÃO<br>ESTUDO PRELIMINAR<br>NÃO LIBERADO PARA OBRA<br>SEM ART / RNT | PROJETA<br><b>31</b><br>06/23 |
|-----------------------------------------------------------------------------------|------------------------------------------------------------|-------------------------------------------------------------------------|-------------------------------|

#### 1 LOCAÇÃO — EIXOS E COORDENADAS

ESCALA 1:100