



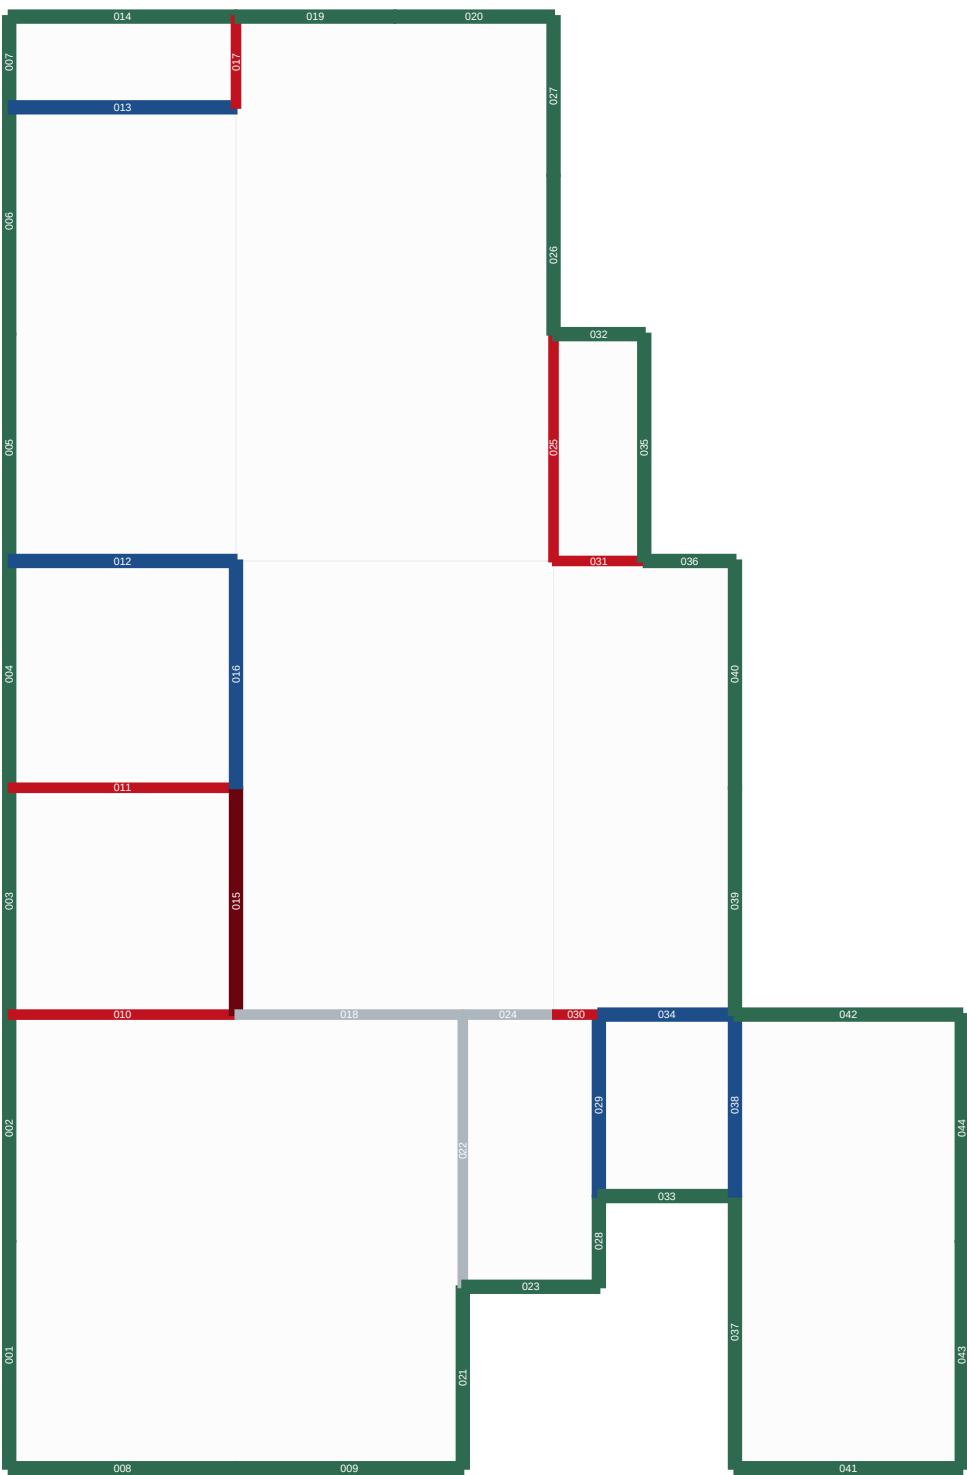

1 PAGINACAO — TERREO
ESCALA 1:100

QUANTITATIVO DE PAINES E MONTANTES

FAMILIA	PAINES	MONTANTES	PI de perfil	COMPOSICAO
PA-1	12	54	140,4	dupla chapa 12,5 + montante 48 x 14 40 + dupla chapa 12,5
PA-2	1	6	15,6	dupla chapa 12,5 + perfil isolante + montante 70 x 14 30
PE-1	45	225	600,6	linhas 32 x 30 x 50 (SD anel) + montante 90 x 14 30 +
PA-3	6	30	83,2	gesso 90 12,5 + montante 90 x 14 30 + gesso 12,5 + reboco
PI-1	3	18	41,8	gesso 12,5 + montante 70 x 14 30 + gesso 12,5
TOTAL	67	341	886,6	

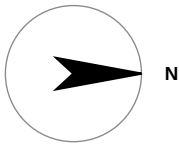

EXTRATO DA LISTA DE PAINES (26 de 67)

CODIGO	FAMILIA	LARGO (mm)	ALT (mm)	MONT.	PROV
PT-001	PE-1	3000	2000	6	T
PT-002	PE-1	3000	2000	6	T
PT-003	PE-1	3000	2000	6	T
PT-004	PE-1	3000	2000	6	T
PT-005	PE-2	3000	2000	6	T
PT-006	PE-1	3000	2000	6	T
PT-007	PE-1	1200	2000	3	T
PT-008	PE-1	3000	2000	6	T
PT-009	PE-1	3000	2000	6	T
PT-010	PA-1	3000	2000	6	T
PT-011	PA-1	3000	2000	6	T
PT-012	PI-1	3000	2000	6	T
PT-013	PI-1	3000	2000	6	T
PT-014	PE-1	3000	2000	6	T
PT-015	PA-2	3000	2000	6	T
PT-016	PI-1	3000	2000	6	T
PT-017	PA-1	1200	2000	3	T
PT-018	PA-1	3000	2000	6	T
PT-019	PE-1	2100	2000	4	T
PT-020	PE-1	2100	2000	4	T
PT-021	PE-1	2400	2000	5	T
PT-022	PI-1	3600	2000	7	T
PT-023	PE-1	1800	2000	4	T
PT-024	PI-1	1200	2000	3	T
PT-025	PA-1	3000	2000	6	T
PT-026	PE-1	2100	2000	4	T

- NOTAS
- * Painéis limitados a 3000 mm por manuseio e transporte.
 - * Montantes a cada 600 mm, 400 mm onde cabido no revestimento exigido.
 - * Não fixar peça entre em moldes sem código, largura, altura, espessura, material e revest.
 - * Numeração por pavimento, a família define a composição interna do painel.

PROJETO PORTO REAL

RESIDENCIA UNIFAMILIAR (MANAUS - AM) | SOUZA TATIANA-PS

PROJETO ARQUITETONICO

PAGINACAO DE PAINES — LIGHT STEEL FRAME

BASE GEOMETRICA Lista Consolidada Projeto (preliminar) UNIDADE: METROS - MM	ESCALA 1:100 FORMATO: A1 MARGEM: 60/50/50/50	EMISSAO ESTUDIO PRELIMINAR LADO LIBERADO PARA CORTA SEM ART / PRINT	PROJETA 18 06/23
--	--	--	-------------------------------