


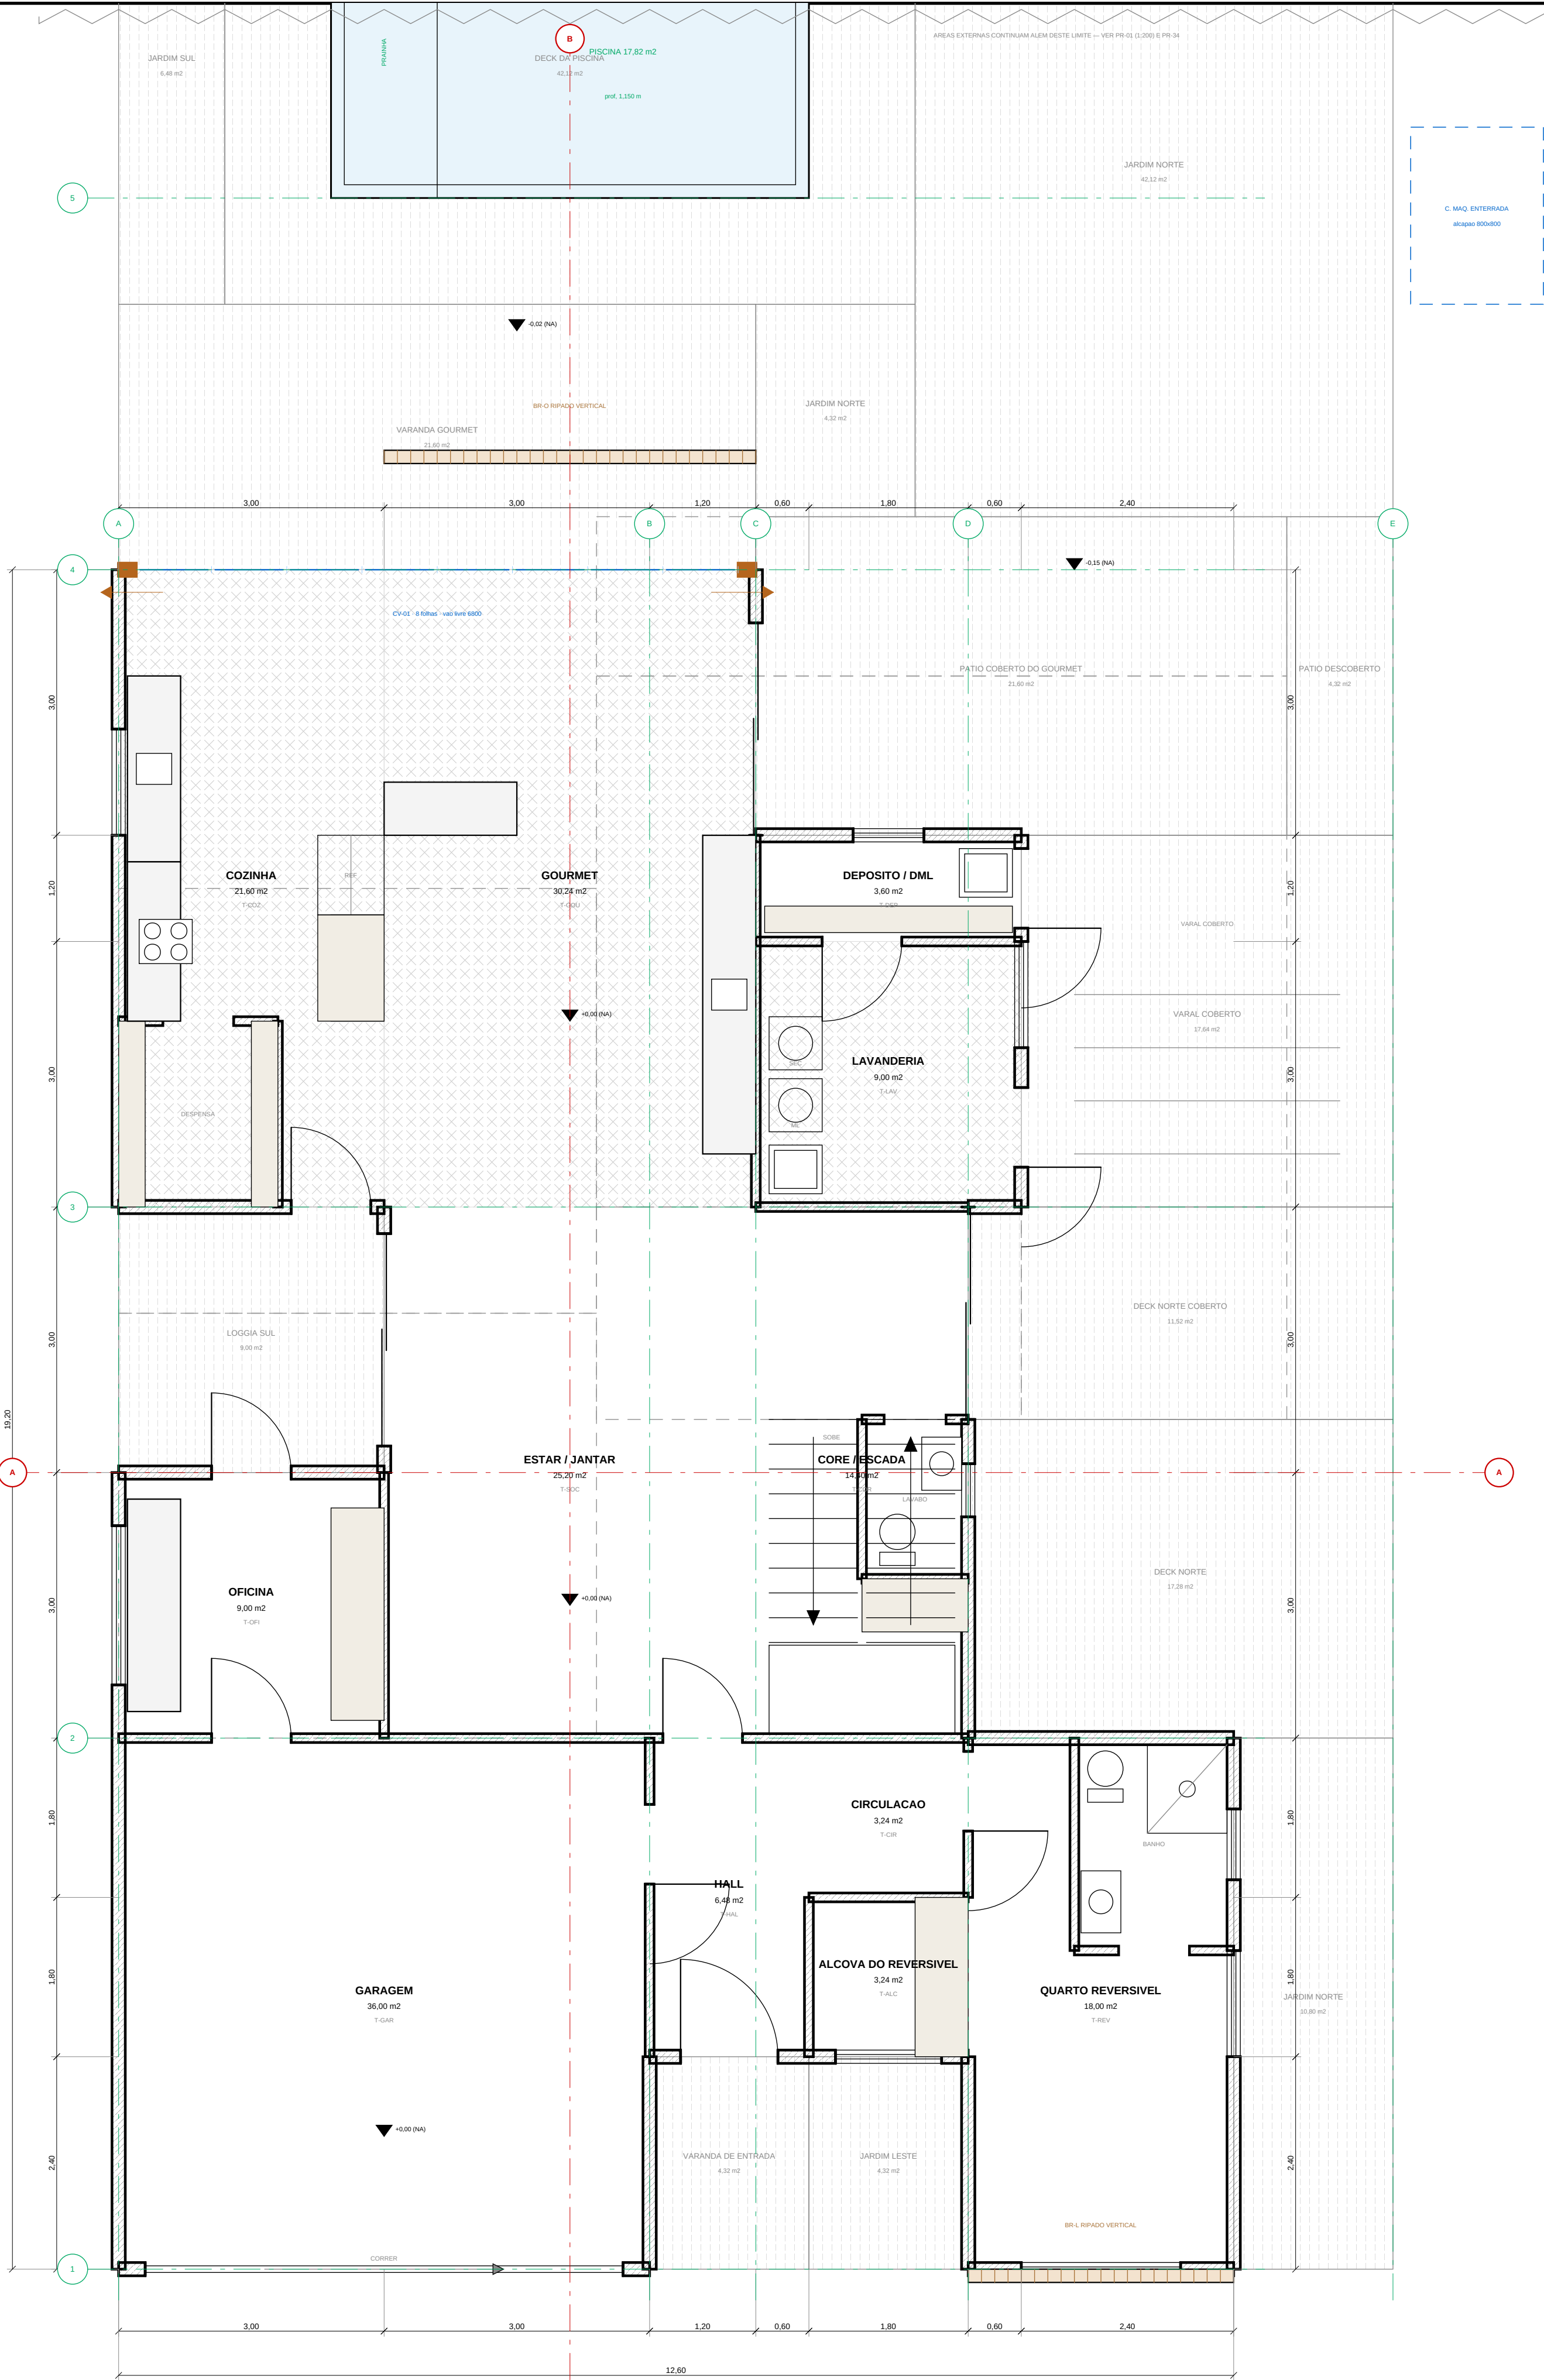

1 PAVIMENTO TERREO
ESCALA 1:50



QUADRO DE ÁREAS — PAVIMENTO TERREO


COD	AMBIENTE	MÓDULO (mm)	ÁREA (m²)
T-GAR	GARAGEM	600x600	36,00
T-HAL	HALL	1800x300	6,48
T-ALC	ALCOVA DO REVERSÍVEL	1800x180	3,24
T-QR	CIRCULAÇÃO	1800x180	3,24
T-REV	QUARTO REVERSÍVEL	3000x600	18,00
T-OFI	OFICINA	3000x300	9,00
T-SOC	ESTAR / JANTAR	4500x600	25,20
T-COR	CORE / ESCADA	2400x600	14,40
T-COZ	COZINHA	3000x750	21,80
T-GOU	GOURMET	4500x700	30,24
T-LAV	LAVANDERIA	3000x300	9,00
T-DEP	DEPOSITO / DML	3000x1200	3,60
TOTAL FECHADO			188,08
T-VAR	VARANDA DE ENTRADA (área)	1800x240	4,32
T-J-E	JARDIM LESTE (área)	1800x400	4,32
T-J-N	JARDIM NORTE (área)	1800x600	10,80
T-LOG	LOGGIA SUL (área)	3000x300	9,00
T-DML	DECK NORTE (área)	4800x300	17,28
T-DIC	DECK NORTE COBERTO (área)	4800x240	11,52
T-VAR	VARAL COBERTO (área)	4500x400	17,64
T-PAT	PATIO COBERTO DO GOURMET (área)	6000x300	25,80
T-PAT	PATIO DESCOBERTO (área)	1200x300	4,32
T-VAR	VARANDA GOURMET (área)	7500x300	25,80
T-DEP	DECK DA PISCINA (área)	7800x400	42,32
T-J-S	JARDIM SUL (área)	1200x600	6,48
T-J-N	JARDIM NORTE (área)	1800x240	4,32
T-J-N	JARDIM NORTE (área)	5400x700	42,32
T-PV	JARDIM DE PUNDO (área)	14800x400	69,32

MAPA DE ESQUADRIAS DO PAVIMENTO


REF	VALOR (mm)	REF	QTD	TIPO
CVE1	7200x2400	0	1	CORTINA DE VIDRO total, 0 folha de 900 mm
J1	1200x1200	1300	4	porta de dormitório, alumínio
J2	800x800	1300	1	porta de banheiro, alumínio
J3	800x800	1300	2	porta de banheiro, alumínio
J4	1800x1200	1300	2	porta de dormitório, alumínio
J5	1200x1200	0	1	porta principal, alumínio
J6	800x1200	0	2	porta interna (divisão unificada)
J7	800x1200	0	6	porta de serviço, alumínio a unidade
J8	800x1200	0	1	porta interna de sala SOLADA com vidros (pali)
J9	5400x2400	0	1	porta de correr, alumínio espado
J10	3600x2400	0	1	porta de correr, alumínio espado

LEGENDA E CONVENÇÕES (NBR 6492 / 8403)

- Elemento seccionado pelo plano de corte (h = 1,50 m)
- Área vista / folha de esquadria
- Mobiliário fixo, equipamento e sinetologia
- Propriedade do pavimento superior e da cobertura
- Eixo modular e linha de corte
- Linha de vista e linha auxiliar

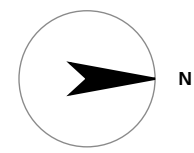

PERCURSO SOLAR — MANUS 1.5

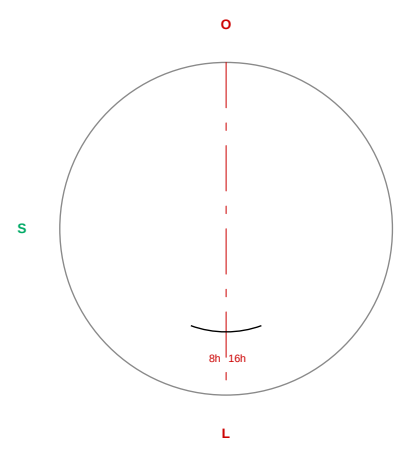

Nota: 1: 4,0 m x 3,0 m (área)

→ segue linha ESTRUTURAL

Nota: 2: 5,0 m x 3,0 m (área)

→ segue linha 2,00 m (área)

- Dimensões em milímetros; cotas de nível em metros.
- Malha modular 600 mm; cotas elevadas a 600.
- Planta externa 120 mm / planta interna 120 mm (p).
- Mobiliário fixo indica pontos de água e energia (NBR 6492).

PROJETO PORTO REAL

RESIDÊNCIA UNIFAMILIAR (MANUS - AM) | SOUS TATIANA (PS)

PROJETO ARQUITETÔNICO

PLANTA BAIXA — PAVIMENTO TERREO

BASE GEOMÉTRICA

União Consolidada

PS: P22 (previsão)

UNIDADE MÉTRICA: mm

ESCALA

1:50

FORMATO A1

MAQUETA 600x900mm

EXIBIÇÃO

ESTUDO PRELIMINAR RBO

MAQUETA PARA OBRA

SEM ART / RNT

PROJETO

02

06/15/REV 02