

- downlight embudo
- ⊕


plafon de sobrepor (forno perfurado / aparente)
- pendente (je-direito duplo)
- linear do tafeito (bancado, closet, mesa)
- arandela de espelho
- balizador de escada
- 2700 K
- 3000 K
- 4000 K
- forno absorvente perfurado (afa 0.70)
- sem forno (panel PPR aparente)

LUMINOTECNICA POR AMBIENTE — METODO DOS LUMENS

AMB	USO	h2	altura	aberto	LUMINARIA	cm	m
T-COR	apoi	30.0	75	108	4 x Plafon LED de sobrepor 24 W	4000 K	96
T-AL	circulacao	6.5	100	151	2 x Downlight LED embudo 18 W	3000 K	36
T-ALC	recep	3.0	100	151	1 x Downlight LED embudo 18 W	2700 K	18
T-COR	circulacao	3.0	100	151	1 x Downlight LED embudo 18 W	3000 K	18
T-REV	recep	12.7	100	200	5 x Downlight LED embudo 18 W	2700 K	90
T-COR	aberto	9.0	100	151	4 x Downlight LED embudo 18 W	4000 K	144
T-SOC	social	25.2	200	242	8 x Downlight LED embudo 24 W	3000 K	144
T-COR	escada	12.2	100	188	2 x Pendente LED de je-direito dup	3000 K	90
T-COR	circulacao	17.8	300	350	7 x Downlight LED embudo 24 W	4000 K	108
T-COR	social	30.2	200	208	6 x Plafon LED de sobrepor 24 W	3000 K	144
T-LAV	banho	9.0	200	240	4 x Downlight LED embudo 18 W	4000 K	72
T-REV	banho	3.0	200	270	2 x Downlight LED embudo 18 W	4000 K	36
S-SOC	recep	21.6	100	182	5 x Downlight LED embudo 18 W	2700 K	90
S-SOC	recep	21.6	100	182	5 x Downlight LED embudo 18 W	2700 K	90
S-AL	circulacao	11.5	100	120	2 x Downlight LED embudo 24 W	3000 K	40
S-LAV	social	7.2	200	350	4 x Downlight LED embudo 24 W	3000 K	96
S-MAS	recep	21.6	100	182	6 x Downlight LED embudo 18 W	2700 K	90
S-SOC-BANHO	banho	4.0	200	230	2 x Downlight LED embudo 18 W	3000 K	36
S-SOC-BANHO	banho	4.0	200	230	2 x Downlight LED embudo 18 W	3000 K	36
T-COR-ESPENSA	banho	9.0	200	398	2 x Downlight LED embudo 24 W	4000 K	48
T-REV-BANHO	banho	4.0	200	230	2 x Downlight LED embudo 18 W	3000 K	36
T-COR-LAVABO	banho	2.0	200	227	1 x Downlight LED embudo 18 W	3000 K	18
S-MAS-BANHO	banho	10.8	200	251	4 x Downlight LED embudo 18 W	3000 K	72
S-MAS-CLOSET	closet	9.0	200	240	4 x Downlight LED embudo 18 W	3000 K	72
S-MAS-OFFICE	office	5.4	300	512	4 x Downlight LED embudo 24 W	4000 K	96

LUZ DE TAREFA

CD	ON	TIPO	QTD	cm
L1-BC-01	banhada BC-01 (T-COR)	linear	2.1 m	4000 K
L1-BC-02	banhada BC-02 (T-COR)	linear	1.8 m	4000 K
L1-BC-03	banhada BC-03 (T-COR)	linear	1.5 m	4000 K
L1-BC-04	banhada BC-04 (T-COR)	linear	3.0 m	4000 K
L1-BC-05	banhada BC-05 (T-COR)	linear	2.4 m	4000 K
L1-LC-01	espelho do banheiro LC-01 (T-COR)	arandela	1	4000 K
L1-LC-02	espelho do banheiro LC-02 (T-REV)	arandela	1	4000 K
L1-LC-03	espelho do banheiro LC-03 (S-SOC)	arandela	1	4000 K
L1-LC-04	espelho do banheiro LC-04 (S-SOC)	arandela	1	4000 K
L1-LC-05	espelho do banheiro LC-05 (S-MAS)	arandela	2	4000 K
L1-S-MAS-CLOSET	closet do S-MAS	linear	3.0 m	3000 K
L1-S-MAS-OFFICE	mesa do office do S-MAS	linear	1.2 m	4000 K
L1-ENCADIA	escada (banheiros)	balizador	6	3000 K

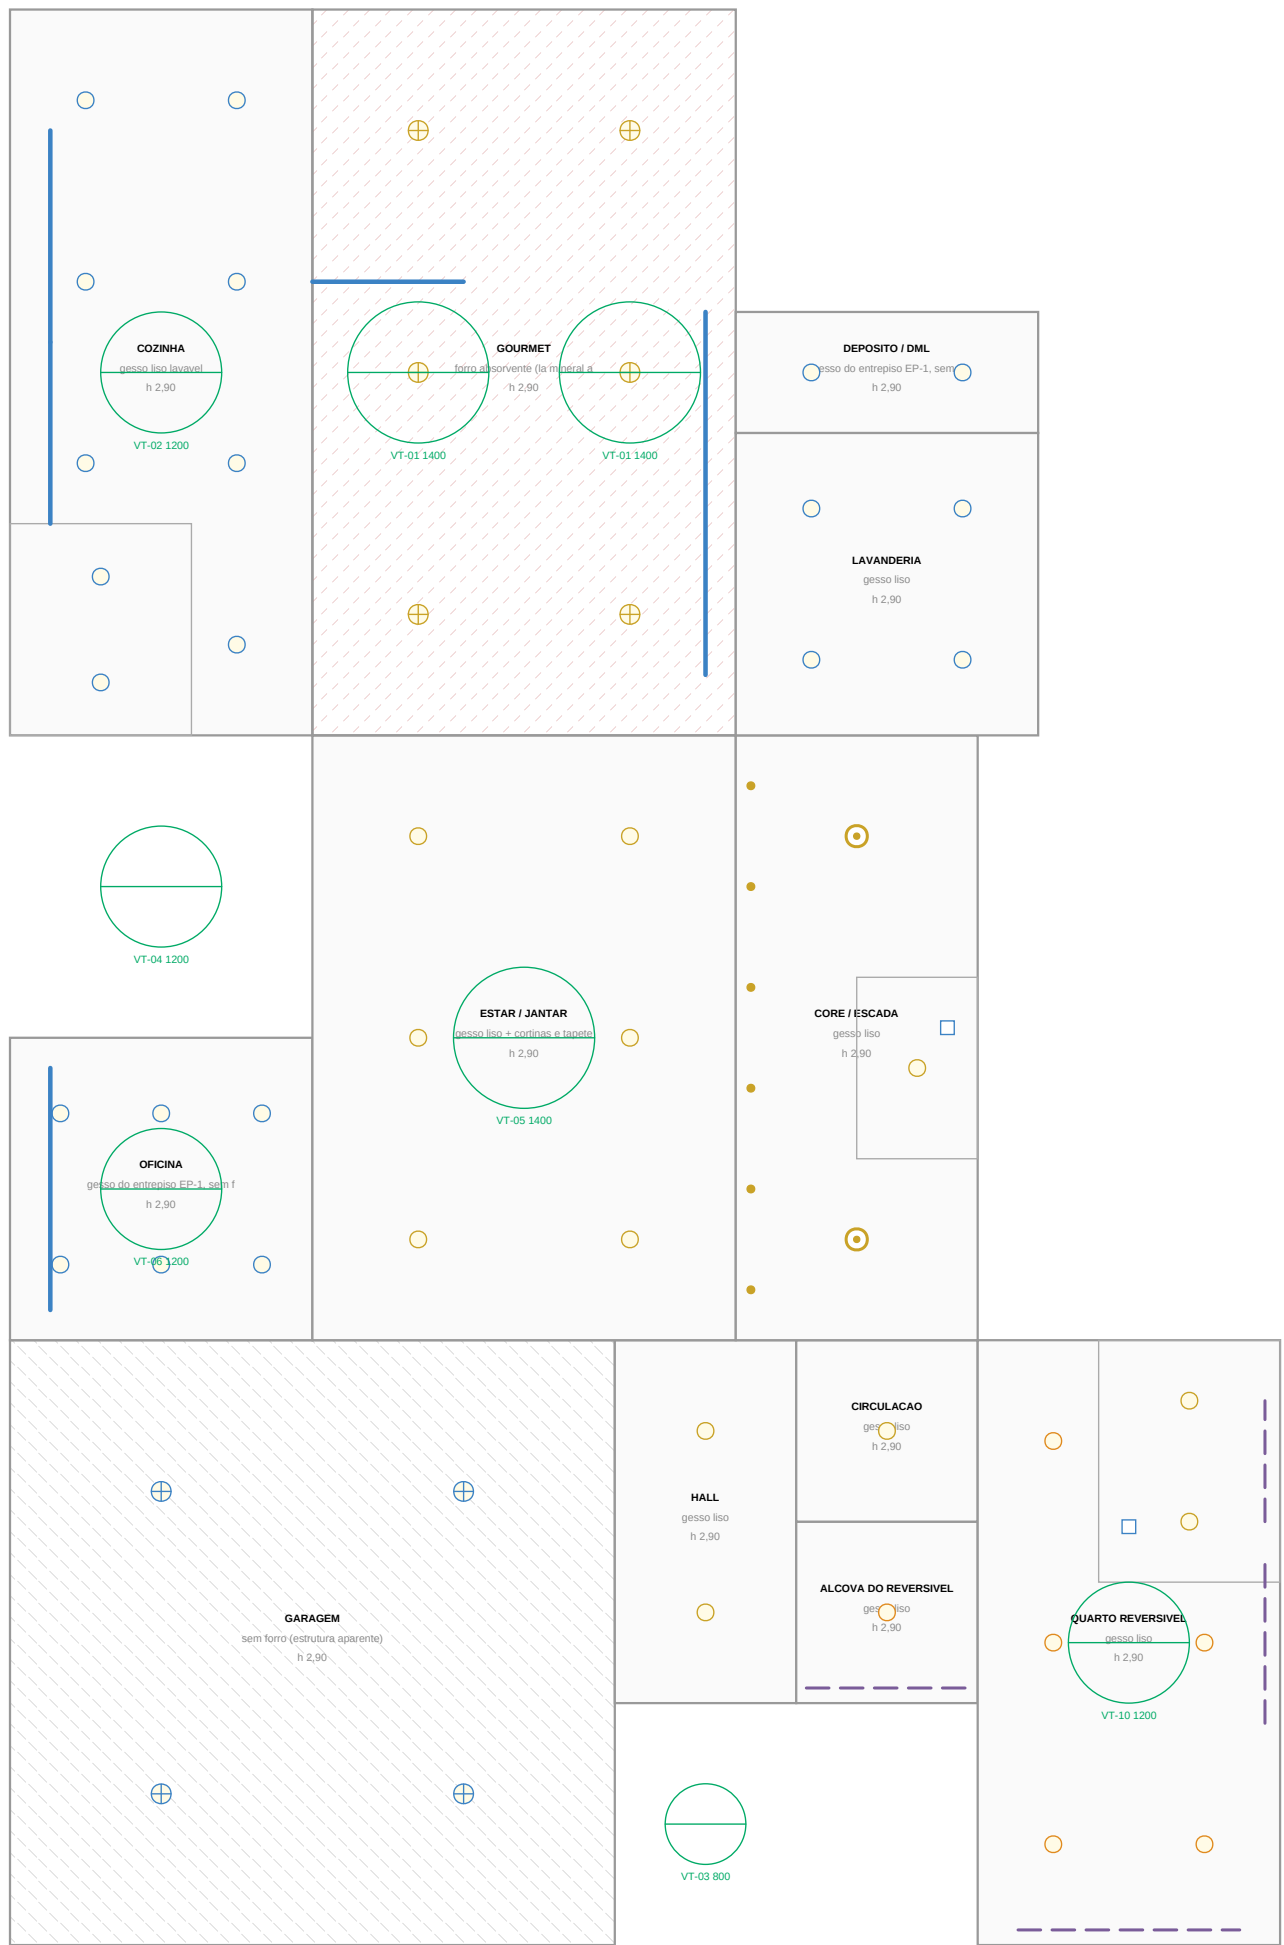

1 FORRO REFLETIDO — TERREO
ESCALA 1:75



2 FORRO REFLETIDO — SUPERIOR
ESCALA 1:75

- NOTAS
- Planta refletida: vista do forno projetada no plano horizontal, terreno e superior.
 - Luminarias pelo METODO DOS LUMENS por ambiente (NBR 9050:2020 / NBR 5413), medida de uniformidade SHI 1.2.
 - 18 pontos gerais, 12 pontos de tarefa, 3074 W (3.3 kWh).
 - Cor: 2.700 K interno, 3.000 K social e circulacao, 4.000 K cozinha, banheiro e hall.
 - 11 pontos de tarefa (pontos), diâmetro em mm.
 - Cantidade (balizador) reduzido de 100 mm ao longo da planta de todo ambiente interno.

PROJETO PORTO REAL

RESIDENCIA UNIFAMILIAR (MANSÃO - AM) (SUA TATIANA-PS)

PROJETO ARQUITETONICO

PLANTA DE FORRO E ILUMINACAO

BASE GEOMETRICA União Consolidada Projeto (preliminar) Unidade (preliminar)	ESCALA 1:75 FORMATO A1 MILIMETROS (1:75)	EXATIDÃO ESTUDO PRELIMINAR RIO Linha (preliminar) SEM ART / RNT	PROVA 16 IN 75 REV 100
--	---	--	------------------------------