


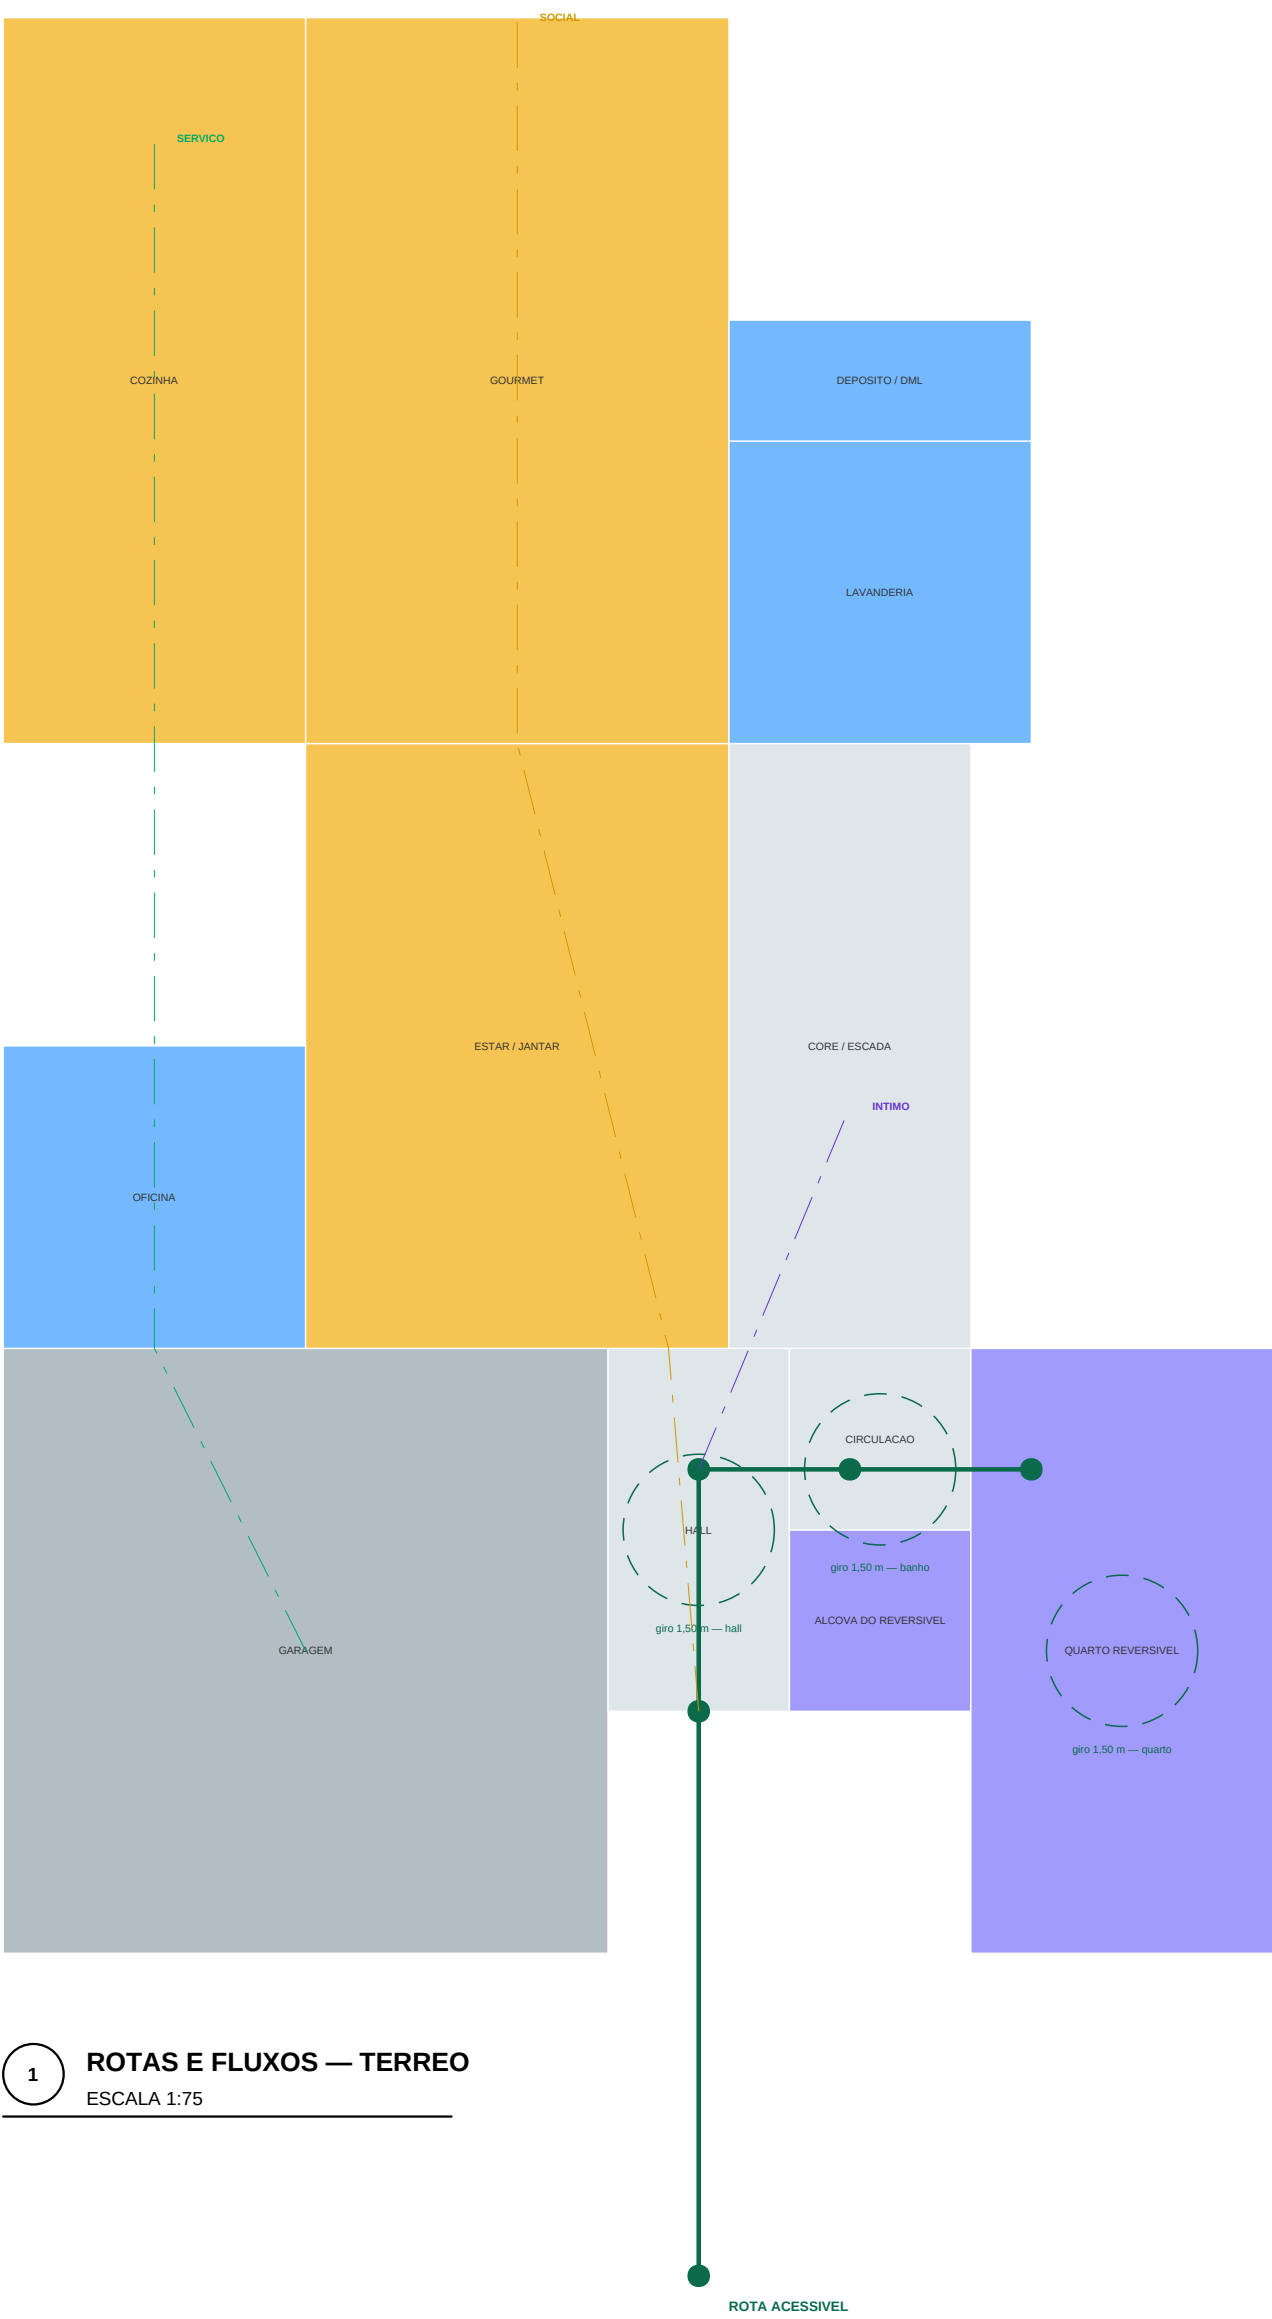


1 ROTAS E FLUXOS — TERREO
ESCALA 1:75

VERIFICACAO NBR 9050

ITEM	EXISTENTE	PROPOSTO	
Visão livre de porta	800 mm	940 mm (altura de 900)	OK
Circuito de giro 360 graus	1.500 mm	hall, banheiro e quarto	OK
Desnível sem rampas	até 5 mm	soluções niveladas	OK
Largura de circulação	900 mm	1.800 mm no hall	OK
Barra de apoio	relevo no piso	instalada no PTE 1 e PTE 2	OK
Barreira acústica	altura livre 730 mm	sem barreiras acústicas	OK
Contraste e interruptor	600 a 1.000 mm	a definir no detalhe	pendente

FLUXOS — SEPARACAO DE CIRCUITOS

CIRCUITO	PERCURSO	CRUZAR O SOCIAL?
Serviço	garagem → elevador → lavanderia → cozinha → despensa	NÃO
Social	entrada → hall → estar → gourmet → alameda → piscina	—
Área de serviço	hall → circulação → banheiro social (quarto reversível) (se não for projeto)	NÃO
Área superior	hall → corredor → hall superior → suíte	NÃO
Área de carga	cozinha → despensa → reservatório	NÃO

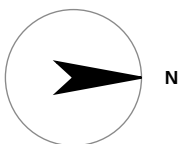

NOTAS

- * Rota acessível do passeio ao quarto reversível e ao banheiro social.
- * Circuito de giro de 1.500 mm verificado nos pontos de manobra.
- * Porta de correr de 900 mm no banheiro social e área de manobra.
- * Reforço para barra de apoio instalada antes do fechamento das placas.

PROJETO PORTO REAL

RESIDENCIA UNIFAMILIAR (MANSÃO - AM) | SOBR TATIANA-PS

PROJETO ARQUITETONICO

ACESSIBILIDADE E FLUXOS

BASE GEOMETRICA	ESCALA	EMISSAO	PROJETO
União Consolidada	1:75	ESTUDO PRELIMINAR RBO	
ISO 9242 (previsão)	FORMATO A1	NÃO LIBERADO PARA OBRA	
UNIDADE MESTRE: AM	MAI 2024 05/05/2024	SEM ART / RNT	17
			05-75 REV 000