

VIDRO POR VAO — FATOR SOLAR (g <= 0.45 nas faces L e O)

VAO	FACE	AMB	m2	VIDRO	g	m2 equiv.	
J04	N	T-REV	0.72	temperado 8 mm laminado	0.70	1.4	OK
J02	N	T-COR	0.36	temperado 8 mm laminado	0.70	0.7	OK
J05	L	T-REV	2.16	laminado 6+4 PVB acústico + controle solar	0.45	2.8	OK
J01	N	T-REV	1.44	temperado 8 mm comum	0.80	3.3	OK
J03	L	T-ALC	1.44	laminado 6+4 PVB acústico + controle solar	0.45	1.9	OK
J05	S	T-COR	2.16	temperado 8 mm comum	0.80	4.9	OK
J01	S	T-COR	1.44	temperado 8 mm comum	0.80	3.3	OK
J01	N	T-LAV	1.44	temperado 8 mm comum	0.80	3.3	OK
J04	O	T-OSP	0.72	temperado 8 mm laminado com controle solar	0.45	0.6	OK
P002	N	T-COR	9.76	temperado 8 mm comum	0.80	13.2	OK
P002	N	T-COR	9.76	temperado 8 mm comum	0.80	13.2	OK
C015	O	T-COR	18.72	laminado 6+4 lona e 8 folhas de 800 mm, g <=	0.35	18.7	OK
P002	S	T-COR	9.76	temperado 8 mm comum	0.80	13.2	OK
J01	N	S-COR	1.44	temperado 8 mm comum	0.80	3.3	OK
J05	S	S-COR	2.16	temperado 8 mm comum	0.80	4.9	OK
J01	L	S-COR	1.44	laminado 6+4 PVB acústico + controle solar	0.45	1.8	OK
J04	L	S-COR	0.72	temperado 8 mm laminado com controle solar	0.45	0.9	OK
J05	S	S-COR	2.16	temperado 8 mm comum	0.80	4.9	OK
J01	O	S-COR	1.44	laminado 6+4 lona e, g <= 0.35	0.35	1.4	OK
J04	S	S-COR	0.72	temperado 8 mm laminado	0.70	1.4	OK
J05	S	S-MAQ	2.16	temperado 8 mm comum	0.80	4.9	OK
P002	O	S-MAQ	9.76	laminado 6+4 PVB acústico lona e, g <= 0.35	0.35	8.6	OK
J04	N	S-MAQ	0.72	temperado 8 mm laminado	0.70	1.4	OK
J01	N	S-MAQ	1.44	temperado 8 mm comum	0.80	3.3	OK

m2 equiv. = área x g (g_ref e o que entra na carga térmica (CLIMA_Q_VIDRO vale para g = 0.35).

Zona social: carga 28200 BTU/h com low-e na cortina, conta 30000 BTU/h instalados. Com temperado comum (g 0.80) a mesma cortina somaria 4813 BTU/h.

SPDA — NBR 5419: AVALIACAO E COMPONENTES


ITEM	VALOR	ORIGEM
Densidade de descarga Ng	12 A/m2 ano	(N) REINATEL/AT — pendência 15
Área de exposição equivalente Ad	2018 m2	L.W = 616*(W) + 5*(L)C, com H = tipo da platanda
Frequência de descarga direta Nd	0.028 (vez)	Ng *Ad *Caf (Caf = 1, variacao localid)
Período de retorno	30 anos	1 / Nd
Classe de praticidade atendida	IV	decisão do projeto. Manuais, 600 pavimentos, etc
Cápitel	área de 160.8 m no perímetro da cobertura	matriz 35 x 20 m e a cobertura cobre toda a sala
Descidas	4 pela estrutura LCP (passado)	espaçamento <= 20 m; montante 155 mm2 <= 50
Aterramento	área de 63.6 m x 4 faixas	cabo no 30 mm2 no perímetro do radier
Proteção interna	SPD+ DPM classe I na entrada + DPM classe I nos quadros	norm 5433 e 5436 5437

FOTOVOLTAICA — DIMENSIONAMENTO

ITEM	VALOR	ORIGEM
Consumo estimado	97.5 kWh/mês - 2952 kWh/ano	sóto por capacidade e fonte (N), Normacao calculada, (Chumbo, Solar
Irradiacao (HSP)	4.4 kWh/m2 dia	(N) Atlas RSPF — pendencia 15
Potência necessária	18.5 kWp	consumo / (HSP * PR 0.75)
Módulos	29 x 550 Wp = 15.55 kWp	82 m2 com 184p, o consumo pedido 35, cabem 29 — instala-se o que cabe
Cobertura disponível	87.1 m2 (superior, menos passante)	OK
Carga na cobertura	0.328 kN/m2	limite decidido em carga 0.15 kN/m2 — OK
Inversor	12 kW em TC 17 (bom bomba solar)	reforma CCGA 1.33
Geracao anual	20688 kWh	cabo 65 % do consumo estimado
Economia e retorno	R\$ 12644/ano - payback 2.5 anos	tarifa R\$ 0.054/kWh (N), custo (N) do BOM

Microgeracao distribuida (REN ANEEL 1.000/2021): compensacao de credito; a rede continua sendo a bateria.

1 PERFIL DE INSOLACAO NA FACHADA OESTE
ESCALA s/ escala

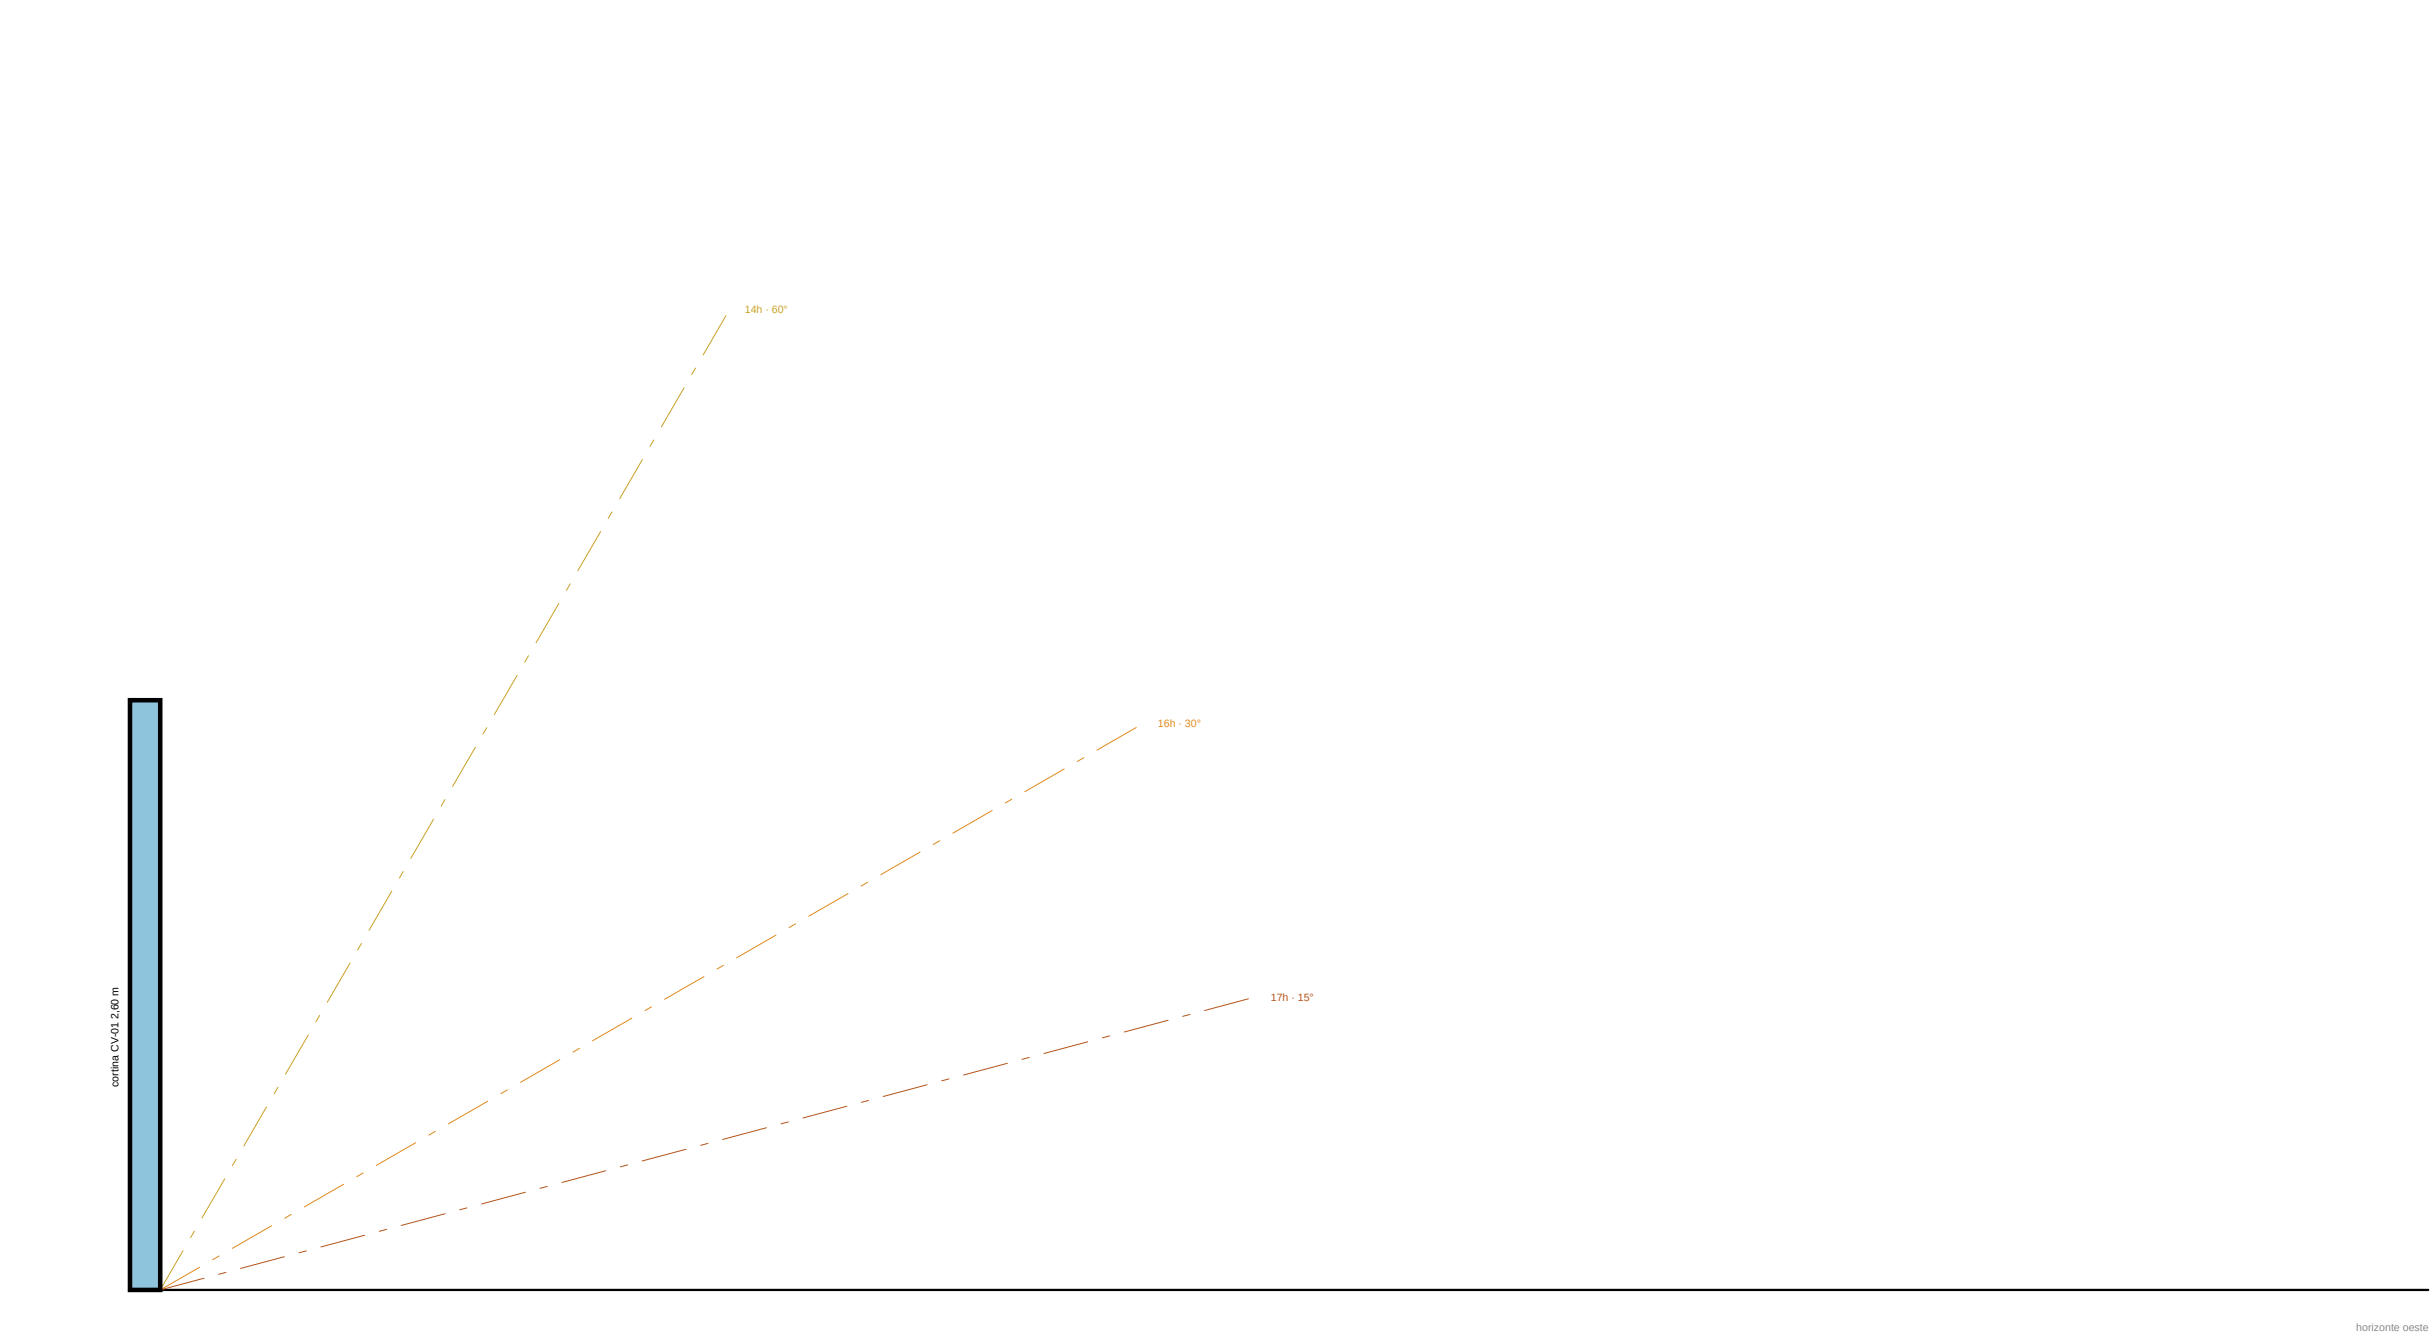

Equinoccio, latitude 3 S: as 16 h o sol está a 30 graus, de frente para a cortina. Bêta de 1 m sombra no os 56 cm de cima, o que resolve o o vidro (g) e o brise vertical.
Com g < 0.80 entram -600 Wh/m2 x 0.80 = 480 Wh/m2, com low-e g = 0.35, 210 Wh/m2. São 18.7 m2, 5.0 kW contra 2.2 kW de calor no estar.

NOTAS
- Treco decorado que ficam cerca depois da estrutura: o vidro da cortina, o peso vidro e a geracao propria.
- Manuais: Ng = 12 descarga/m2 ano (N) — entre os materiais do pais, irradiacao 4.6 kWh/m2 dia (N).
- A estrutura de aço do LCP e decidida natural (NBR 5433-3); a protecao custo capto, area e conexao, não cobre pela fachada.
- Valores (N) de solo e de prazo pendencia 15.

PROJETO PORTO REAL

RESIDENCIA UNIFAMILIAR (MANAUS - AM) (SUS TATIANA-PS)

PROJETO ARQUITETONICO

ENERGIA — FOTOVOLTAICA, SPDA E VIDRO SOLAR

BASE GEOMETRICA Linha Consolidada em PDF (previsão) UNIDADE: METROS: mm	ESCALA s/ escala FORMATO A1 MILHA 405/500/500	EMISSAO ESTUDIO PRELIMINAR RBO NAO LIBERADO PARA OBRA SEM ART / RNT	PROJETA 41 em TS REVISO
--	--	--	---------------------------------------