
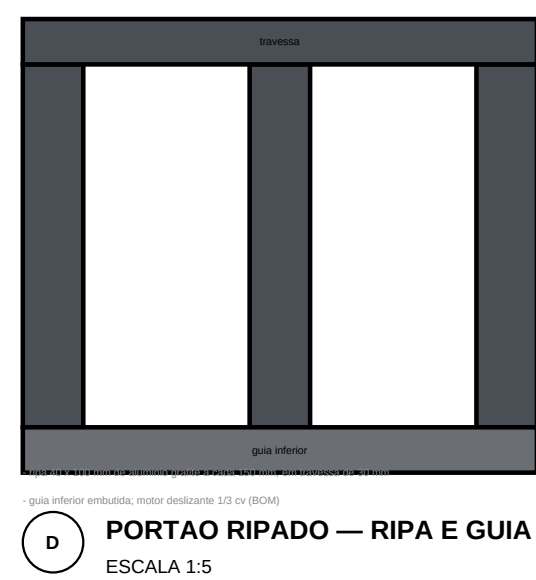


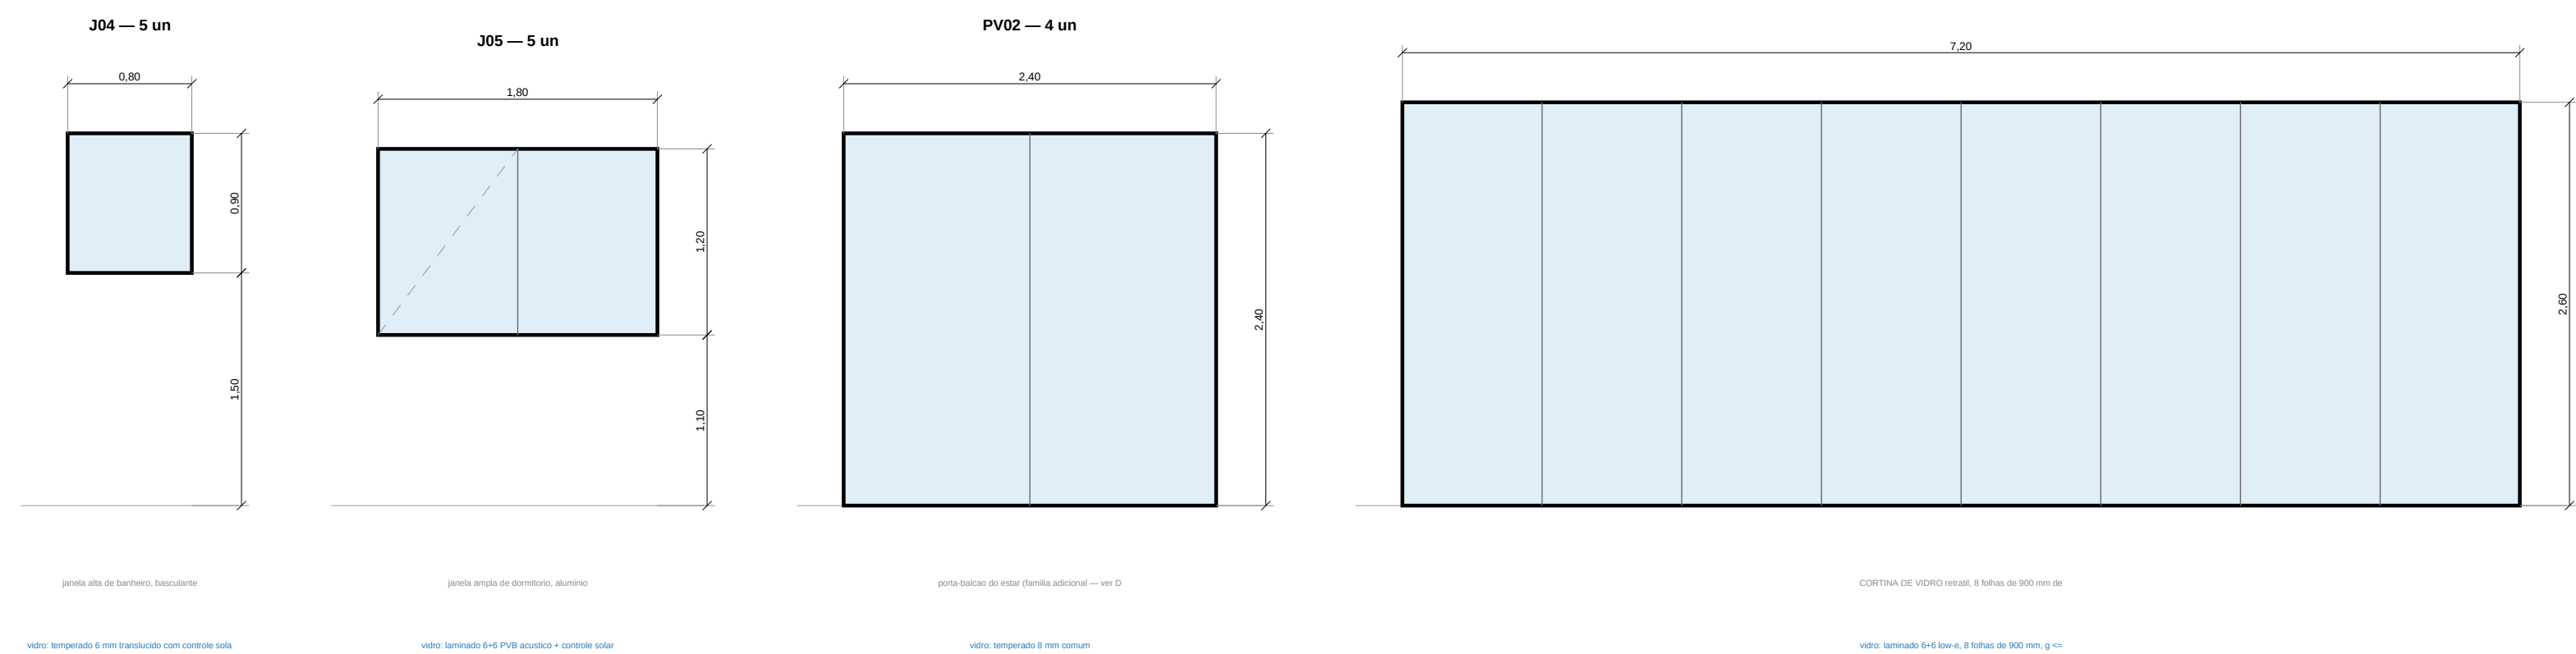

PROJETO PORTO REAL			
RESIDENCIA UNIFAMILIAR (MANAUS) - IM (5)05 TAPARA (P)			
PROJETO ARQUITETONICO			
ESQUADRIAS — TIPOS, QUANTIDADES E DETALHES			
BIGUE GEOMETRICA Lista Correlativa po-022 (previsto) UNIDADE MESTRE (m²)	ESCALA 1:40 • 1:5 FORMATO A1 SALHA 900/600/300	EMISSAO ESTUDO PRELIMINAR R00 NÃO LIERACAO PARA OBRA SEM IMT / IMT	PRECISAO 52 de 75 REV 00