



1 BC-01 GABINETE SOB GRANITO
ESCALA 1:40

4 mod. - 3 pontos - 0 grau - 24 peças - perfil gôta de alumínio graf

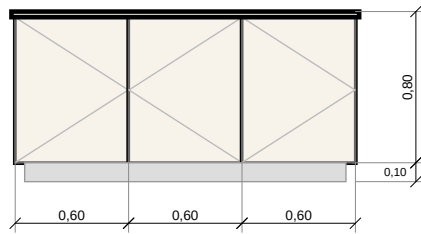


2 BC-02 GABINETE SOB GRANITO
ESCALA 1:40

3 mod. - 3 pontos - 0 grau - 18 peças - perfil gôta de alumínio graf

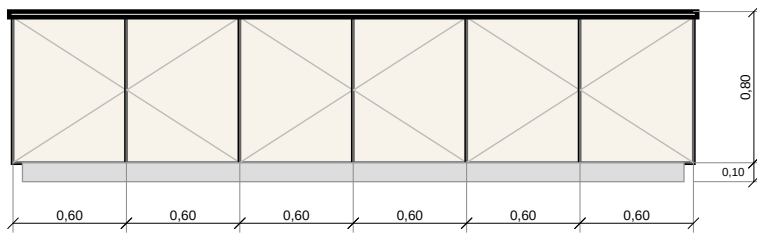


3 BC-04 GABINETE SOB GRANITO
ESCALA 1:40

6 mod. - 6 pontos - 0 grau - 36 peças - perfil gôta de alumínio graf

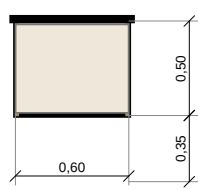


9 LC-02 GAB. LAVATORIO
ESCALA 1:40

2 mod. - 0 pontos - 2 grau - 20 peças - canto voltado a 45 graus (cort)

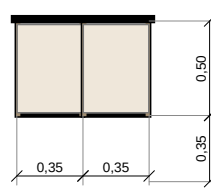


10 LC-15 GAB. LAVATORIO
ESCALA 1:40

2 mod. - 0 pontos - 2 grau - 20 peças - canto voltado a 45 graus (cort)

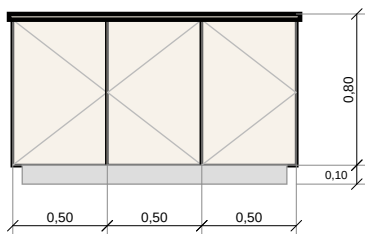


4 BC-03 GABINETE SOB GRANITO
ESCALA 1:40

3 mod. - 3 pontos - 0 grau - 18 peças - perfil gôta de alumínio graf

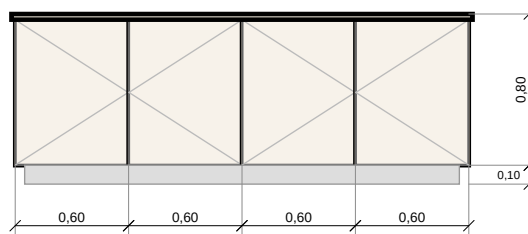


5 BC-06 GABINETE SOB GRANITO
ESCALA 1:40

4 mod. - 4 pontos - 0 grau - 24 peças - perfil gôta de alumínio graf

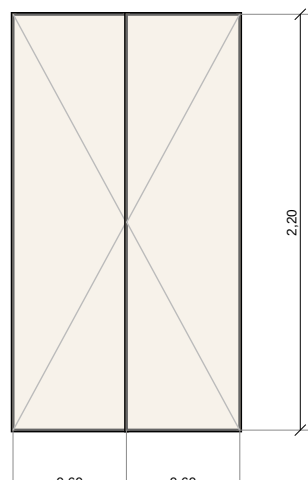


6 AR-08 ARMARIO ALTO
ESCALA 1:40

2 mod. - 2 pontos - 0 grau - 20 peças - perfil gôta de alumínio graf

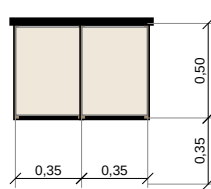


11 LC-05 GAB. LAVATORIO
ESCALA 1:40

2 mod. - 0 pontos - 2 grau - 20 peças - canto voltado a 45 graus (cort)

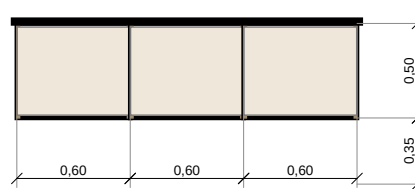


12 LC-11 GAB. LAVATORIO
ESCALA 1:40

3 mod. - 0 pontos - 3 grau - 30 peças - canto voltado a 45 graus (cort)

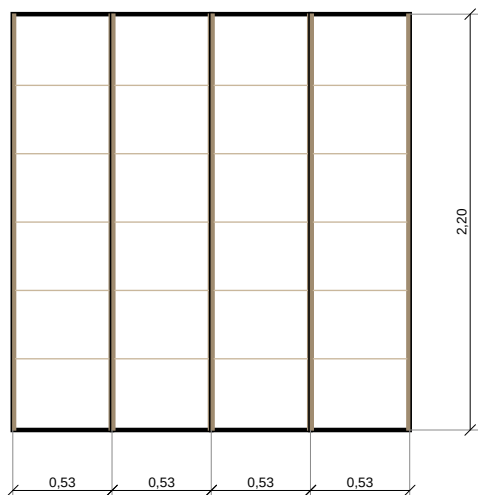


7 AR-06 PRATELEIRAS
ESCALA 1:40

4 mod. - 0 pontos - 0 grau - 40 peças - perfil gôta de alumínio graf

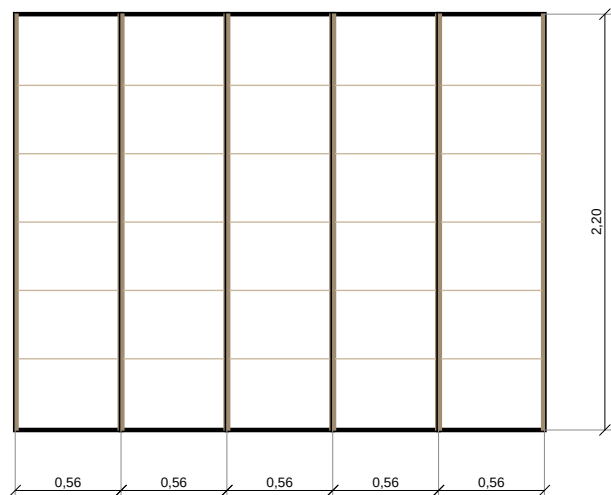

8 AR-03 PRATELEIRAS
ESCALA 1:40

5 mod. - 0 pontos - 0 grau - 50 peças - perfil gôta de alumínio graf

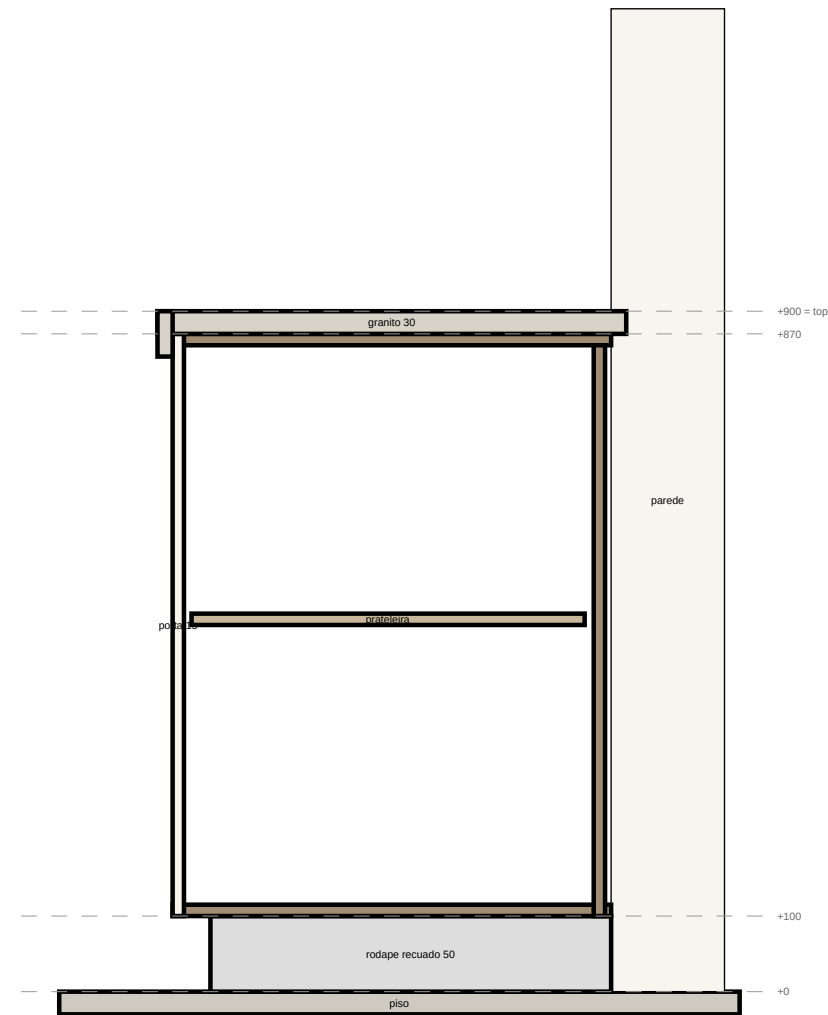

A SECAO DO GABINETE SOB GRANITO — APOIO E RODAPE
ESCALA 1:10

NOTAS

- Gabinete sob granito: caixa de MDF 15 mm sobre suporte, rodape recuado 50 mm, tempo a 800 mm. Módulo com todos sem prateleira, módulo de cooktop com uma.
- Gabinete de lavatório suspenso a 200 mm do piso, uma gaveta por módulo, cuba de apoio.
- Porta por módulo, dobradiças pela altura (2 até 900, 3 até 1.500, 4 até 2.000, 5 acima).
- Prateleira trançada e arcos de porta. Puxador perfil gôta grafite nas portas sociais.

PROJETO PORTO REAL

RESIDENCIA UNIFAMILIAR | MARAULIS - AM | SOBR TATIANA-PS

PROJETO ARQUITETONICO

MARCENARIA I — GABINETES DE COZINHA, GOURMET, OFICINA E BANHOS

BASE GEOMETRICA	ESCALA	EMISSAO	PROJECION
União Consolidada	1:40 • 1:10	ESTUDIO PRELIMINAR RBO	56
Projeto (previsão)	FORMATO A1	NAO LIBERADO PARA OBRA	
UNIDADE: METRO: mm	MAQUETA: 600/900/300	SEM ART / RNT	em TS REVISO