


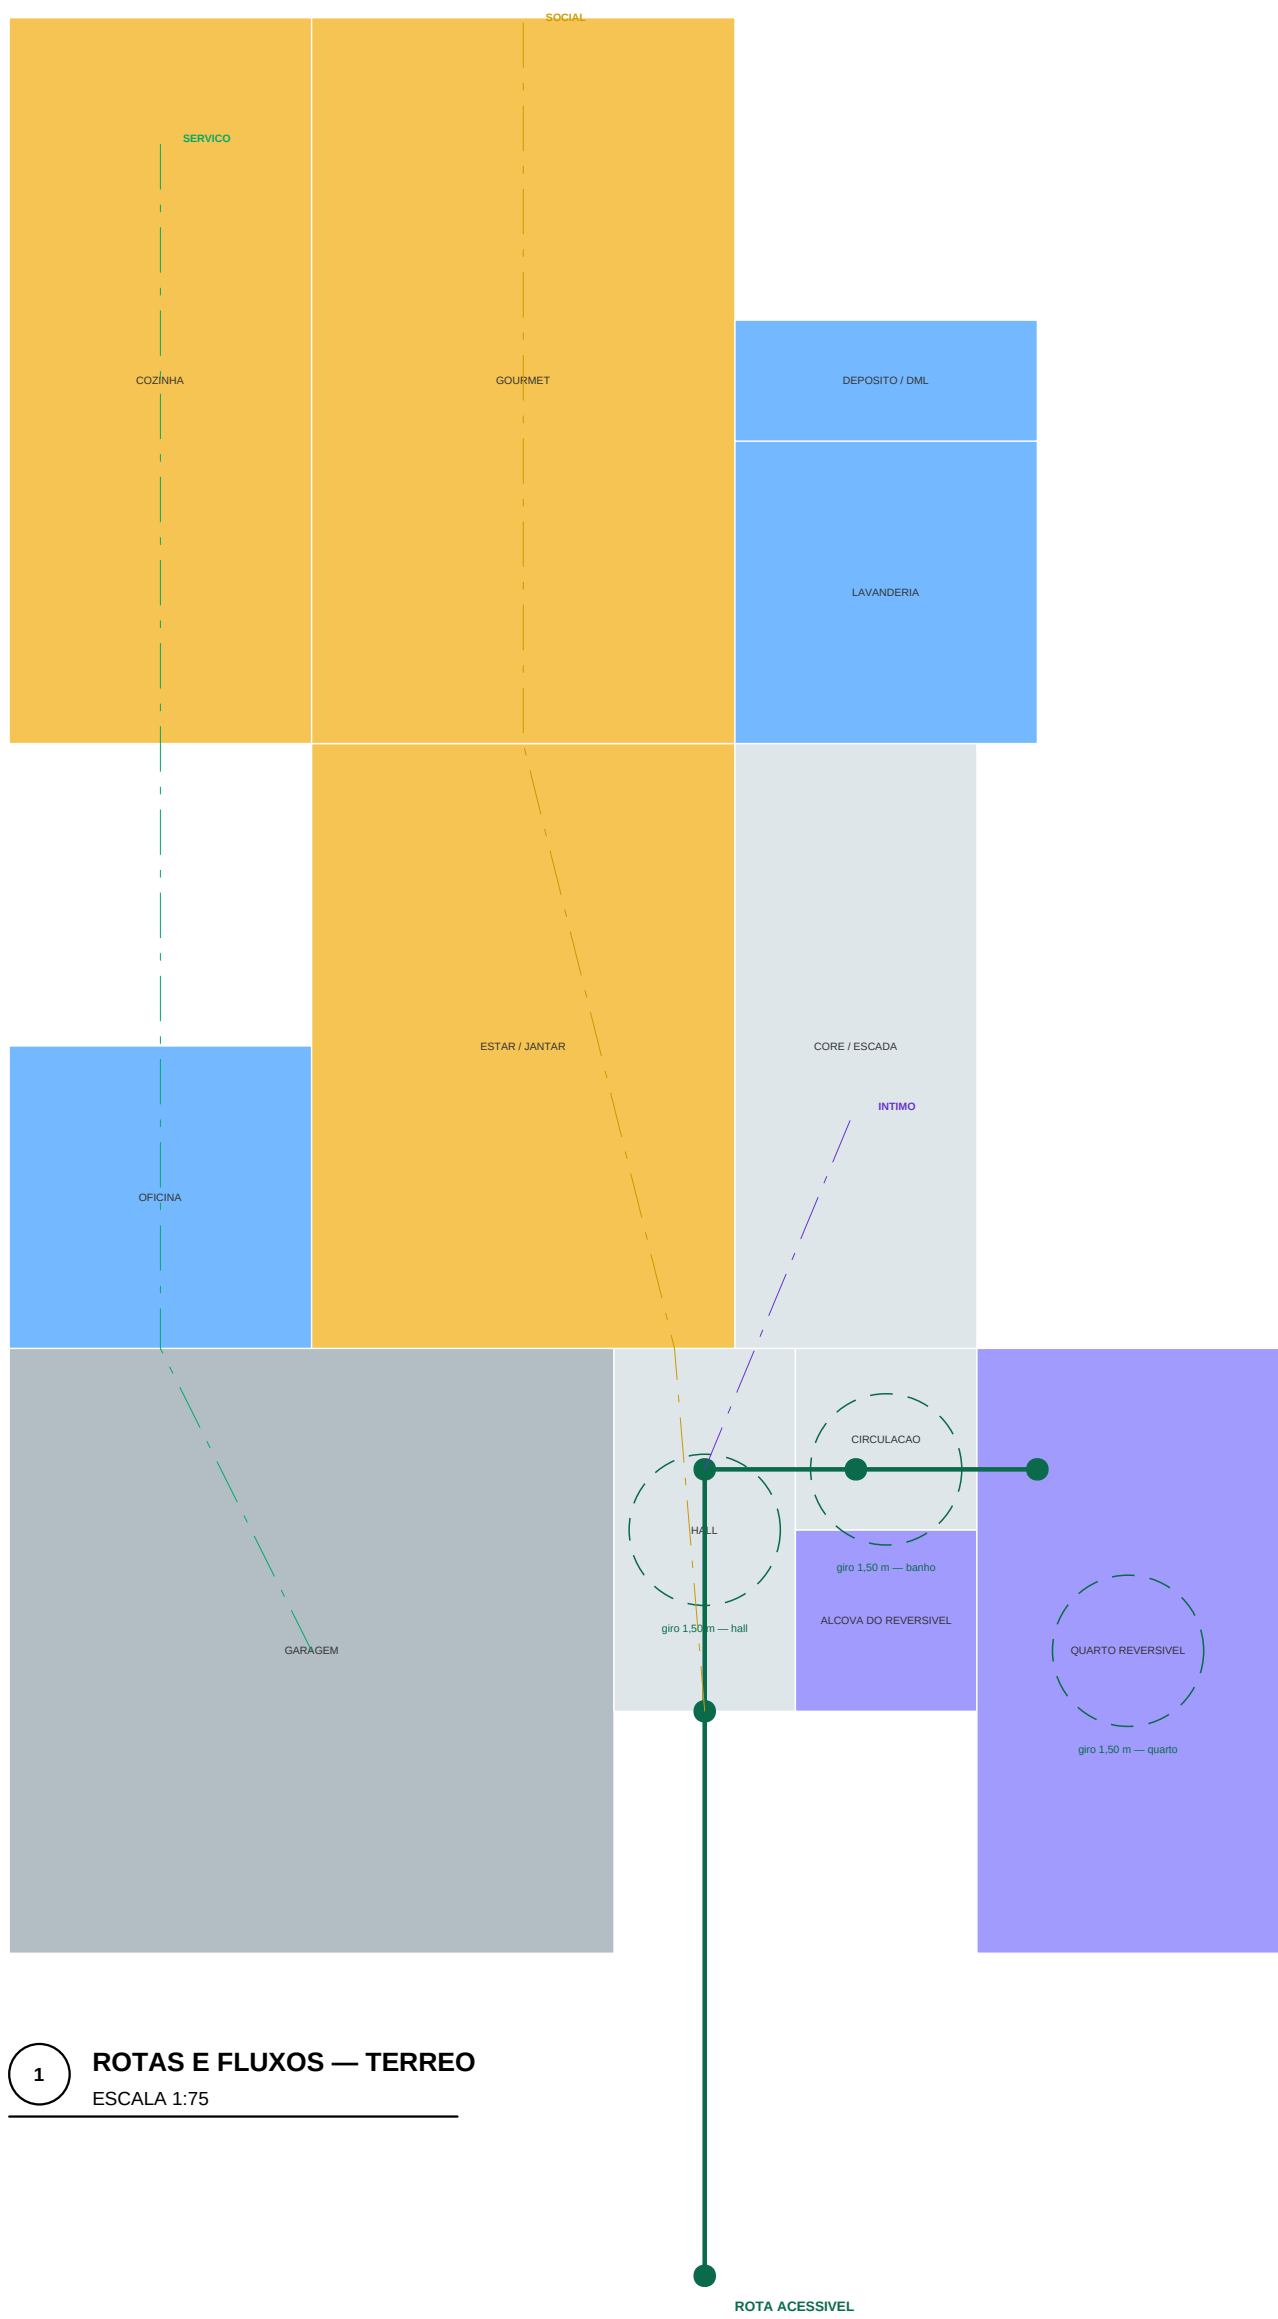


1 ROTAS E FLUXOS — TERREO
ESCALA 1:75

VERIFICACAO NBR 9050

ITEM	EXISTENTE	PROJETO	
Visão livre de porta	800 mm	940 mm (prof. de 900)	OK
Circuito de giro 360 graus	1.500 mm	hall, banheiro e quarto	OK
Desnível sem rampas	até 5 mm	soluções niveladas	OK
Largura de circulação	900 mm	1.800 mm no hall	OK
Barra de apoio	relevo no piso	instalada no PTE 1 e PTE 2	OK
Barreira acústica	altura livre 730 mm	sem barreiras sob a calha	OK
Contraste e interruptor	600 a 1.000 mm	a definir no detalhe	pendente

FLUXOS — SEPARACAO DE CIRCUITOS

CIRCUITO	PERCURSO	CRIÇA O SOCIAL?
Serviço	garagem → oficina → lavanderia → cozinha → despensa	NÃO
Social	entrada → hall → estar → gourmet → alameda → piscina	—
Área de lazer	hall → circulação → barbeque social (quarto reversível) (por outro projeto)	NÃO
Área de estudo	hall → sala → hall superior → suíte	NÃO
Área de carga	cozinha → despensa → reserv. hall	NÃO

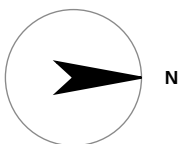

- NOTAS
- * Rota acessível do passeio ao quarto reversível e ao banheiro social.
 - * Circuito de giro de 1.500 mm verificado nos pontos de manobra.
 - * Porta de correr de 900 mm no banheiro social e área de varanda.
 - * Reforço para barra de apoio instalada antes do fechamento das placas.

PROJETO PORTO REAL

RESIDENCIA UNIFAMILIAR (MANSÃO - AM) | SOUZA TATIANA-PS

PROJETO ARQUITETONICO

ACESSIBILIDADE E FLUXOS

BASE GEOMETRICA Linha Consolidada ISO 9122 (previável) UNIDADE MESTRE: mm	ESCALA 1:75 FORMATO A1 MILHA 955/000000	EMISSÃO ESTUDO PRELIMINAR R56 NÃO LIBERADO PARA OBRA SEM ART / RNT	PROVA 17 DE 48 REVISOES
--	---	---	--------------------------------------