
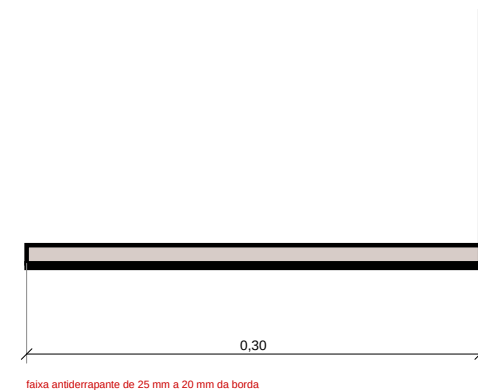
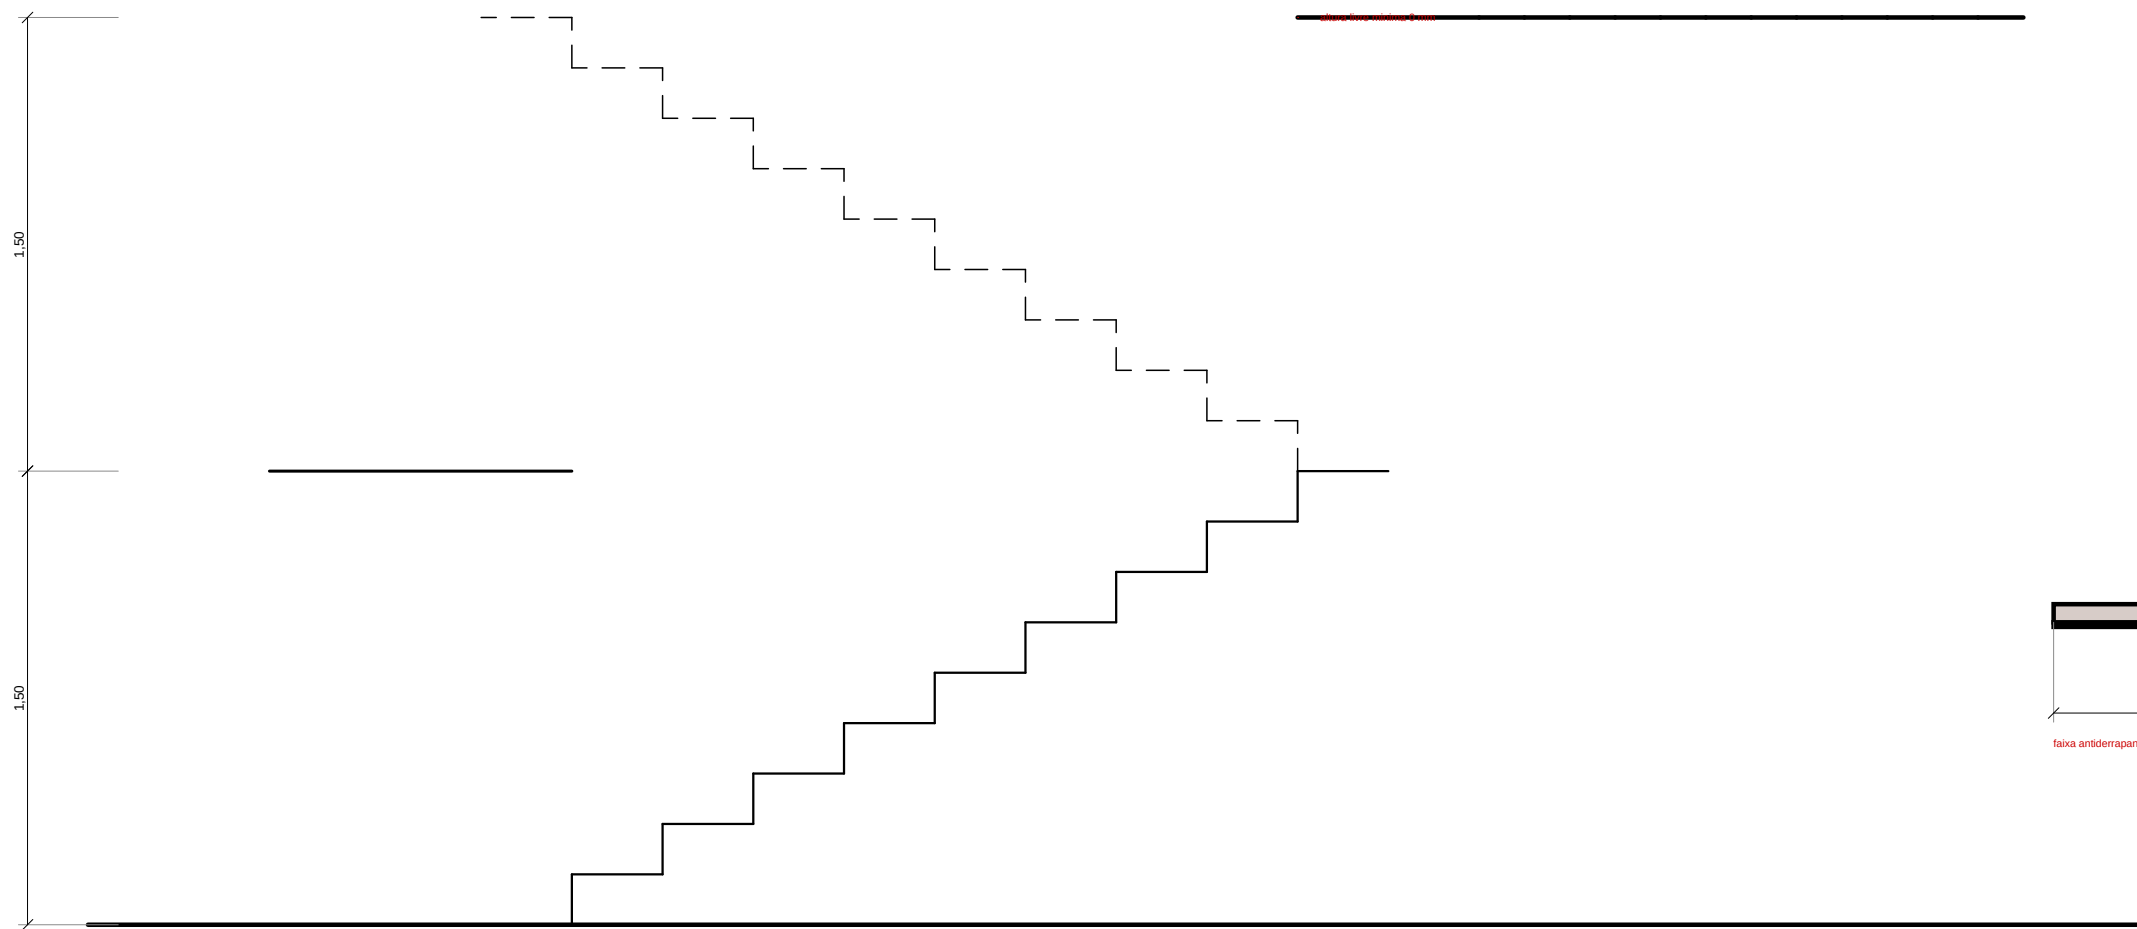


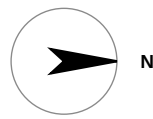

espelho fechado (NBR 9050)

chapa 80x80x3 3 mm + preenchido 90x100

## 1 PLANTA DA ESCADA

ESCALA 1:25

### VERIFICACAO DA ESCADA

| ITEM                  | PROPOSTO      | NORMA                                                   |         |
|-----------------------|---------------|---------------------------------------------------------|---------|
| Espelho               | 186,67 mm     | 18 a 18 cm (NBR 9077)                                   | OK      |
| Piso                  | 300 mm        | min 28 cm                                               | OK      |
| Bondex (2h + g)       | 633,3 mm      | 600 a 650 mm                                            | OK      |
| Largura útil do lance | 1000 mm       | min 1.200 mm (para coberturas) e 1.300 mm (para rampas) | OK      |
| Platamar              | 1000 mm       | min largura do lance                                    | OK      |
| Altura livre mínima   | 0 mm          | min 2100 mm                                             | REVISAR |
| Guarda-corpo          | 1100 mm       | min 1.200 mm (NBR 14738)                                | OK      |
| Corrimão              | 920 a 1000 mm | Acima 92 cm e 10 cm (NBR 9050)                          | OK      |
| Espelho fechado       | sem           | conformidade com esta norma                             | OK      |
| Desnível verificado   | 3000 mm       | 18 a 186,67 mm                                          | OK      |

### O QUE A PLANTA NAO MOSTRA

| QUESTAO                                                | RESPOSTA   |
|--------------------------------------------------------|---|
| Por que o primeiro espelho sobre o y é 18,67?          | o primeiro espelho sobre o y é 18,67 mm, com 1.000 mm de altura livre — visto que a altura da cobertura do primeiro lance é 18,67 mm.      |
| Por que a verificação da altura livre é bidimensional? | altura livre da escada e o único critério que não aparece em planta horizontal, dependendo da cor da escada e da cor do que há acima dela. |
| O que há sob o segundo lance?                          | intergelo com altura útil variável, dimensionado como amarrado (NBR 9050) — mas a circulação tem espaço livre.                             |
| Por que espelho fechado?                               | alguma verificação precisa a partir do pé de quem usa degrau ou sem mobilidade reduzida (NBR 9050).                                        |
| Por que corrimão duplo?                                | 920 mm para adulto e 700 mm para criança, em caso de escada aberta para a sala, o segundo corrimão é o que realmente se usa.               |

### NOTAS

- 18 espelhos de 186,67 mm e piso de 300 mm. Bondex 2h + g = 633,3 mm (linha recomendada 600 a 650).
- Altura livre mínima 2100 mm (NBR 9077), verificada diagonal a degrau contra a laje e o vazio acima.
- Guarda-corpo 1100 mm, corrimão duplo em 920 e 700 mm (NBR 9050).
- dois perfis U 200 laterais com degraus em chapa aluminada 3 mm.

## PROJETO PORTO REAL

RESIDENCIA UNIFAMILIAR (MARIAUS - AM) | 500x700mm-PS

PROJETO ARQUITETONICO

### ESCALA — DESENHO EXECUTIVO

| BASE GEOMETRICA     | ESCALA            | EMISSAO                | PROJECION     |
|---------------------|-------------------|------------------------|---------------|
| Unidade Consolidada | indicada          | ESTUDIO PRELIMINAR R56 |               |
| Projeto (previsão)  | FORMATO A1        | NAO LIBERADO PARA OBRA | 25            |
| Unidade (previsão)  | MAQUETA 600x900mm | SEM ART / RNT          | 06-48 REV 006 |