


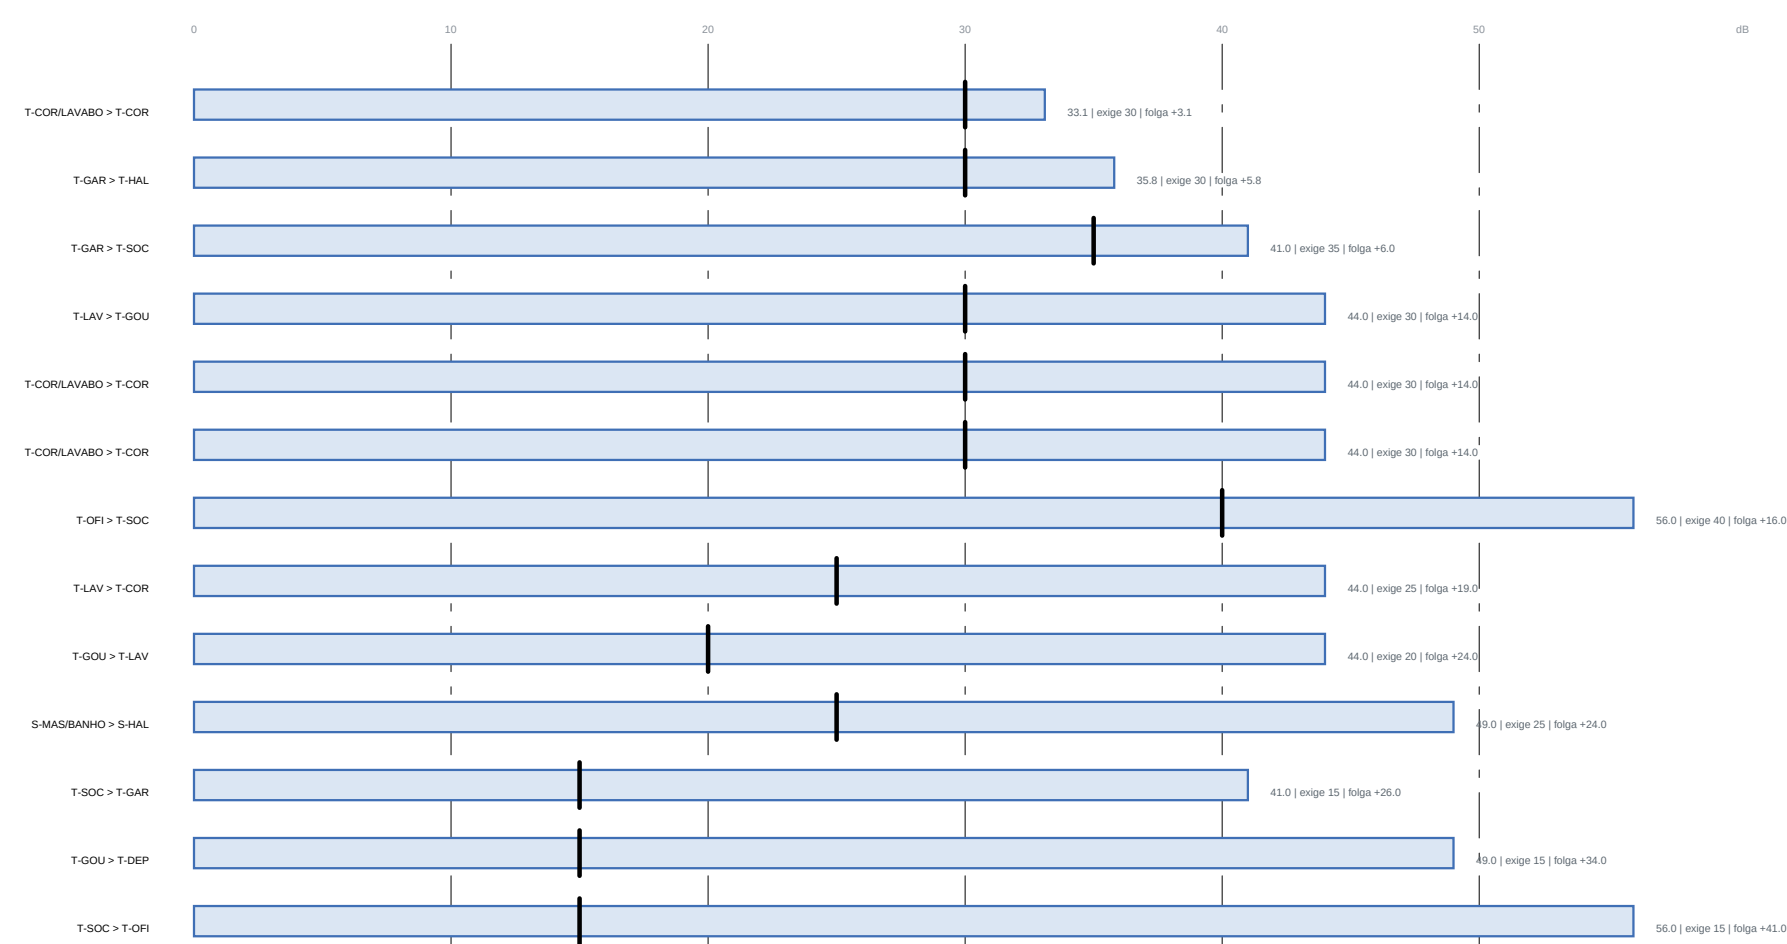

tanta = isolamento obtido; traca vertical = exigido (nível da fonte menos limite do receptor, NBR 10152)

O QUE MUDOU EM R52

ONCE	ANTES	DEPOIS	POB-QUE
Barrão campoforteiro - hall de entrada	porta de corral (1m 11) — conjunto de 20,2 dB	parede CISA, 41 dB	o acesso de visita passou para a circulação
Barrão campoforteiro - quarto feminino	porta aos 20 — conjunto de 25,1 dB, esqda 35	parede CISA, 41 dB	era a por passagem da casa, e não era a visita!
Hall 3 gangster	porta aos — 20,6 dB, esqda 30	PSE isolada, 35 — 35,8 dB	porta entre gangster e casa tem muita ruído para ser música
Barrão campoforteiro - circulação	nao havia porta	PSE isolada, 35 — 37,6 dB, esqda 35	único acesso do barrão, e abre para fora
Bou de chaves	encostado na parede do hall	correria horizontal, sob a janela alta	consequência da porta nova, e agora das 900 mm de seu regradado a primeira borda

TABELAS ADOTADAS

ITEM	VALOR	FONTE
Fonete: sacia vendida	75 (R\$)	prática corrente de contabilidade
Fonete: lico de chocolate	70 (R\$)	prática corrente de contabilidade
Fonete: cocotinha e gourmet	75 (R\$)	prática corrente de contabilidade
Fonete: ester e jantar	70 (R\$)	prática corrente de contabilidade
Fonete: ganjagem	75 (R\$)	prática corrente de contabilidade
Fonete: máquina de lavar e secar	70 (R\$)	prática corrente de contabilidade
Fonete: oficina	60 (R\$)	prática corrente de contabilidade
Limite: teatro	40 (R\$)	NBR 13132-2017 (circulação e entrada adossados)
Limite: circulações	40 (R\$)	NBR 13132-2017 (circulação e entrada adossados)
Limite: cocotinha	40 (R\$)	NBR 13132-2017 (circulação e entrada adossados)
Limite: depósito	50 (R\$)	NBR 13132-2017 (circulação e entrada adossados)
Limite: dormitório	20 (R\$)	NBR 13132-2017 (circulação e entrada adossados)
Limite: entrada	40 (R\$)	NBR 13132-2017 (circulação e entrada adossados)
Limite: sala	40 (R\$)	NBR 13132-2017 (circulação e entrada adossados)
Limite: garagem	50 (R\$)	NBR 13132-2017 (circulação e entrada adossados)
Limite: office	40 (R\$)	NBR 13132-2017 (circulação e entrada adossados)
Limite: oficina	50 (R\$)	NBR 13132-2017 (circulação e entrada adossados)
Limite: serviço	50 (R\$)	NBR 13132-2017 (circulação e entrada adossados)
Porta: acústica	R\$ 20,00	tabela de mercado declarada
Porta: corre	R\$ 20,00	tabela de mercado declarada
Porta: oca	R\$ 20,00	tabela de mercado declarada
Porta: sólida	R\$ 20,00	tabela de mercado declarada
Porta: sólida vedada	R\$ 30,00	tabela de mercado declarada

NOTAS

- Esta prancha existe porque o proprietário perguntou e que 103 verificações não sabem responder: quem entra na casa ouve o chuveiro do banheiro da entrada?

* Ouvia. A parede era boa (Rw 44) e a porta era de correr (Rw 25); o conjunto entregava 20 dB. Em acústica o elo fraco DOMINA — não se faz média aritmética de isolamento, se soma energia que passa.

- Isolamento só se exige ENTRE zonas. Dentro da fita social o ruído não é defeito, é o programa.

* D adotado igual ao R composto (simplificação declarada). Isto é pre-verificação de projeto, não ensaio de campo da NBR 15575-3.

PROJETO PORTO REAL RESIDENCIA UNIFAMILIAR P1 60x40,25 - IM1 (5.035 TAPADA, 0,9)			
PROJETO DE ARQUITETONICO			
DESEMPENHO ACUSTICO ENTRE AMBIENTES			
BASE GEOMETRICA Lista Consolidada (90x152 (envase)) ANEXO MESTRE (0,6)	ESCALA s/ escala FORMATO A1 NAUHA 600/300/200	EMISSAO ESTUDO PRELIMINAR R56 NAO LIBERADO PARA OBRA SEM ART. 1.887	PROVA 39 de 42 RE R56