



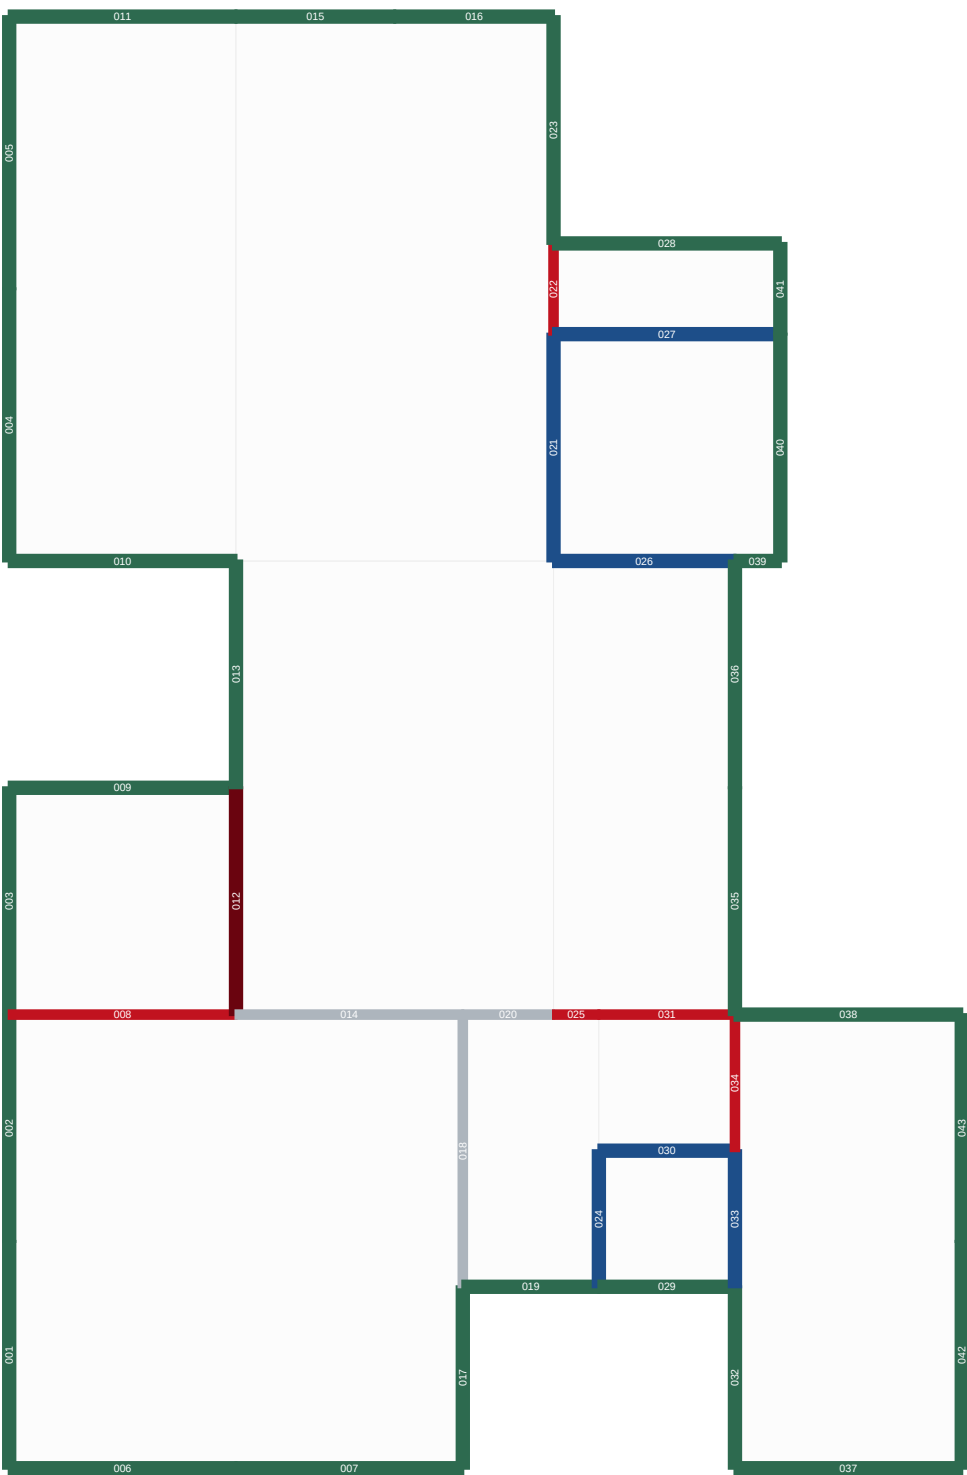

1 PAGINACAO — TERREO  
ESCALA 1:100

QUANTITATIVO DE PANEIS E MONTANTES

| FAMILIA | PANEIS | MONTANTES | MT de perfil | COMPOSICAO                                                 |
|---------|--------|-----------|--------------|------------------------------------------------------------|
| PA-1    | 14     | 63        | 183,8        | dupla chapa 12,5 + montante 48 cr 16 + dupla chapa 12,5    |
| PA-2    | 1      | 6         | 15,6         | dupla chapa 12,5 + perfil isolante + montante 70 cr 16 80  |
| PE-1    | 47     | 253       | 837,8        | linhas 32 + 80 cr 50 (SD enq) + montante 90 cr 16 90 +     |
| PA-3    | 6      | 26        | 75,4         | gesso 60 12,5 + montante 90 cr 16 90 + gesso 12,5 + reboco |
| PA-1    | 3      | 16        | 41,8         | gesso 12,5 + montante 70 cr 16 90 + gesso 12,5             |
| TOTAL   | 71     | 367       | 954,2        |                                                            |

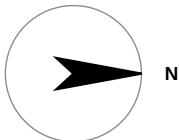

EXTRATO DA LISTA DE PANEIS (26 de 71)

| CODIGO | FAMILIA | LARGO (mm) | ALT (mm) | MONT. | PRV |
|--------|---------|------------|----------|-------|-----|
| PT-001 | PE-1    | 3000       | 2000     | 6     | T   |
| PT-002 | PE-1    | 3000       | 2000     | 6     | T   |
| PT-003 | PE-1    | 3000       | 2000     | 6     | T   |
| PT-004 | PE-1    | 3000       | 2000     | 7     | T   |
| PT-005 | PE-1    | 3000       | 2000     | 7     | T   |
| PT-006 | PE-1    | 3000       | 2000     | 6     | T   |
| PT-007 | PE-1    | 3000       | 2000     | 6     | T   |
| PT-008 | PA-1    | 3000       | 2000     | 6     | T   |
| PT-009 | PE-1    | 3000       | 2000     | 6     | T   |
| PT-010 | PE-1    | 3000       | 2000     | 6     | T   |
| PT-011 | PE-1    | 3000       | 2000     | 6     | T   |
| PT-012 | PA-2    | 3000       | 2000     | 6     | T   |
| PT-013 | PE-1    | 3000       | 2000     | 6     | T   |
| PT-014 | PA-1    | 3000       | 2000     | 6     | T   |
| PT-015 | PE-1    | 2100       | 2000     | 4     | T   |
| PT-016 | PE-1    | 2100       | 2000     | 4     | T   |
| PT-017 | PE-1    | 2400       | 2000     | 5     | T   |
| PT-018 | PA-1    | 3000       | 2000     | 7     | T   |
| PT-019 | PE-1    | 1800       | 2000     | 4     | T   |
| PT-020 | PA-1    | 1200       | 2000     | 3     | T   |
| PT-021 | PA-1    | 3000       | 2000     | 6     | T   |
| PT-022 | PA-1    | 1200       | 2000     | 3     | T   |
| PT-023 | PE-1    | 3000       | 2000     | 6     | T   |
| PT-024 | PA-1    | 1800       | 2000     | 4     | T   |
| PT-025 | PA-1    | 600        | 2000     | 2     | T   |
| PT-026 | PA-1    | 2400       | 2000     | 6     | T   |

- NOTAS
- \* Painéis limitados a 3000 mm por manuseio e transporte.
  - \* Montantes a cada 600 mm, 400 mm onde cabulo ou revestimento exigir.
  - \* Não fixar pica entre em moldes sem código, largura, altura, espessura, material e revest.
  - \* Numeração por pavimento, a família define a composição interna do painel.

PROJETO PORTO REAL

RESIDENCIA UNIFAMILIAR (MANAUS - AM) | SOUZA TATIANA-PS

PROJETO ARQUITETONICO

PAGINACAO DE PANEIS — LIGHT STEEL FRAME

|                                                                                    |                                                                  |                                                                               |                                       |
|------------------------------------------------------------------------------------|------------------------------------------------------------------|-------------------------------------------------------------------------------|---------------------------------------|
| BASE GEOMETRICA<br>Lista Consolidada<br>psd-RS2 (previsão)<br>UNIDADE: METROS - MM | ESCALA<br><b>1:100</b><br>FORMATO: A1<br>MILIMETROS: 600/300/300 | EMISSAO<br>ESTUDIO PRELIMINAR RS2<br>TUDO LIBERADO PARA OBRA<br>SEM ART / RNT | PROJETA<br><b>18</b><br>06-48 REV 003 |
|------------------------------------------------------------------------------------|------------------------------------------------------------------|-------------------------------------------------------------------------------|---------------------------------------|