


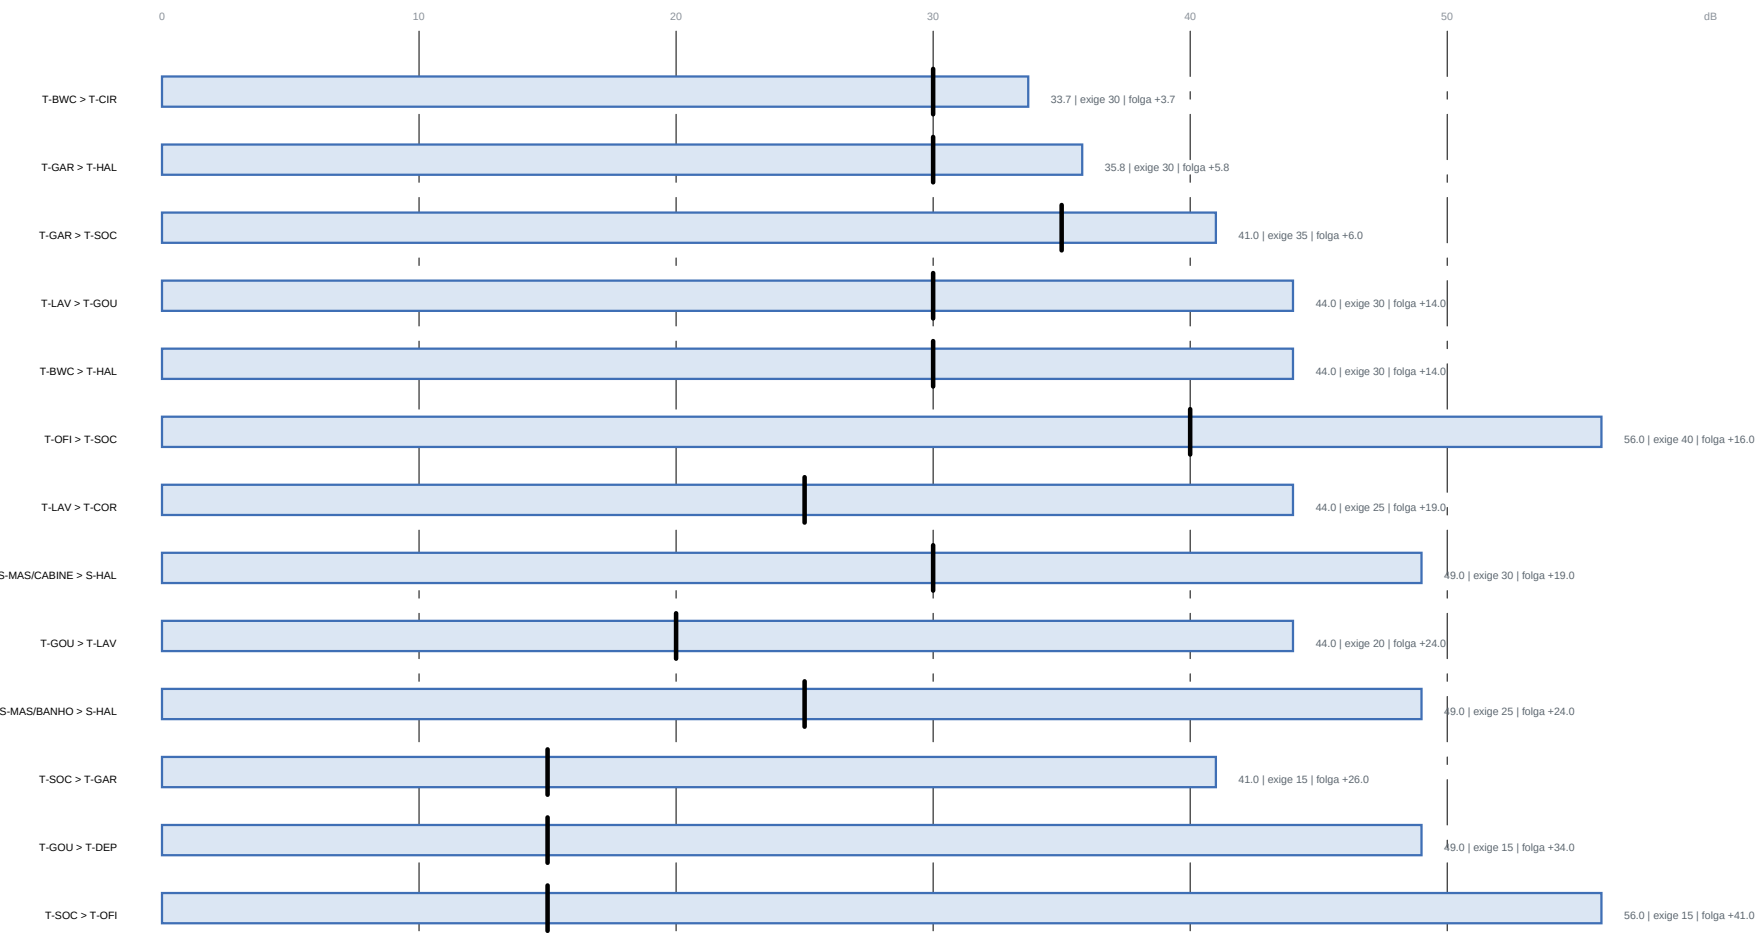

Barra = isolamento obtido; traço vertical = exigência (valor da fonte menos limite do receptor, NBR 15102)

O QUE MUDOU EM R\$2

ONDE	ANTES	DEPOIS	POR QUE
Banho compartilhado + hall de entrada	porta de correr (Pw 22) — conjunto de 20,2 dB	parede CEGSA, 44 dB	o acesso de volta passou para a circulação
Banho compartilhado + quarto eventual	porta com (Pw 22) — conjunto de 23,5 dB, exigia 25	parede CEGSA, 44 dB	era a por passagem da casa, e não era a saída
Hall + garagem	porta seca — 36,9 dB, exigia 35	PDS lanta vedada — 36,9 dB	porta entre garagem e casa tem lanta lanta para ser usada
Banho compartilhado + circulação	não havia porta	PDS lanta vedada — 33,7 dB, exigia 25	único acesso do banho, e abria para fora
Bloco do chuveiro	encostado na parede do hall	canto arredado, toldo e janela alta	consequência da porta nova, a regra dos 900 cm de box obrigou a primeira tentativa

TABELAS ADOTADAS

ITEM	VALOR	FONTE
Fonte: caixa sanitária	75 dB(A)	prática corrente de acústica
Fonte: bloco do chuveiro	75 dB(A)	prática corrente de acústica
Fonte: cozinha e gourmet	75 dB(A)	prática corrente de acústica
Fonte: sala e jantar	75 dB(A)	prática corrente de acústica
Fonte: garagem	75 dB(A)	prática corrente de acústica
Fonte: máquina de lavar e secar	75 dB(A)	prática corrente de acústica
Fonte: oficina	85 dB(A)	prática corrente de acústica
Limite: banho	45 dB(A)	NBR 15102:2017 (circulação e entrada adiabática)
Limite: circulação	45 dB(A)	NBR 15102:2017 (circulação e entrada adiabática)
Limite: cozinha	45 dB(A)	NBR 15102:2017 (circulação e entrada adiabática)
Limite: depósito	55 dB(A)	NBR 15102:2017 (circulação e entrada adiabática)
Limite: dormitório	35 dB(A)	NBR 15102:2017 (circulação e entrada adiabática)
Limite: entrada	45 dB(A)	NBR 15102:2017 (circulação e entrada adiabática)
Limite: estar	45 dB(A)	NBR 15102:2017 (circulação e entrada adiabática)
Limite: garagem	55 dB(A)	NBR 15102:2017 (circulação e entrada adiabática)
Limite: office	45 dB(A)	NBR 15102:2017 (circulação e entrada adiabática)
Limite: oficina	55 dB(A)	NBR 15102:2017 (circulação e entrada adiabática)
Limite: serviço	55 dB(A)	NBR 15102:2017 (circulação e entrada adiabática)
Fonte: academia	Pw 25 dB	Nota de mercado declarada
Fonte: cinema	Pw 25 dB	Nota de mercado declarada
Fonte: sala	Pw 25 dB	Nota de mercado declarada
Fonte: sala de	Pw 25 dB	Nota de mercado declarada
Fonte: sala de visita	Pw 30 dB	Nota de mercado declarada

NOTAS

1 Esta planilha está pensada para o proprietário perguntar e que 100 verificações não sabem responder: quem entra na casa ouve o chuveiro do banheiro da entrada?

2 Ouviu. A parede era boa (Pw 42), mas ali é a porta era do corredor (Pw 22), o conjunto entregava 20 dB. Em acústica é o bloco DOMINA — não se faz média aritmética do isolamento, se soma energia que passa.

3 Isolamento se se exige ENTRE zonas. Dentro da file social o ruído não é definido, é o programa.

4 O aditivo igual ao 10 cm (propriedade declarada). Não é pre-verificação de projeto, mas erro do corpo da NBR 15107-3.

PROJETO PORTO REAL

RESIDENCIA UNIFAMILIAR (MANSÃO - AM) | SOBR TATIANA-PS

PROJETO ARQUITETONICO

DESEMPENHO ACUSTICO ENTRE AMBIENTES

BASE GEOMETRICA	ESCALA	EMISSAO	PROVA
Lista Consolidada	s/ escala	ESTUDIO PRELIMINAR R\$2	
psu-R\$2 (previsível)	FORMATO A1	IMAO LIBERADO PARA OBRA	39
UNIDADE MESTRE: AM	MALHA 605/500/300	SEM ART / RNT	06-48 REV R\$2