


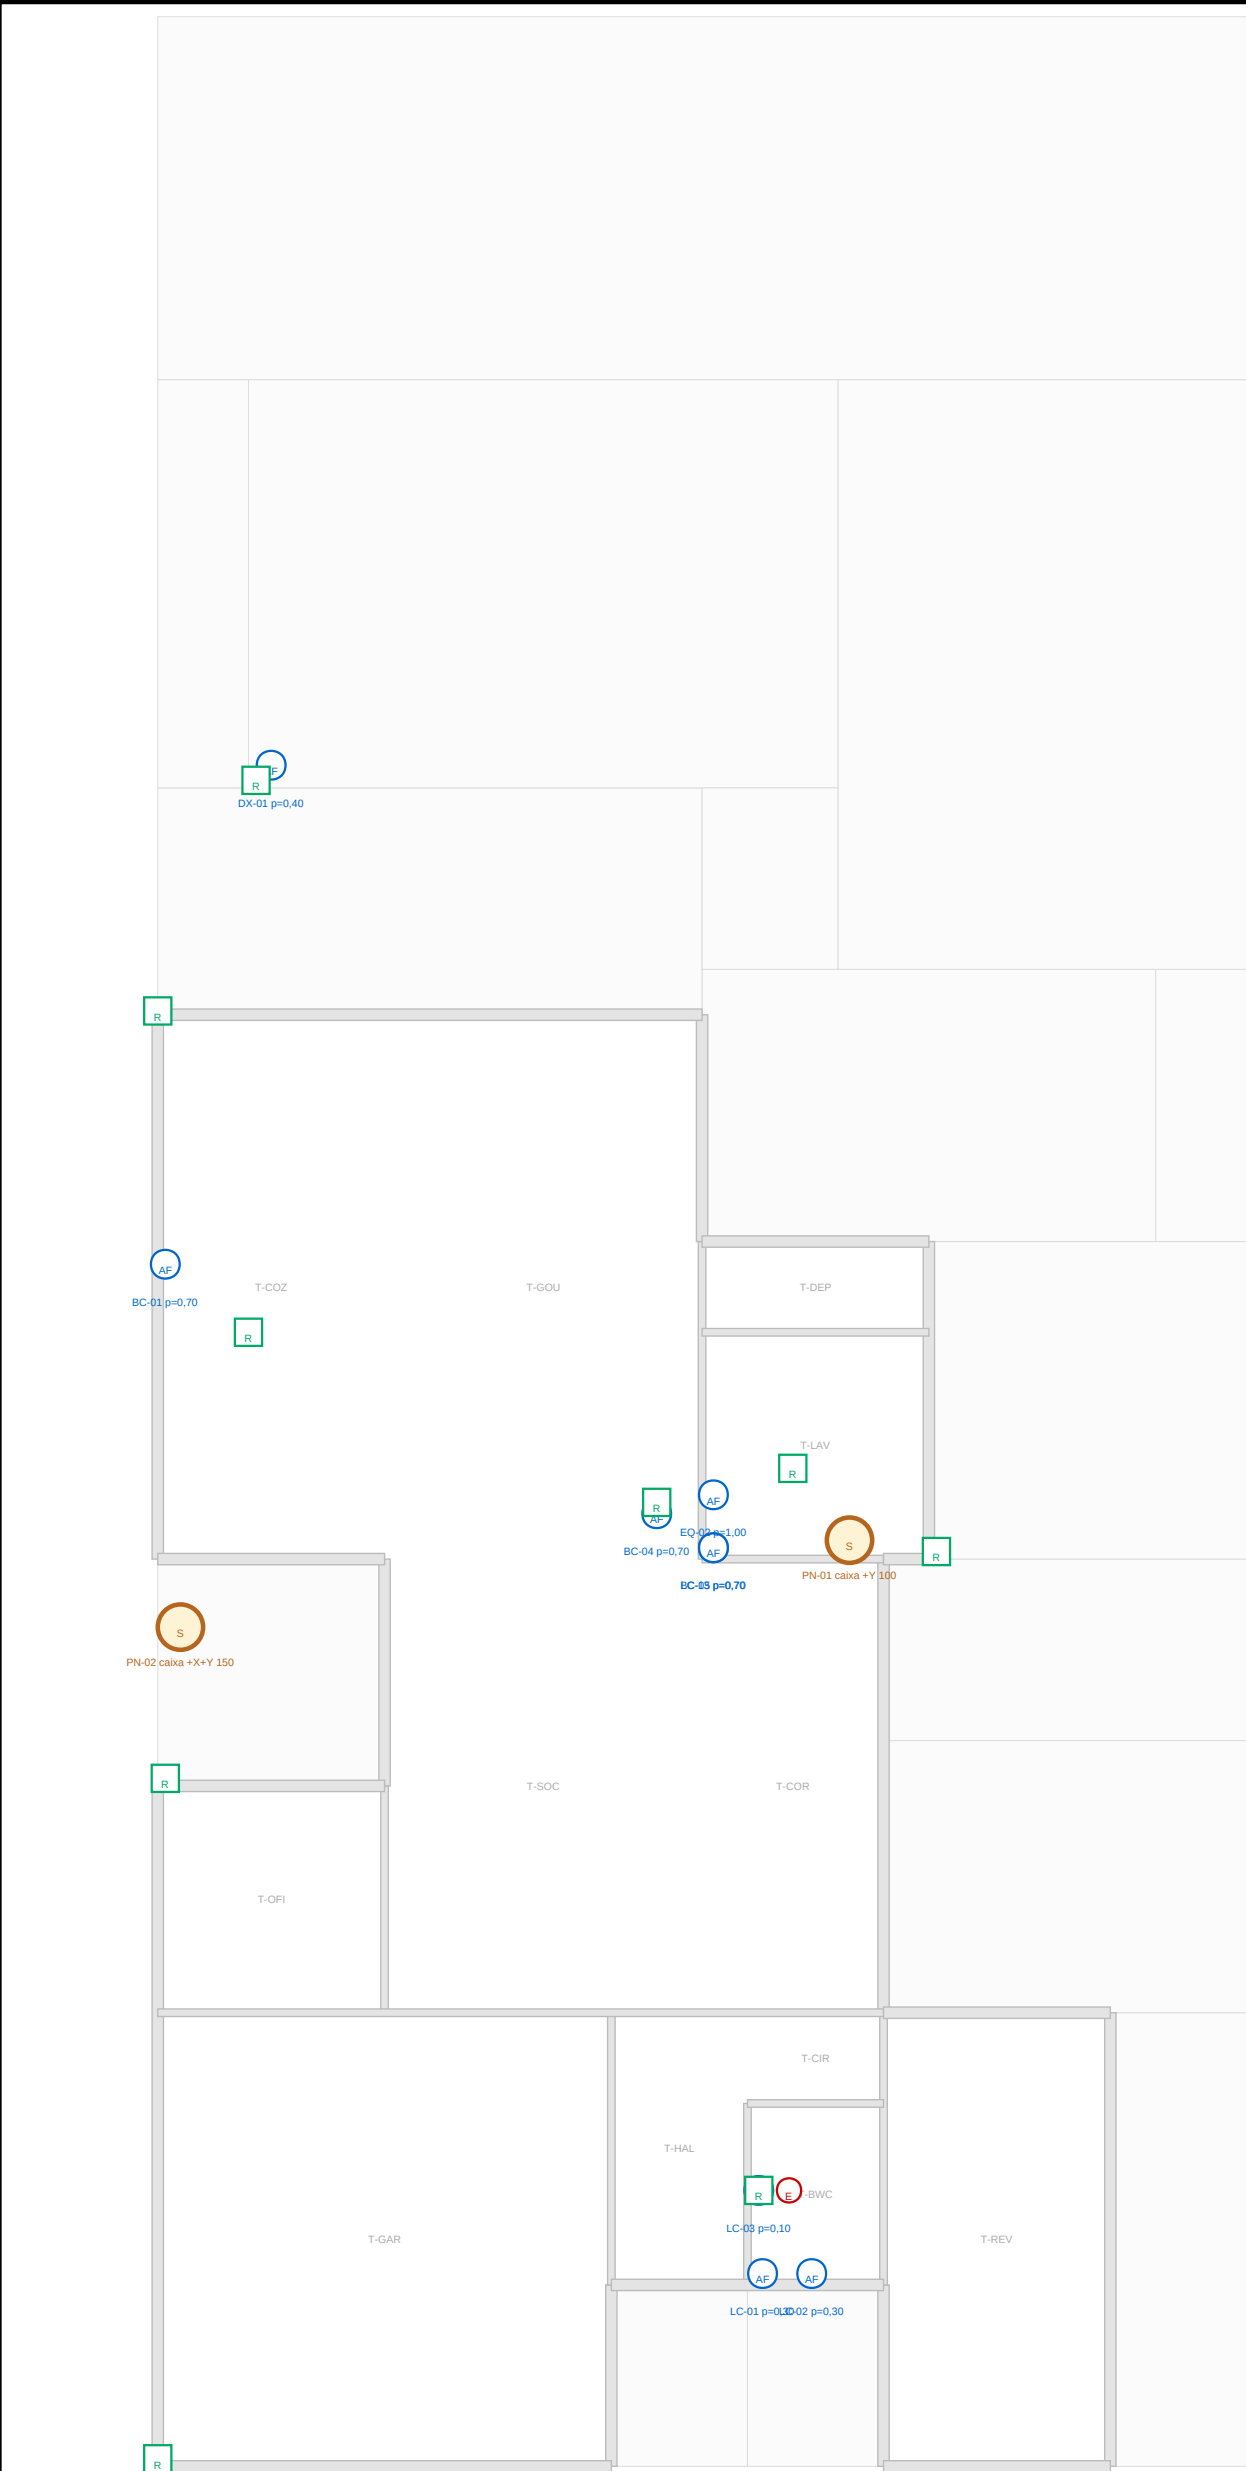


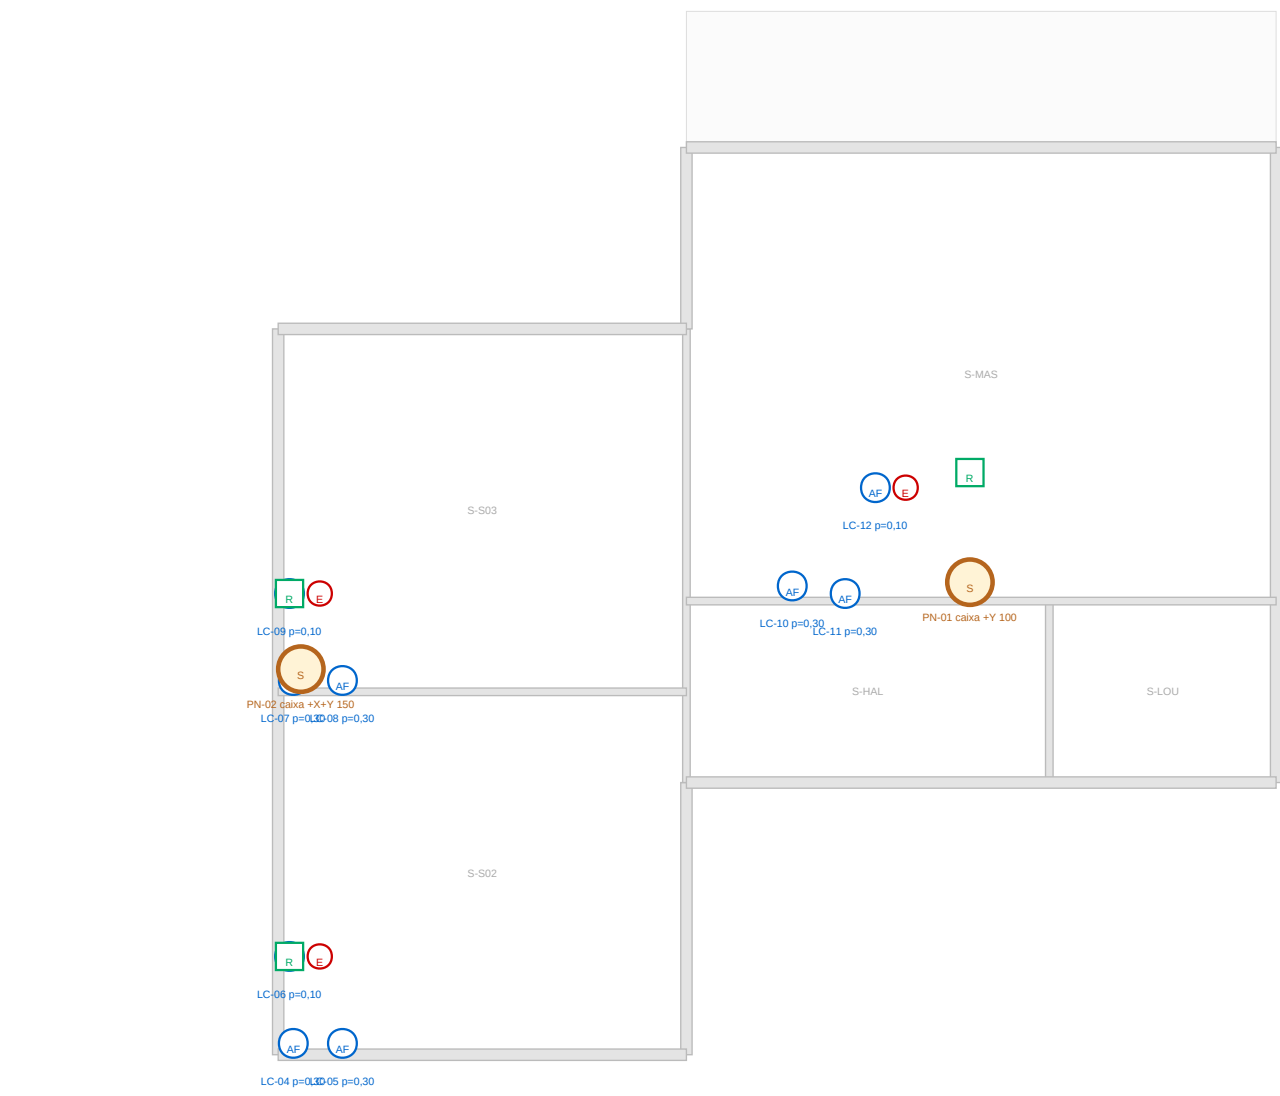

1 PONTOS HIDRAULICOS — TERREO
ESCALA 1:100

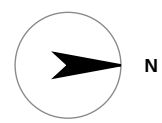

2 PONTOS HIDRAULICOS — SUPERIOR
ESCALA 1:100

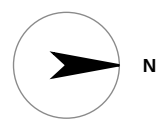

TRECHO	PECAS	PESOS	Q (L/s)	DN AGUA	V (m/s)	UMC	DN ESGOTO	REGIME
Superior	8	2.10	0.435	DN25	1.19	27	DN100	pressurizado
Terreo	9	4.80	0.884	DN25	1.81	36	DN100	gravidade
GERAL	18	7.00	0.794	DN32	1.31	33	DN100	gravidade

COD	AMB	TIPO	PESO	UMC	DN AF	DN ESG	QUENTE
LC-01	T-BWC	vaso	0.30	6	DN25	DN40	—
LC-02	T-BWC	lavatório	0.30	1	DN25	DN40	—
LC-03	T-BWC	box	0.30	2	DN25	DN40	sim
LC-04	S-SID	vaso	0.30	6	DN25	DN40	—
LC-05	S-SID	lavatório	0.30	1	DN25	DN40	—
LC-06	S-SID	box	0.30	2	DN25	DN40	sim
LC-07	S-SID	vaso	0.30	6	DN25	DN40	—
LC-08	S-SID	lavatório	0.30	1	DN25	DN40	—
LC-09	S-SID	box	0.30	2	DN25	DN40	sim

COD	AMB	TIPO	PESO	UMC	DN AF	DN ESG	QUENTE
LC-01	S-MAS	vaso	0.30	6	DN25	DN40	—
LC-02	S-MAS	lavatório	0.30	1	DN25	DN40	—
LC-03	S-MAS	box	0.30	2	DN25	DN40	sim
LC-04	T-LAV	vaso	0.70	3	DN25	DN40	—
LC-05	T-COZ	sim	0.70	3	DN25	DN40	—
LC-06	T-COZ	sim	0.70	3	DN25	DN40	—
LC-07	T-LAV	sim	0.70	3	DN25	DN40	—
LC-08	T-LAV	lavatório	1.00	3	DN25	DN40	—
LC-09	T-DPA	banho, entrada	0.40	2	DN25	DN40	—

DECISAO	CONSEQUENCIA HIDRAULICA
Chuveiro elétrico em vez de aquecimento central	peso 0.02 por chuveiro em vez de 0.40; a soma cai de 5.2 para 7.0 pesos e o alimentador de DN40 para DN32
Limite de velocidade por conforto, não por norma	DN32 elevando a soma a 2.07 m/s e 3.0 m/s e não mais DN40. Cuida alguns metros de tubo
Pressurizador no terço superior	0.5 mca por gravidade nos setores chuveiro elétrico, TC-14 entrega 12 mca
Reuso pluvial sem ligação a rede	rede de reuso e floculante separada, com cot e identificação próprias, não há ponto de conexão cruzada possível
Canal de grelhas antes da impetora	coluna + TC-11 [DN11] > TC-12 < rede, DN100 com conteúdo de 2%

NOTAS

- Água fria por metrado dos pesos (DN25) Q = 0.30 e vazante dos pesos = 0.794 L/s com 7.0 pesos.
- Alimentador DN32 a 1.32 m/s — limitado pelo conforto (2.0 m/s) não pela norma (3.0 m/s).
- Exigido por UMC (DN25) 33 UMC, tubo de queda DN100, ventilação DN80.
- Chuveiro ELA TRACO tem peso 0.02, nos 0.40 a decisão de aquecimento impede aqui como diâmetro menor em toda a casa.

PROJETO PORTO REAL

RESIDENCIA UNIFAMILIAR (MANSÃO - AM) | SOBR TATIANA-PS

PROJETO ARQUITETONICO

INSTALACOES HIDROSSANITARIAS

BASE GEOMETRICA

União Consolidada

Projeto (preliminar)

UNIDADE MESTRE: AM

ESCALA

1:100

FORMATO A1

MALHA 600/600/300

EMISSAO

ESTUDO PRELIMINAR RM

IMAGEM LIBERADA PARA OBRA

SEM ART / RNT

PROVA

26

IN-25 REV RM