


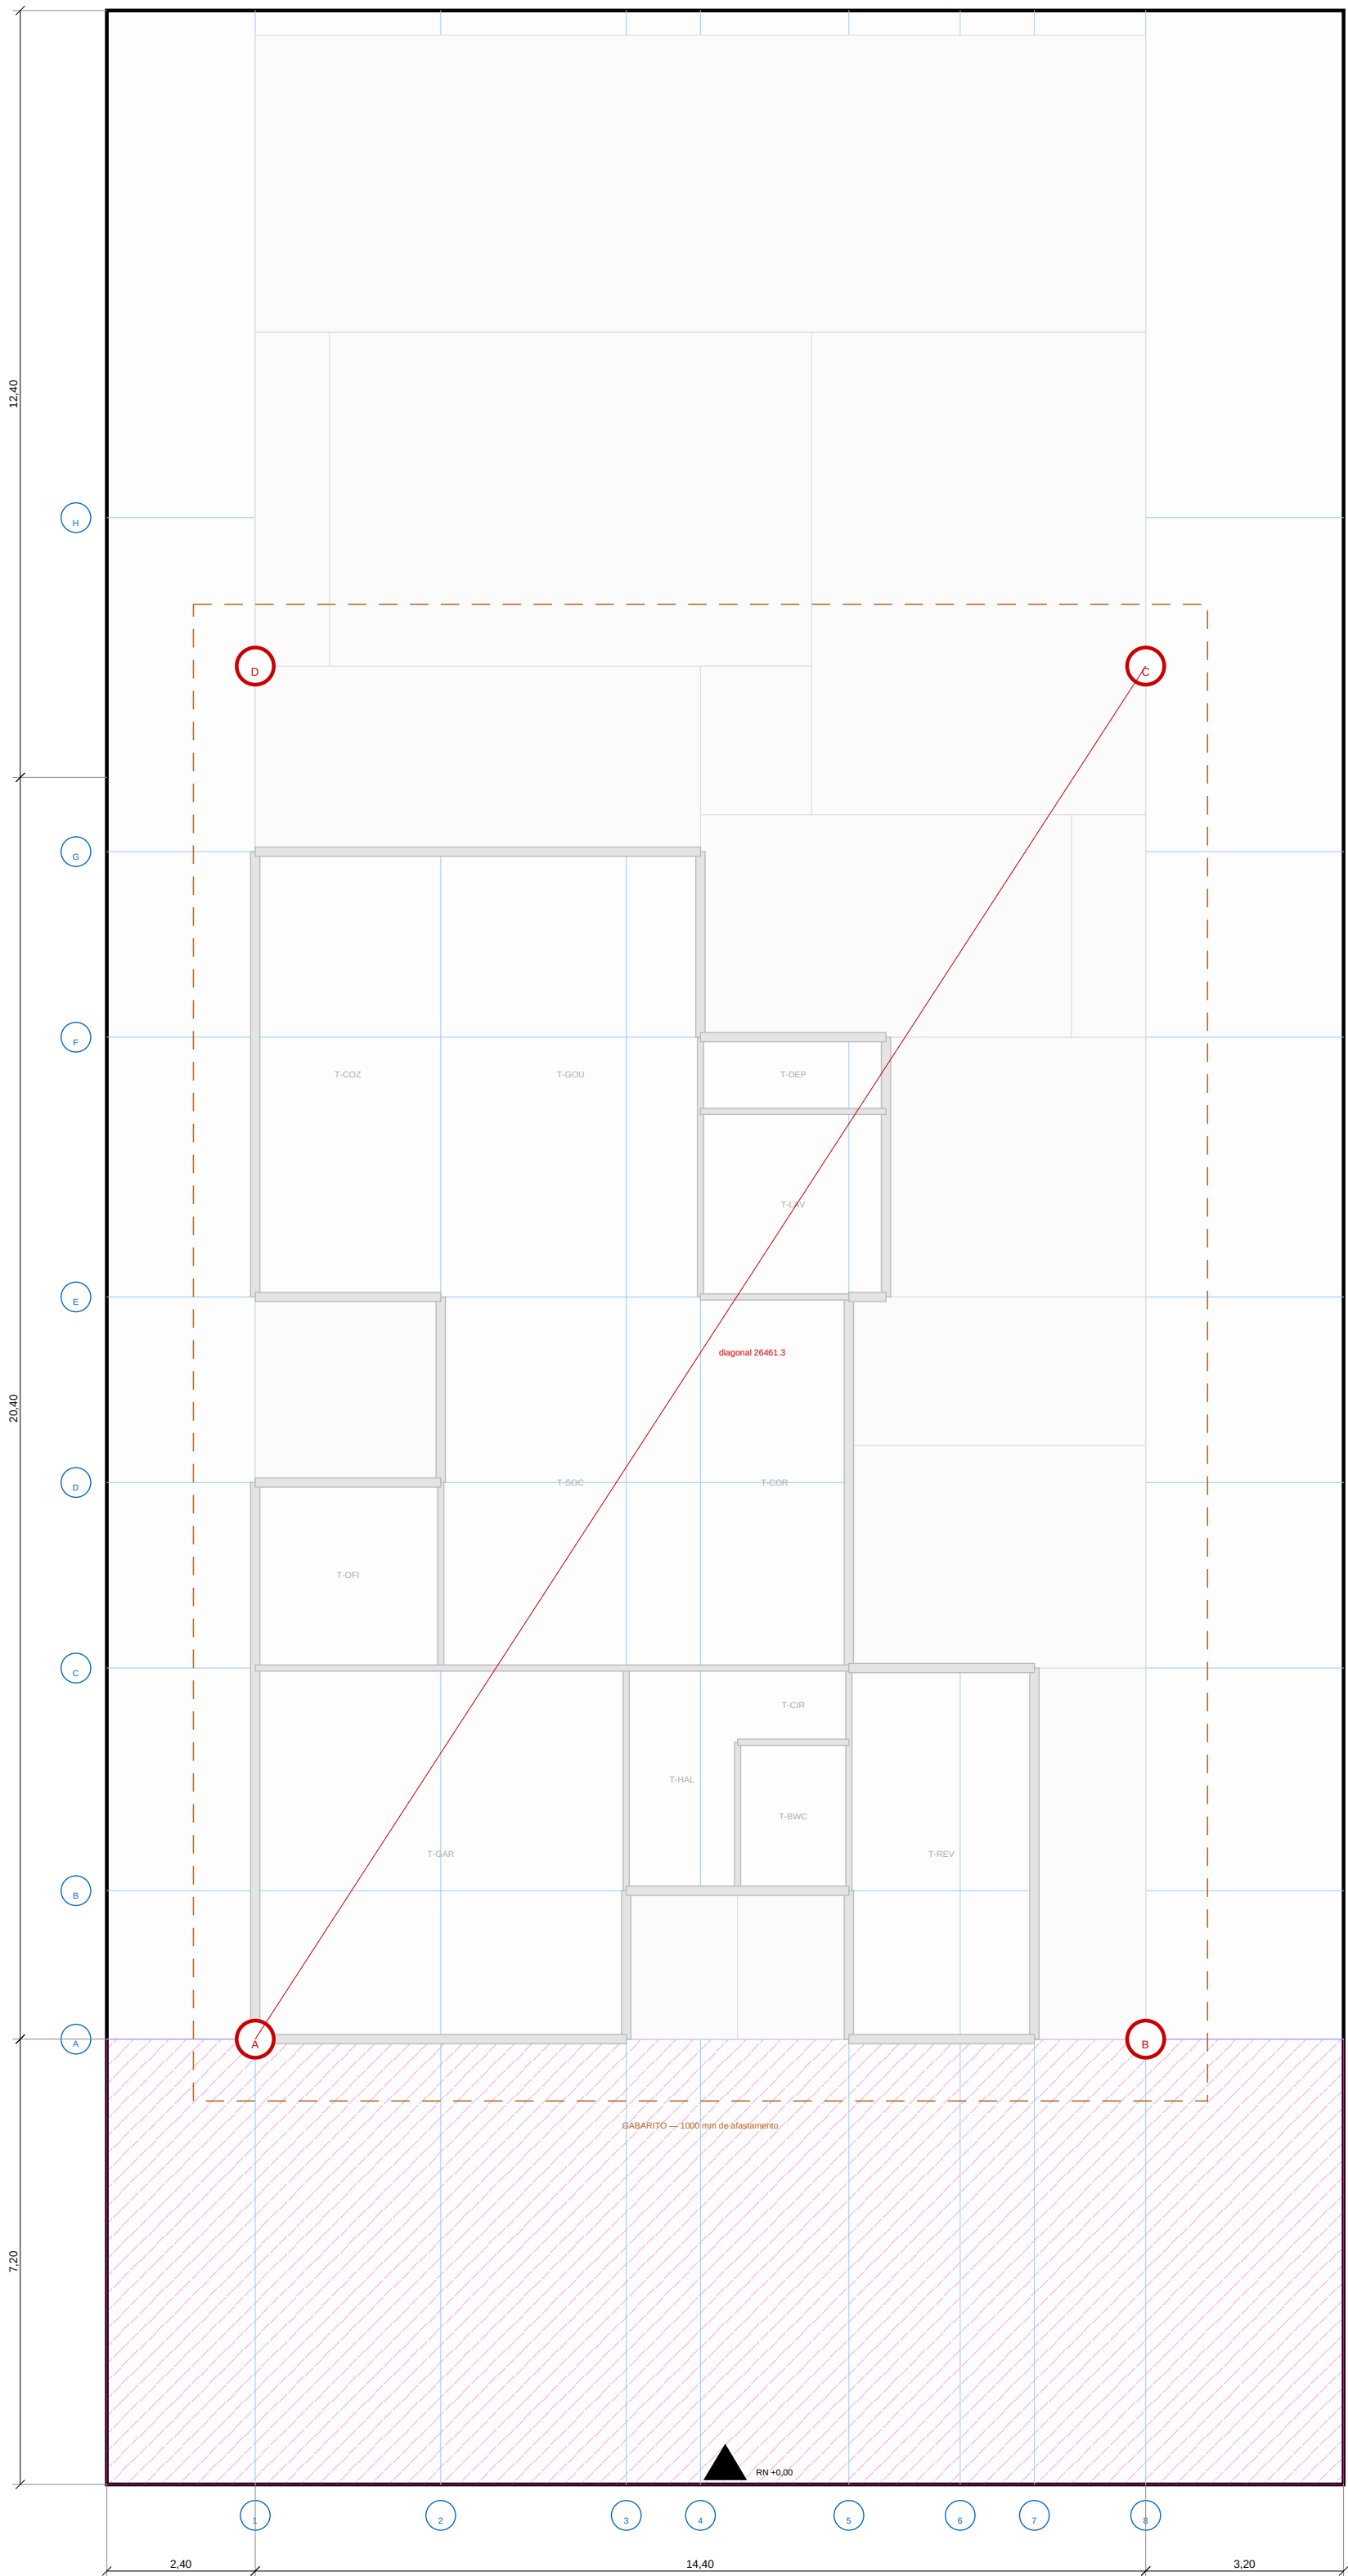

COORDENADAS DOS CANTOS (mm)

CANTO	X	Y	DIVISA SUL	DIVISA NORTE	TESTADA	ESBDO	DIAGONAL
A	2400	7200	2400	17600	7200	32800	26461,3
B	18800	7200	18800	3200	7200	32800	26461,3
C	18800	28400	18800	3200	28400	19600	26461,3
D	2400	28400	2400	17600	28400	19600	26461,3

PROCEDIMENTO DE LOCACAO

#	PASSO	CRITERIO DE ACABTE
1	Conferir as divisas com o material de base	divergencia acima de 10 mm interromper a locacao
2	Instalar o RMC marca de concreto 200 x 200 x 100 mm, fora da area de obra	fora da area de obra
3	Montar o gabarito a 1000 mm do cantoneiro	perguntas 75 x 75 e tubos 20 x 100
4	Marcar os eixos X (1) a X (10) e Y (1) a Y (10) no gabarito	linha coordenada multiplo de 200 mm
5	Cotar cada canto dos QUADs divises	verificar em cada canto, erro de cada lado
6	Conferir a diagonal A-C	26461,3 mm com tolerancia de 10 mm
7	Conferir o quadrado por 3-4-5 em cada canto	antes de qualquer concretagem
8	Registrar em ata com foto e medidas	gabarito continuo nos dois lados da divisa, conferencia

EIXOS MODULARES

DIRECAO	PROJECAO (mm)
X (1) a X (10)	2400 5400 8400 9600 12600 13800 15000 16800
Y (1) a Y (10)	7200 9600 13200 14200 15000 16800 18400 20800
Módulo	principal 600 mm - submódulo 300 mm
Origem	canto frontal esquerdo da base
Unidade	milímetros

NOTAS

- Locacao e o unico desenho em que o erro nao tem impacto direto a casa se do lugar.
- Cada canto e cotado dos QUADs divises, nunca em cabos acumulados — erro de cada soma, erro de referencia independente nao.
- Conferencia obrigatoria pela diagonal 26461,3 mm entre A e C antes de concretar o radier.
- Foto no ato de locacao, alinhado ao medidor TC-06, com 0,001 m por acurado do terreno.

PROJETO PORTO REAL

RESIDENCIA UNIFAMILIAR (MANSO) - AM | SOBR TATIANA-PS

PROJETO ARQUITETONICO

LOCACAO DE OBRA E GABARITO

BASE GEOMETRICA Linha Consolidada Projeto (previsão) Unidade: milímetros (mm)	ESCALA 1:100 FORMATO A1 Módulo: 600/300 (mm)	EXIBICAO ESTUDIO PRELIMINAR RM Linha Libertada para Obra SEM ART / RNT	PROJECOA 31 de 35 REVIRAS
--	---	---	---------------------------------