
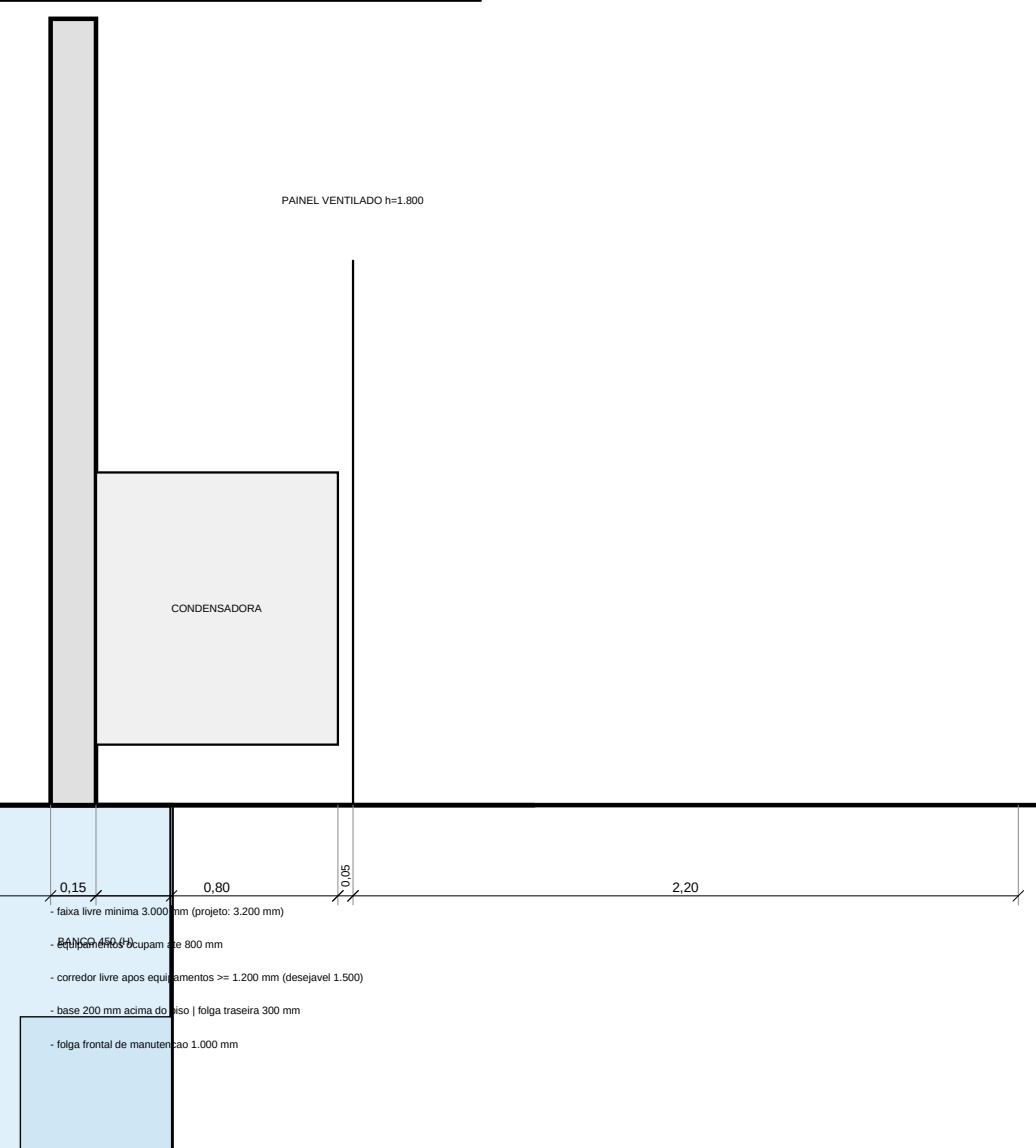


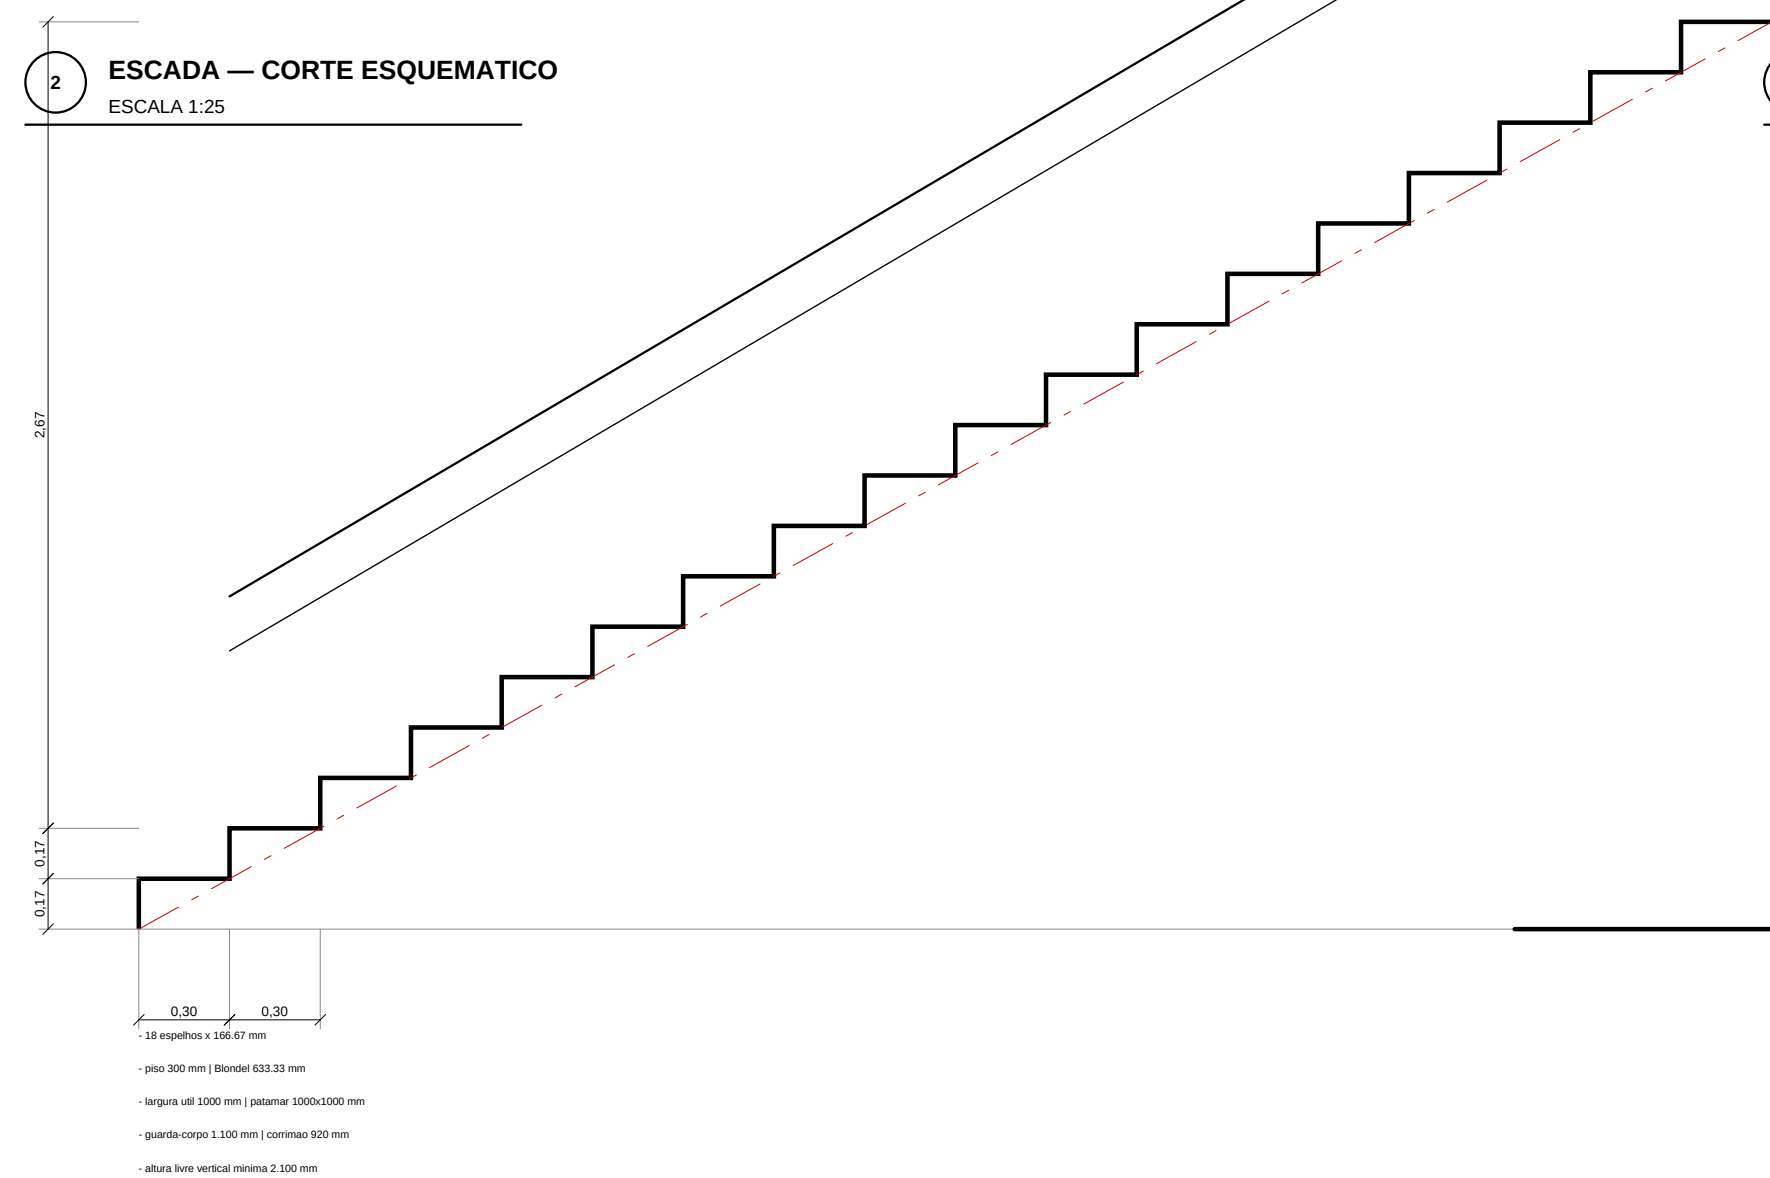

- Detalhes de estudo — não liberados para fabricação ou corte (sem nesting codificado).
- Parede externa consolidada em 150 mm; divisória interna em 100 mm (H).
- Escada reconciliar com estrutura, guarda-corpo e espessura de acabamento antes de definitiva.

PROJETO PORTO REAL RESIDENCIA UNIFAMILIAR (MANAUS - AM) (SOLTA TAMBORA 05)			
PROJETO ARQUITETONICO DETALHES CONSTRUTIVOS AMPLIADOS			
BASE GEOMETRICA Lista Consolidada pos 002 (previous) UNIDADE MESTRE - 004	ESCALA indicada FORMATO A1 MELHORA 000/000/000	ENTRADA ESTUDO PRELIMINAR 002 NÃO LIBERADO PARA OBRA SEM ART - 001	PRONCHIA 10 09.10. REV 007