


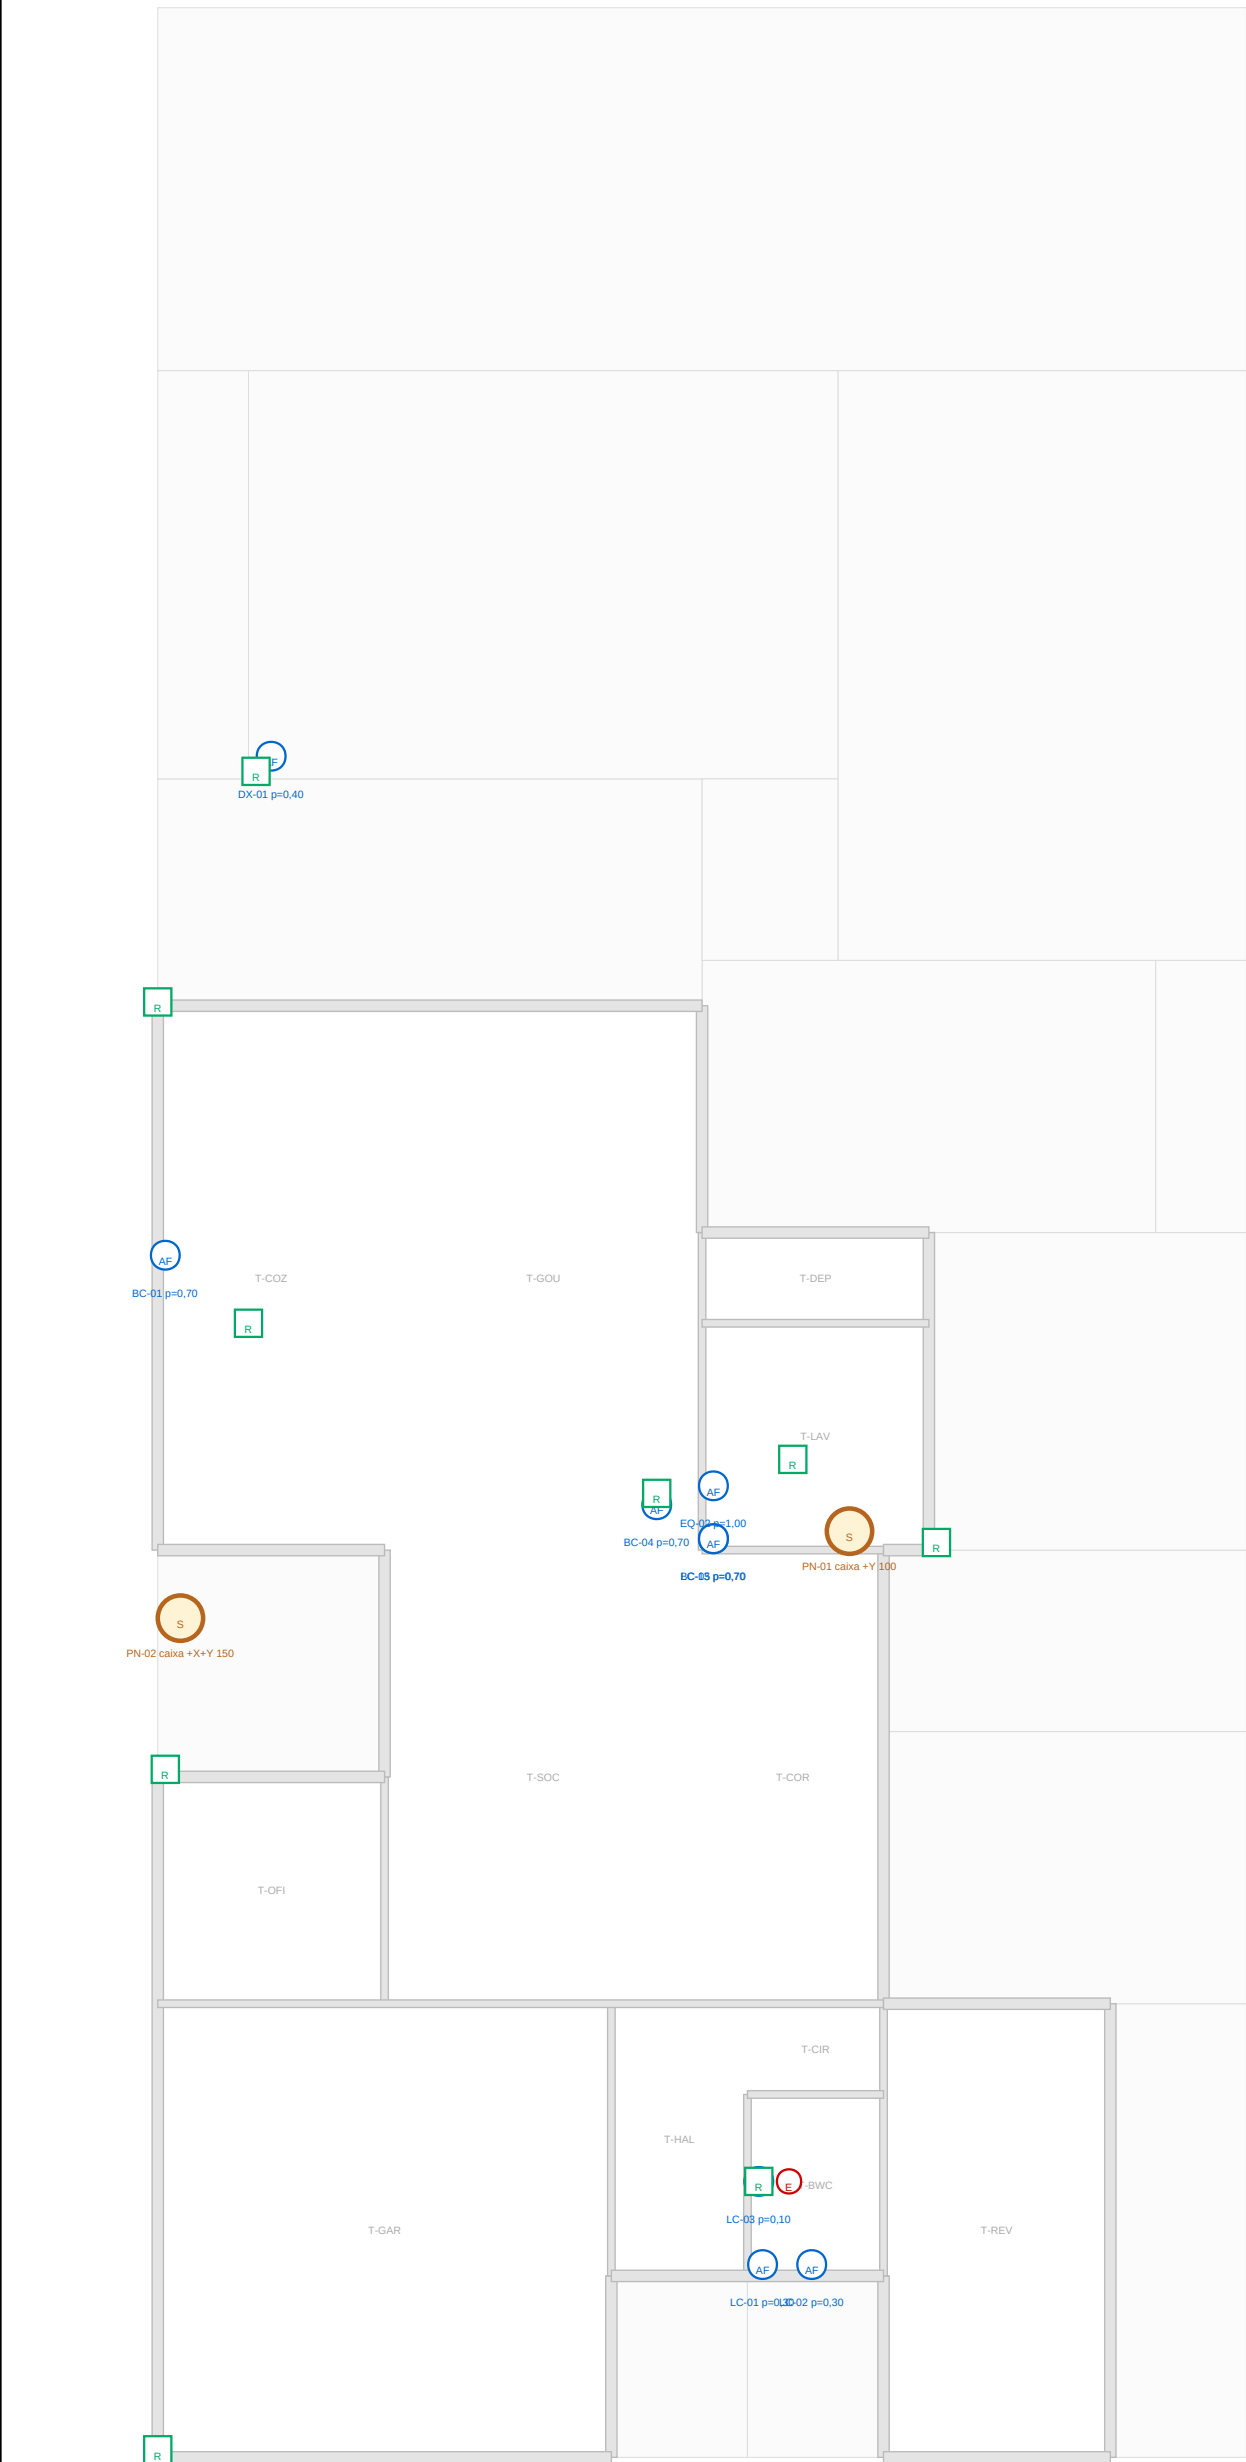


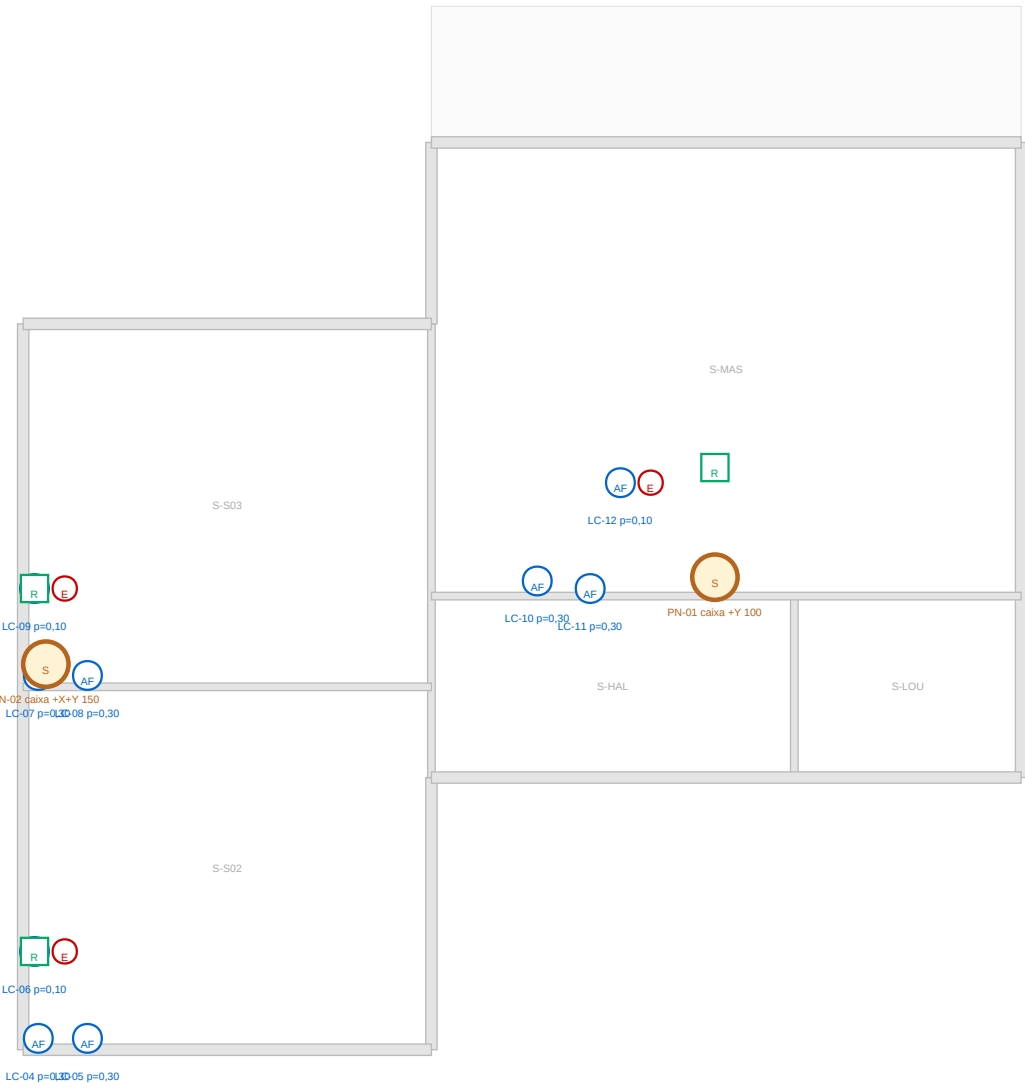

1 PONTOS HIDRAULICOS — TERREO
ESCALA 1:100

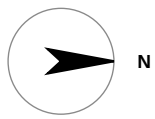

2 PONTOS HIDRAULICOS — SUPERIOR
ESCALA 1:100

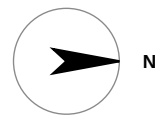

TRECHO	PECAS	PESOS	Q (L/s)	DN AGUA	V (m/s)	UMC	DN ESGOTO	REGIME
Superior	8	2.10	0.435	DN25	1.19	27	DN100	pressurizado
Terreo	9	4.80	0.884	DN25	1.81	36	DN100	gravidade
GERAL	18	7.00	0.794	DN32	1.31	33	DN100	gravidade

COD	AMB	TIPO	PESO	UMC	DN AF	DN ESG	QUENTE
LC-01	T-BWC	vaso	0.30	6	DN25	DN40	—
LC-02	T-BWC	lavatório	0.30	1	DN25	DN40	—
LC-03	T-BWC	box	0.30	2	DN25	DN40	sim
LC-04	S-S02	vaso	0.30	6	DN25	DN40	—
LC-05	S-S02	lavatório	0.30	1	DN25	DN40	—
LC-06	S-S02	box	0.30	2	DN25	DN40	sim
LC-07	S-S03	vaso	0.30	6	DN25	DN40	—
LC-08	S-S03	lavatório	0.30	1	DN25	DN40	—
LC-09	S-S03	box	0.30	2	DN25	DN40	sim

COD	AMB	TIPO	PESO	UMC	DN AF	DN ESG	QUENTE
LC-01	S-MAS	vaso	0.30	6	DN25	DN40	—
LC-02	S-MAS	lavatório	0.30	1	DN25	DN40	—
LC-03	S-MAS	box	0.30	2	DN25	DN40	sim
LC-04	T-LAV	vaso	0.70	3	DN25	DN40	—
LC-05	T-CO2	sim	0.70	3	DN25	DN40	—
LC-06	T-CO2	sim	0.70	3	DN25	DN40	—
LC-07	T-LAV	sim	0.70	3	DN25	DN40	—
LC-08	T-LAV	lavatório	1.00	3	DN25	DN40	—
LC-09	T-DPA	banho, entrada	0.40	2	DN25	DN40	—

DECISAO	CONSEQUENCIA HIDRAULICA
Chuveiro elétrico em vez de aquecimento central	peso 0.02 por chuveiro em vez de 0.40; a soma cai de 5.2 para 7.0 pesos e o alimentador de DN40 para DN32
Limite de velocidade por conforto, não por norma	DN32 elevando a soma a 2.07 m/s e 3.0 m/s e não mais DN40. Cuida alguns metros de tubo
Pressurizador na rede superior	0.5 mca por gravidade nas setores chuveiro elétrico, TC-14 entrega 12 mca
Redes pluviais sem ligação a valas	rede de rede e fisicamente separada, com cot e identificação próprias, não há ponto de conexão cruzada possível
Canal de grelhas antes da inspeção	cota 10.1 > TC-11 (DN-1) > TC-12 > rede, DN100 com cobertura de 2%

PROJETO PORTO REAL

RESIDENCIA UNIFAMILIAR (MANSÃO - AM) | SOBR TATIANA-PS

PROJETO ARQUITETONICO

INSTALACOES HIDROSSANITARIAS

BASE GEOMETRICA

Unia Consolidada

Projeto (preliminar)

UNIDADE MESTRE: AM

ESCALA

1:100

FORMATO A1

MALHA 600/600/600

EMISSAO

ESTUDO PRELIMINAR R47

NAO LIBERADO PARA OBRA

SEM ART / RNT

PROVACA

26

IN-25 REV R47