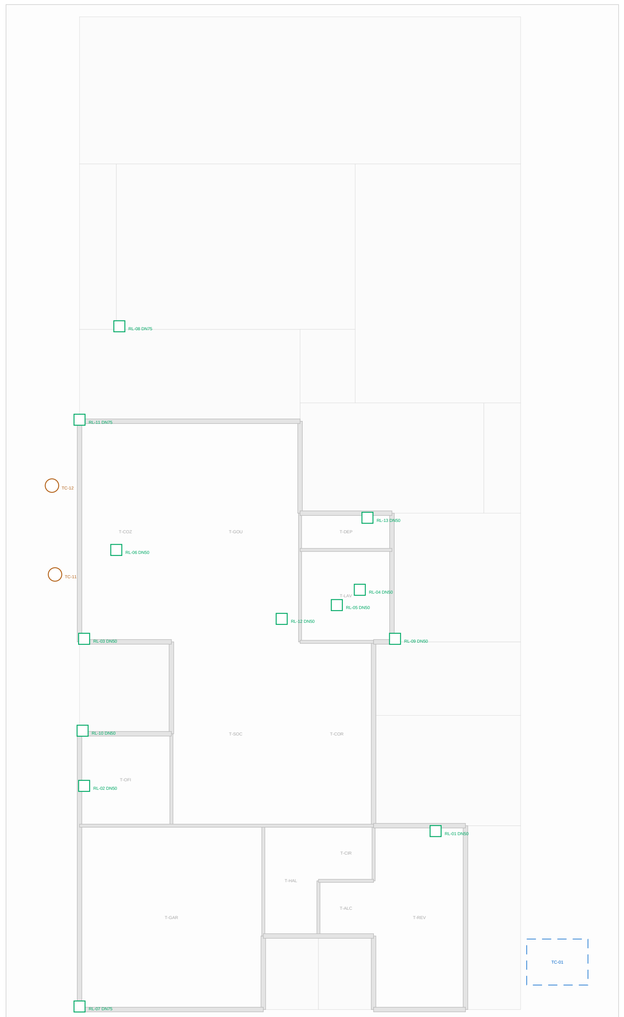


N

RALOS E CAIMENTOS

COD	AMB	AMBIENTE	TIPO	DN	CAIMENTO	AREA (m2)
RL-13	T-DEP	DEPOSITO / DML	ralo seco 100	DN50	1.0%	3.60
RL-01	T-REV	QUARTO REVERSIVEL	ralo linear 600	DN50	1.5%	18.00
RL-02	S-S02	SUITE 02	ralo linear 600	DN50	1.5%	25.92
RL-03	S-S03	SUITE 03	ralo linear 600	DN50	1.5%	25.92
RL-04	S-MAS	SUITE MASTER	ralo linear 900	DN50	1.5%	46.80
RL-05	T-LAV	LAVANDERIA	ralo sifonado 150	DN50	1.5%	9.00
RL-06	T-COZ	COZINHA	ralo sifonado 100	DN50	1.5%	21.60
RL-07	T-GAR	GARAGEM	ralo linear 6.000	DN75	1.0%	36.00
RL-08	T-DKP	DECK DA PISCINA	canaleta com grelha	DN75	1.0%	42.12
RL-11	T-ALP	VARANDA GOURMET	ralo linear 7.200 sob a cortina	DN75	1.0%	21.60
RL-12	T-GOU	GOURMET	ralo sifonado 150	DN50	1.0%	30.24
RL-09	T-VRL	VARAL COBERTO	ralo sifonado 150	DN50	1.0%	17.64
RL-10	T-LOG	LOGGIA SUL	ralo sifonado 150	DN50	1.0%	9.00

BALANCO PLUVIAL

ITEM	VALOR	
Area de contribuicao da cobertura	331.56 m2	
Intensidade de projeto	180 mm/h (TR 25 anos, m)	
Vazao total / por descida	15.7491 L/s	3.9373 L/s
Calha externa	150 x 100 mm	
Descidas	4 x DN100	
Decisao pluvial	RETENCAO — reservatorio dimensionado pelo EXCEDENTE de vazao	
Reuso	REJEITADO por decisao do proprietario em R02	
Area impermeabilizada do lote	329.40 m2 de 800 m2 (41.2 %)	
Gatilho da Lei 1.192/2007	obriga acima de 500 m2 — nao obriga, adotada por decisao do proprietario	
Vazao antes / depois	8.00	21.96 L/s
Reservatorio de retencao	8.38 m3, orificio de 59 mm, esvazia em 35 min	
Area externa drenada	63.72 m2	

IMPERMEABILIZACAO E DETALHES DE AGUA

ITEM	ESPECIFICACAO	RAZAO
Sistema	manta liquida poliuretanica, 2 demaos	flexivel: acompanha a movimentacao do contrapiso seco sobre LSF
Subida na parede	300 mm	respingo de piso molha o rodape; e em LSF o rodape e gesso
Subida no box	1800 mm	altura do chuveiro: e ali que a agua bate todos os dias
Soleira do box	15 mm	desnivel suficiente para conter, baixo o bastante para nao tropecar
Teste de estanqueidade	estanqueidade com lamina de 50 mm por 72 h	em LSF o vazamento nao mancha: apodrece o OSB por dentro, sem aviso
Ralo linear no box	600 a 900 mm	caimento em uma direcao so: menos recorte de piso e menos erro de obra

1 **DRENAGEM — IMPLANTACAO**
ESCALA 1:100

NOTAS

- Cobertura: 331.56 m2 de contribuicao, I = 180 mm/h, C = 0.95 -> Q = 15.7491 L/s em 4 descidas DN100.
- Caimento de 1.5% em area molhada interna e 1% em area externa.
- Impermeabilizacao: manta liquida poliuretanica, 2 demaos, subindo 300 mm na parede e 1800 mm no box.
- Retencao de 8.38 m3 sob o acesso de veiculos, com orificio de 59 mm calibrado na vazao de pre-ocupacao. Nao ha rede de reuso: agua potavel unica.

PROJETO PORTO REAL

RESIDENCIA UNIFAMILIAR | MANAUS - AM | SUS6 TARUMA (H)

PROJETO ARQUITETONICO

DRENAGEM PLUVIAL E DE PISO

BASE GEOMETRICA	ESCALA	EMISSAO	PRANCHA
Lista Consolidada (pos-R32 (prevalece))	1:100	ESTUDO PRELIMINAR R04	29
UNIDADE MESTRE: mm	FORMATO A1	NAO LIBERADO PARA OBRA	de 41 REV R04
	MALHA 800/300/150	SEM ART / RRT	