


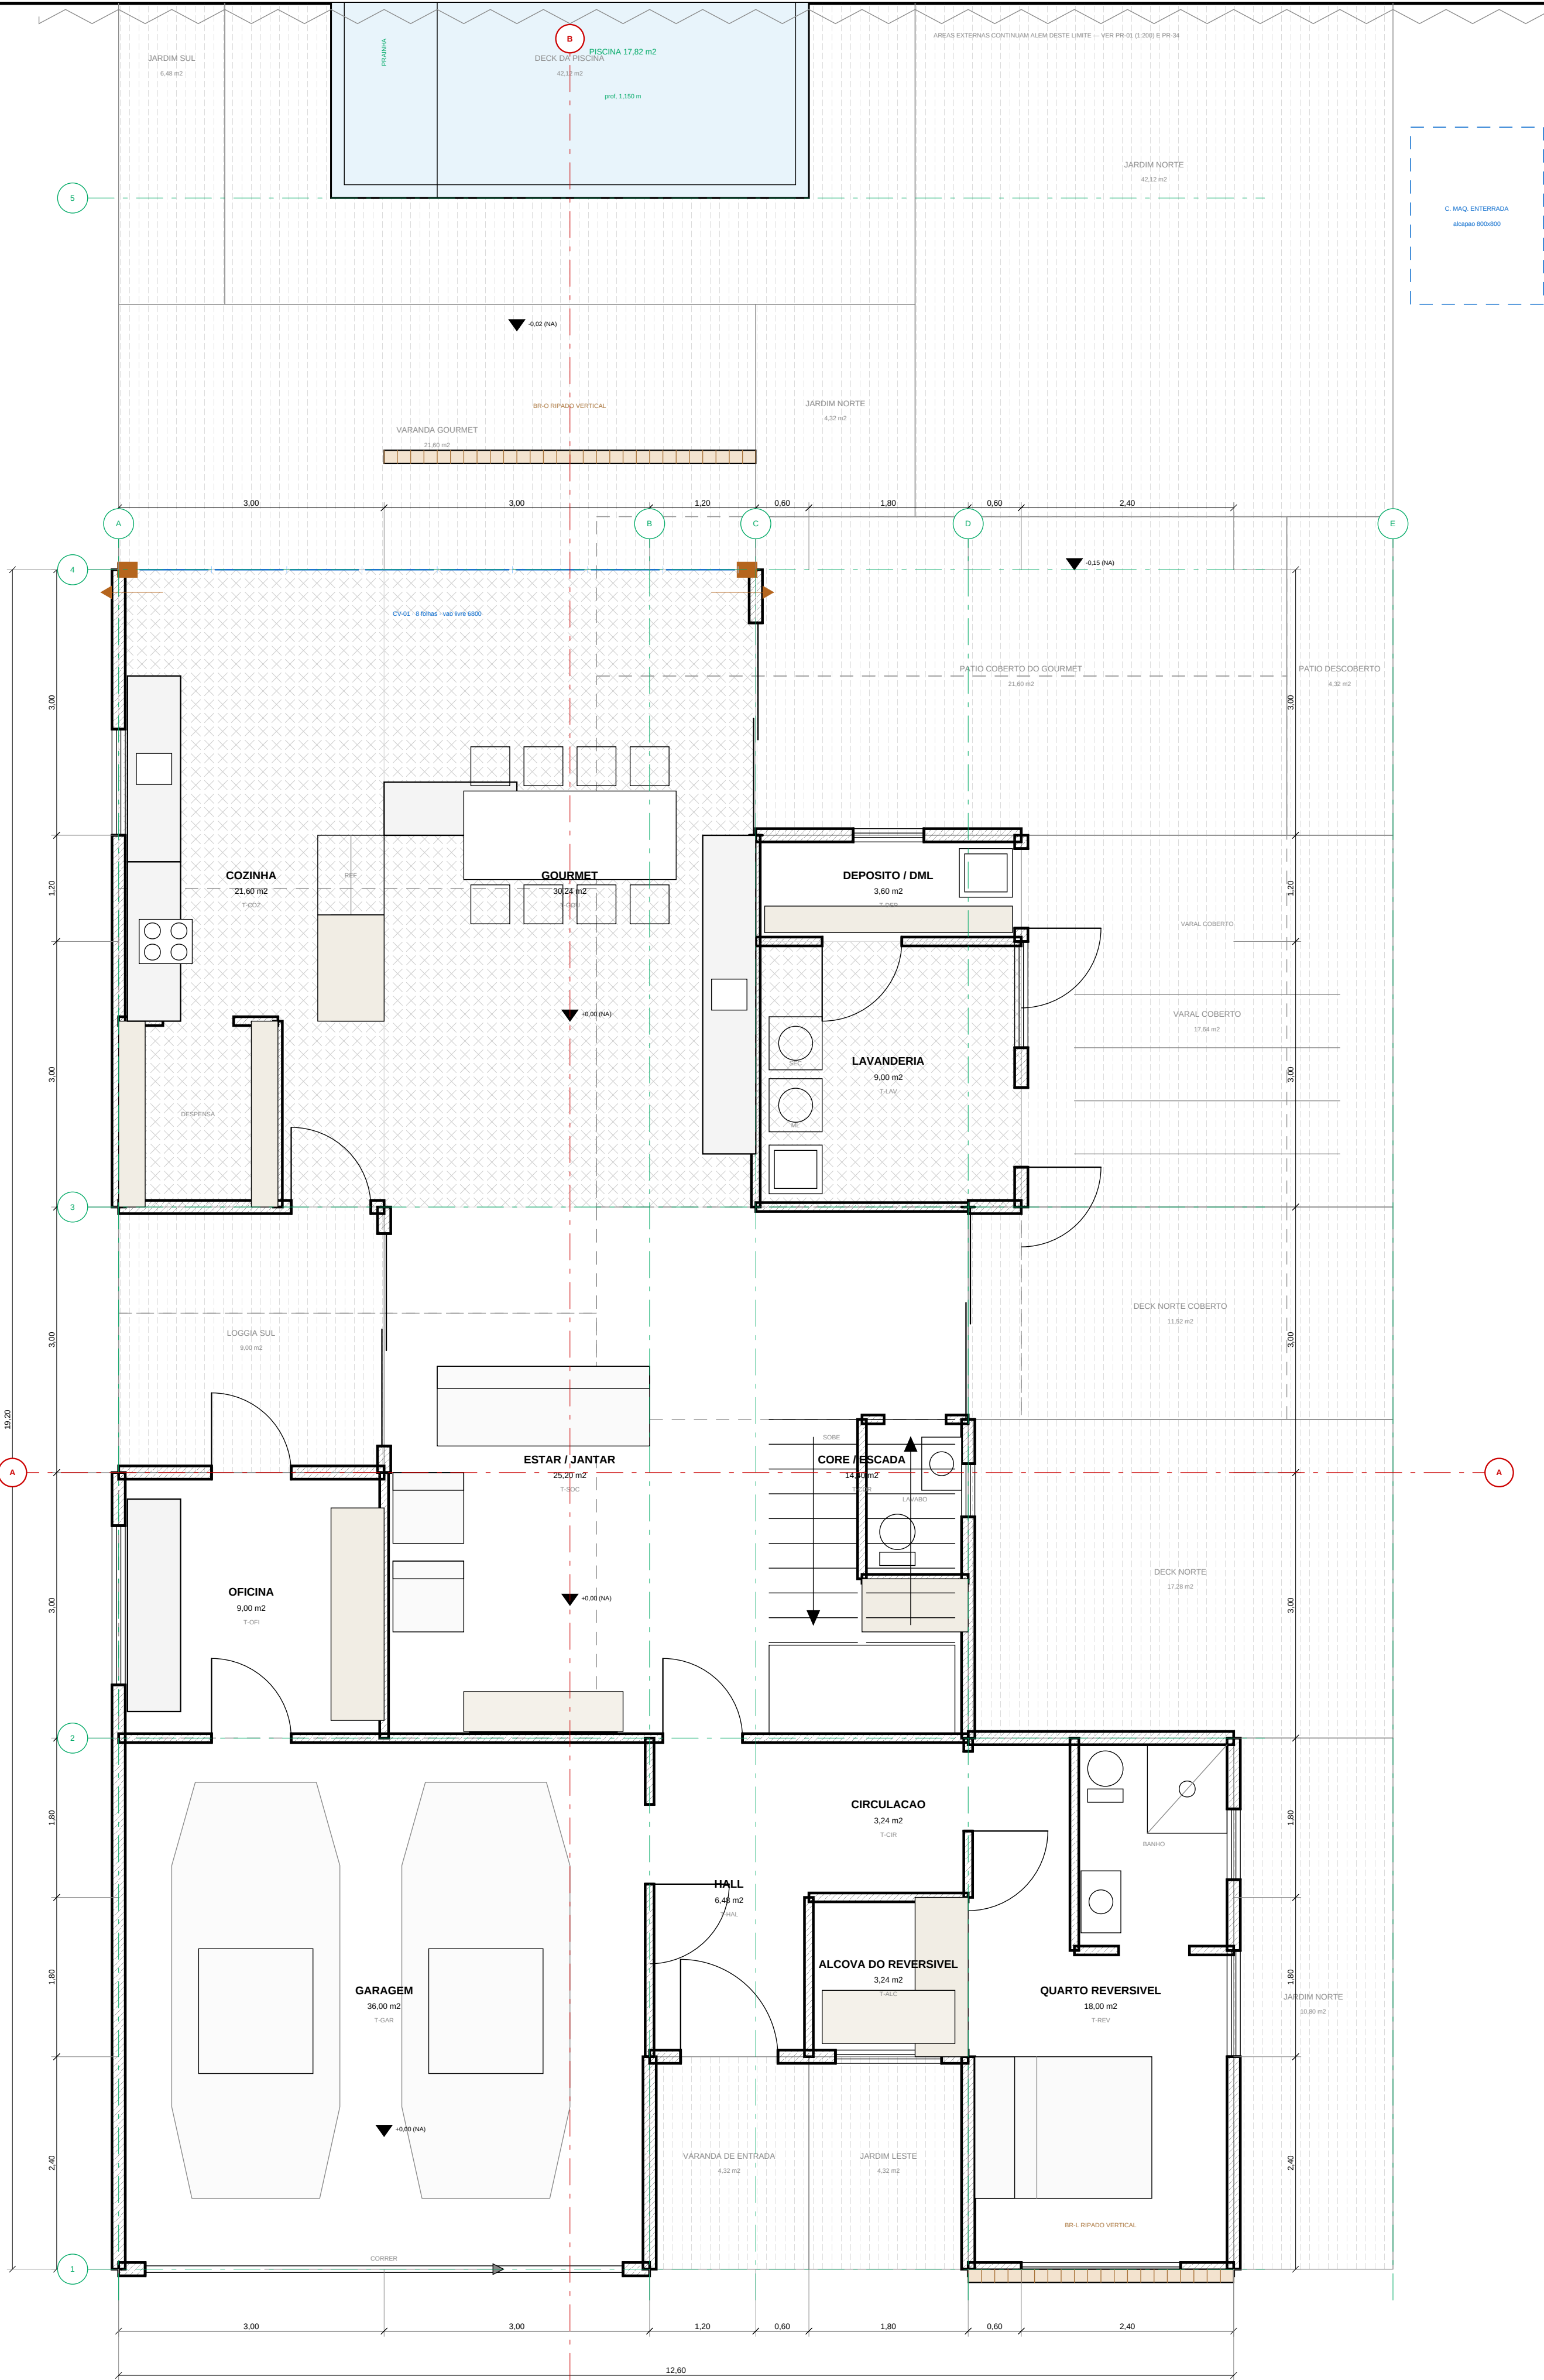

1 PAVIMENTO TERREO
ESCALA 1:50




QUADRO DE ÁREAS — PAVIMENTO TERREO			
COD	AMBIENTE	MÓDULO (mm)	ÁREA (m²)
T-GAR	CARAGEM	600x600	36,00
T-HAL	HALL	1800x3000	5,40
T-ALC	ALCOVA DO REVERSÍVEL	1800x1800	3,24
T-CIR	CIRCULAÇÃO	1800x1800	3,24
T-REV	QUARTO REVERSÍVEL	3000x3000	18,00
T-OFI	OFICINA	3000x3000	9,00
T-SOC	ESTAR / JANTAR	4500x4500	20,25
T-COR	CORE / ESCADA	2400x4500	10,80
T-COZ	COZINHA	3000x2700	8,10
T-GOU	GOUREMET	4500x2700	12,15
T-LAV	LAVANDERIA	3000x3000	9,00
T-DEP	DEPÓSITO / D.M.	3000x1200	3,60
TOTAL FECHADO			186,09
T-VAR	VARANDA DE ENTRADA (área)	1800x2400	4,32
T-J.E	JARDIM LESTE (área)	1800x4500	8,10
T-J.N	JARDIM NORTE (área)	1800x3000	5,40
T-LOG	LOGGIA SUL (área)	3000x3000	9,00
T-D.M	DECK NORTE COBERTO (área)	4800x3000	14,40
T-D.M	DECK NORTE COBERTO (área)	4800x2400	11,52
T-VAR	VARAL COBERTO (área)	4500x4500	20,25
T-PAT	PATIO COBERTO DO GOUREMET (área)	6000x3000	18,00
T-PAT	PATIO DESCOBERTO (área)	1200x3000	3,60
T-VAR	VARANDA GOUREMET (área)	7500x3000	22,50
T-DEP	DECK DA COZINHA (área)	7500x4500	33,75
T-J.S	JARDIM SUL (área)	1200x4500	5,40
T-J.N	JARDIM NORTE (área)	1800x2400	4,32
T-J.N	JARDIM NORTE (área)	5400x7500	40,50
T-PAT	JARDIM DE FUNDO (área)	14400x4800	69,12


REF	VALOR (mm)	QTD	QTD	TIPO
CVE1	7000x2000	0	1	CORTINA DE VEDAR VIDRO, 0 folha de 900 mm
J1	1200x1200	1200	4	porta de banheiro, alumínio
J2	800x800	1800	1	porta de banheiro, alumínio
J3	800x800	1800	2	porta de banheiro, alumínio
J4	1800x1200	1200	2	porta de banheiro, alumínio
J5	1200x1200	1200	2	porta de banheiro, alumínio
J6	1200x1200	0	1	porta principal, alumínio
J7	800x1200	0	2	porta interna (divisão unidades)
J8	800x1200	0	5	porta de serviço, alumínio a unidade
J9	800x1200	0	1	porta interna de fumaça SOLADA com vidros (pau)
J10	5400x2400	0	1	porta de correr, alumínio espelho
J11	3600x2400	0	1	porta de correr, alumínio espelho

LEGENDA E CONVENÇÕES (NBR 6492 / 8403)

- Elemento seccionado pelo plano de corte (h = 1,50 m)
- Área vista / folha de espelho
- Modulador fixo, equipamento e simbologia
- Propriedade do pavimento superior e da cobertura
- Eixo modular e linha de corte
- Linha de corte e linha auxiliar

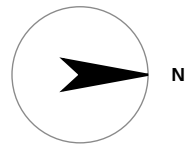

PERCURSO SOLAR — MANUS 1.5

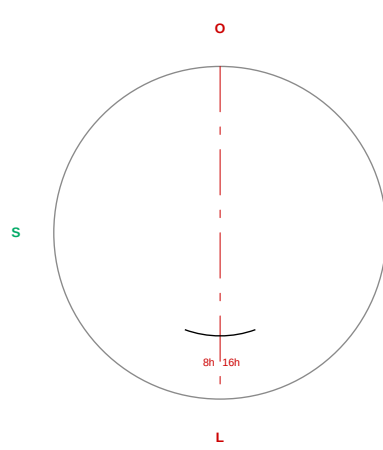

Nota: 1:50 m e 1:50 m
= escala para o projeto
Nota: 1:50 m e 1:50 m
= escala para o projeto

- Dimensões em milímetros, cotas de nível em metros.
- Modulador 600 mm, cotas em metros.
- Planta externa 120 mm / planta interna 120 mm (p).
- Modulador fixo indica pontos de água e esgoto (NBR 6492).

PROJETO PORTO REAL

RESIDÊNCIA UNIFAMILIAR (MANUS - AM) (SOL TARTARUGA)

PROJETO ARQUITETÔNICO

PLANTA DE LAYOUT — PAVIMENTO TERREO

BASE GEOMÉTRICA

União Consolidada

PROJETO (previsão)

UNIDADE MÉTRICA: mm

ESCALA

1:50

FORMATO A1

VALORES: 600/600/600

EXIBIÇÃO

ESTUDO PRELIMINAR R7B

UNO LIBERADO PARA OBRAS

SEM ART / RNT

PROJETO

04

6/73 REV. 01