


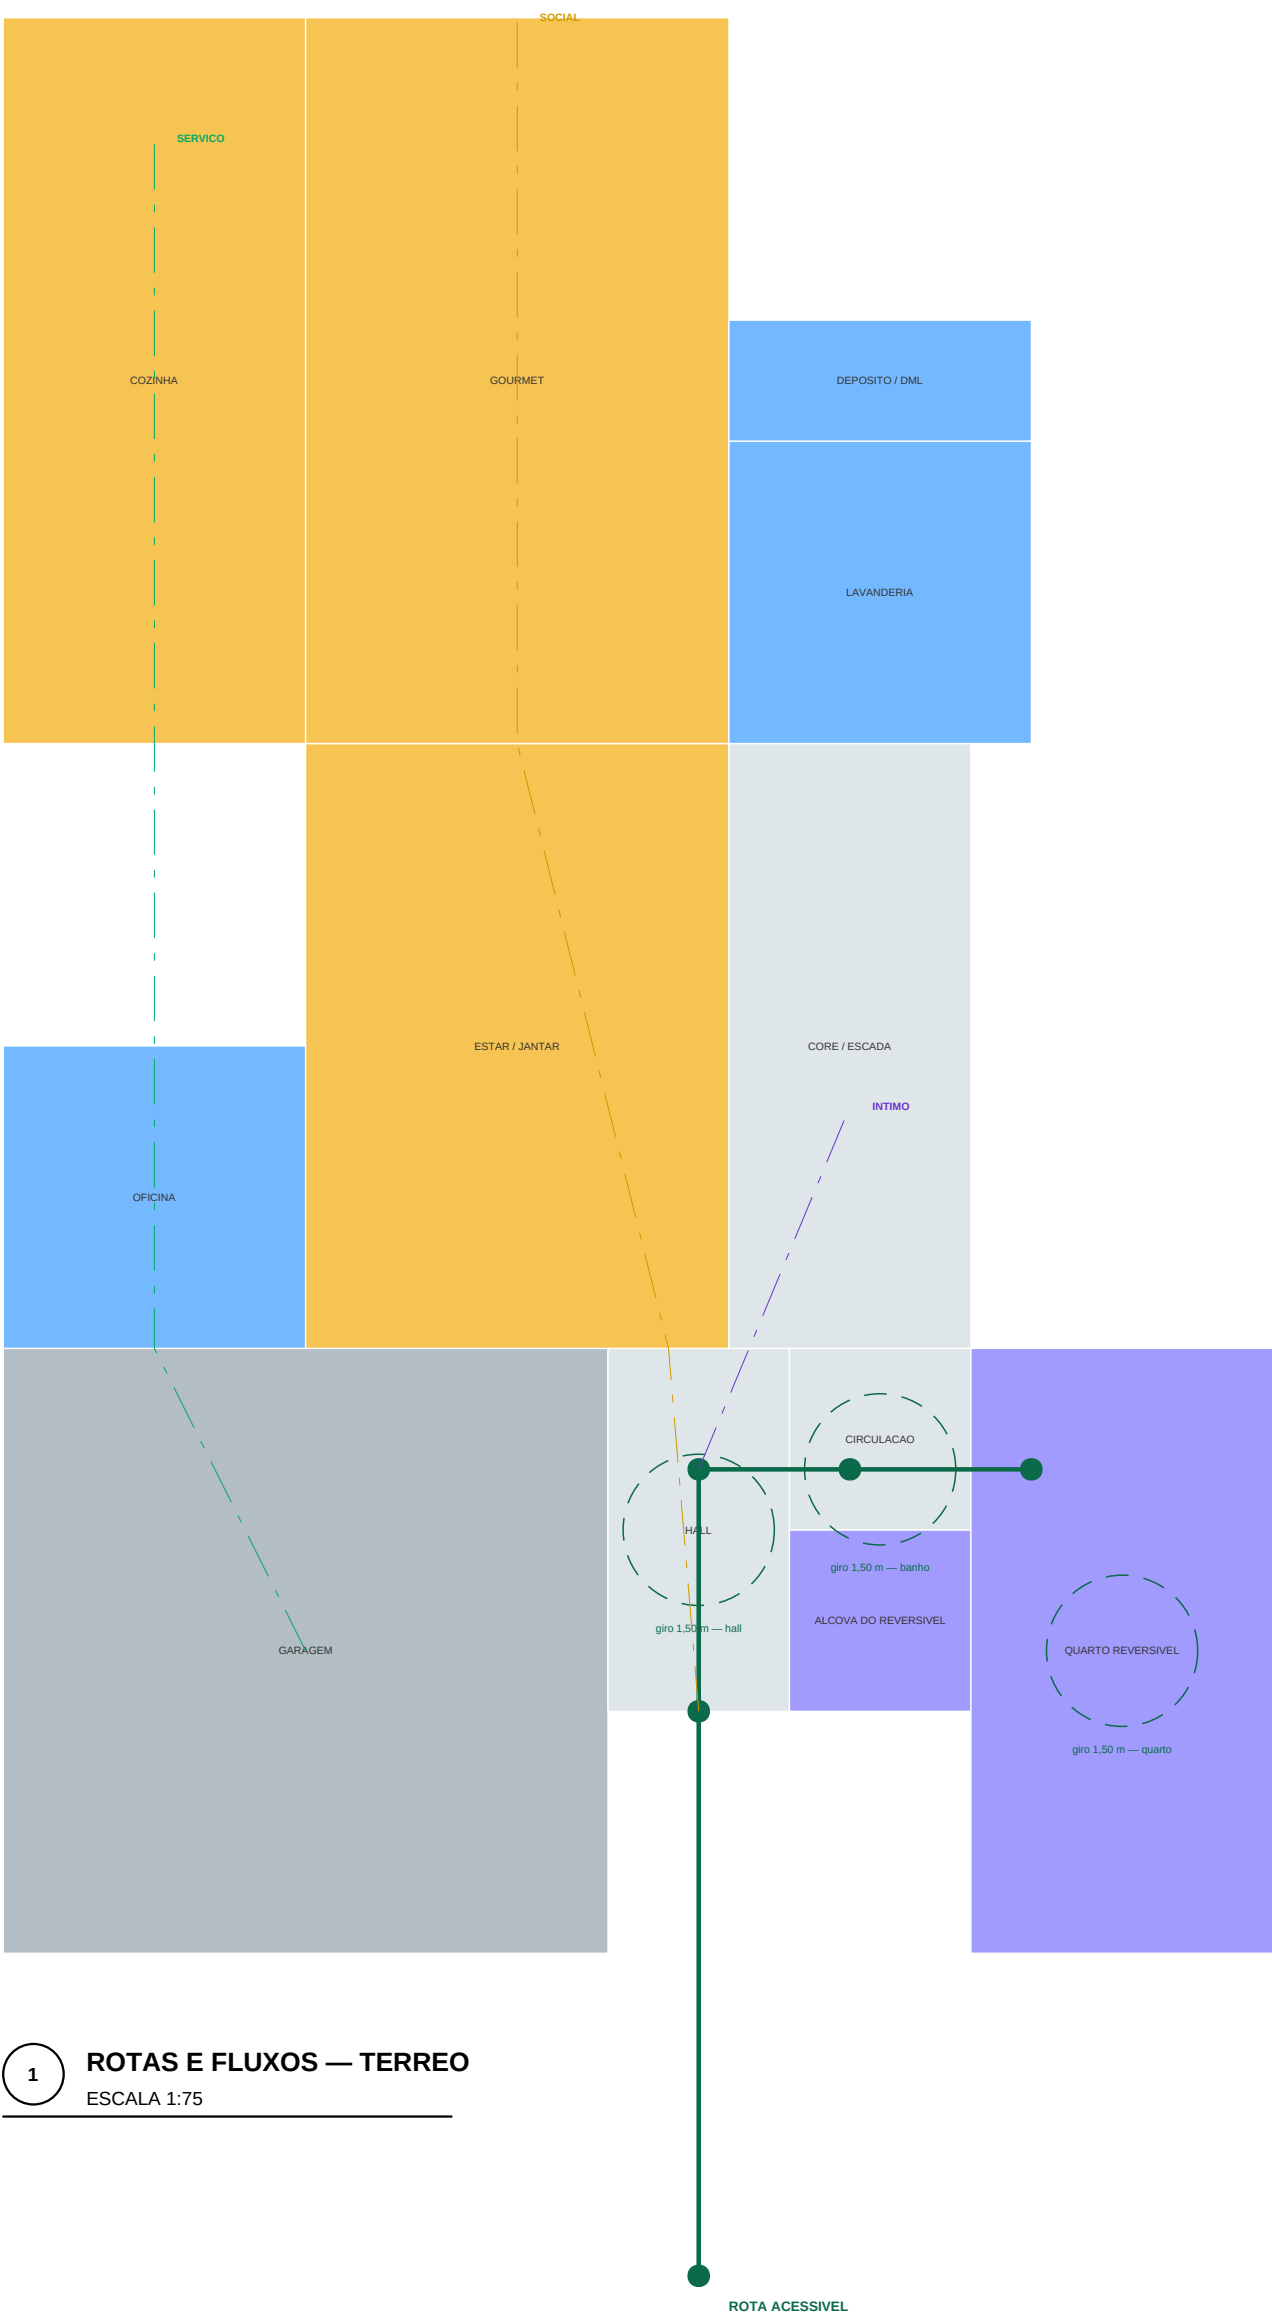


1 ROTAS E FLUXOS — TERREO
ESCALA 1:75

VERIFICACAO NBR 9050

ITEM	EXISTENTE	PROPOSTO	
Vel. livre de porta	800 mm	940 mm (altura de 900)	OK
Circulo de giro 360 graus	1.500 mm	hall, banheiro e quarto	OK
Desnivel sem rampas	até 5 mm	terminos nivelados	OK
Largura de circulacao	900 mm	1.800 mm no hall	OK
Barras de apoio	relevo no piso	ambuido no PTE 1 e PTE 2	OK
Barranca acessivel	altura livre 750 mm	sem barreiras até a calha	OK
Corredor e interruptor	600 a 1.000 mm	a definir no eletrico	pendente

FLUXOS — SEPARACAO DE CIRCUITOS

CIRCUITO	PERCURSO	CRIÇA O SOCIAL?
Servico	garagem -> oficina -> lavanderia -> cozinha -> despensa	NÃO
Social	entrada -> hall -> estar -> gourmet -> alameda -> piscina	—
Servico Interno	hall -> circulacao -> banheiro social (quarto reversivel) (se não for projeto)	NÃO
Servico Superior	hall -> cora -> hall superior -> suites	NÃO
Uso e carga	cozinha -> despensa -> refeit hall	NÃO

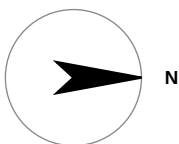

- NOTAS
- * Rota acessivel do passeio ao quarto reversivel e ao banheiro social.
 - * Circulo de giro de 1.500 mm verificado nos pontos de manobra.
 - * Porta de correr de 900 mm no banheiro social e area de varanda.
 - * Refeitico para bar do apoio ambuido antes do fechamento das placas.

PROJETO PORTO REAL

RESIDENCIA UNIFAMILIAR (MANSÃO - AM) | SOUS TATIANA-PS

PROJETO ARQUITETONICO

ACESSIBILIDADE E FLUXOS

BASE GEOMETRICA Linha Consolidada ISO 9122 (previsto) UNIDADE MESTRE: mm	ESCALA 1:75 FORMATO A1 MILHA 955/000/000	EMISSAO ESTUDO PRELIMINAR R7B NÃO LIBERADO PARA OBRA SEM ART / RNT	PROVA 17 IN-73 REVIEW
---	--	---	------------------------------------