



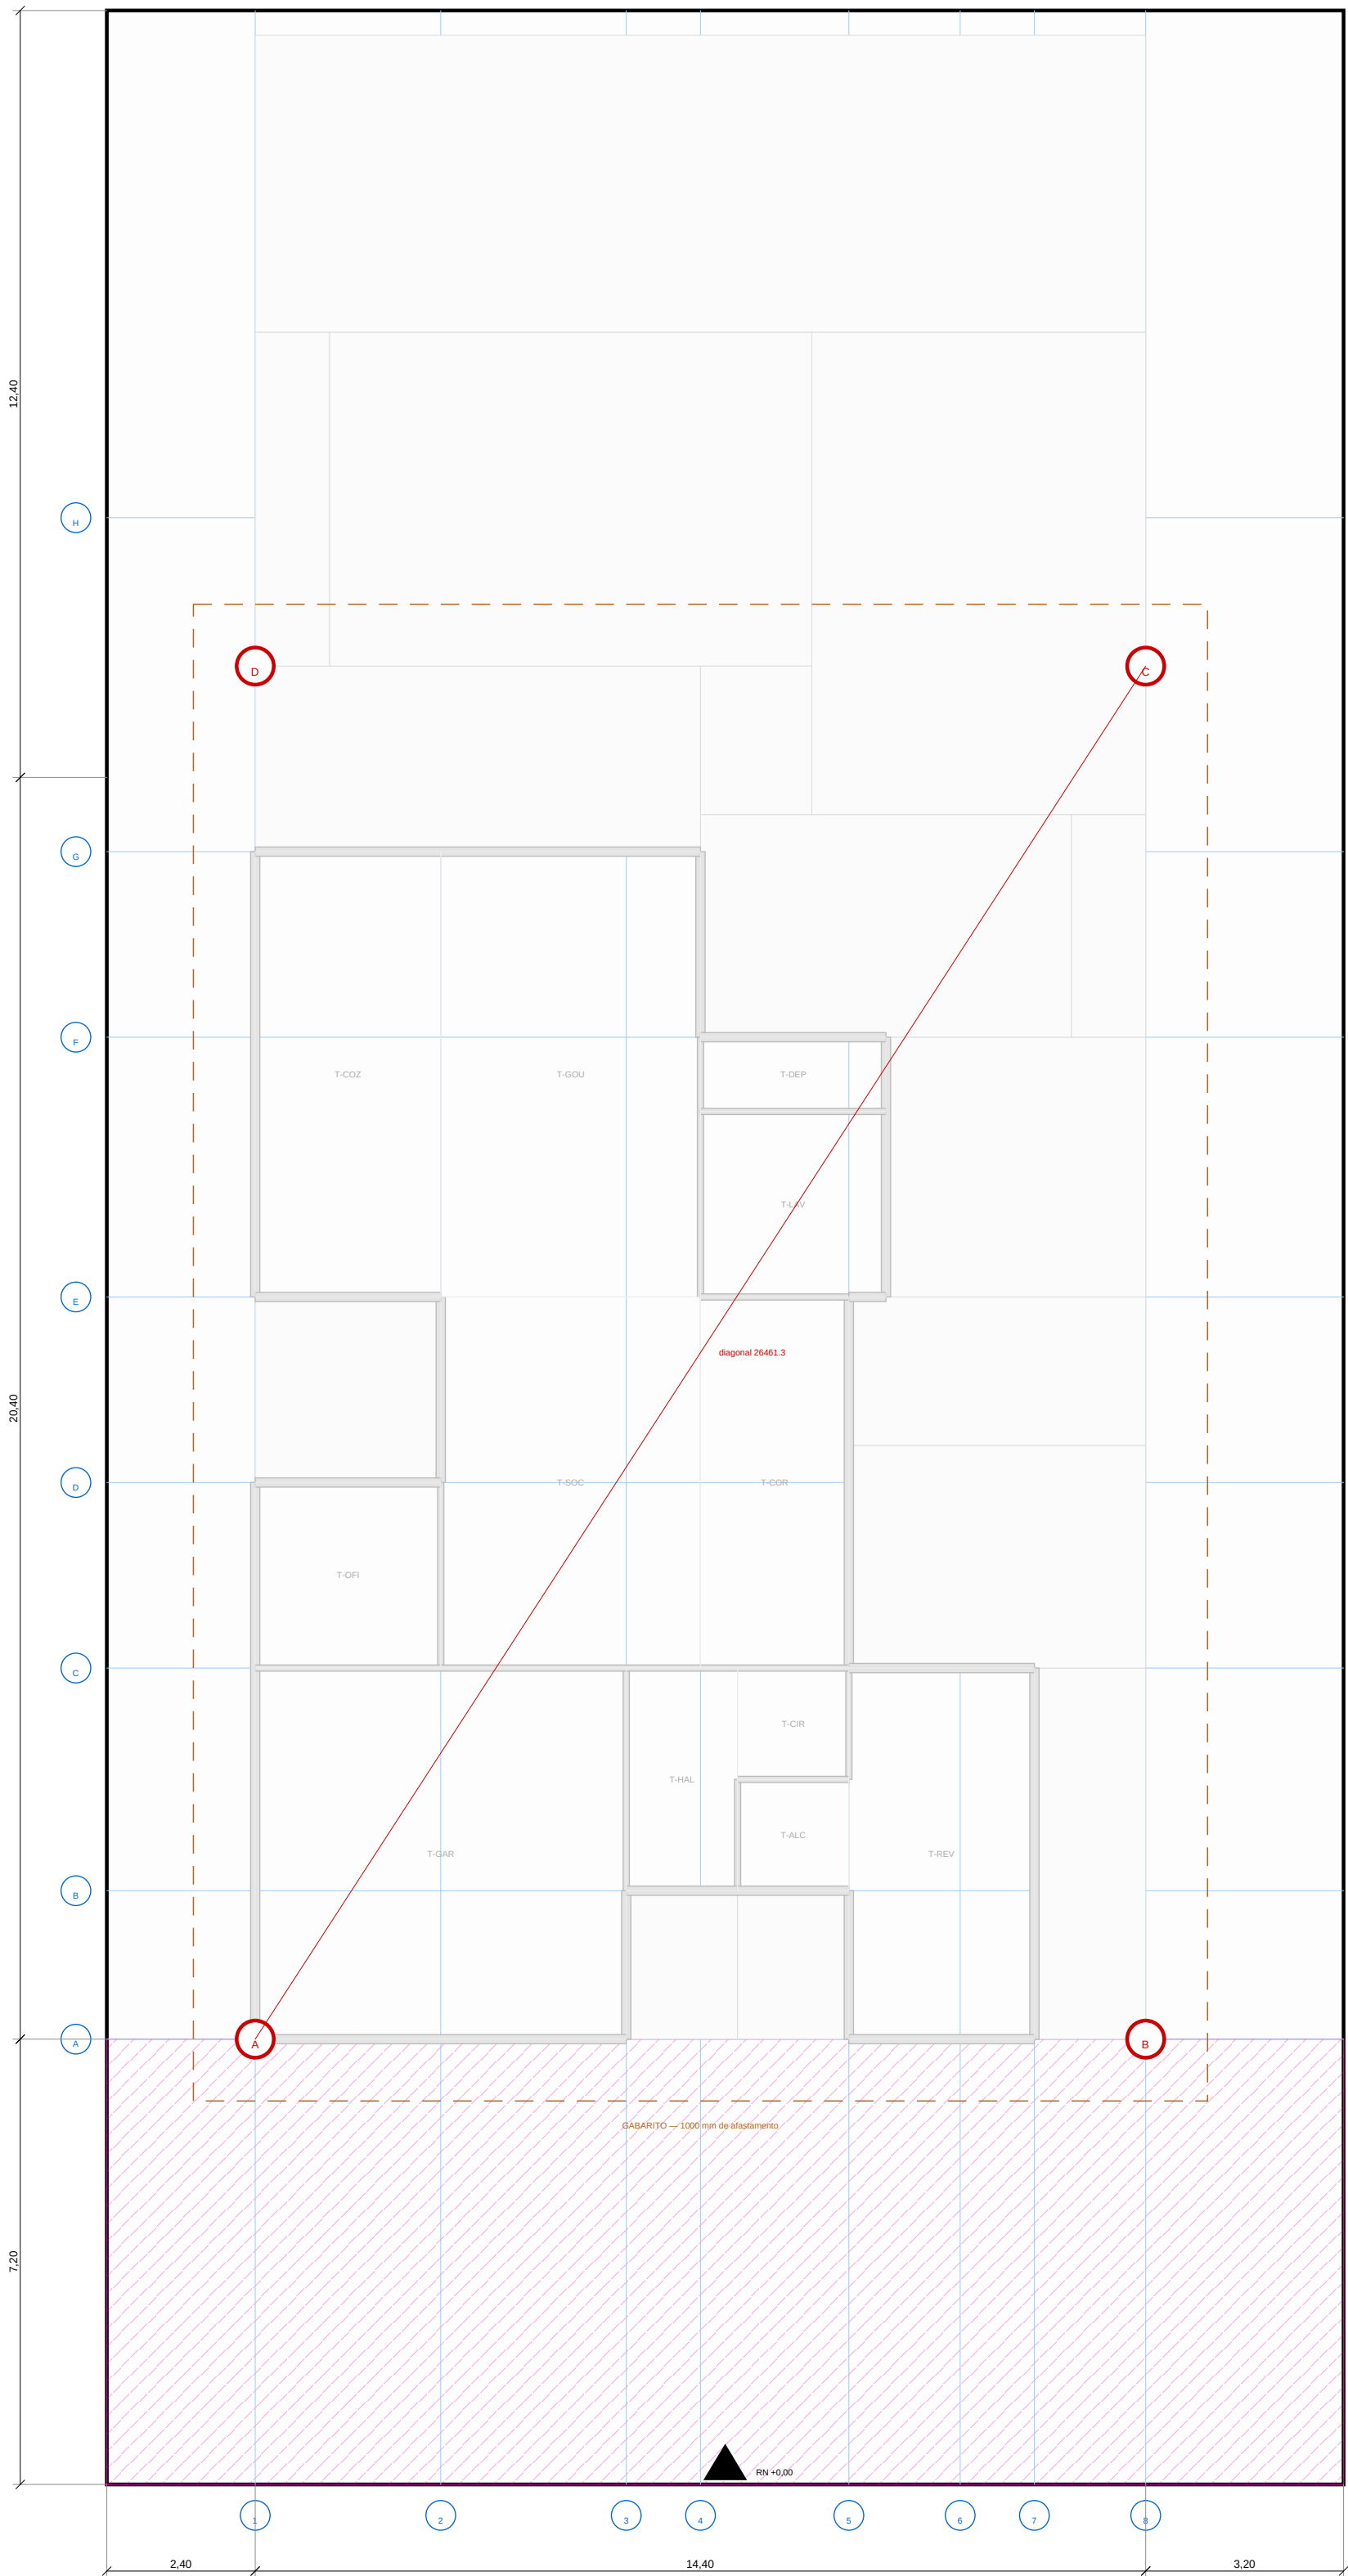

1. LOCACAO — EIXOS E COORDENADAS
ESCALA 1:100

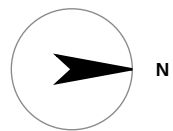

COORDENADAS DOS CANTOS (mm)

CANTO	X	Y	DIVISA SUL	DIVISA NORTE	TESTADA	QUILHO	DIAGONAL
A	2400	7200	2400	17600	7200	32800	26461,3
B	18800	7200	18800	3200	7200	32800	26461,3
C	18800	28400	18800	3200	28400	19600	26461,3
D	2400	28400	2400	17600	28400	19600	26461,3

PROCEDIMENTO DE LOCACAO

#	PASSO	CRITERIO DE ACABO
1	Conferir as divisas com o material de base	divergencia maxima de 10 mm interromper a locacao
2	Instalar o RMC marca de concreto 200 x 200 x 100 mm, fora da area de obra	fora da area de obra
3	Montar o gabarito a 1000 mm do cantoneiro	perpendicular 75 x 75 a tubos 20 x 100
4	Marcar os eixos X, Y e Z a 10 mm no gabarito	linha coordenada maxima de 200 mm
5	Colar cado canto dos QUADs dividas	verificar em cado, erro de cado de 10 mm
6	Conferir a diagonal A-C	26461,3 mm com tolerancia de 10 mm
7	Conferir o quadrado por 3-4-5 em cada canto	antes de qualquer concretagem
8	Registrar em ata com foto e modelo	gabarito continuo nos dois lados da obra, conferencia

EIXOS MODULARES

DIRECAO	AXES (mm)
X (L x R)	2400 5400 8400 9600 12600 13800 15000 16800
Y (A x H)	7200 9600 13200 14200 15000 28400 29400 32800
Matia	principal 800 mm - subgalo 300 mm
Origen	canto frontal esquerdo da base
Unidade	milimetros

NOTAS

- Locacao e o unico desenho em que o erro nao tem consequncia para o caso de erro de lugar.
- Cada canto e cado dos QUADs dividas, nunca em cado acumulado — erro de cado soma, erro de referencia independente nao.
- Conferencia obrigatoria pela diagonal 26461,3 mm entre A e C antes de concretar o nada.
- Ata no ato de locacao, alinhado ao metodo TC-06, cado 0,00 + 1 para acabado do terreno.

PROJETO PORTO REAL

RESIDENCIA UNIFAMILIAR (MANSO) - AM | SOU TATIANA-PS

PROJETO ARQUITETONICO

LOCACAO DE OBRA E GABARITO

BASE GEOMETRICA Linha Consolidada Projeto (previsao) UNIDADE: METRO: MM	ESCALA 1:100 FORMATO: A1 MILHA: 600/600/600	DIVISAO ESTUDIO PRELIMINAR R7B LIMITE LIBERADO PARA OBRA SEM ART / RNT	PROJECOA 31 DE TI REVISAO
--	--	---	---------------------------------