


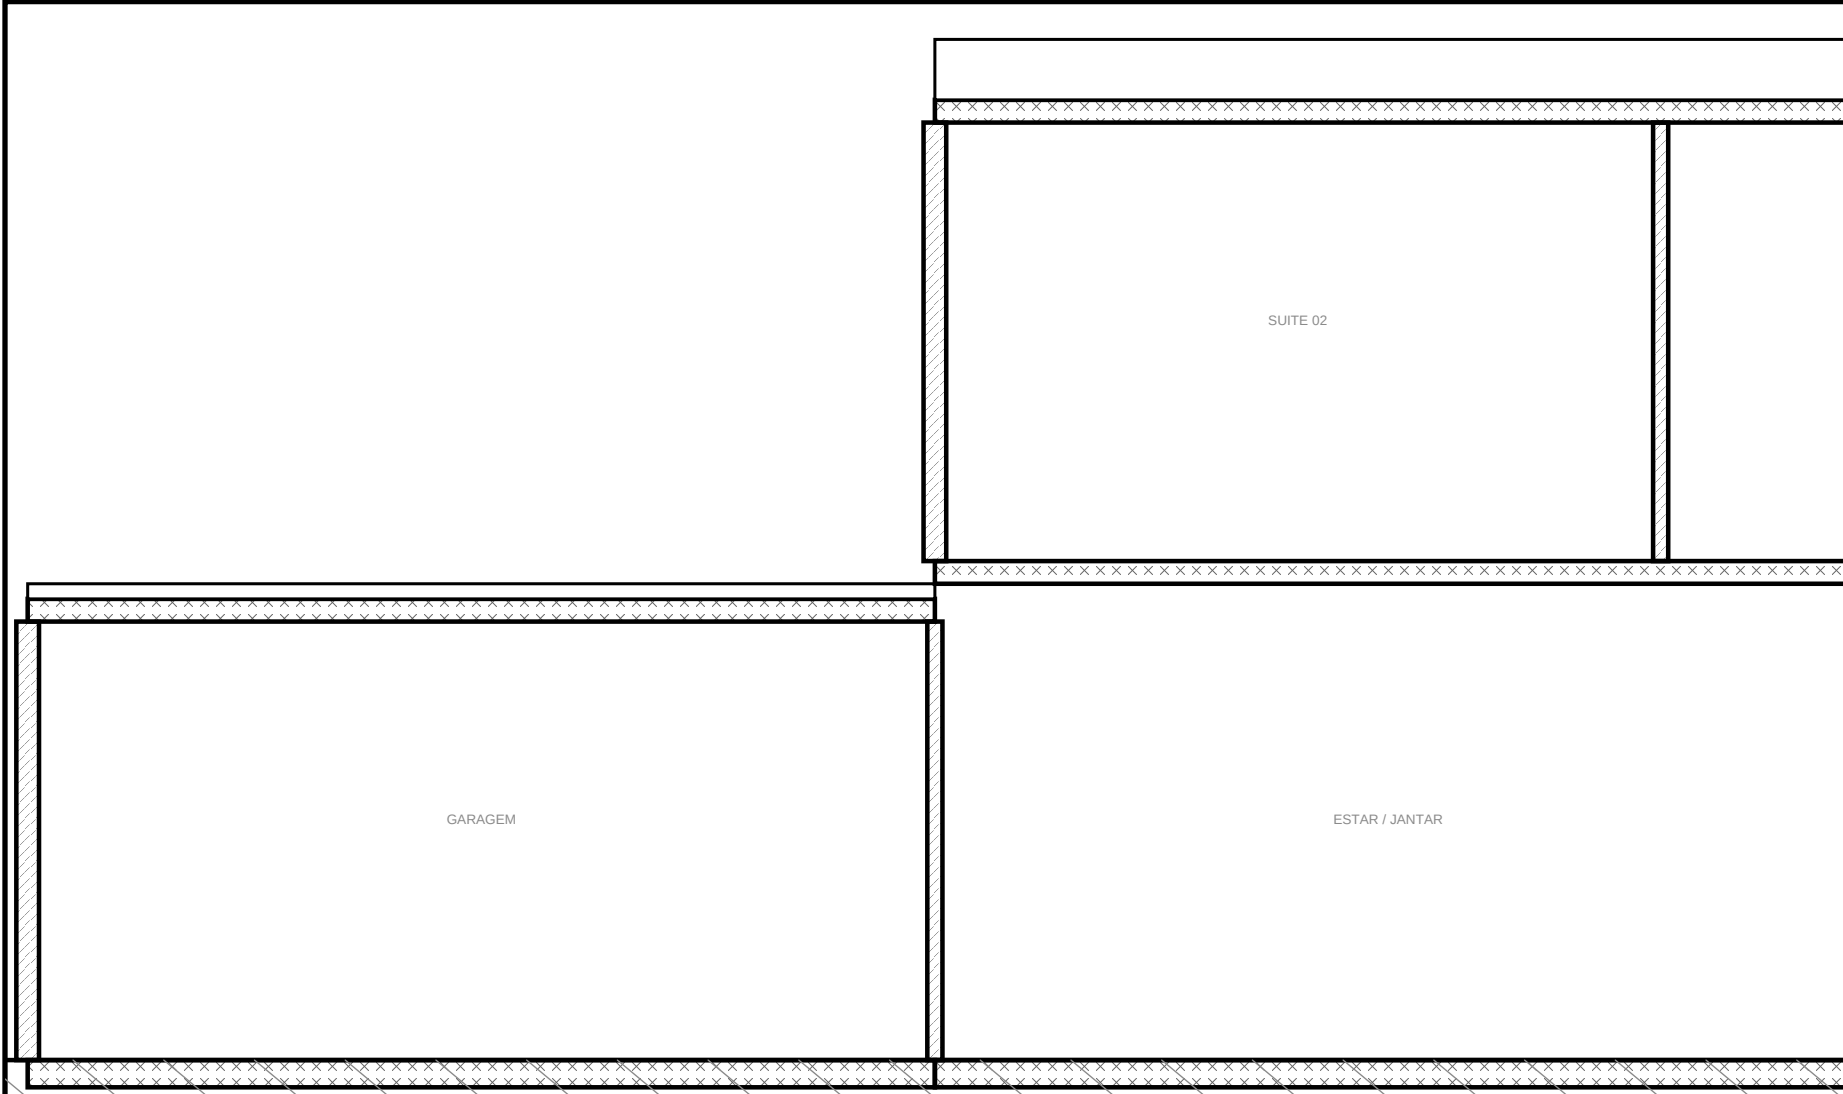
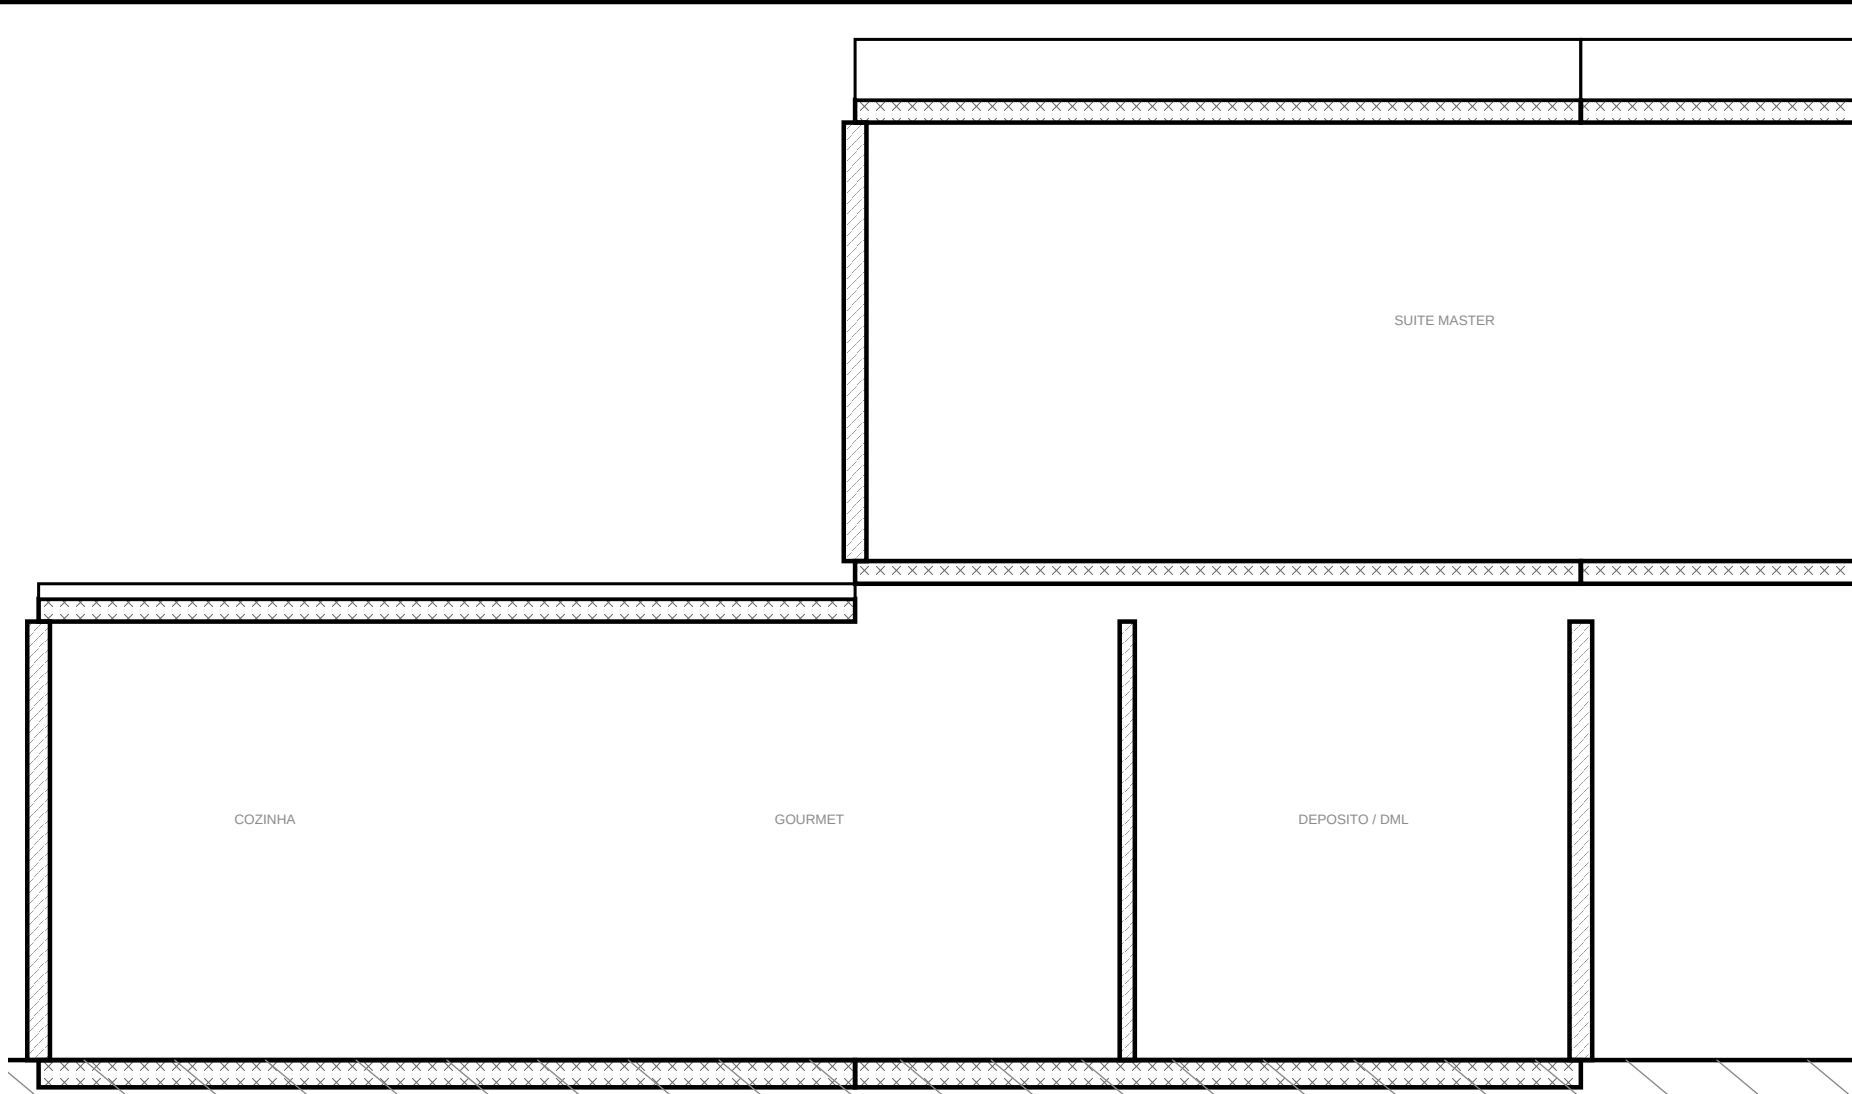


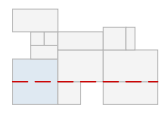



1 CORTE 1-1 — GARAGEM
ESCALA 1:50

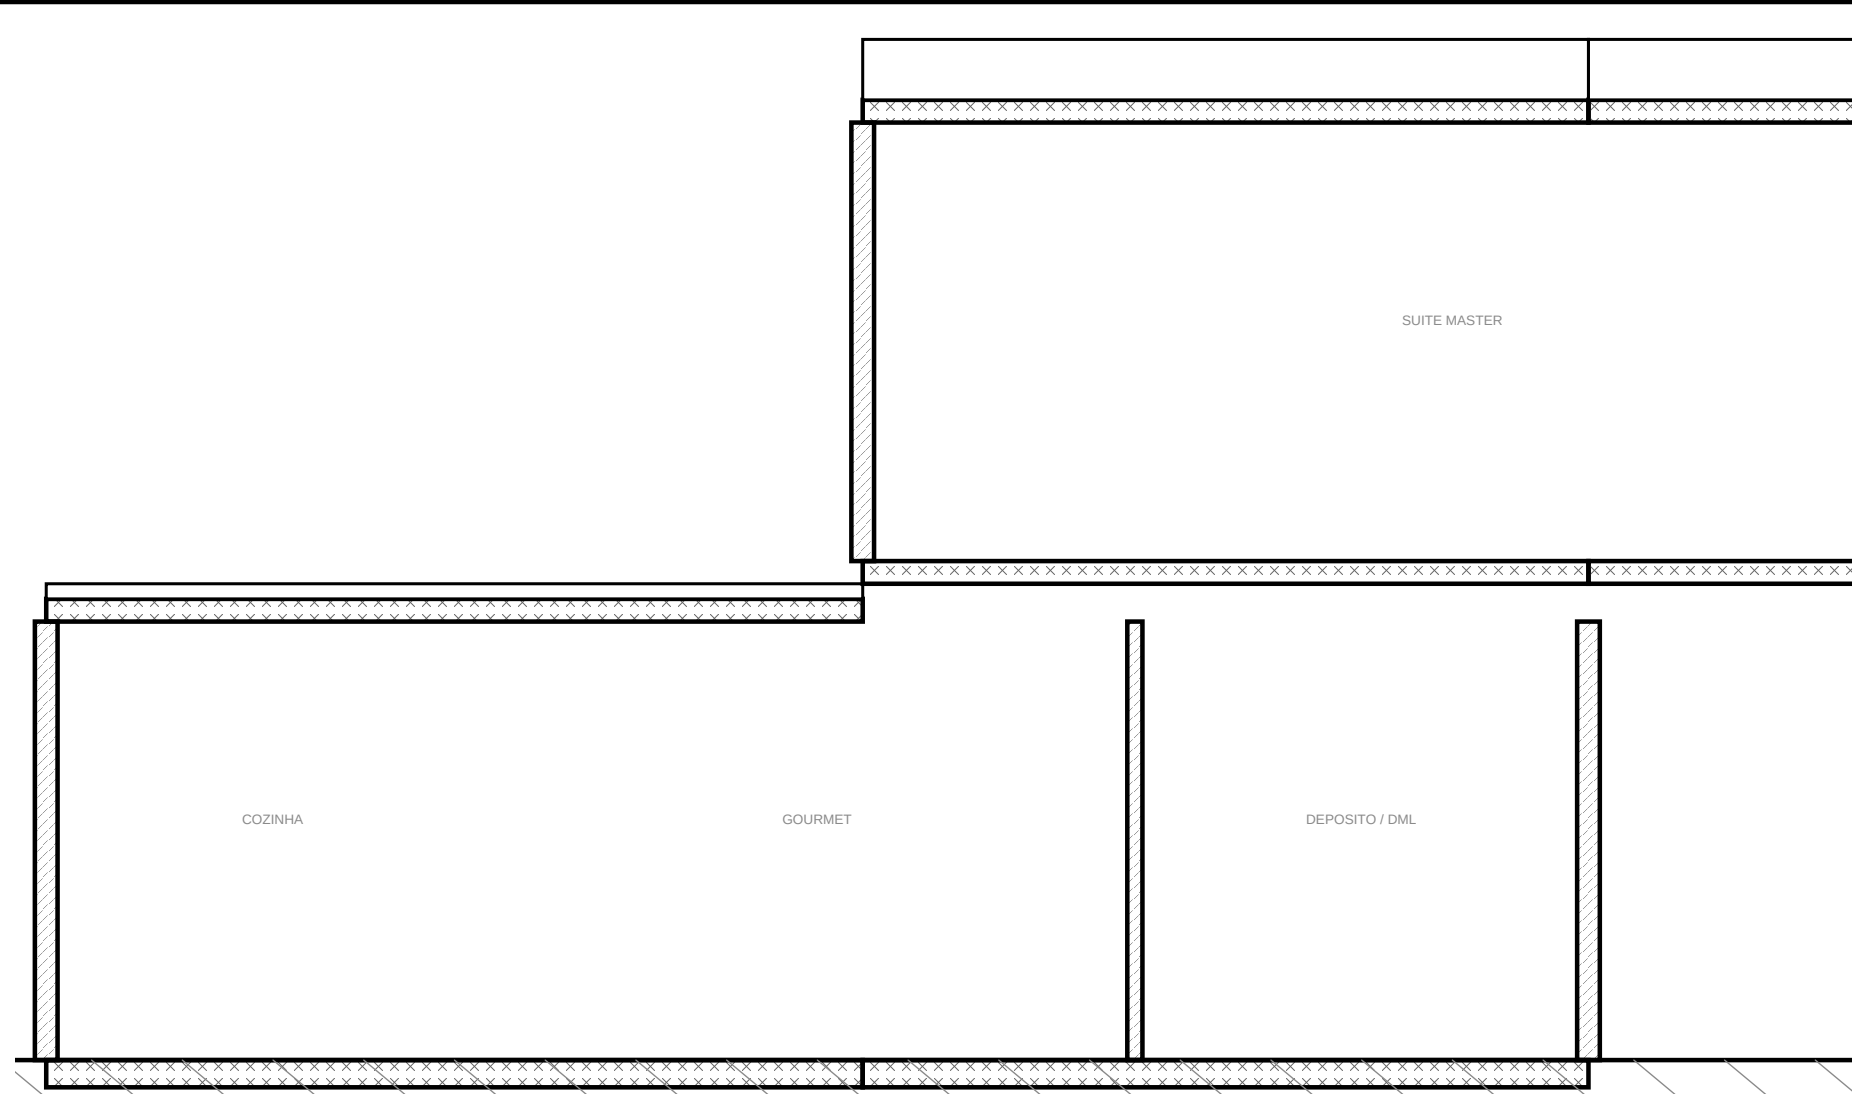



2 CORTE 2-2 — COZINHA
ESCALA 1:50

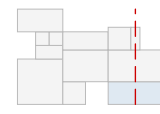



3 CORTE 3-3 — GOURMET
ESCALA 1:50

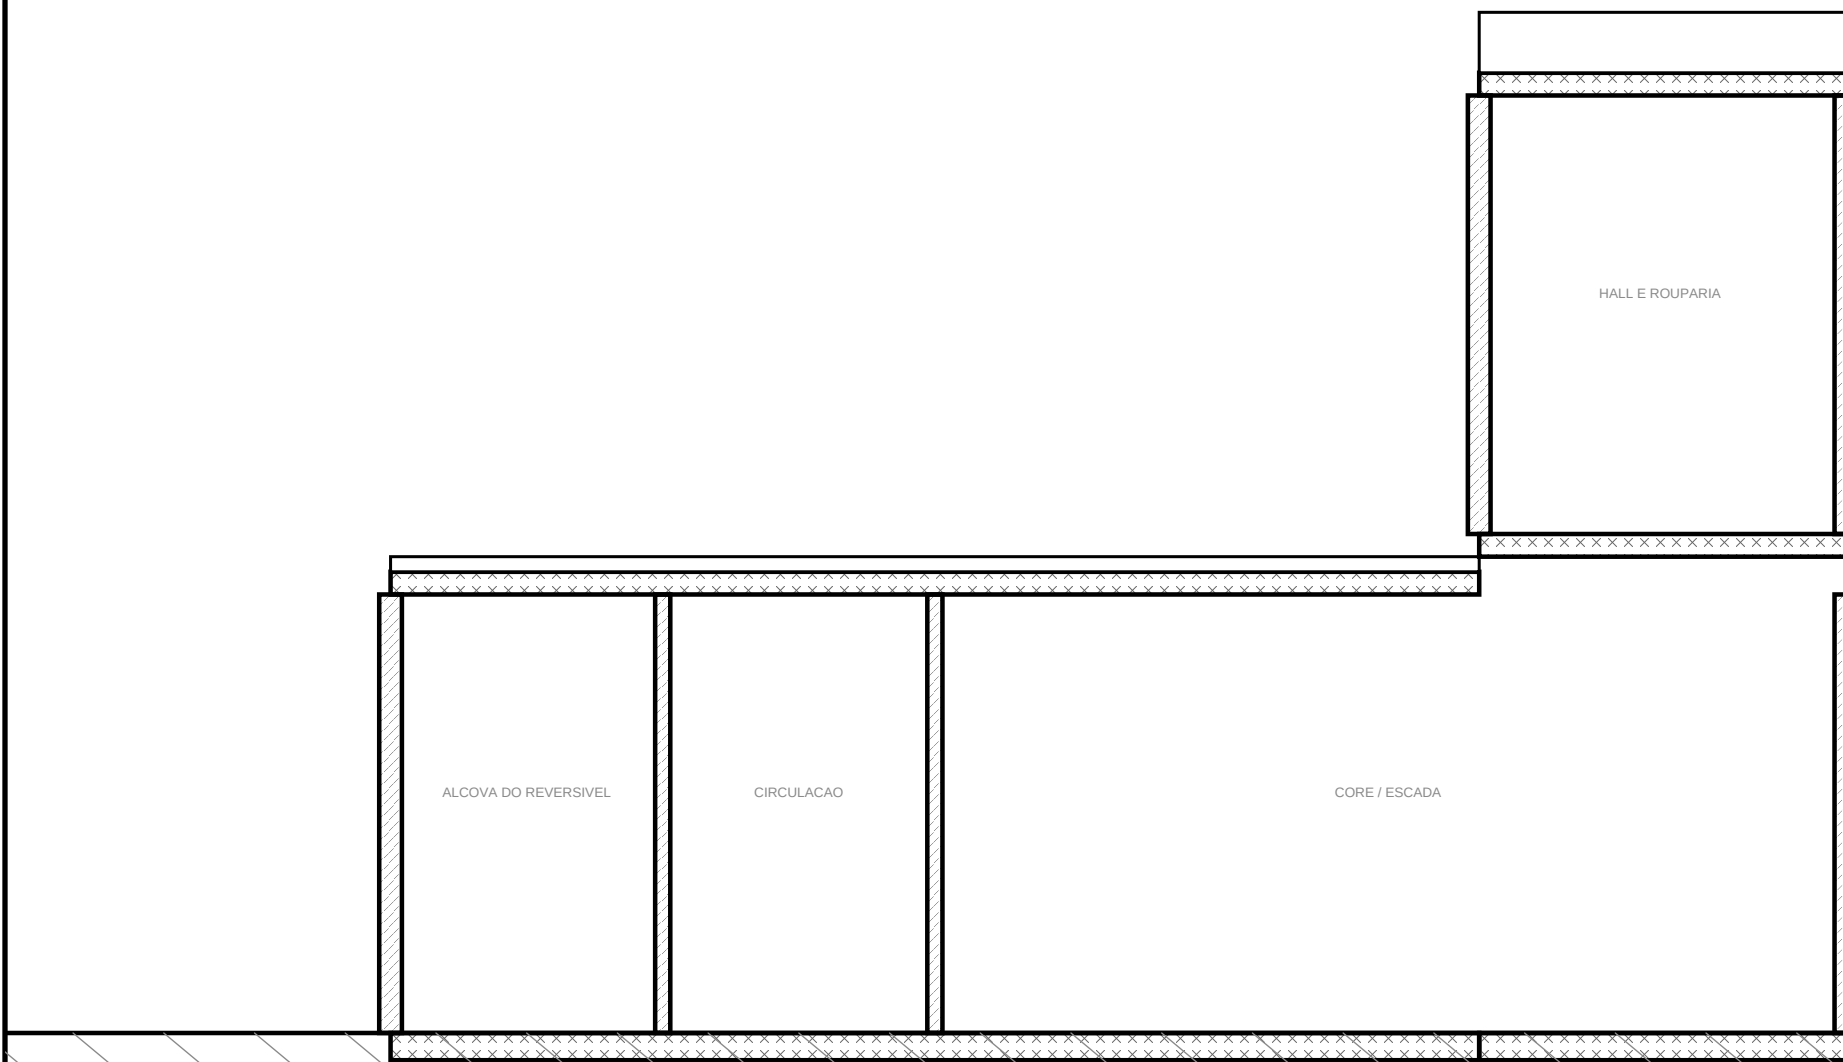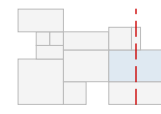

4 CORTE 4-4 — SUITE MASTER
ESCALA 1:50

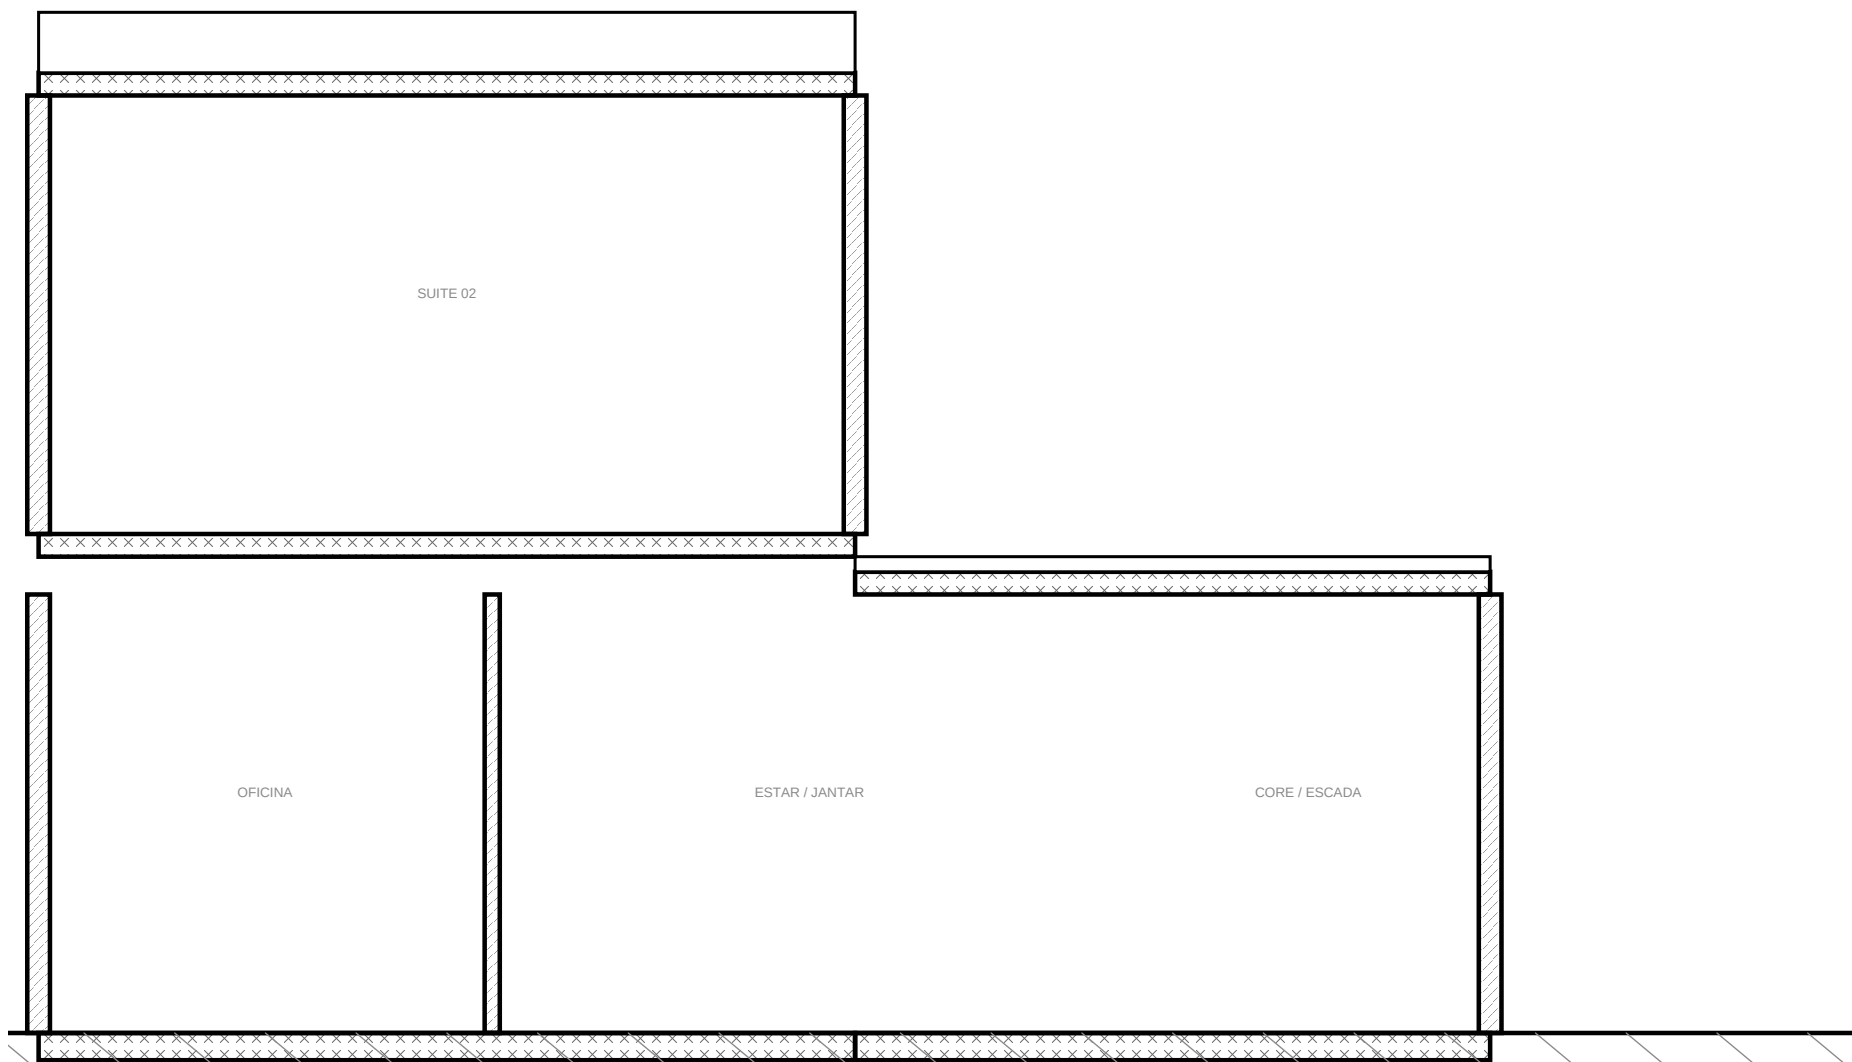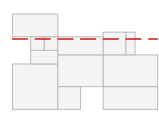

5 CORTE 5-5 — BANHOS DAS SUITES 02 E 03
ESCALA 1:50

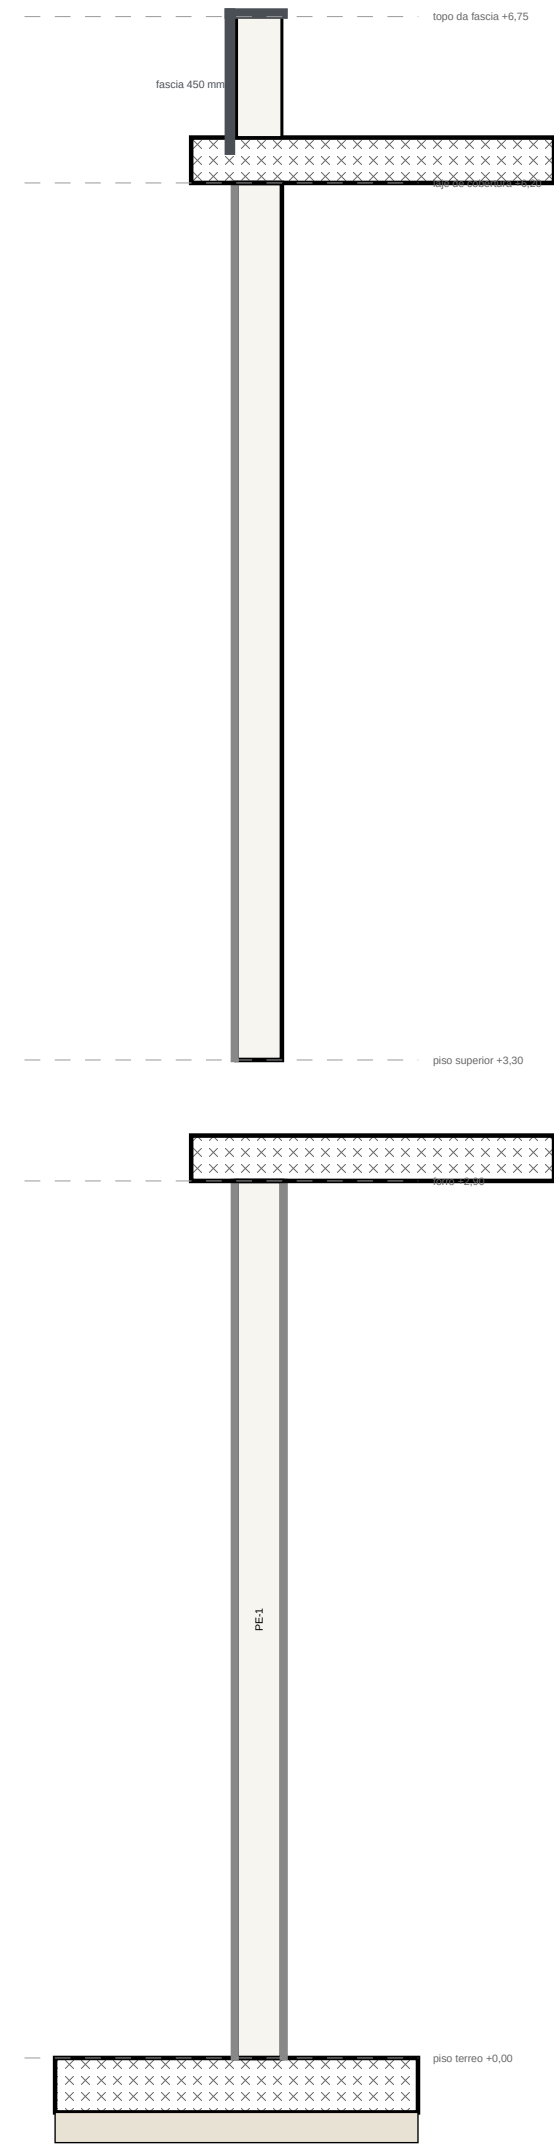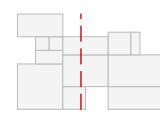

6 CORTE DE FACHADA — PE-1, RADIER A FASCIA
ESCALA 1:25

representação controlada (PR-47)

- NOTAS
- Cada corte passa pelo centro do ambiente que o nomeia, o plano e o eixo estão na planta cheia ao lado do Rót.
 - Pe-direto 2000 mm, piso a piso 2000 mm - radier 180 mm.
 - Corte controlado de fachada: do radier à fachada, com os cantos da PE-1 (PR-12) e a fachada de desenho (PR-7).
 - Cortes gerados pelo mesmo desenhador: dos cortes AA e BB (PR-16).

PROJETO PORTO REAL

RESIDENCIA UNIFAMILIAR (MANAUS - AM) | SUITE TATIANA-PR

PROJETO ARQUITETONICO

CORTES POR AMBIENTE E CORTE DE FACHADA

BASE GEOMETRICA	ESCALA	EMISSAO	PROJECION
Lista Consolidada	1:50 • 1:25	ESTUDIO PRELIMINAR R7B	50
PR-122 (previsão)	FORMATO A1	NAO LIBERADO PARA OBRA	6x 7,5 REVERTE
UNIDADE METRICA: MM	MILIMETROS (50/100/200)	SEM ART / RNT	